
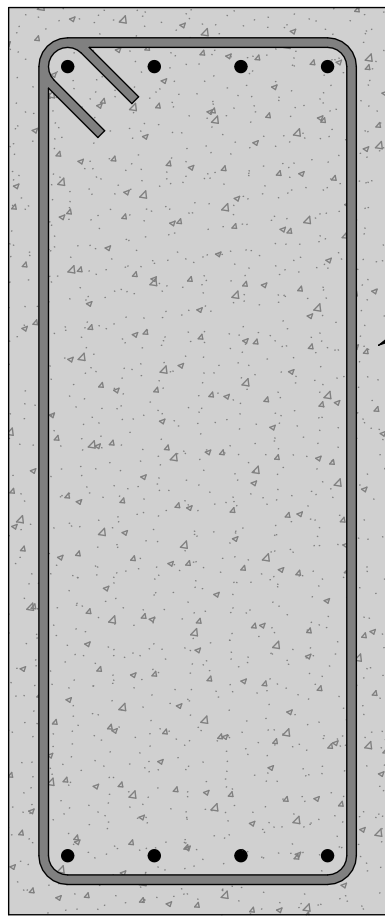


ESTE PLANO ES PROPIEDAD INTELECTUAL DE SOLARTE Y CIA. INGENIEROS CALCULISTAS S.A. SE PROHIBE SU REPRODUCCION O MODIFICACION PARCIAL O TOTAL. EN CASO DE MODIFICARSE VO UTILIZARSE INDEBIDAMENTE. LA EMPRESA QUEDA EXENTA DE CUALQUIER RESPONSABILIDAD QUE PUEDA DERIVAR DE SU UTILIZACION.

3772-25

EDIFICACIÓN DE VIVIENDA EN 8 PISOS Y 1 SOTANO

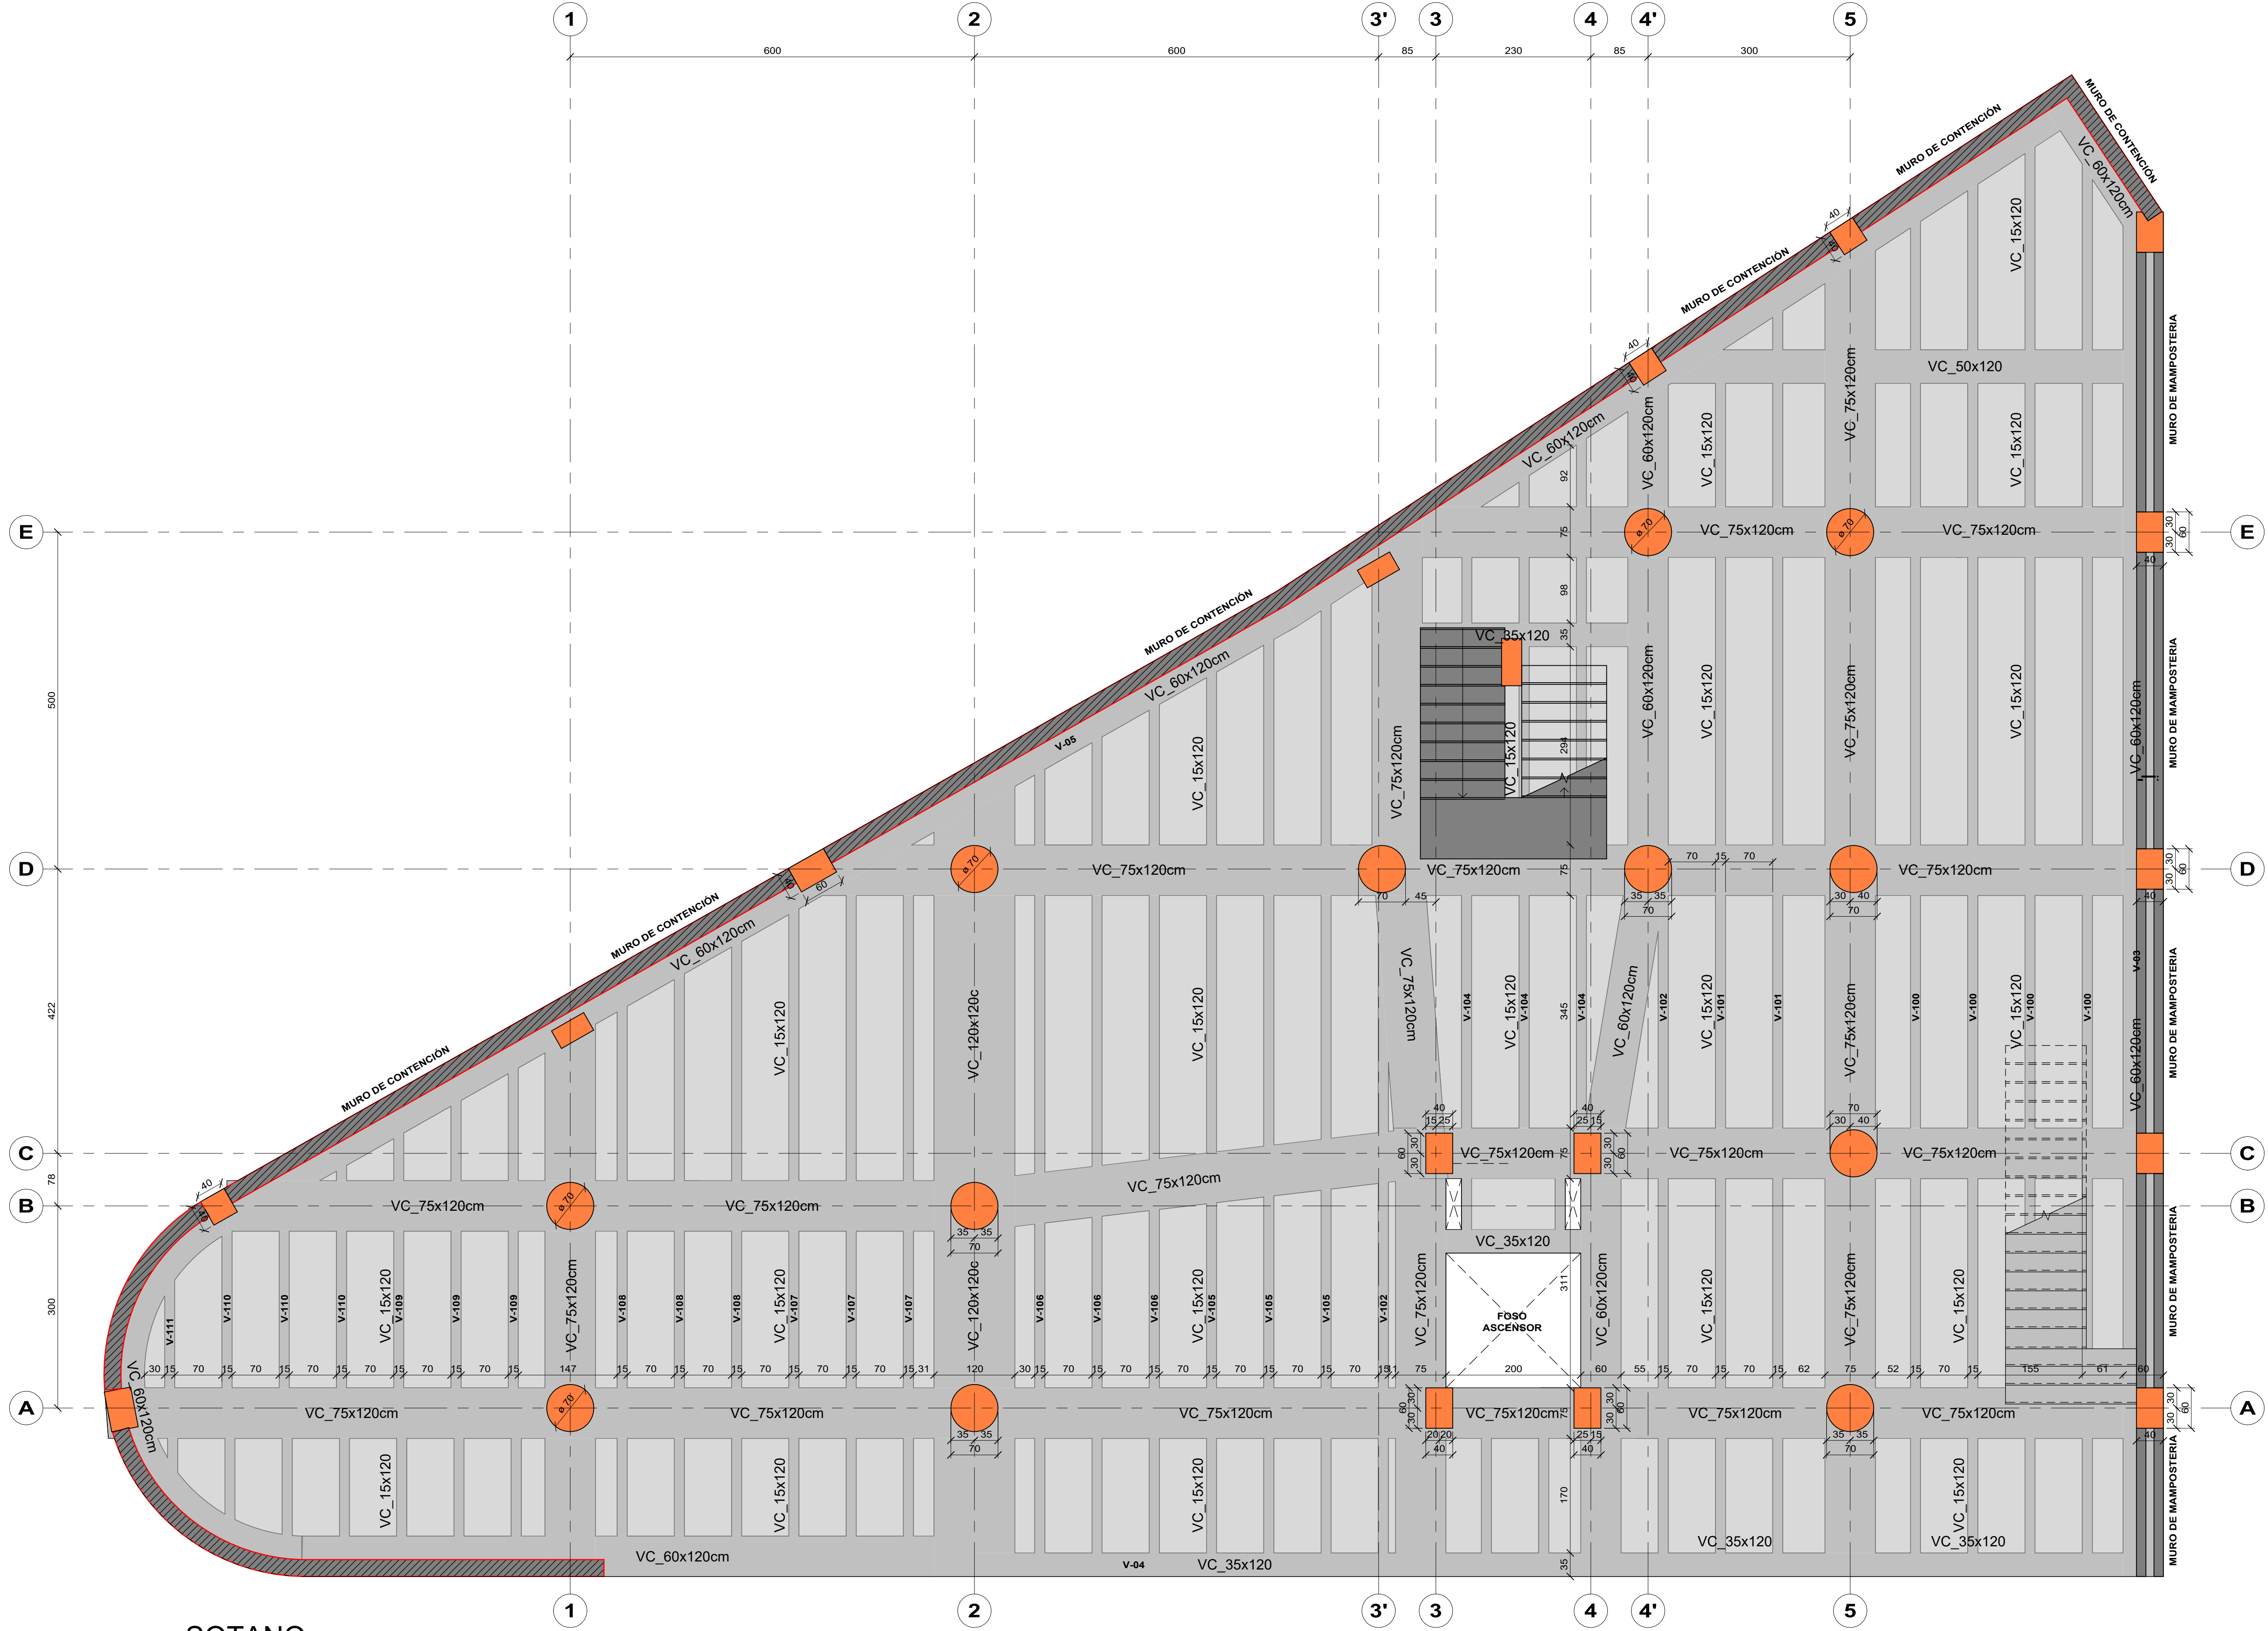


Según Despiece

VIGA CIM 50x120

1 : 10

1 SOTANO
1 : 50

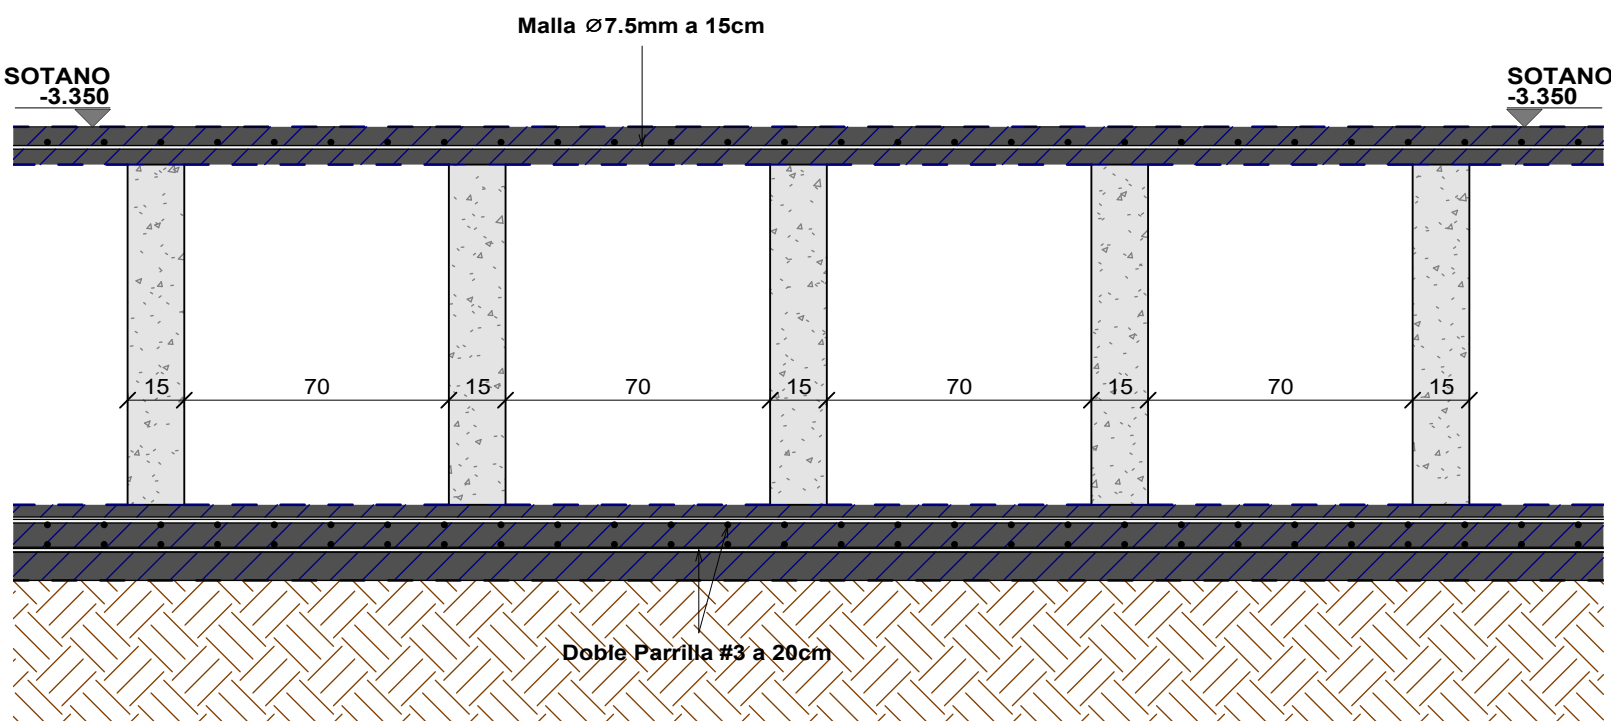

3 Sección 5
1 : 20

VERSIÓN	FECHA	REVISIONES O MODIFICACIONES	MODIFICÓ

SISTEMA ESTRUCTURAL	Sistema: PORTICOS EN CONCRETO RESISTENTE A MOMENTO			ESPECIFICACIONES DE MATERIALES					
	Ro:	Grupo de Uso:	Capacidad:						
	7.0	I	DES						
	Espectro de Diseño: MICROZONIFICACIÓN								
	Zona:	Fa:	Fv:						
	2	1.2	1.13						
	Cimentación: LOSA CIMENTACIÓN								
	qa (Kg/cm²):	Estudio de Suelos:							
	1.20								
	GLORIA INES ROSALES								
Cargas Muertas:			Cargas Vivas:						
APTO:450kg/m2			APTO:180kg/m2						
BALCONES:150kg/m2			BALCONES:500kg/m2						
ESCALERAS:150kg/m2			ESCALERAS:300kg/m2						
GRUPO DE OCUPACION							CATEGORIA	ELEMENTO	TIEMPO
R2							1	Columnas - Vigas Losas Macizas Muros interiores no portantes	1 (una) hora 1 (una) hora 1 (una) hora
NORMA DISEÑO:							NSR-10		

Curaduría

Emilito Para:

Propietario:		Proyecto Estructural:	
Acción Fiduciaria S.A como vocera y administradora del Fideicomiso FA-6547 Proyecto Florentino			
Revisó:		ING. JUAN RAUL SOLARTE G. Mat. 876 CAUCA	
Proyecto:		Diseño:	
EDIFICACIÓN DE VIVIENDA EN 8 PISOS Y 1 SOTANO BARRIO EL PEÑON		ING. JULIAN ENRIQUEZ	
Proyecto N°:		Colaboró:	
3772-25		ING. FABIAN ROJAS	
Unidad Estructural:		Dibujó:	
EDIFICIO		RENÉ MONTAÑO BOTERO	
Fecha:		Contiene:	
FEBRERO 2026	Escala:	PLANO CIMENTACION	
	Como se indica	Plano N°:	
		100	
		Versión:	