

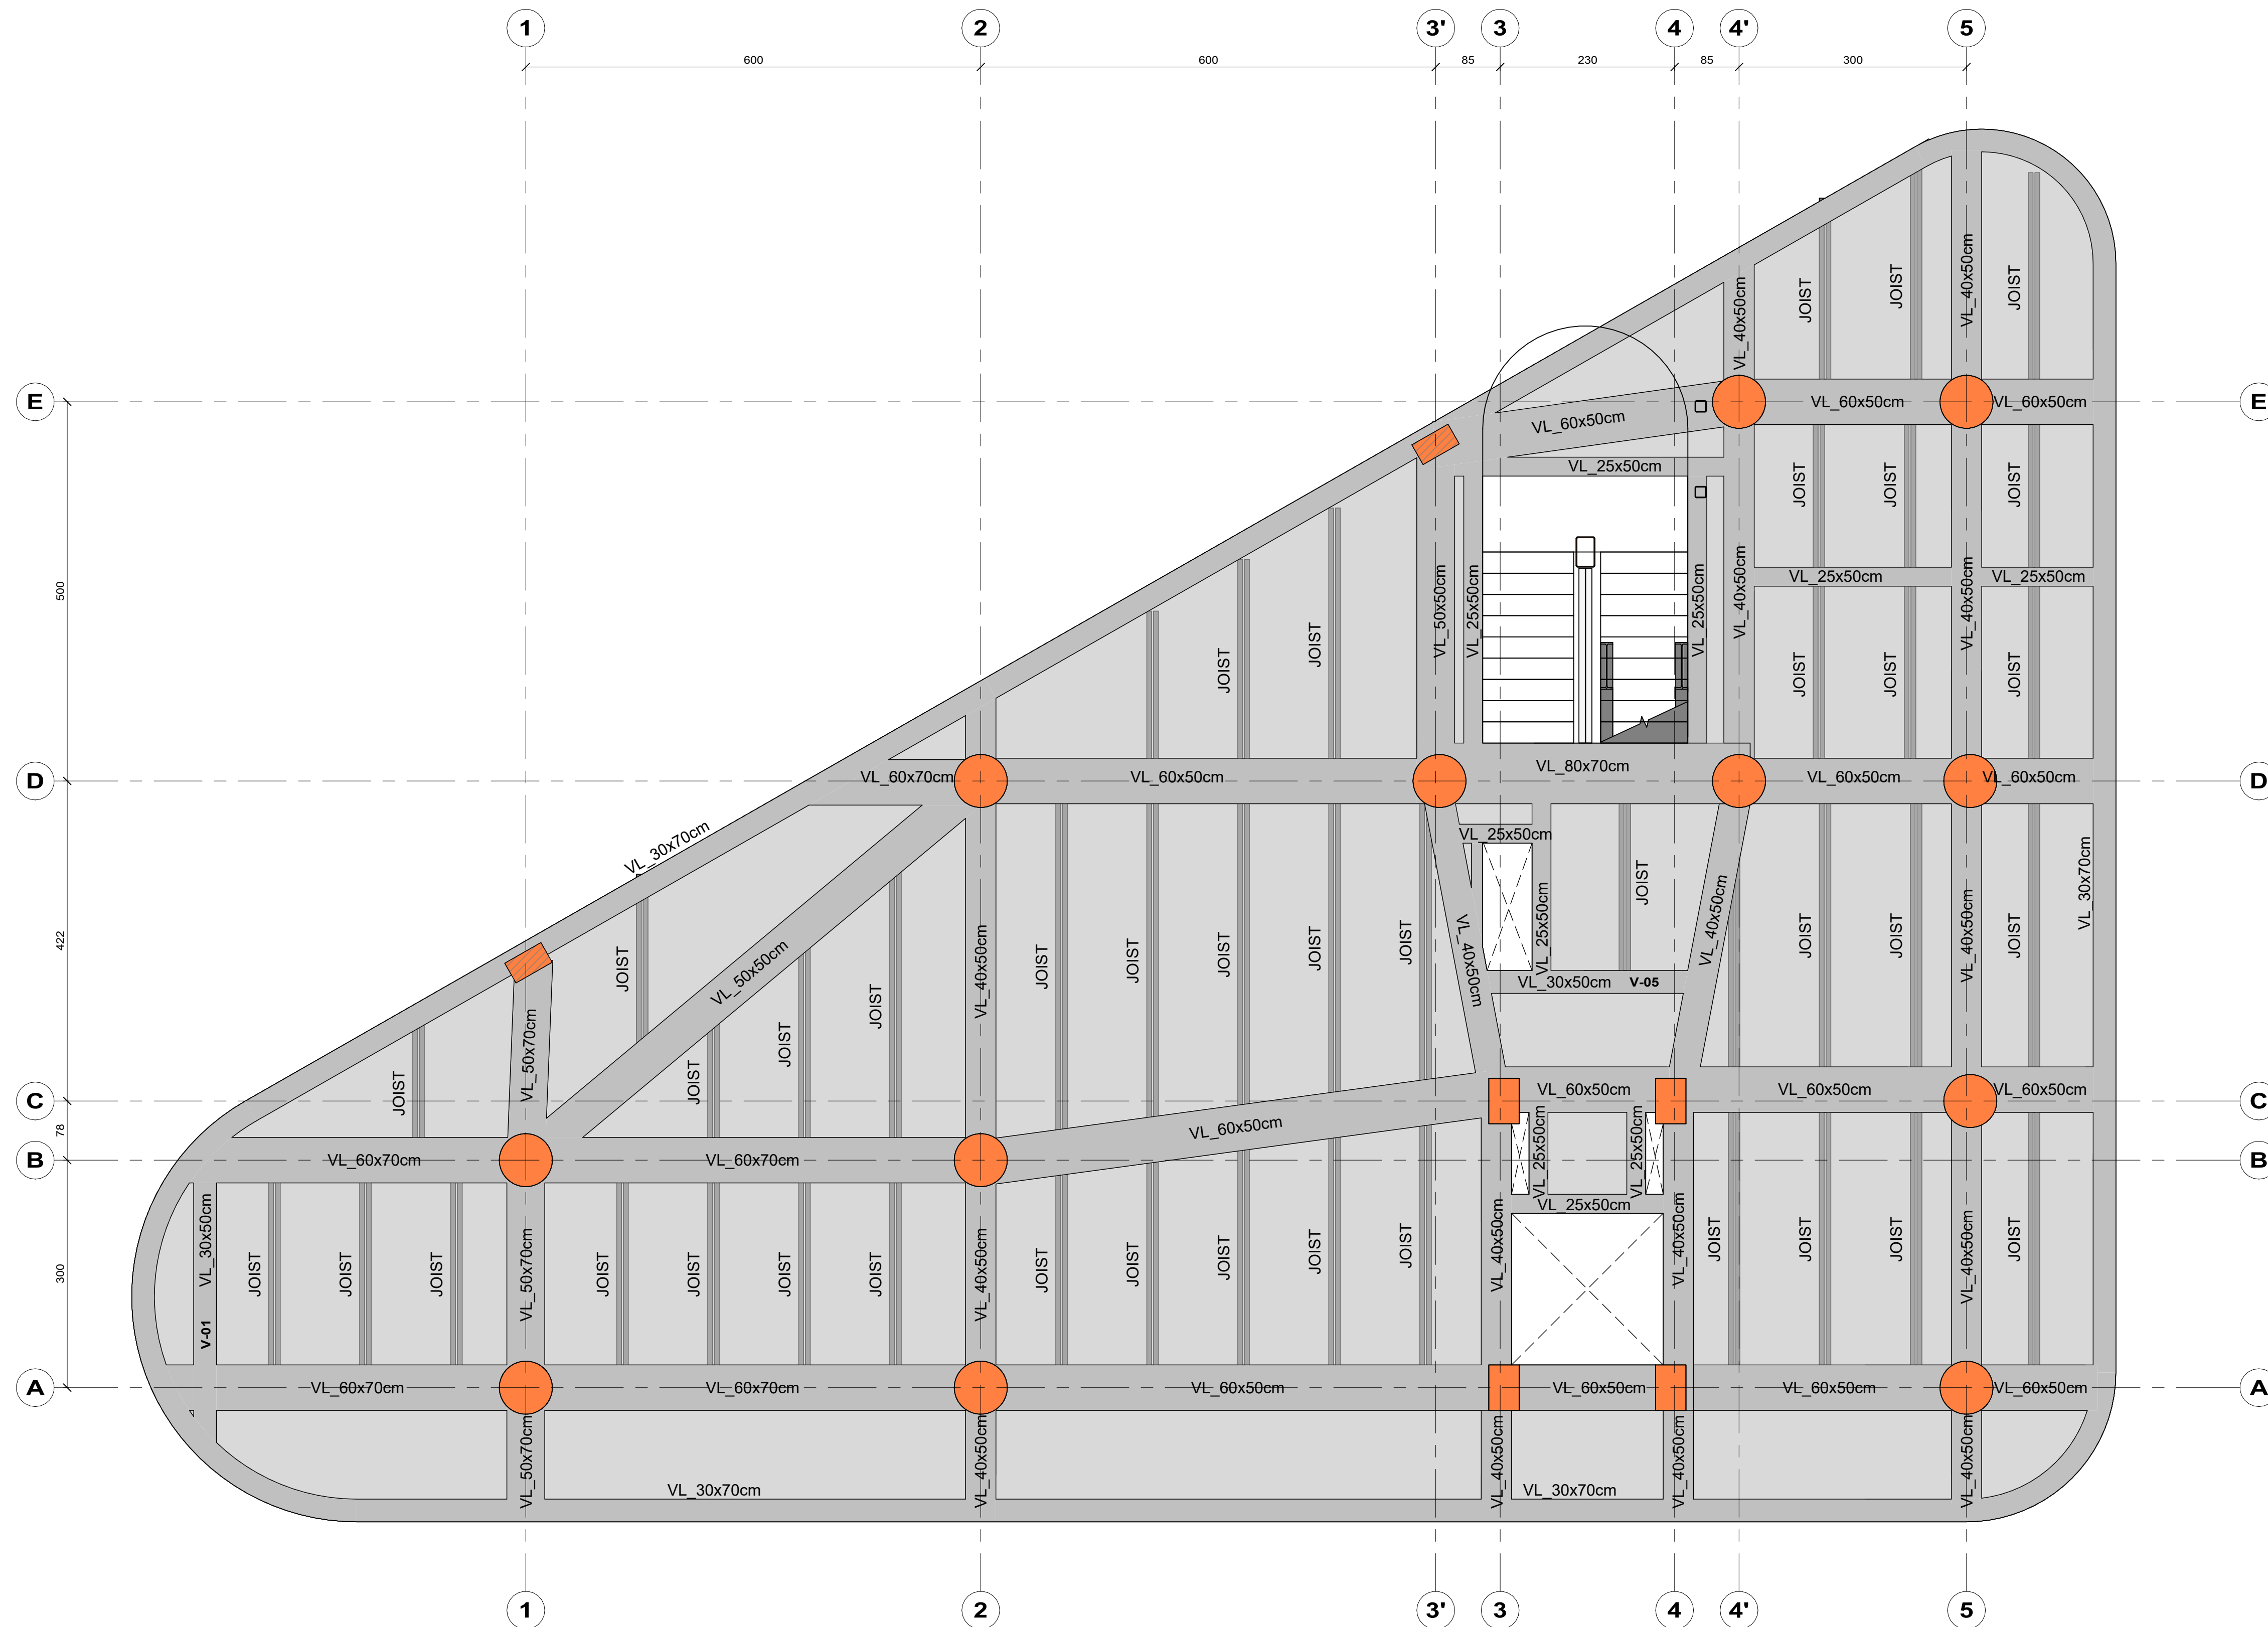
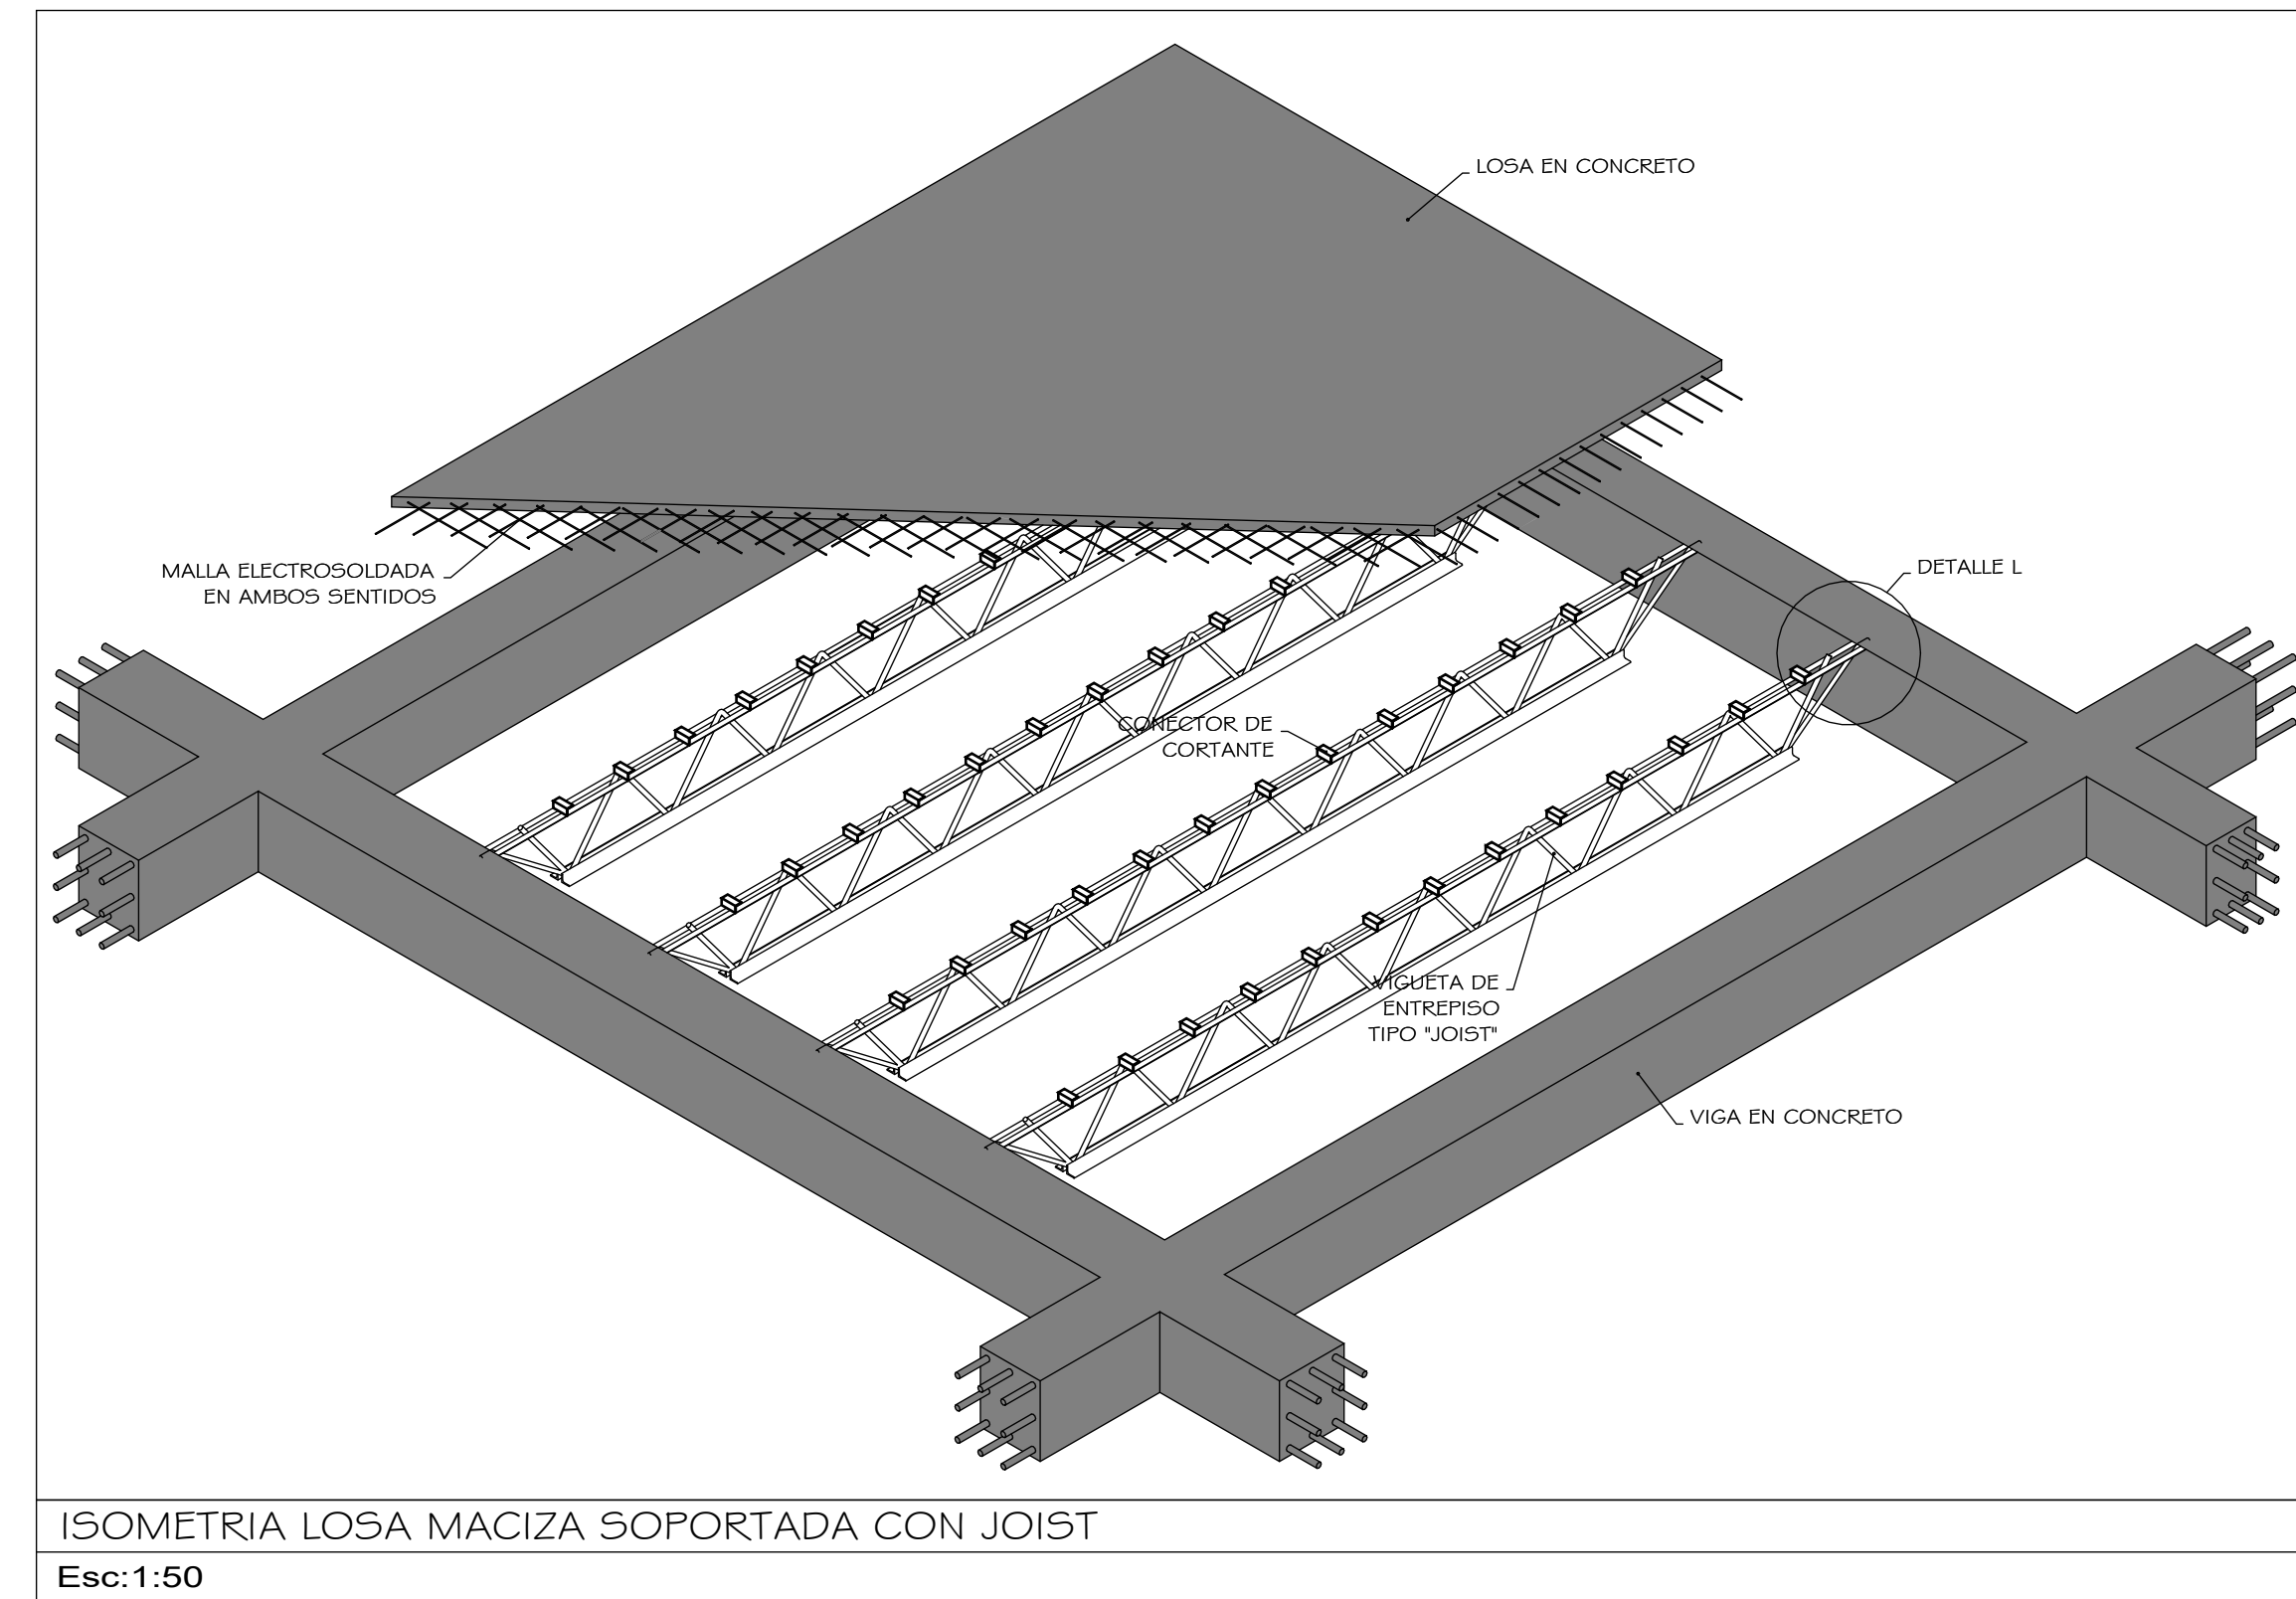
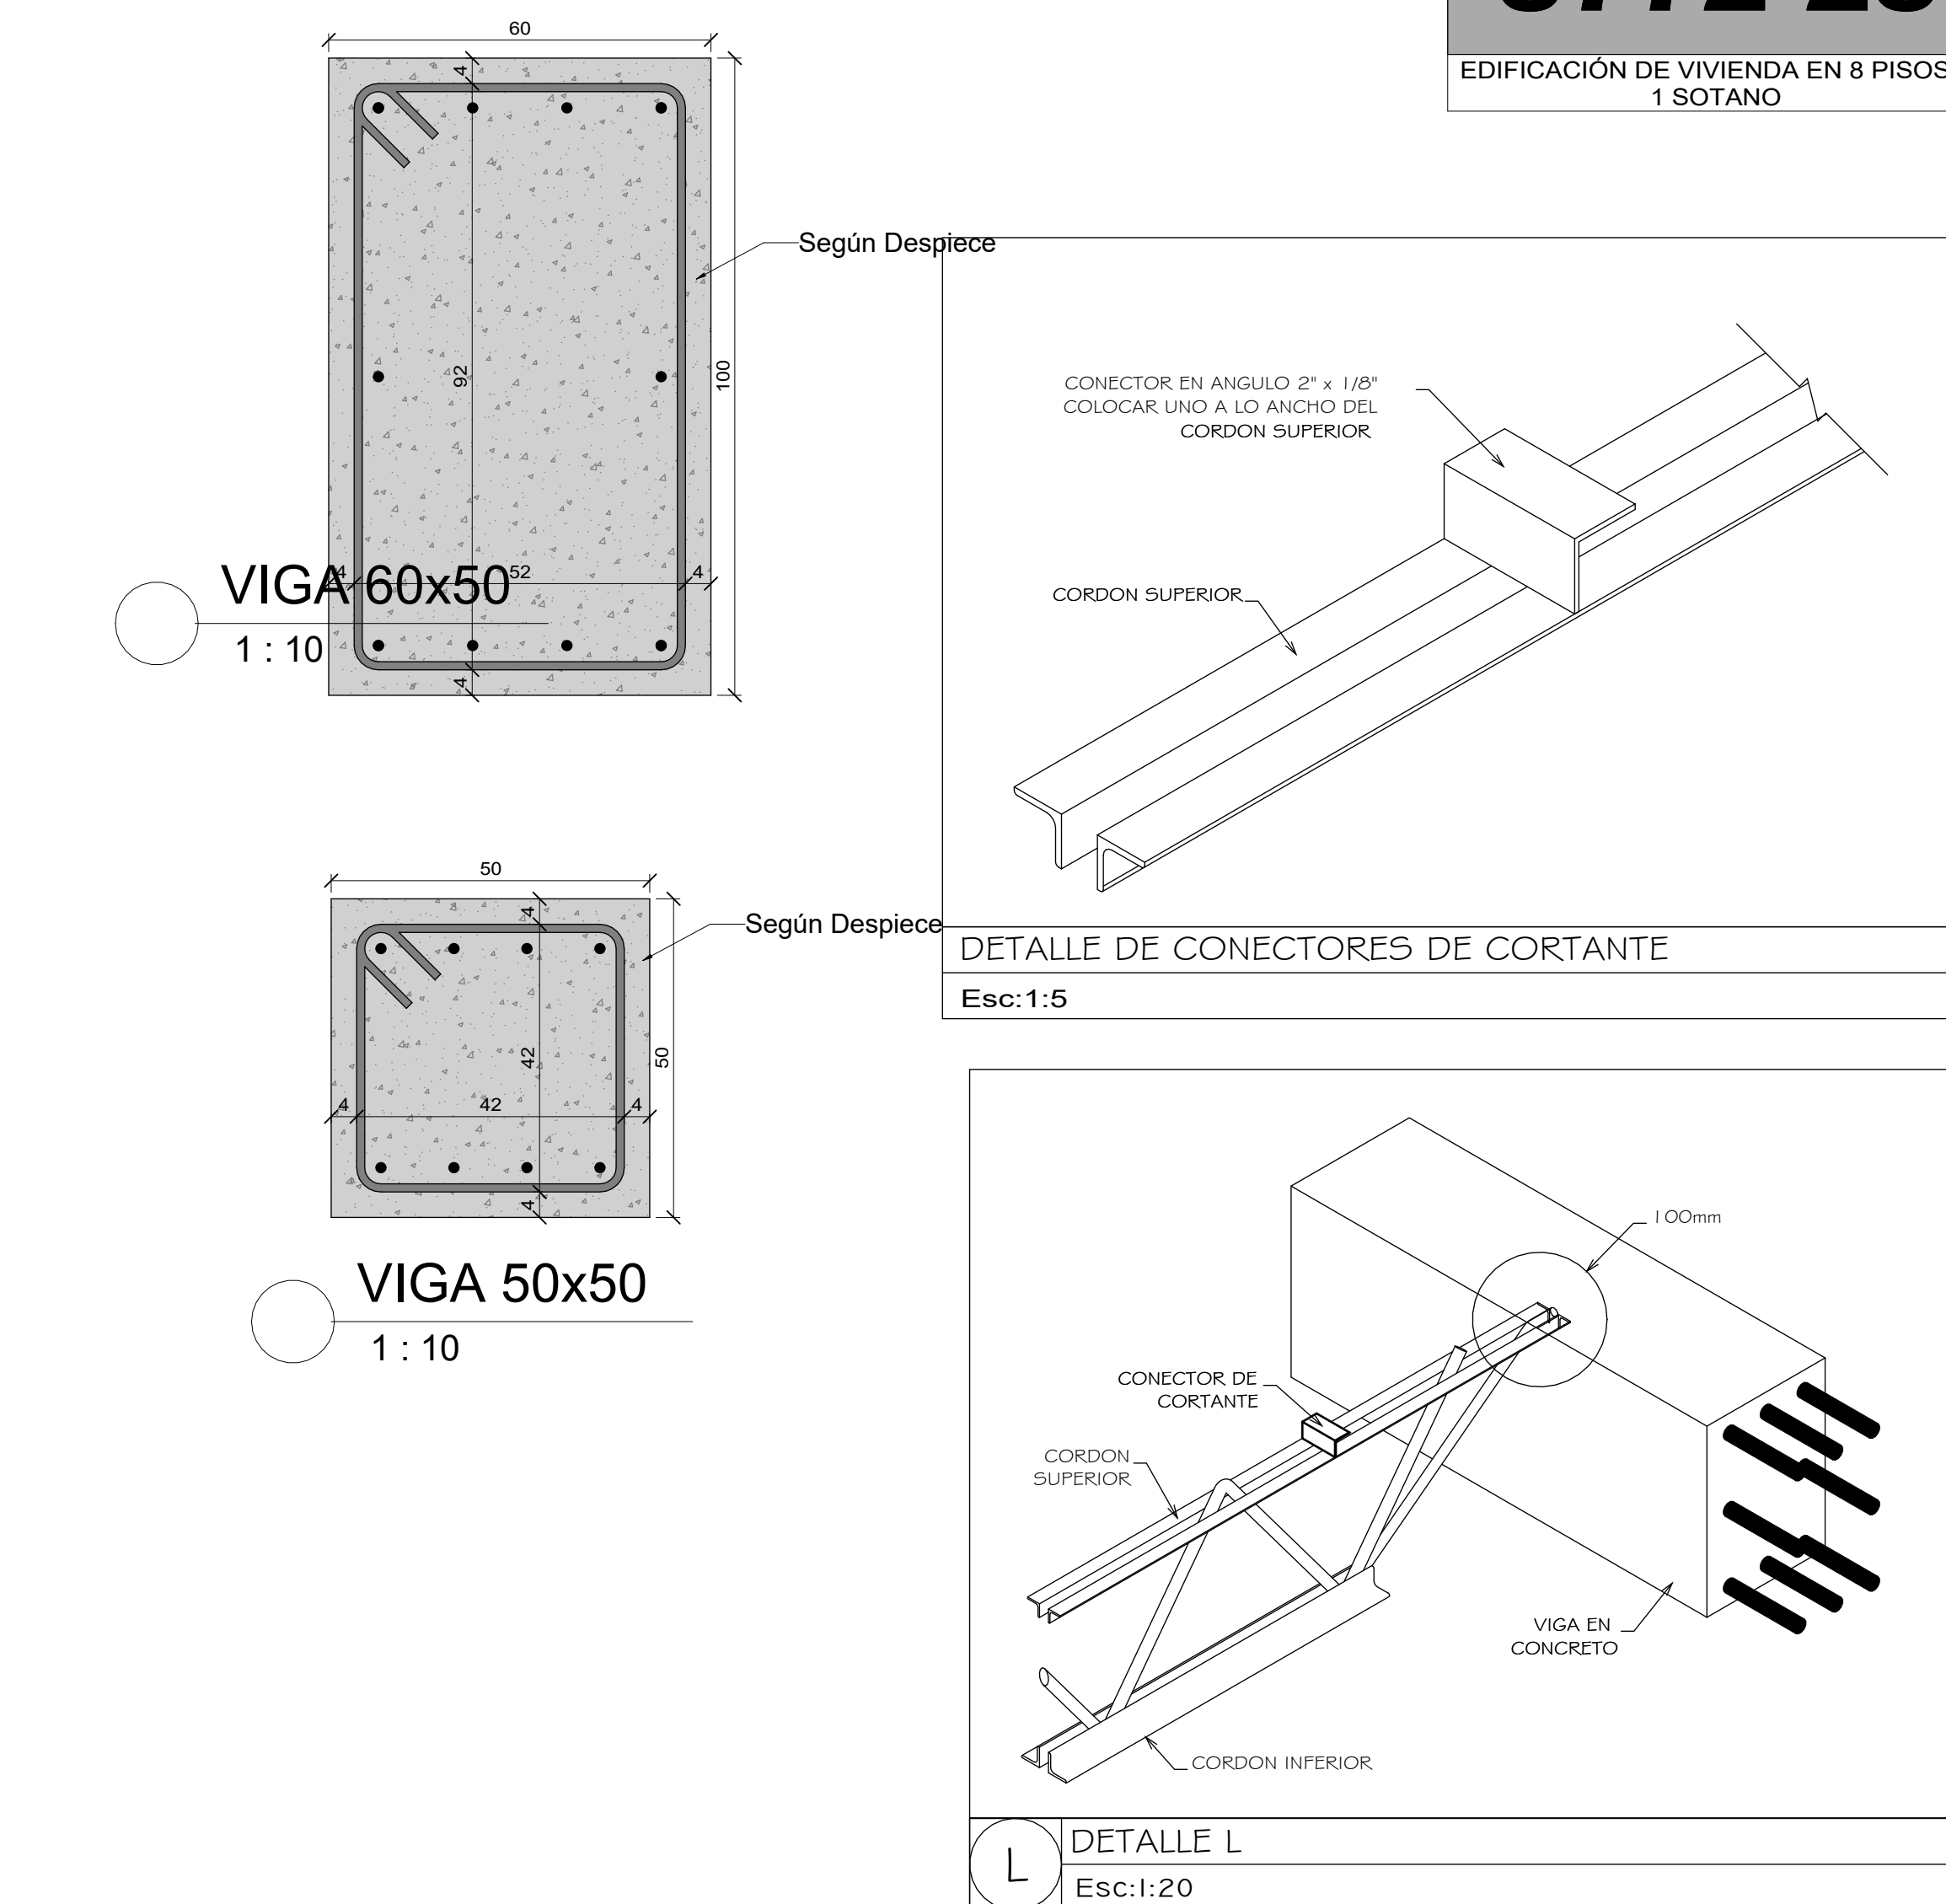


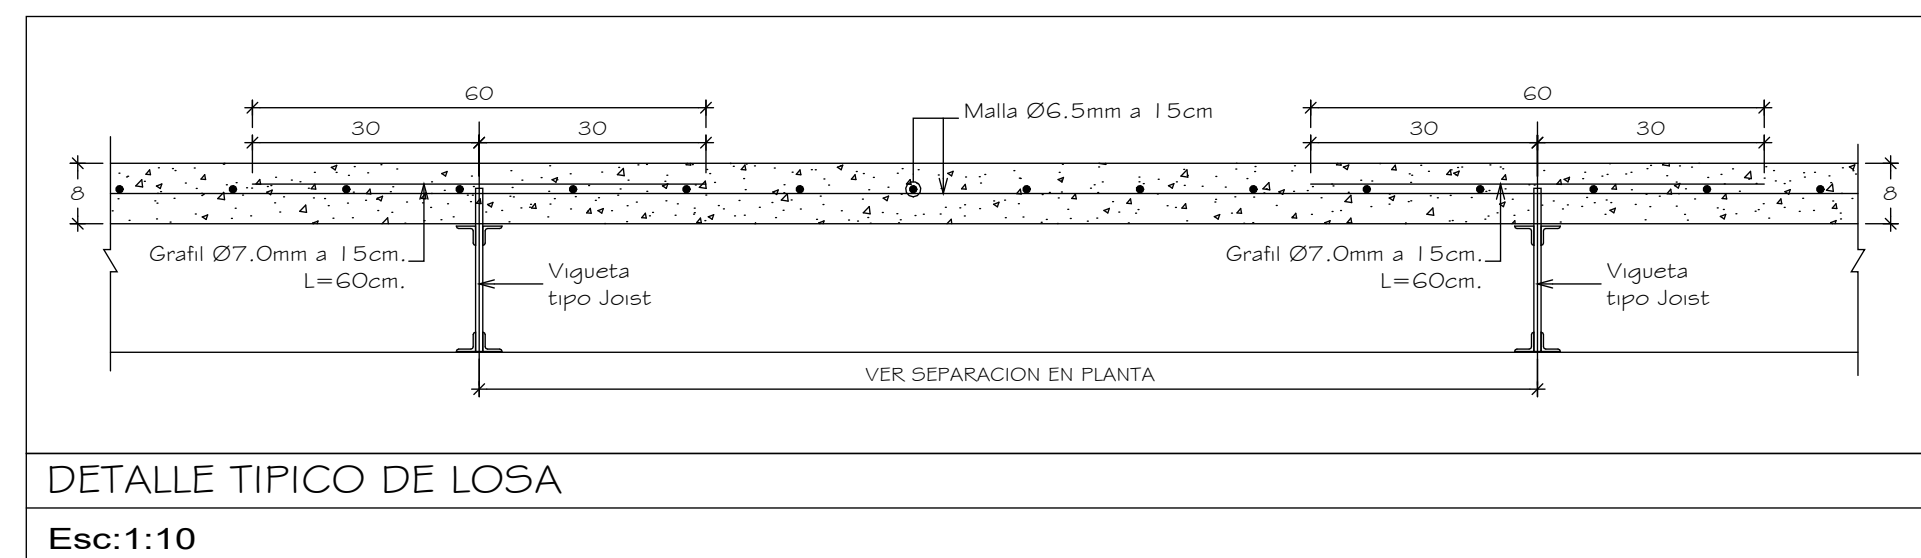

1 PISO 2
1 : 50

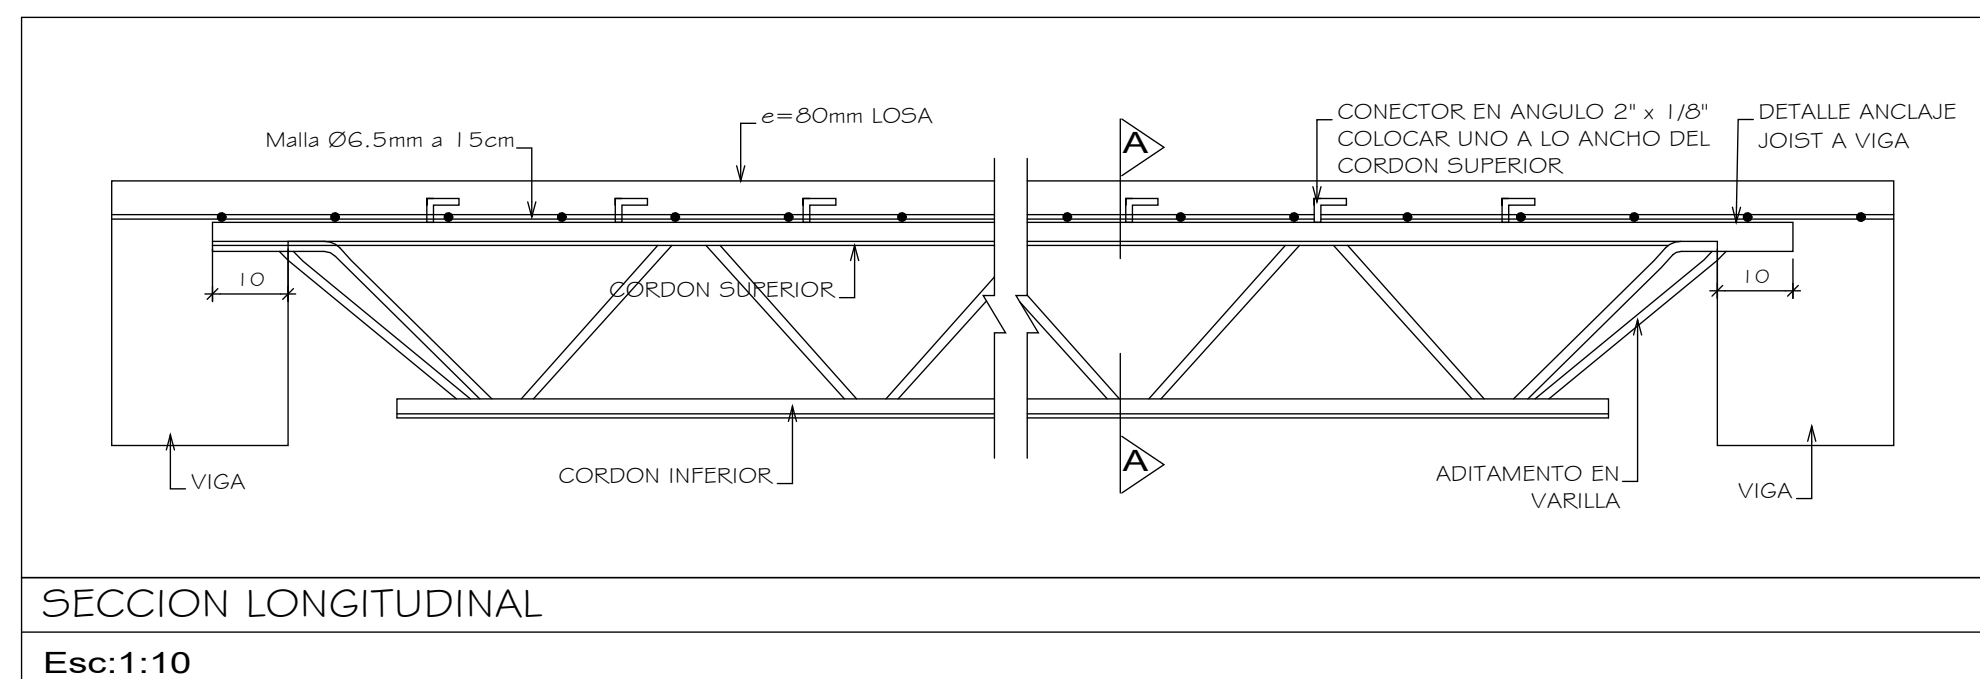

ESPECIFICACIONES DE MATERIALES			
CONCRETO:		C.5.11: El concreto debe mantenerse húmedo por lo menos 7 días después de la fundición.	
CURADO DEL CONCRETO:		C.4.31: Seguir la clase de exposición, para garantizar durabilidad.	
RELACION a/mc PARA MEZCLAS DE CONCRETO:		C.3.3.2: Tamaño nominal nominal del agregado grueso.	
AGREGADOS:		El refuerzo debe cumplir C.21.1.5 (NTC-2289-NT-22043)	
GENERALES:		F y 420 MPa (4200 Kg/cm ²) Corrugado para diámetros iguales o mayores a #2 debe cumplir Norma ASTM A-706. C.3.3.3.4	
BARRAS:		F y 485 MPa (4850 Kg/cm ²) C.3.3.3.5 a C.3.3.3.10 NTC 2806	
MALLAS:			
0			
RESISTENCIA AL FUEGO			
GRUPO DE OCUPACIÓN	CATEGORIA	ELEMENTO	TIEMPO
R2	1	Columnas - Vigas Losas Macizas Muros interiores no portantes	1 (una) hora 1 (una) hora 1 (una) hora
NORMA DISEÑO:		NSR-10	

	a	a	a	a	Emitido Para:	CURADURIA
--	---	---	---	---	---------------	-----------

Propietario: Acción Fiduciaria S.A como vocera y administradora del Fideicomiso FA-6547 Proyecto Florentino	
Proyecto: EDIFICACIÓN DE VIVIENDA EN 8 PISOS Y 1 SOTANO BARRIO EL PEÑON	
Proyecto N°: 3772-25	
Unidad Estructural: EDIFICIO	
Fecha: FEBRERO 2026	Escala: Como se indica

Proyecto Estructural:	
	
Revisó:	
ING. JUAN RAUL SOLARTE G. Mat. 476 CAUCA	
Diseño:	
ING. JULIAN ENRIQUEZ	
Colaboró: ING. FABIAN ROJAS	Dibujó: RENÉ MONTAÑO BOTE
Contiene:	
PLANO NIV. 2	
Plano N°: 102	Versión: