







ESTE PLANO ES PROPIEDAD INTELECTUAL DE SOLARTE Y CIA. INGENIEROS CALCULISTAS S.A. SE PROHIBE SU REPRODUCCION O MODIFICACION PARCIAL O TOTAL. EN CASO DE MODIFICARSE VO UTILIZARSE INDEBIDAMENTE. LA EMPRESA QUEDA EXENTA DE CUALQUIER RESPONSABILIDAD QUE PUEDA DERIVAR DE SU UTILIZACION.

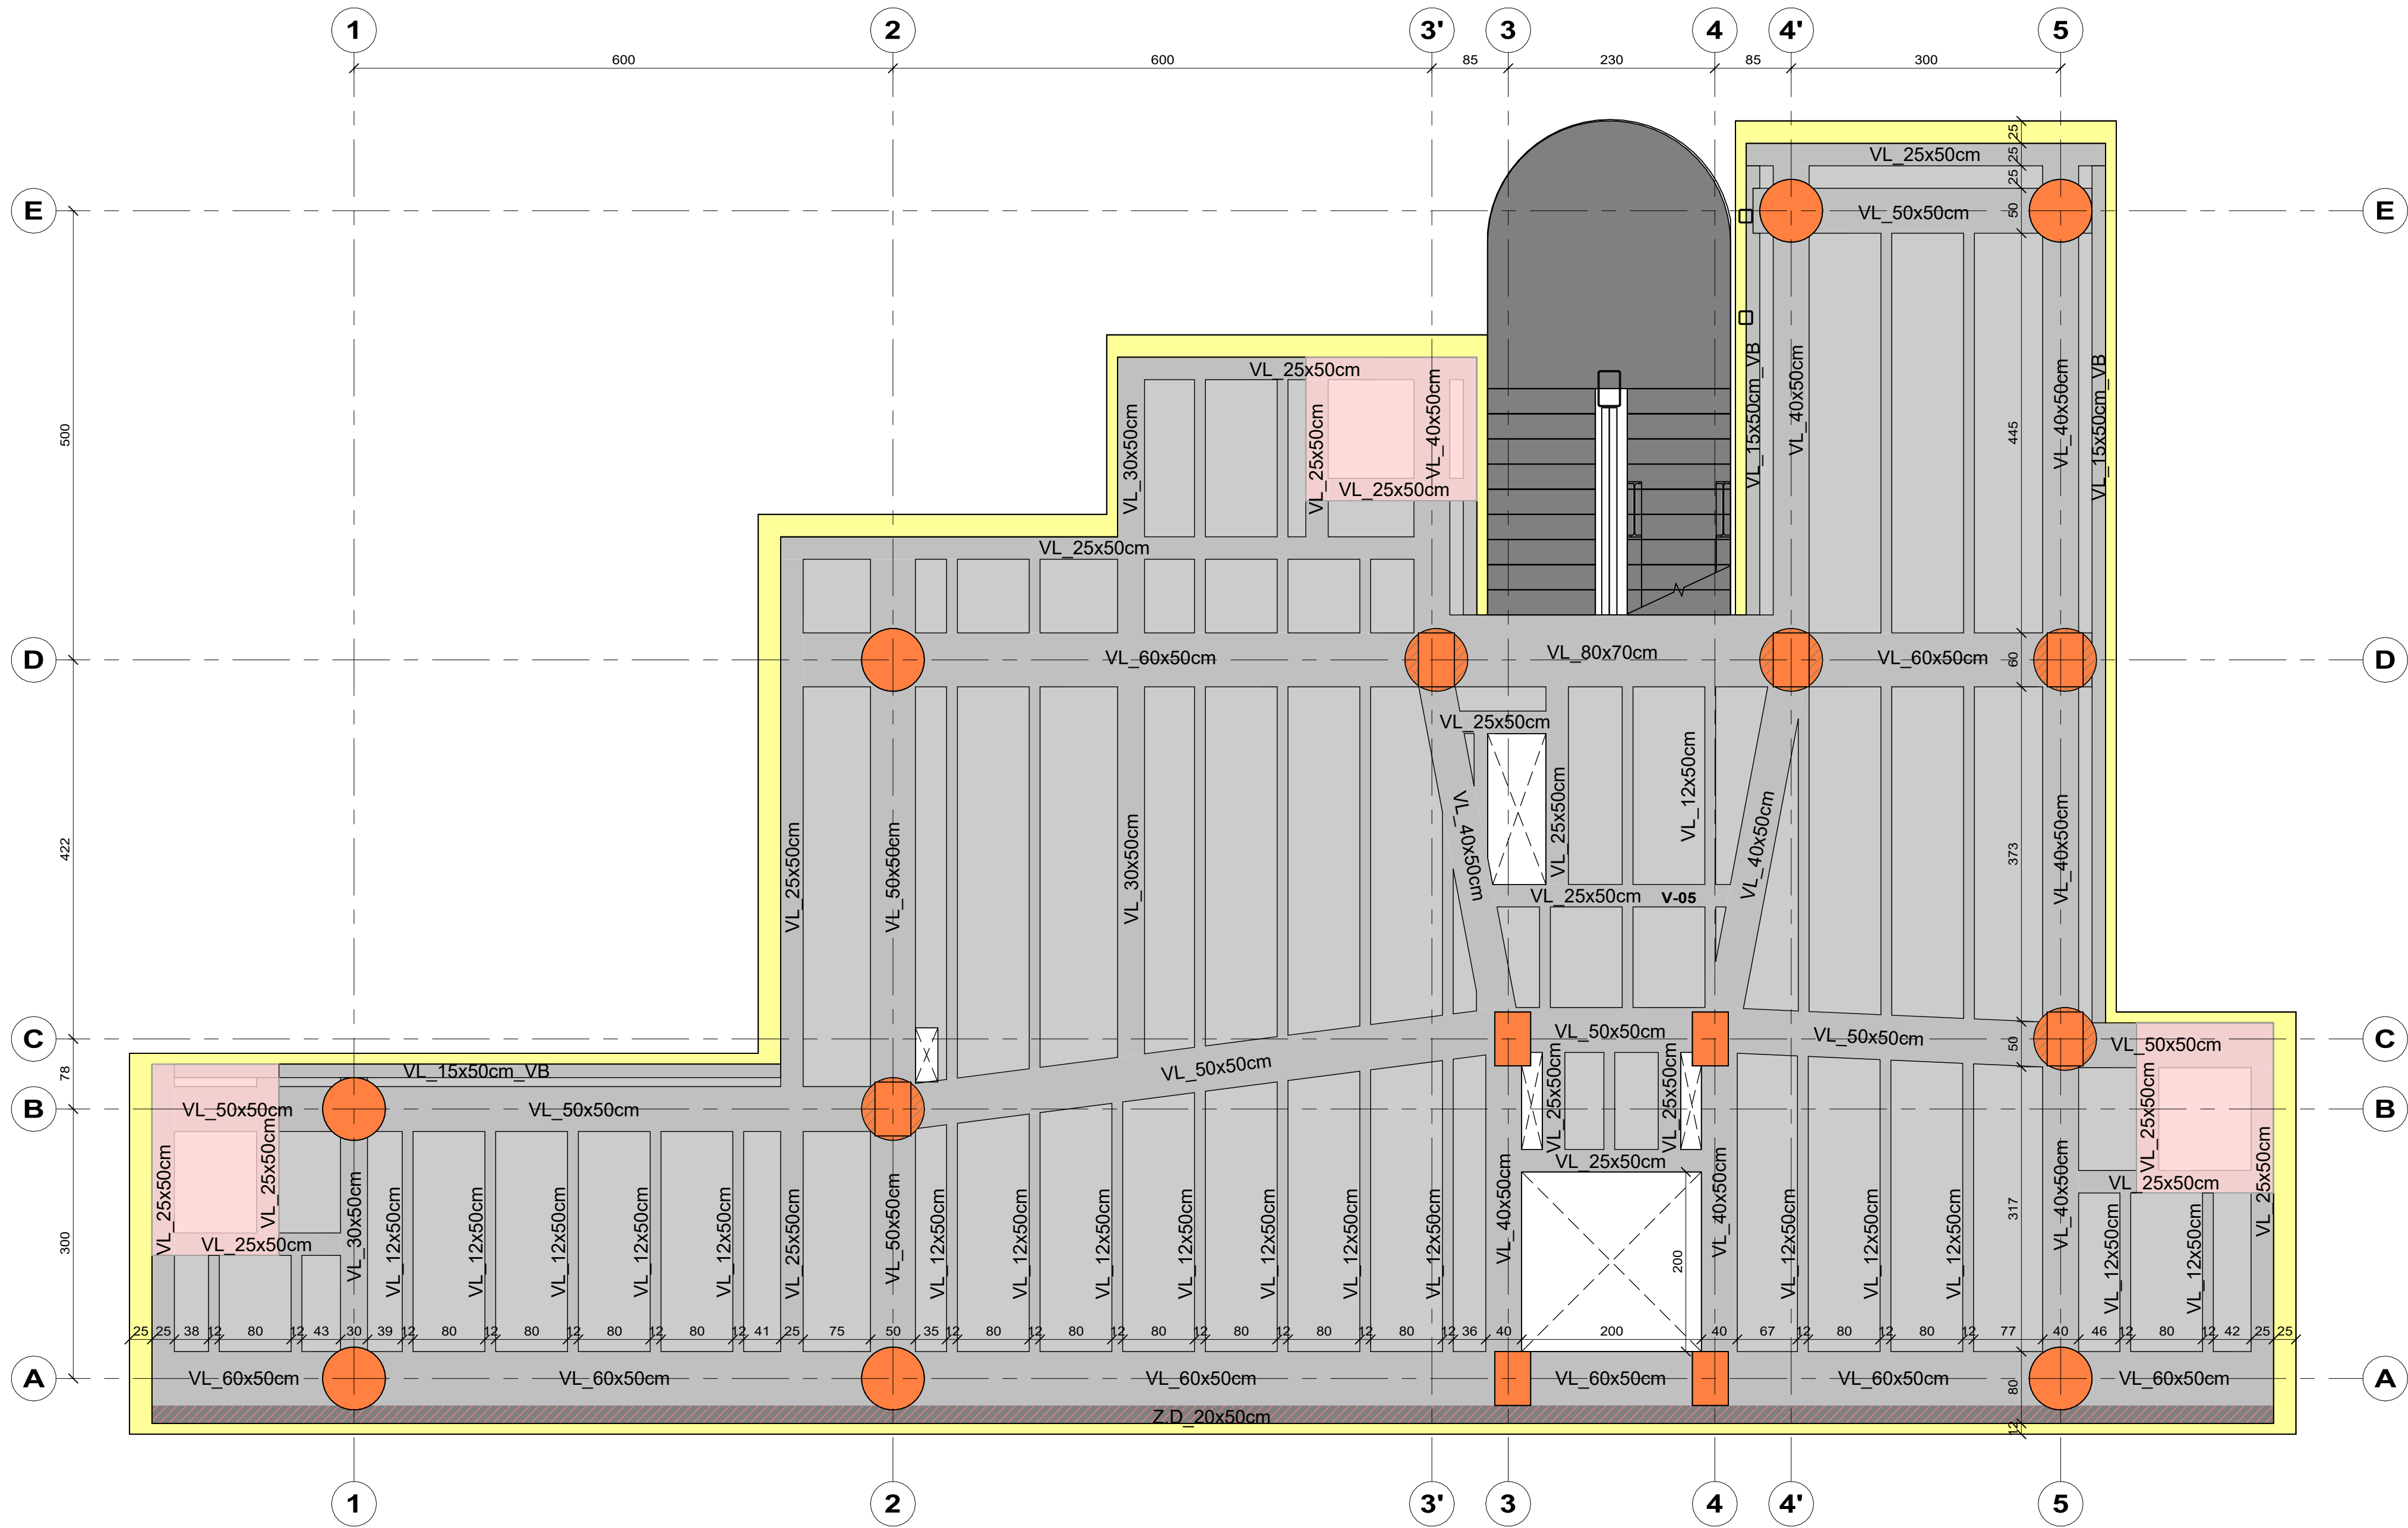



1 PISO 3
1 : 50

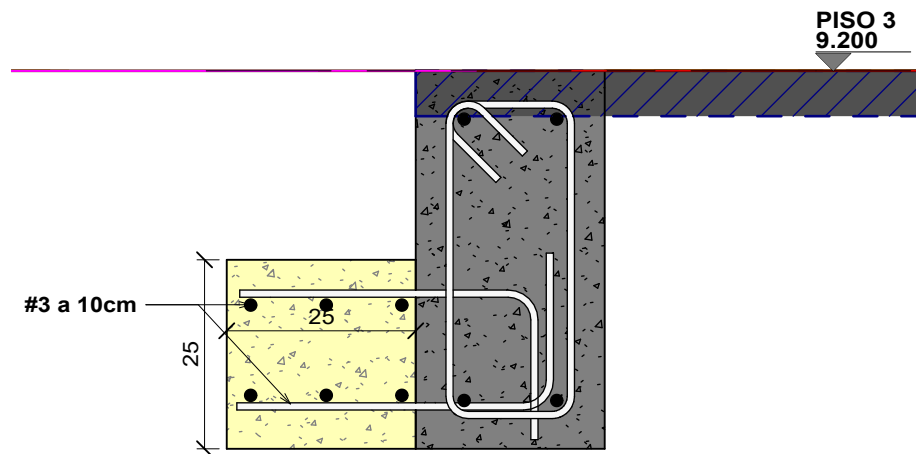

2 Detalle tipo
1 : 10

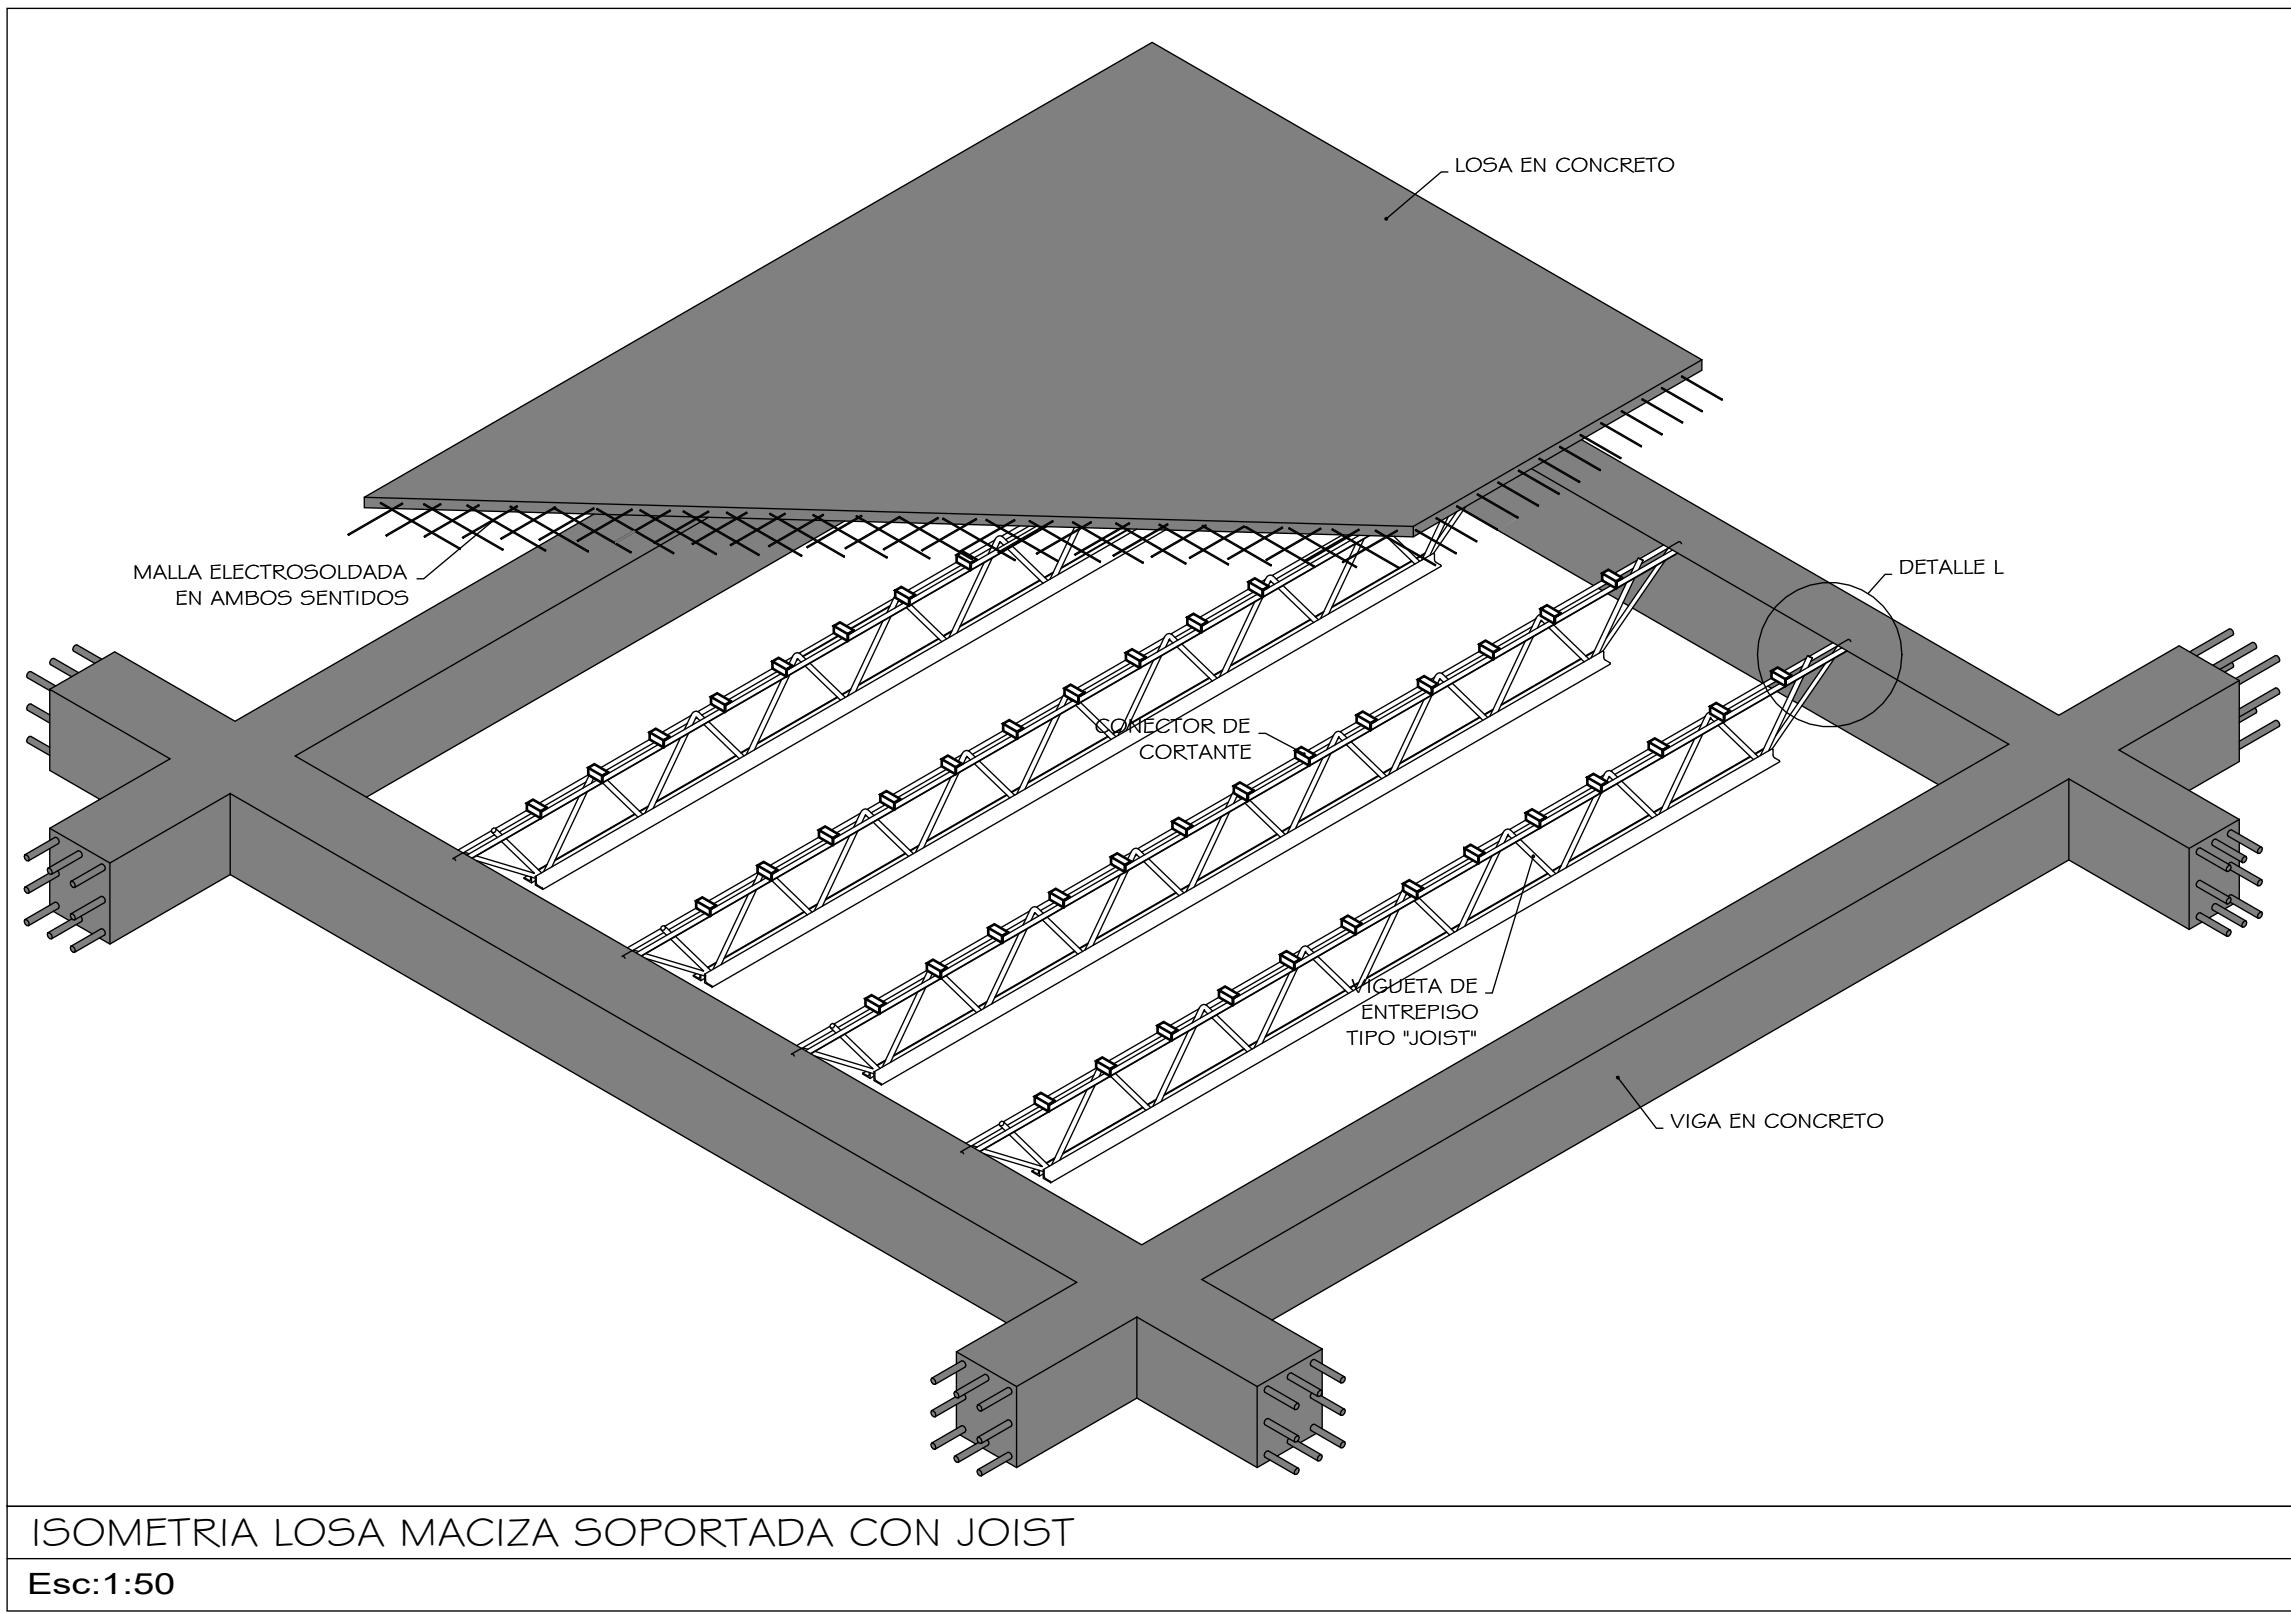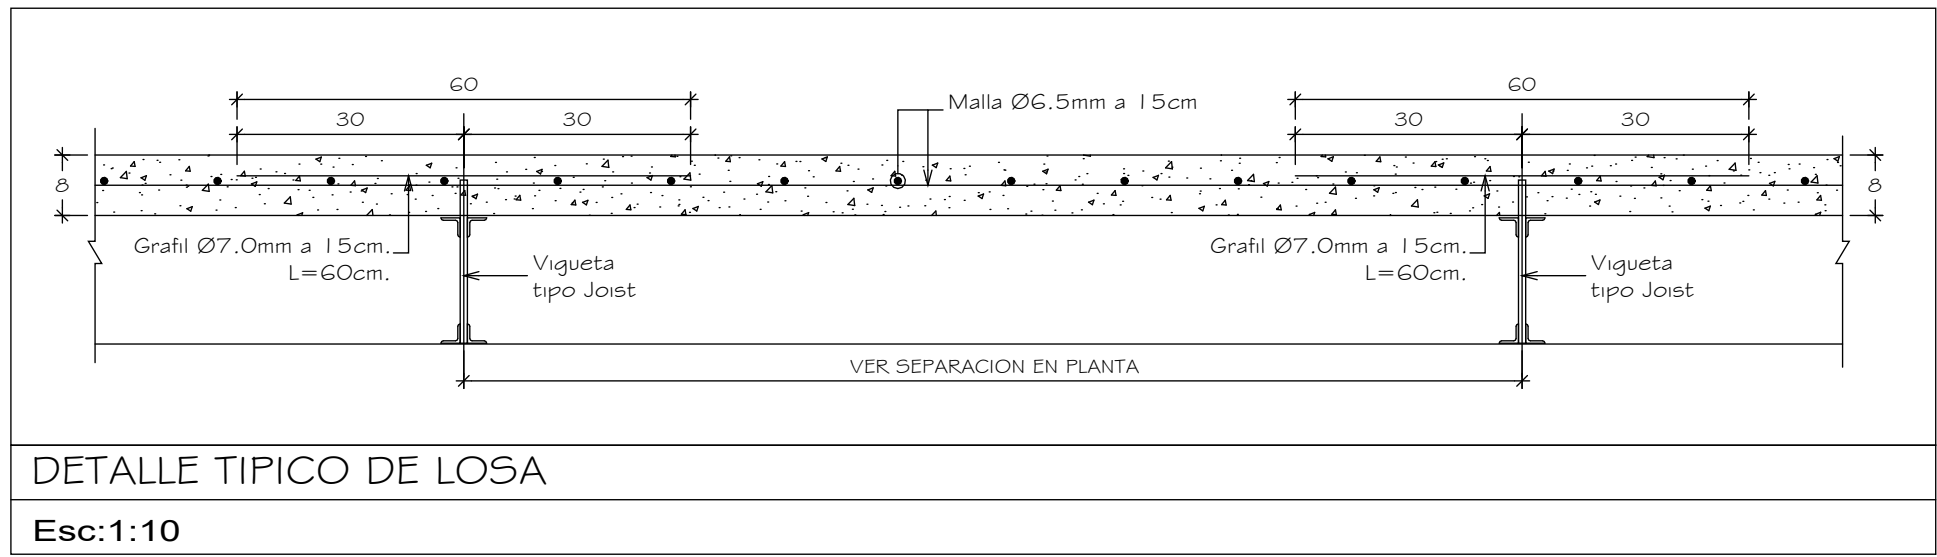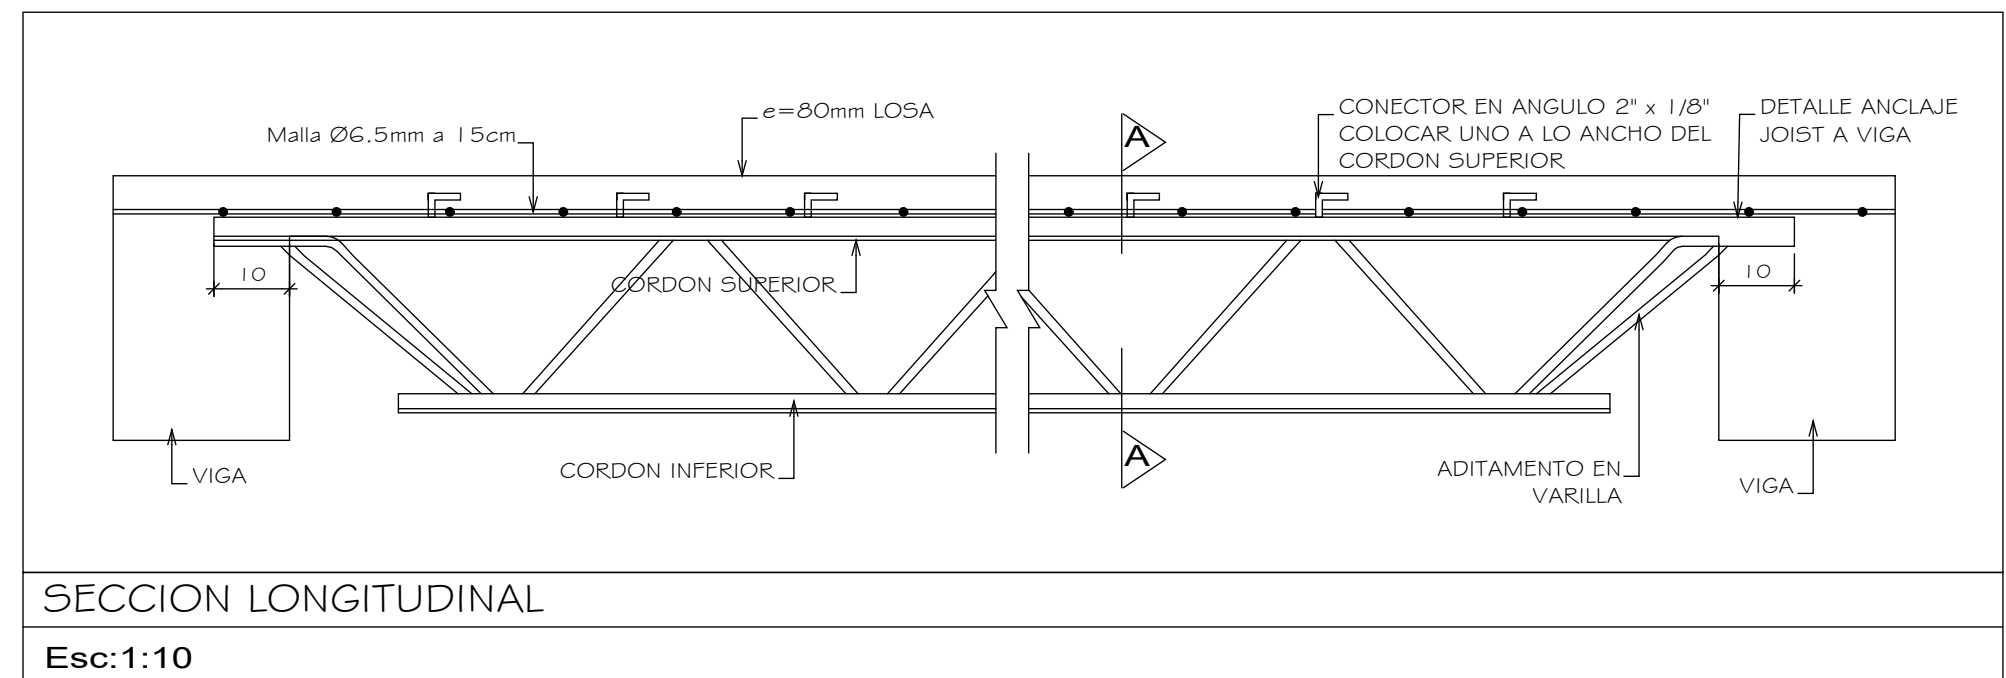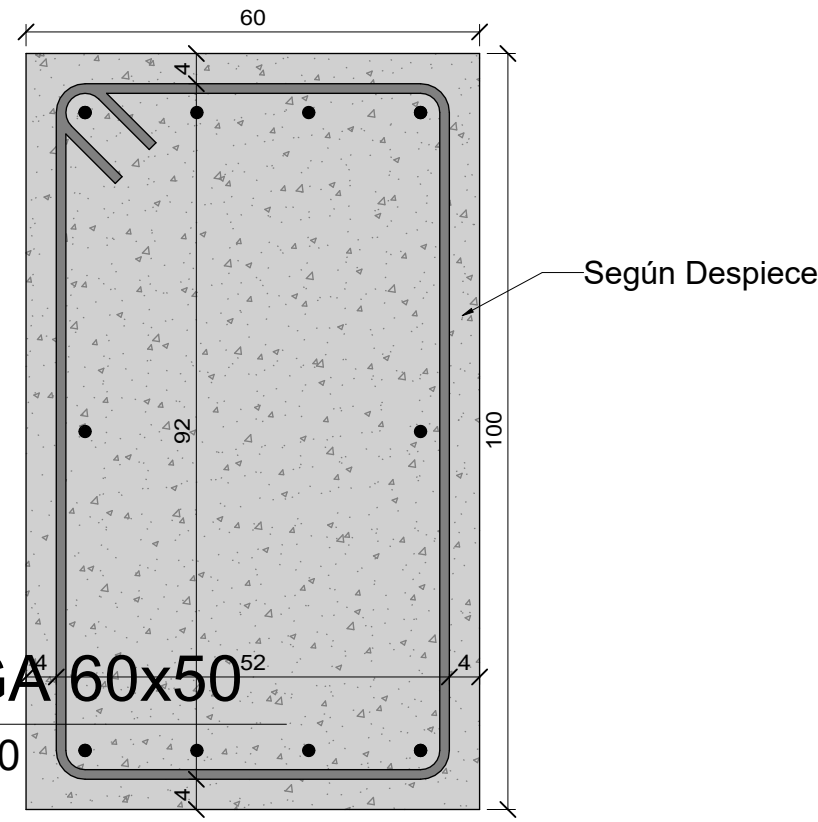

ISOMETRIA LOSA MACIZA SOPORTADA CON JOIST
Esc:1:50

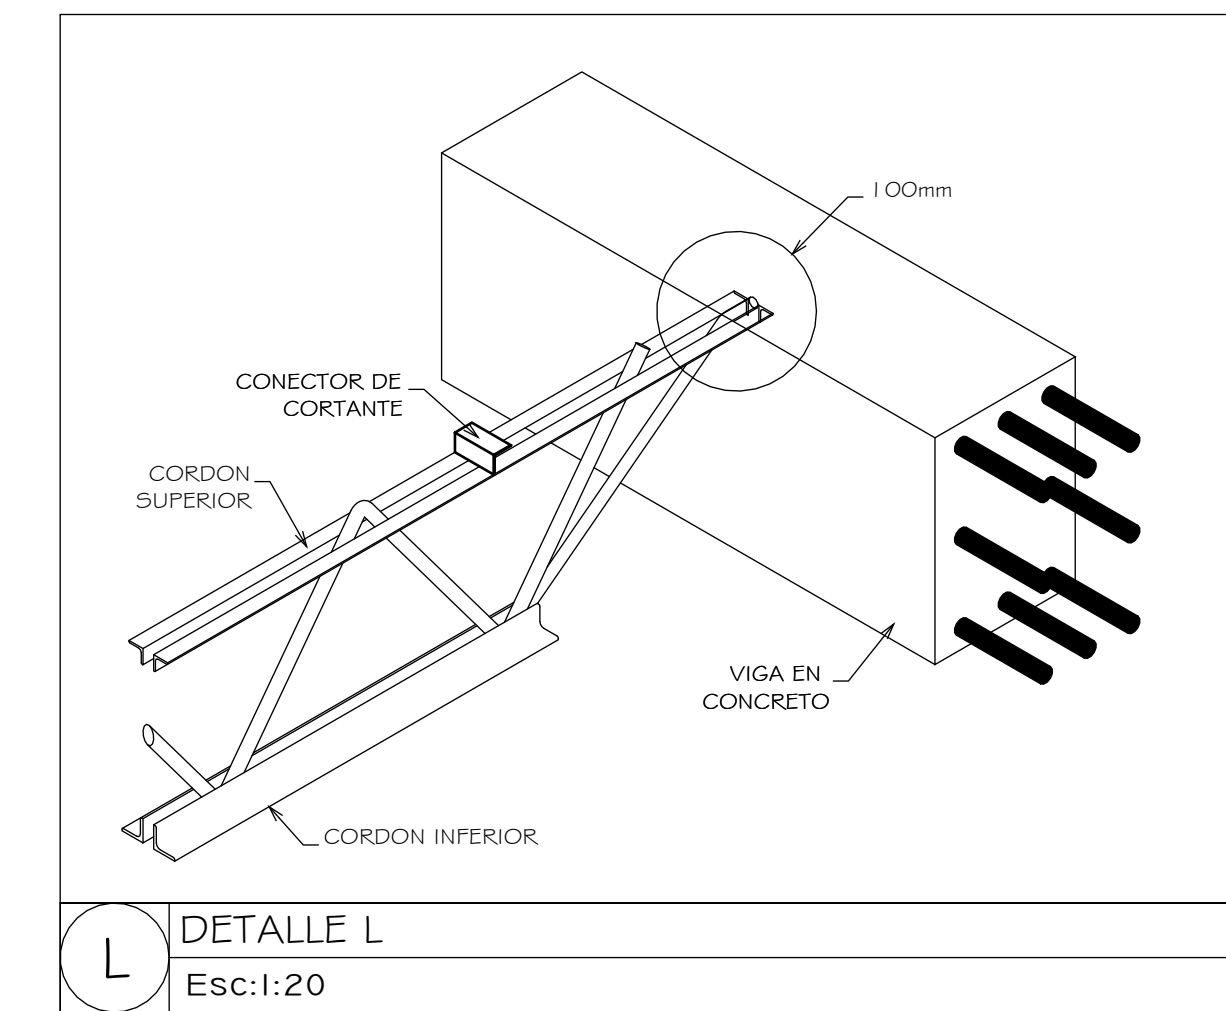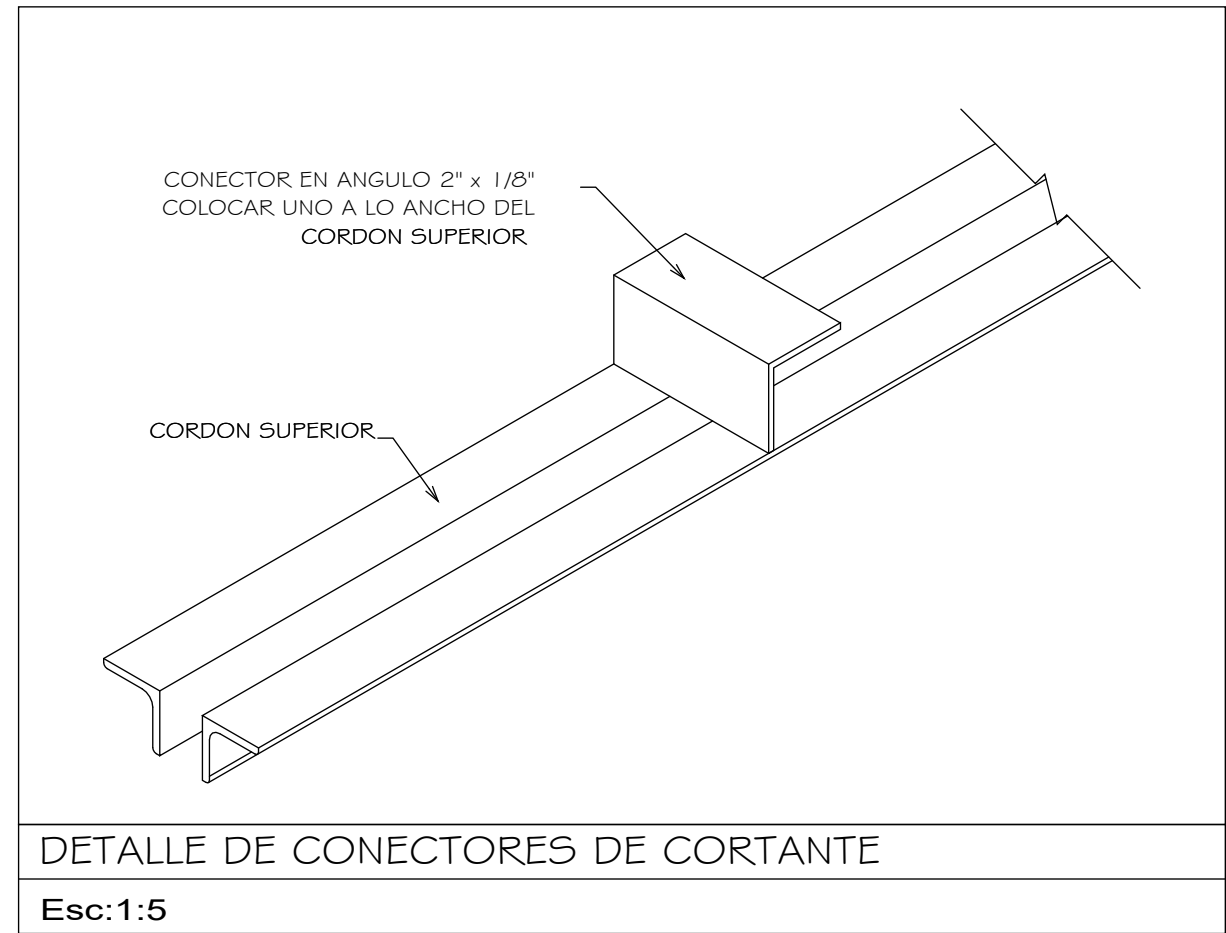

ESPECIFICACIONES DE MATERIALES

CONCRETO:	C.5.11: El concreto debe mantenerse húmedo por lo menos 7 días después de la fundición.
CURADO DEL CONCRETO:	C.4.3.1: Según la clase de exposición, para garantizar durabilidad.
RELACION a/mc PARA MEZCLAS DE CONCRETO:	C.3.3.2: Tamaño máximo nominal del agregado grueso.
AGREGADOS:	C.3.3.2: Tamaño máximo nominal del agregado grueso.
GENERALES:	El refuerzo debe cumplir C.21.1.5 (NTC2289-NTC2043)
BARRAS:	Fy = 420 Mpa (4200 Kg/cm²) Corrugado para diámetros iguales ó mayores a #2 debe cumplir Norma ASTM A-706. C.3.5.3.4
MALLAS:	Fy ≥ 485 Mpa (4850 Kg/cm²) C.3.5.3.5 a C.3.5.3.10 NTC 5806

RESISTENCIA AL FUEGO

GRUPO DE SOLICITACION	CATEGORIA	ELEMENTO	TIEMPO
R2	1	Columnas - Vigas	1 (una) hora
		Losas Macizas	1 (una) hora
		Muros interiores no portantes	1 (una) hora

NORMA DISEÑO: NSR-10

CURADURIA

Propietario:	Acción Fiduciaria S.A como vocera y administradora del Fideicomiso FA-6547 Proyecto Florentino		Proyecto Estructural:		
Revisó:	ING. JUAN RAUL SOLARTE G. Mat. 876 CAUCA		Diseño:	ING. JULIAN ENRIQUEZ	
Proyecto:	EDIFICACIÓN DE VIVIENDA EN 8 PISOS Y 1 SOTANO		Colaboró:	ING. FABIAN ROJAS	Dibujó: RENÉ MONTAÑO BOTERO
Proyecto N°:	3772-25		Contiene:	PLANO NIV. 3	
Unidad Estructural:	EDIFICIO		Fecha:	FEBRERO 2026	Escala: Como se indica
Plano N°:	103		Versión:		

3772-25

EDIFICACIÓN DE VIVIENDA EN 8 PISOS Y 1 SOTANO