


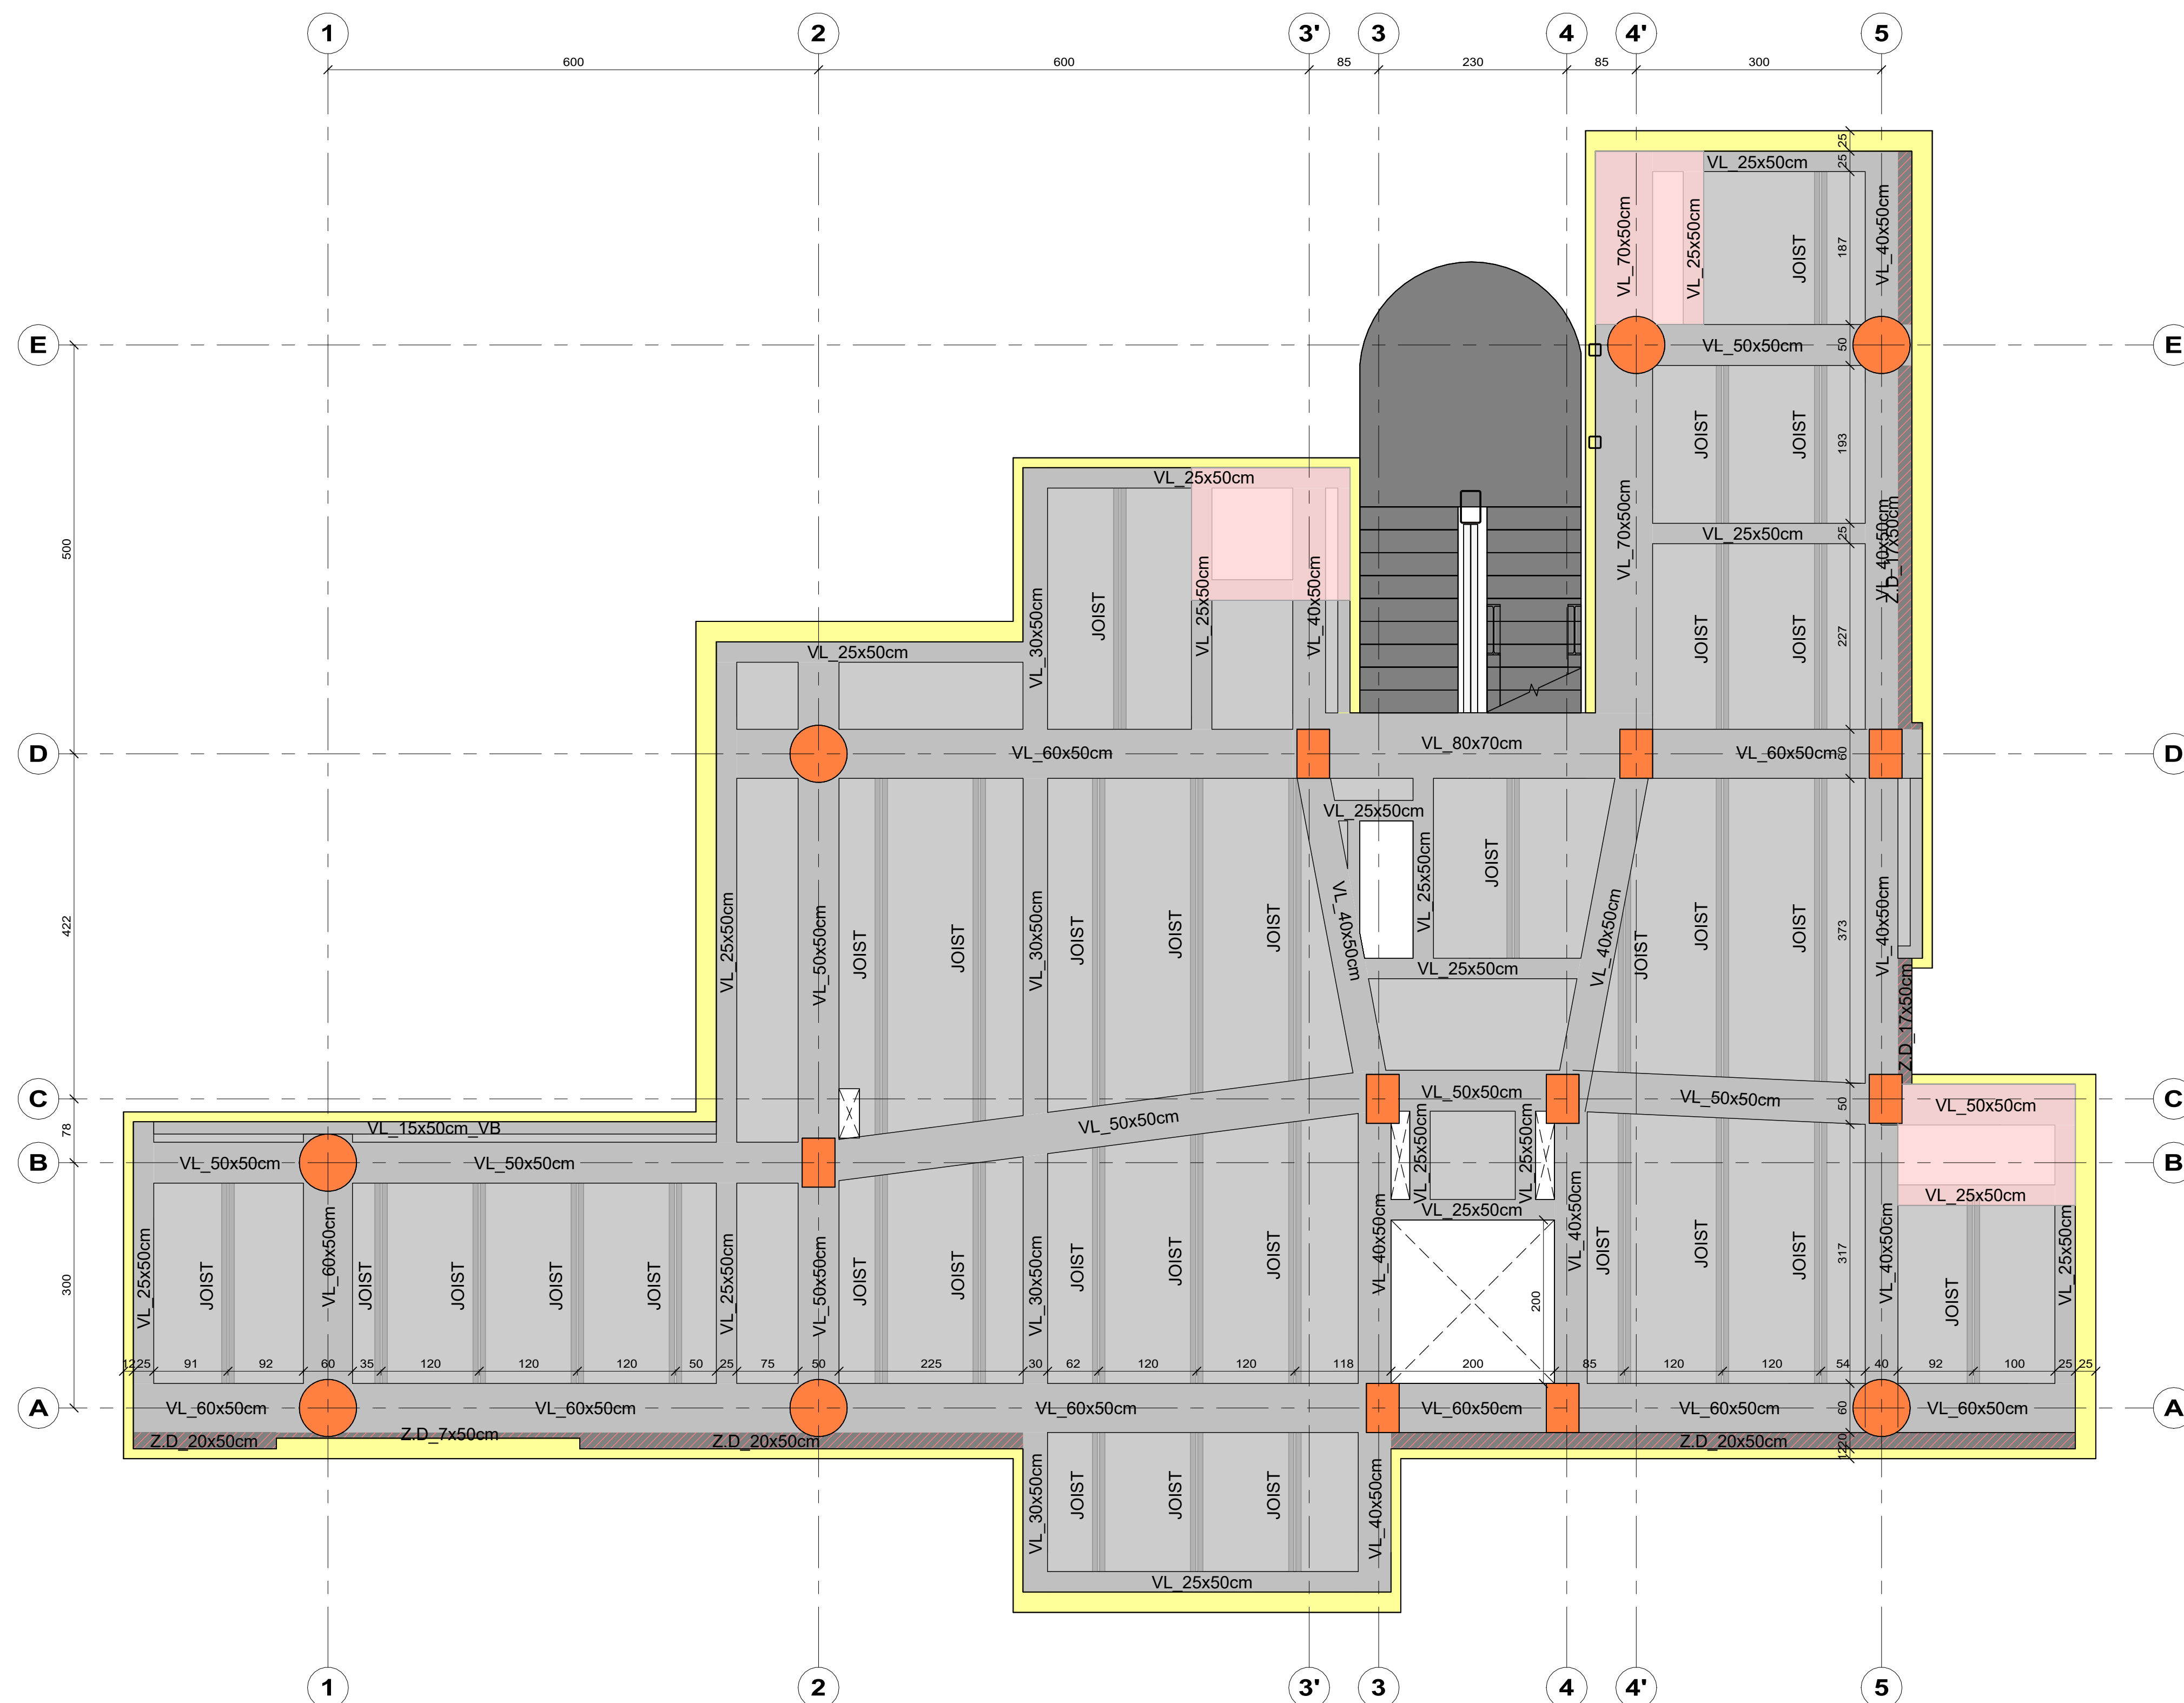
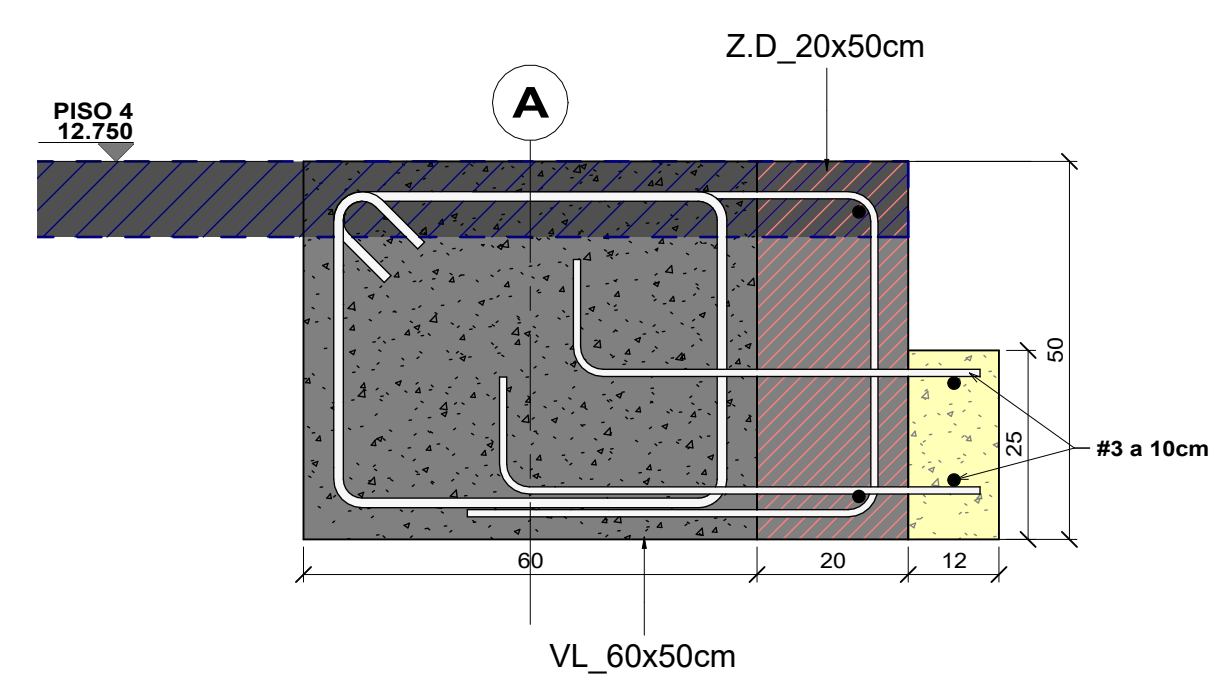
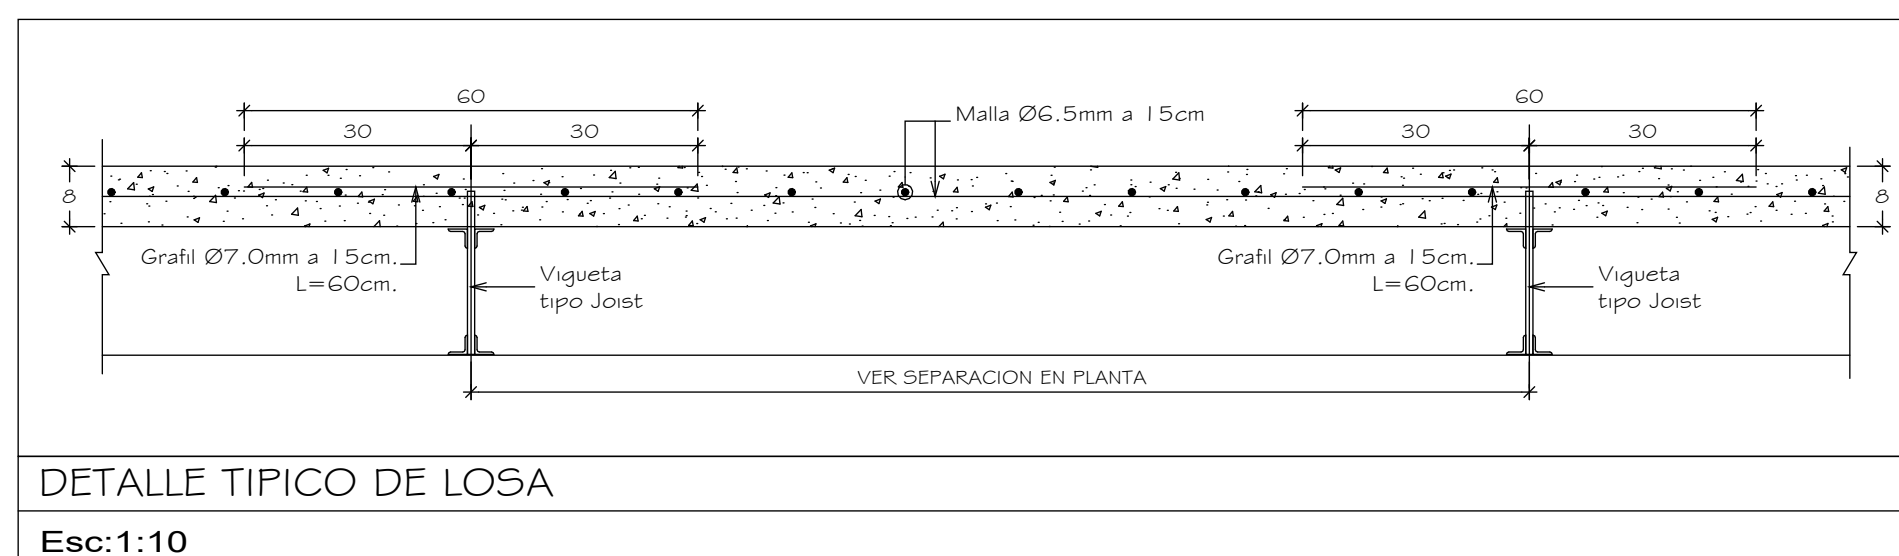
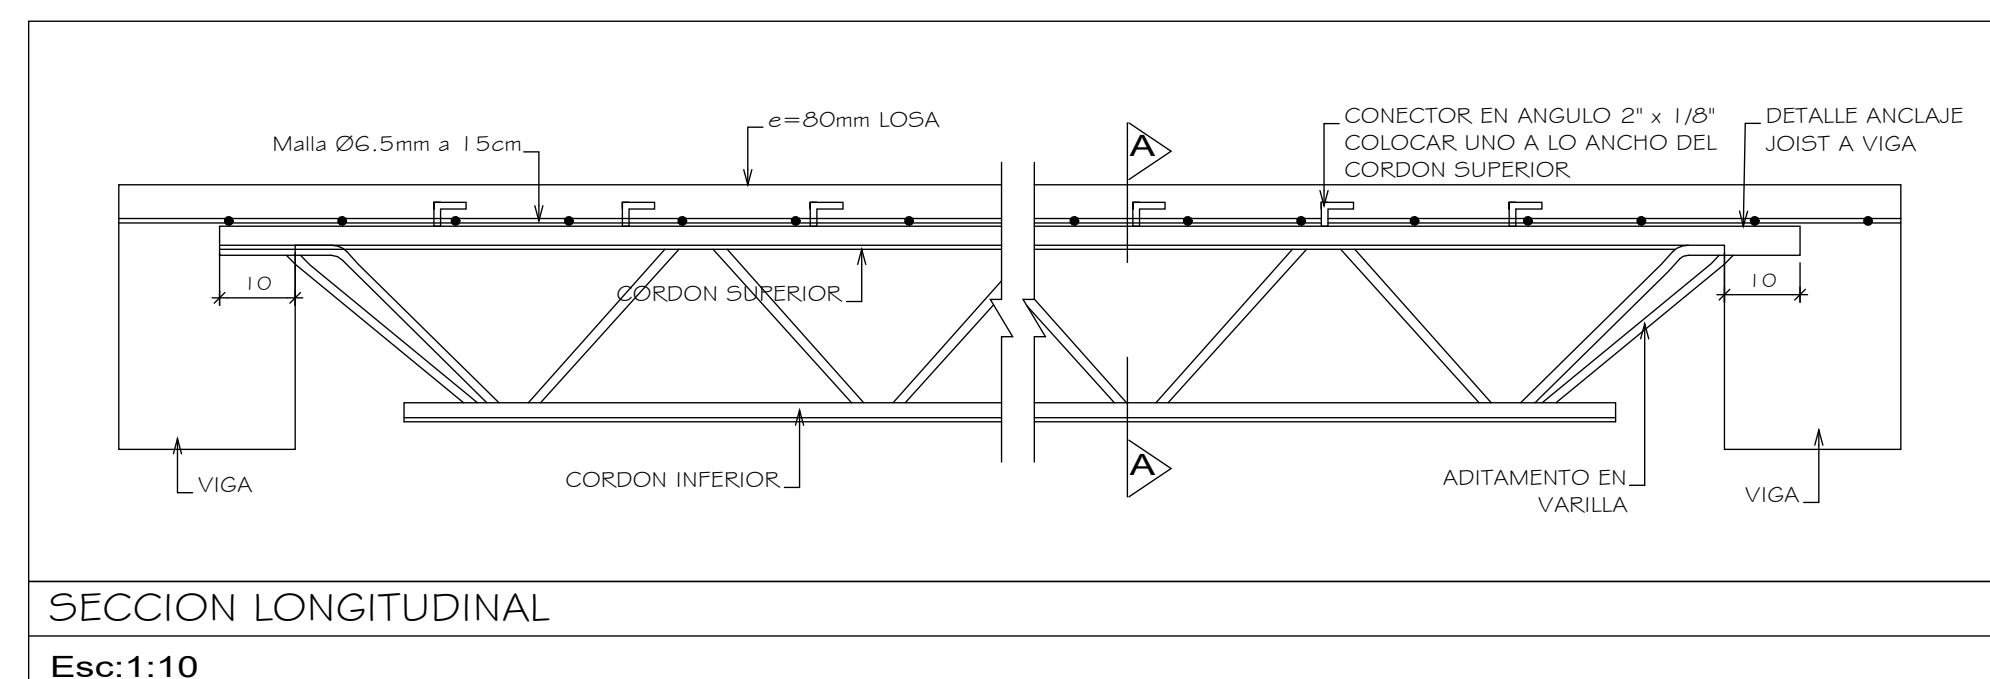


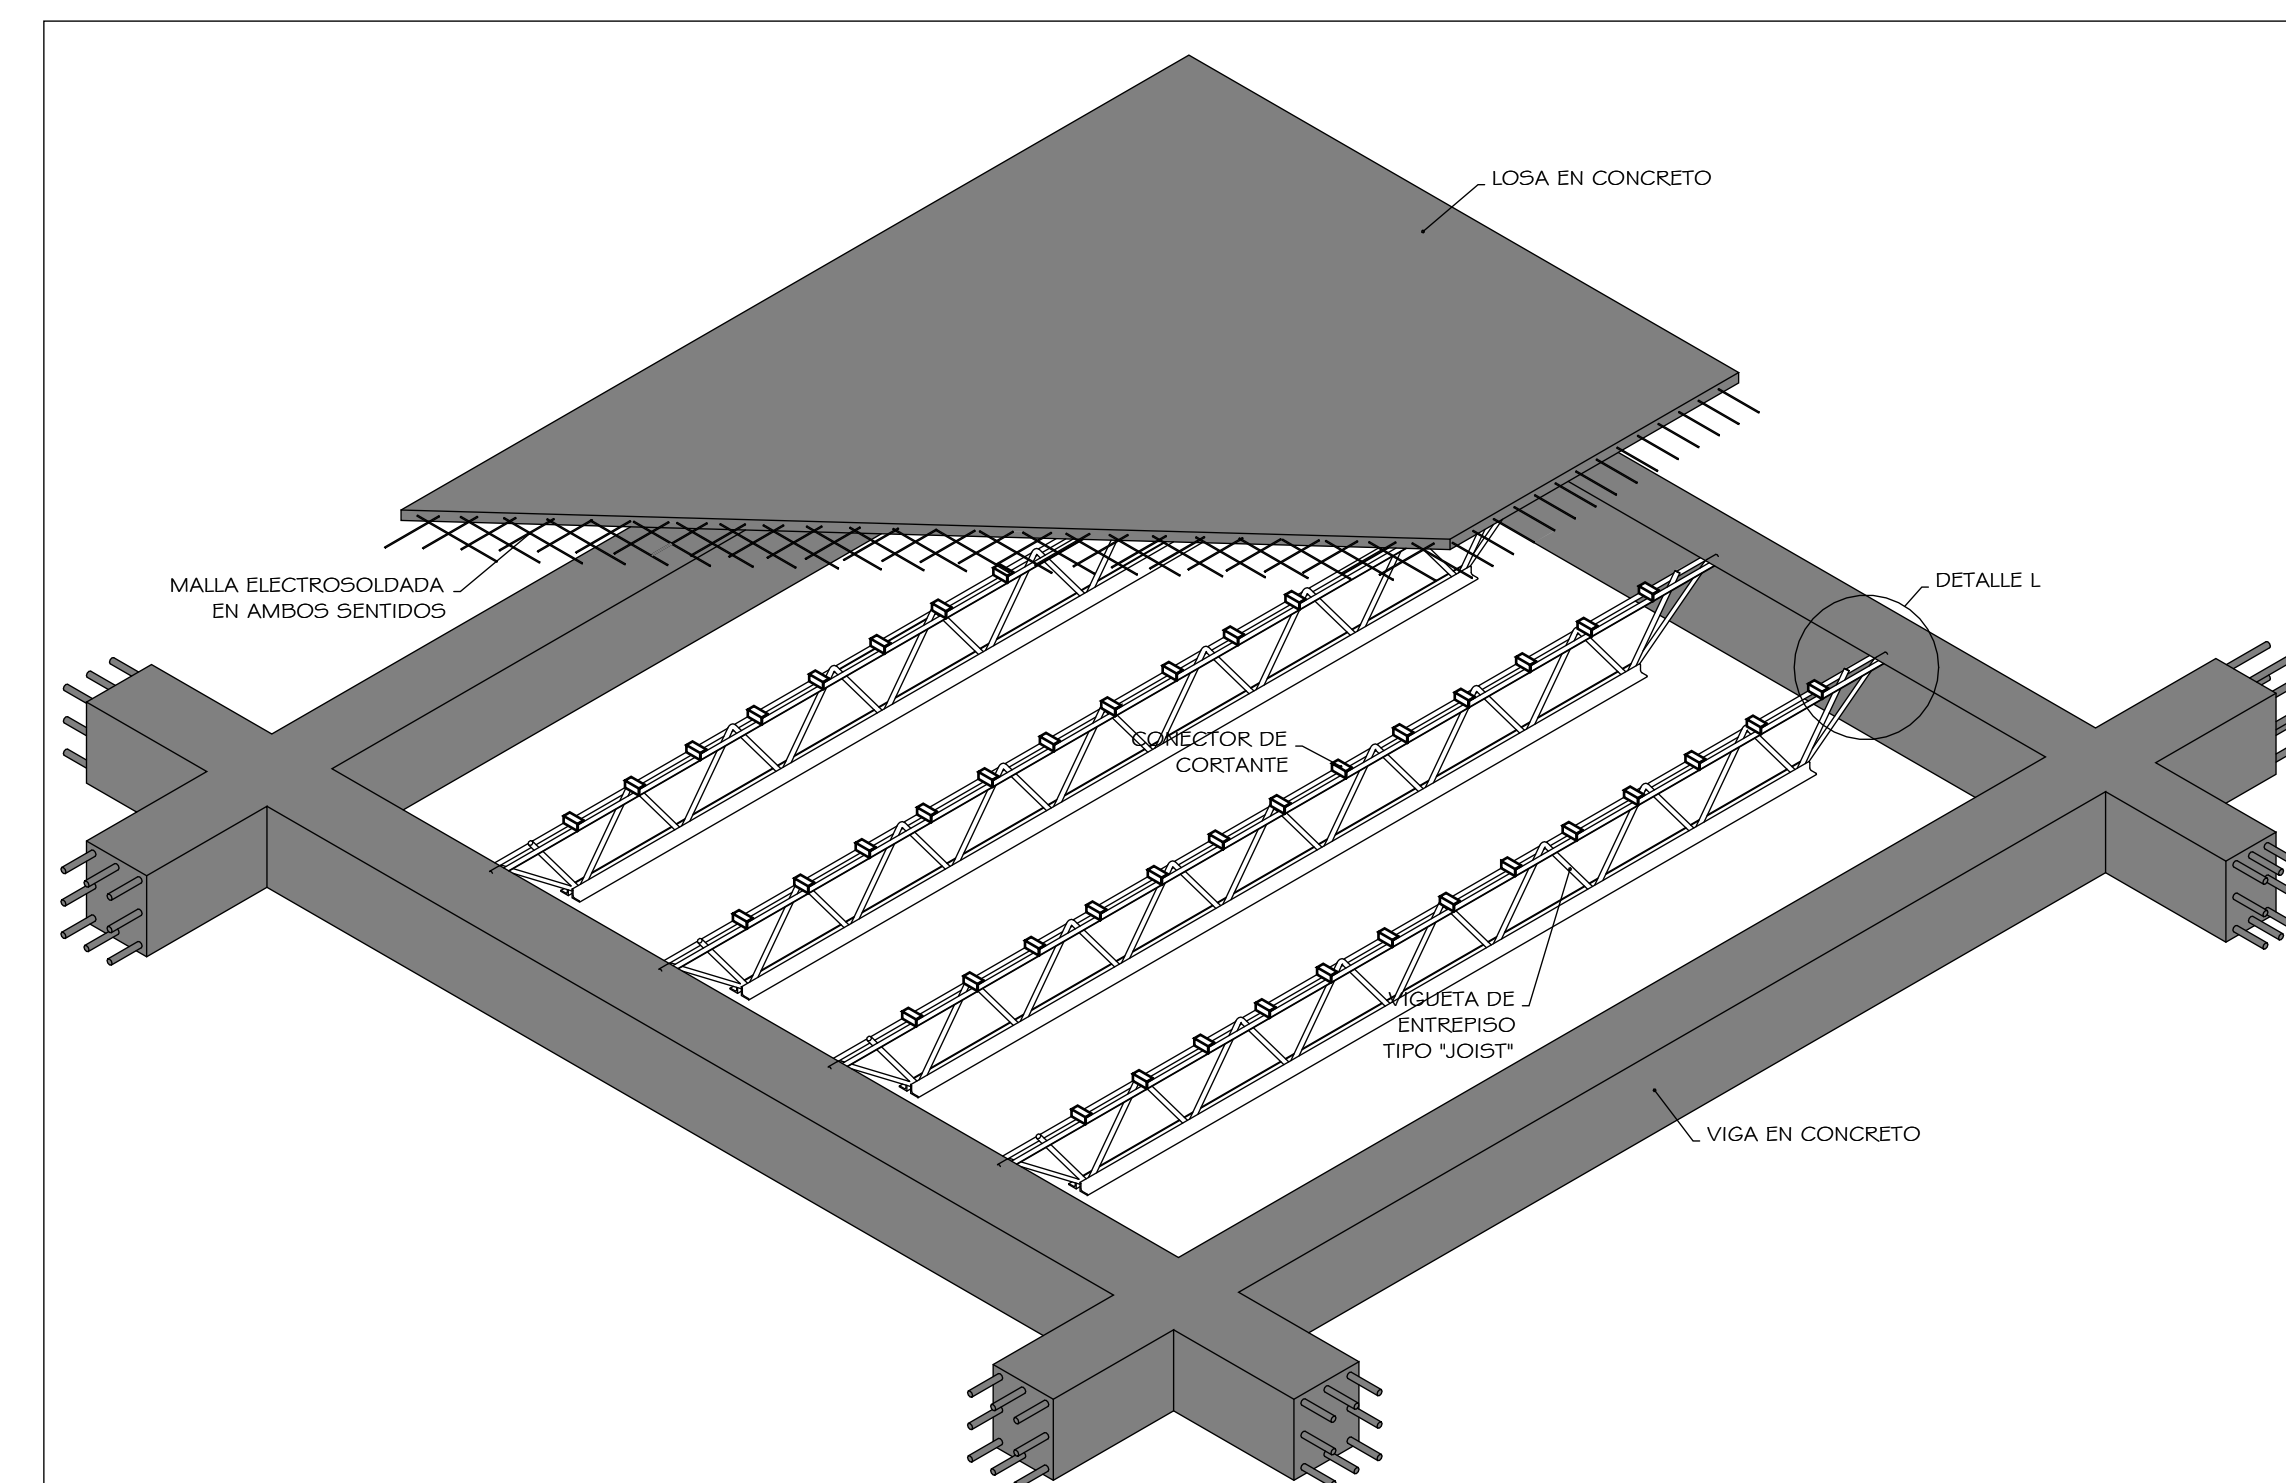

1 PISO 4
1 : 50

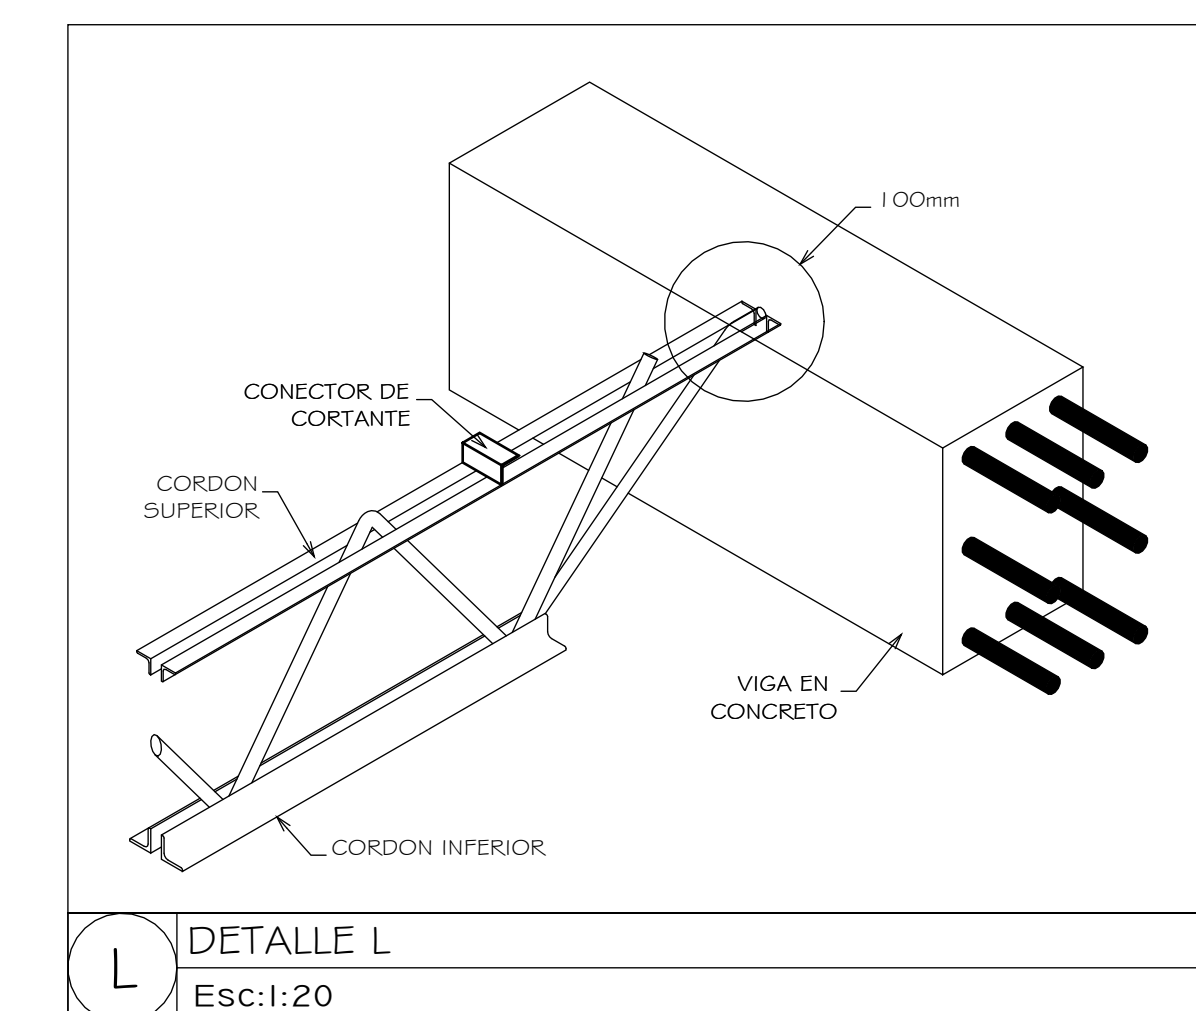

2 Det. Tipo Zona Dura
1 : 10

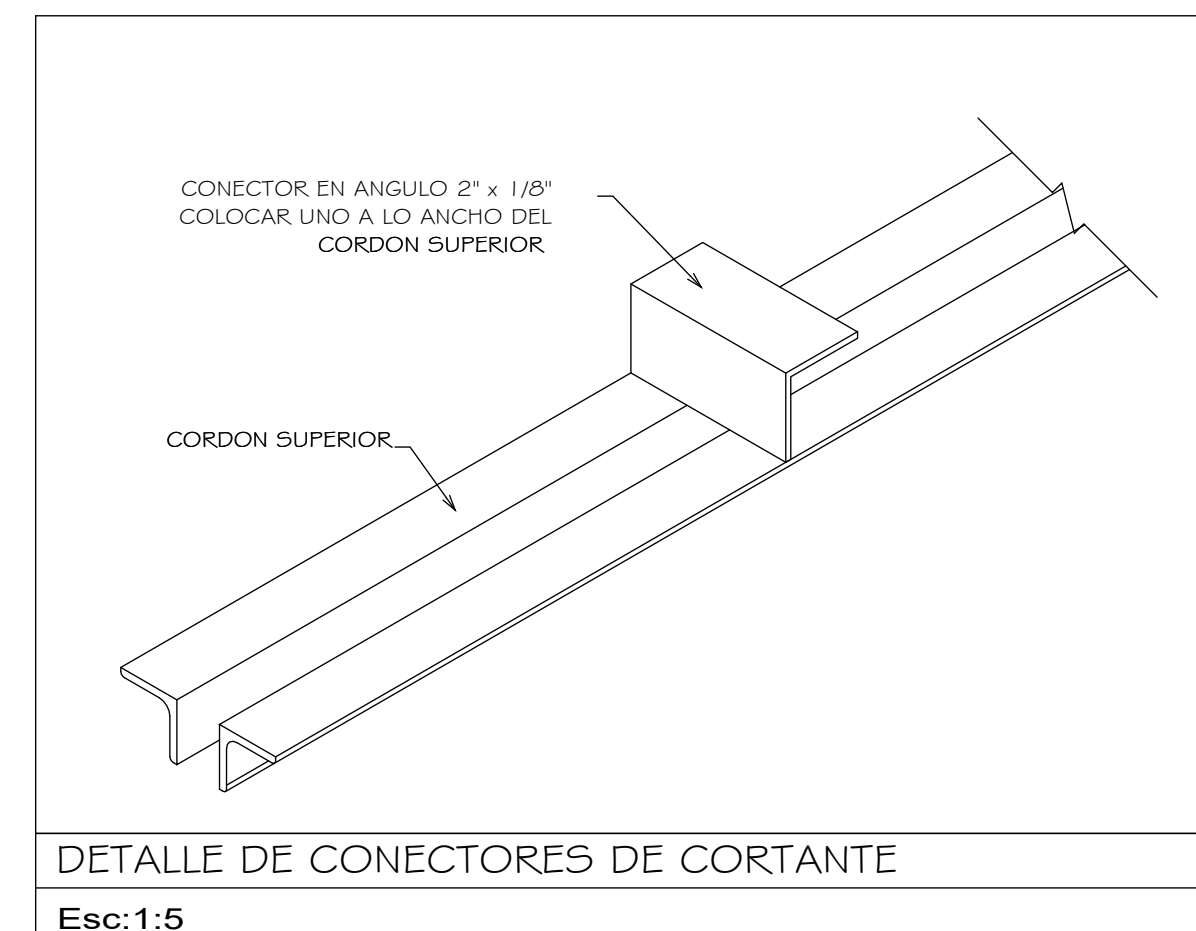

ISOMETRIA LOSA MACIZA SOPORTADA CON JOIST
Esc:1:50

ESPECIFICACIONES DE MATERIALES				
CONCRETO:		C.5.1.1 El concreto debe mantenerse húmedo por lo menos 7 días después de la fundición.		
CURADO DEL CONCRETO:		C.4.3.1 Seguir la forma de exposición, para garantizar durabilidad.		
RELACION a/mc PARA MEZCLAS DE CONCRETO:		C.3.3.2 Tamaño máximo nominal del agregado grueso.		
AGREGADOS:		El refuerzo debe cumplir C.211.1.5 (NTC-288-ATC2943).		
GENERALES:		Fy = 420 MPa (4200 Kg/cm ²)		
BARRAS:		Corrugado para diámetros iguales o mayores a #2 debe cumplir norma ASTM A-706. C.3.5.3.4		
MALLAS:		Fy = 485 MPa (4850 Kg/cm ²) C.3.5.3.5 a C.3.5.3.10 NTC 2808		
RESISTENCIA AL FUEGO				
GRUPO DE OCUPACION	CATEGORIA	ELEMENTO	TIEMPO	
R2	1	Columnas - Vigas Losas Macizas Muros interiores no portantes	1 (una) hora	1 (una) hora
NORMA DISEÑO:		NSR-10		

Para: CURADURIA

Proyecto: Acción Fiduciaria S.A como vocera y administradora del Fideicomiso FA-6547 Proyecto Florentino	Proyecto Estructural:  Revisó: ING. JUAN RAUL SOLARTE G. Mat. 676 CAUCA		
Proyecto: EDIFICACION DE VIVIENDA EN 8 PISOS Y 1 SOTANO BARRIO EL PEÑON	Diseño: ING. JULIAN ENRIQUEZ		
Proyecto N°: 3772-25	Colaboró: ING. FABIAN ROJAS Dibujó: RENÉ MONTAÑO BOTERO		
Unidad Estructural: EDIFICIO	Contiene: PLANO NIV. 4		
Fecha: FEBRERO 2026	Escala: Como se indica	Plano N°: 104	Version: