

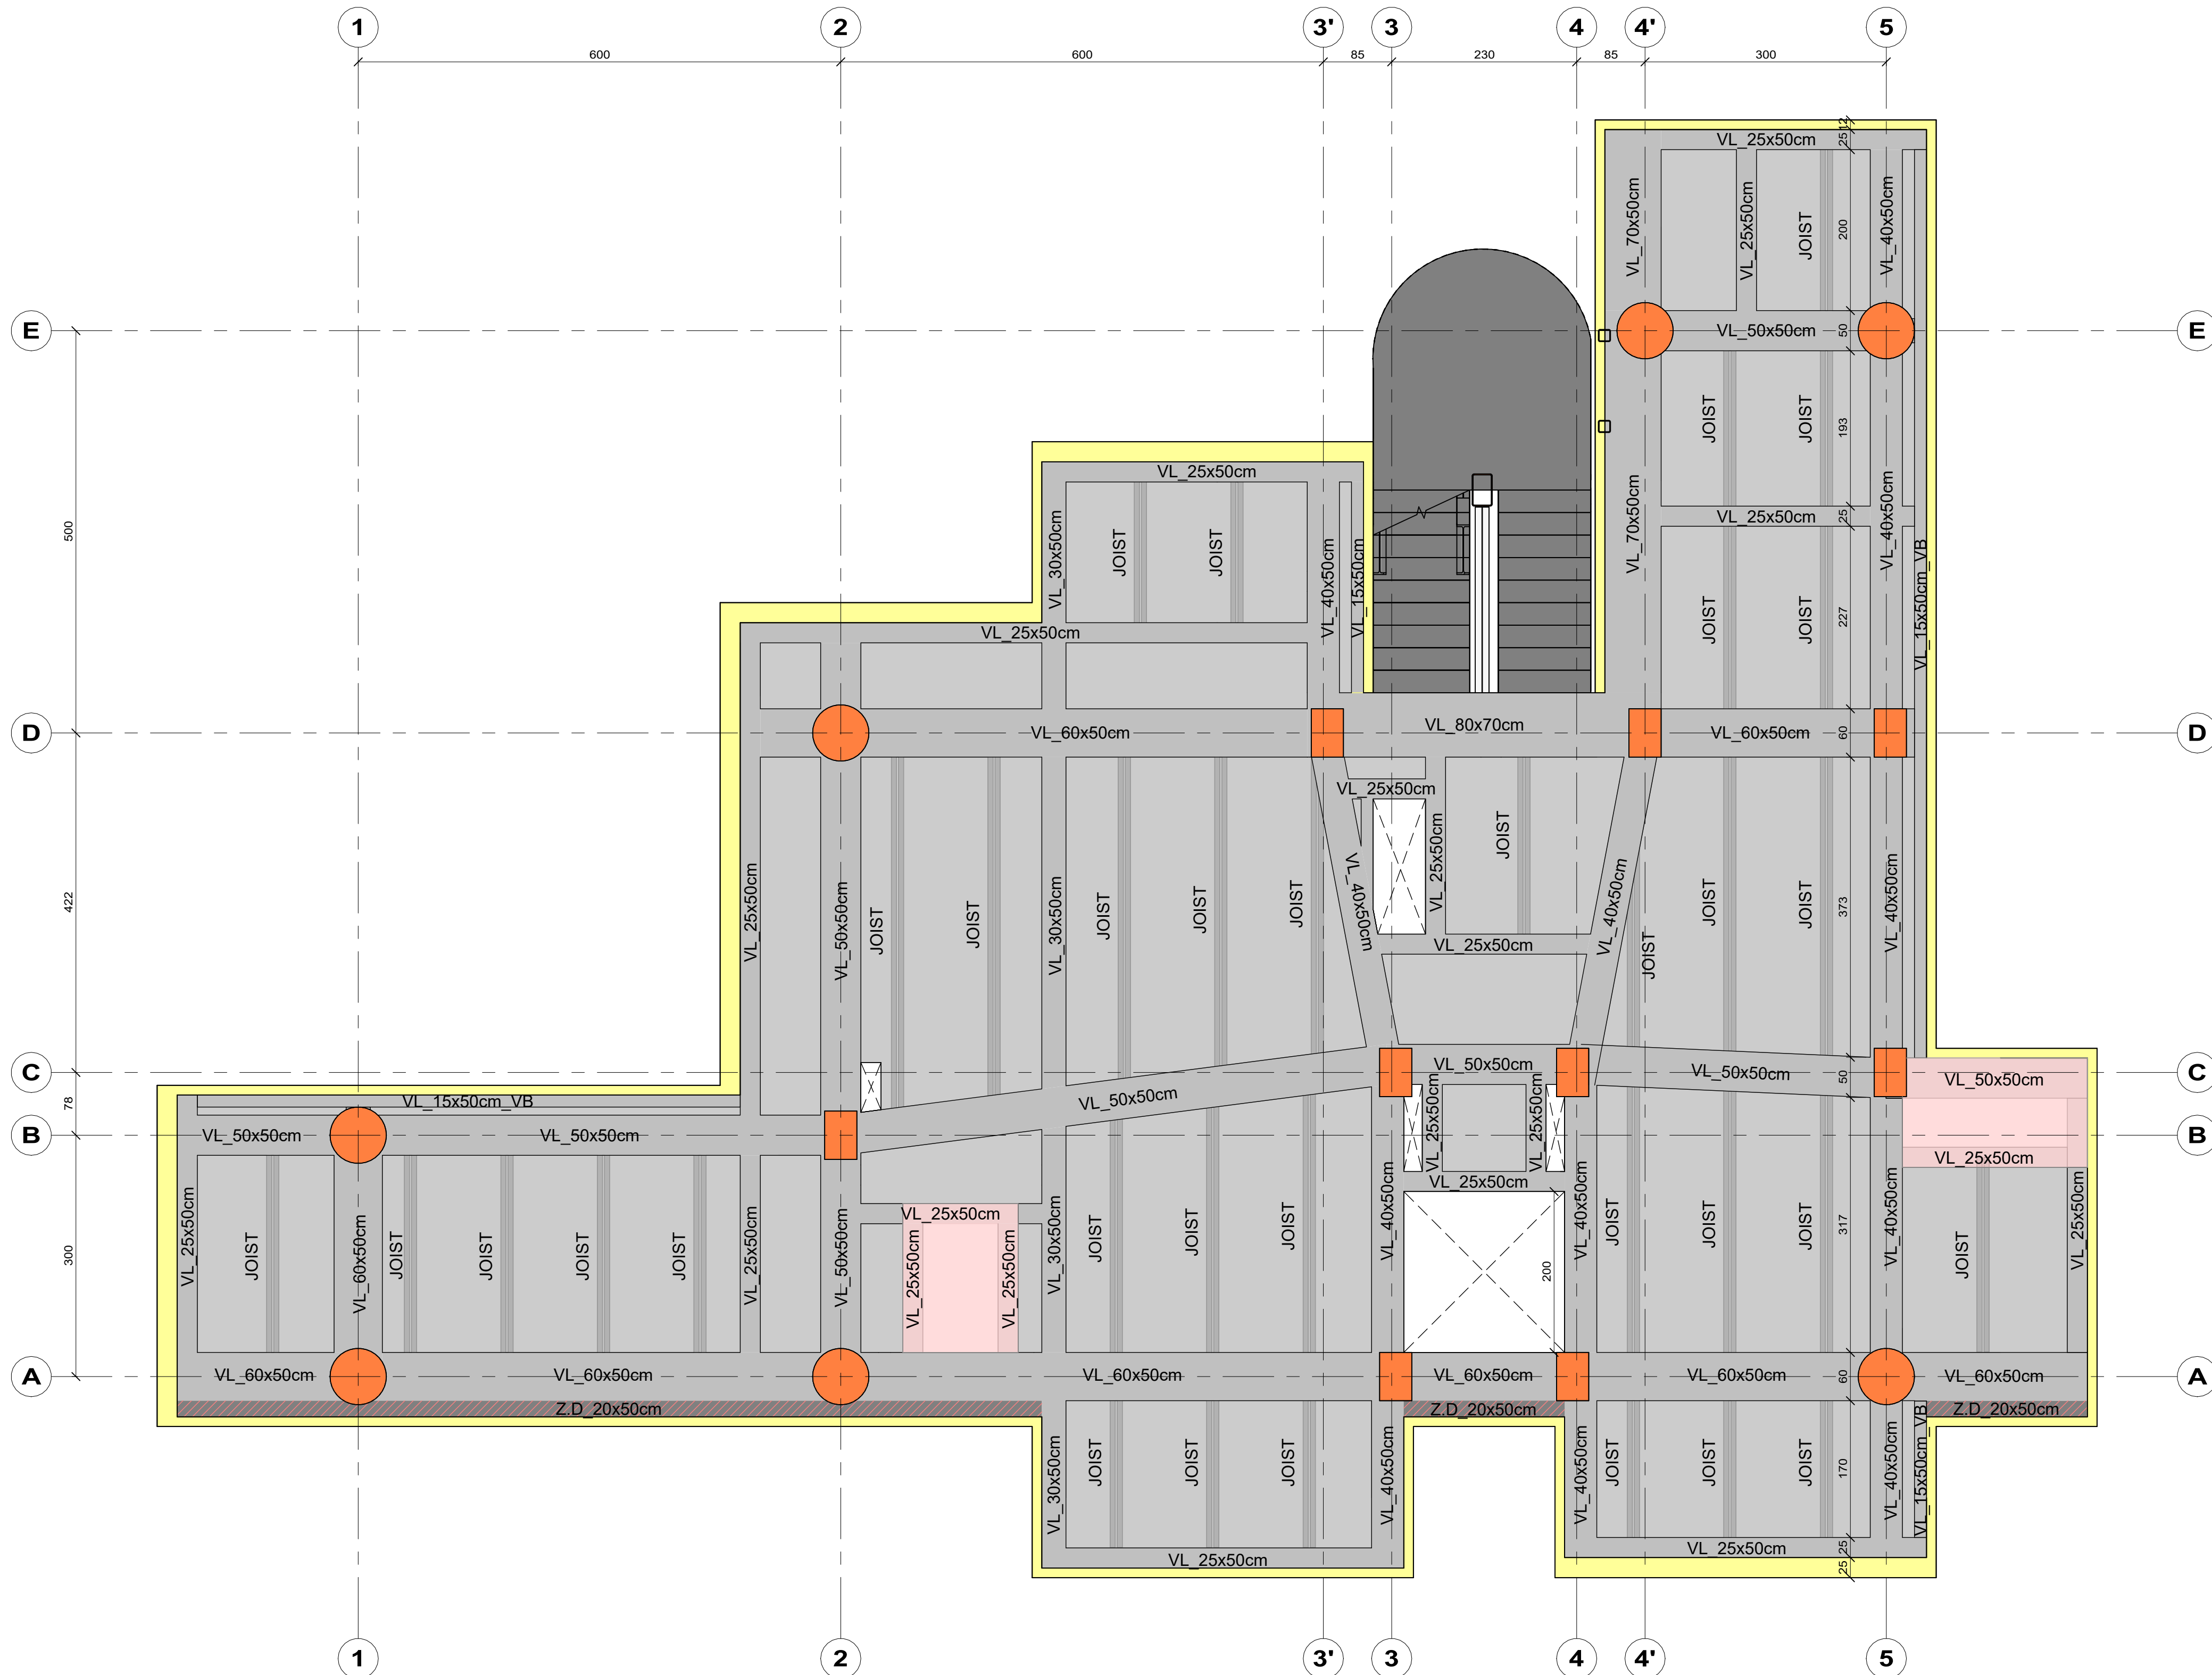
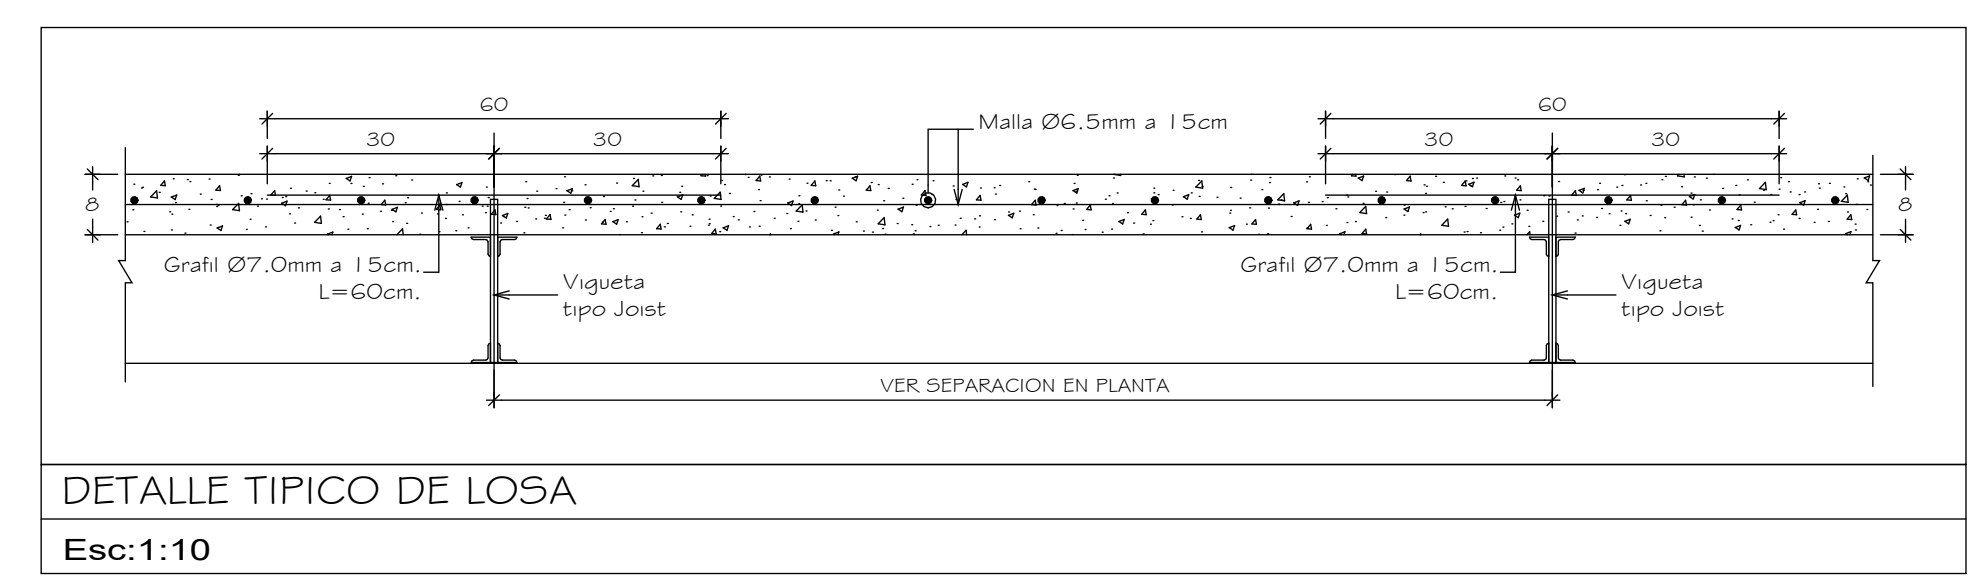
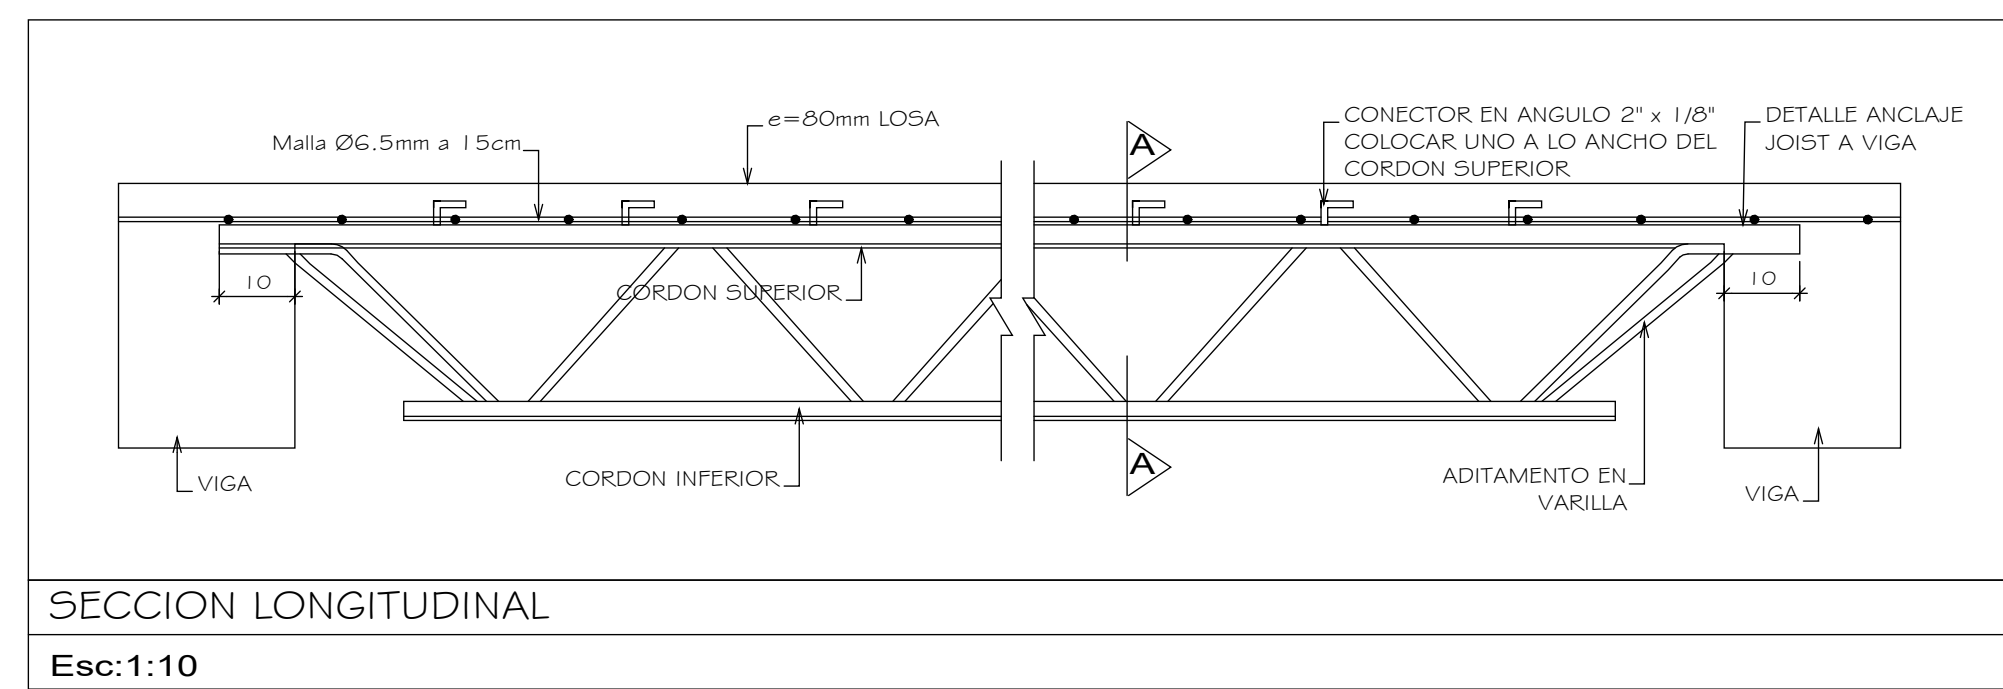
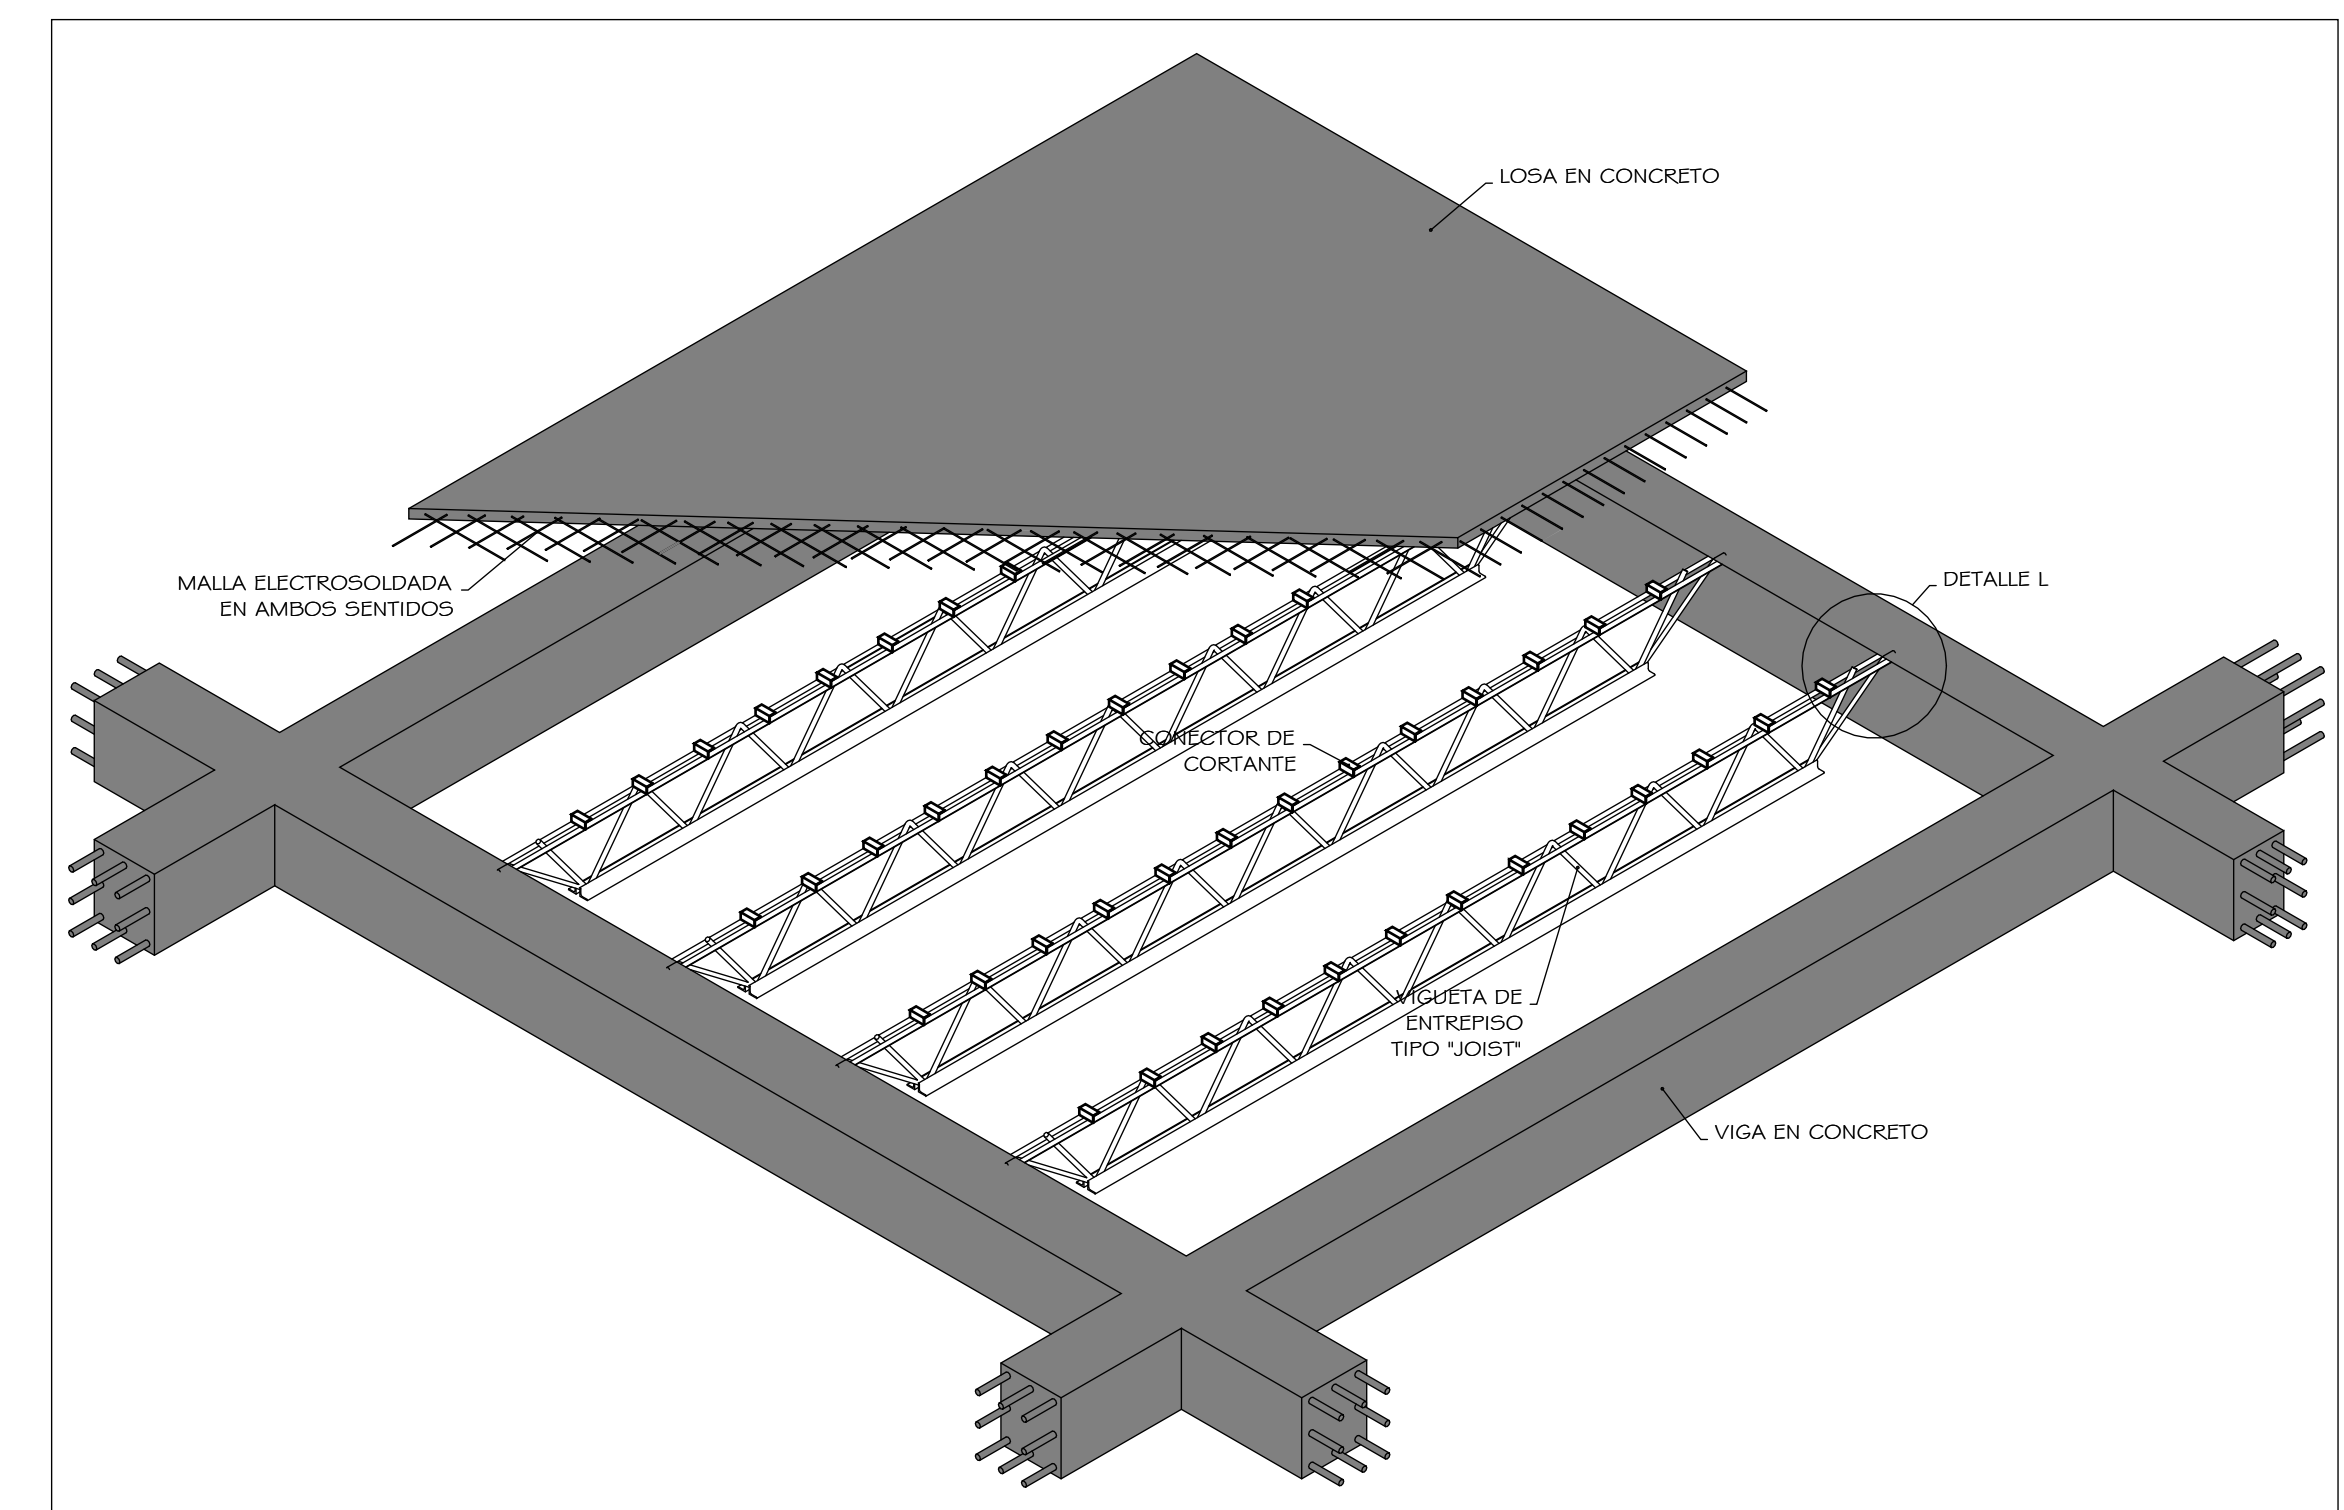
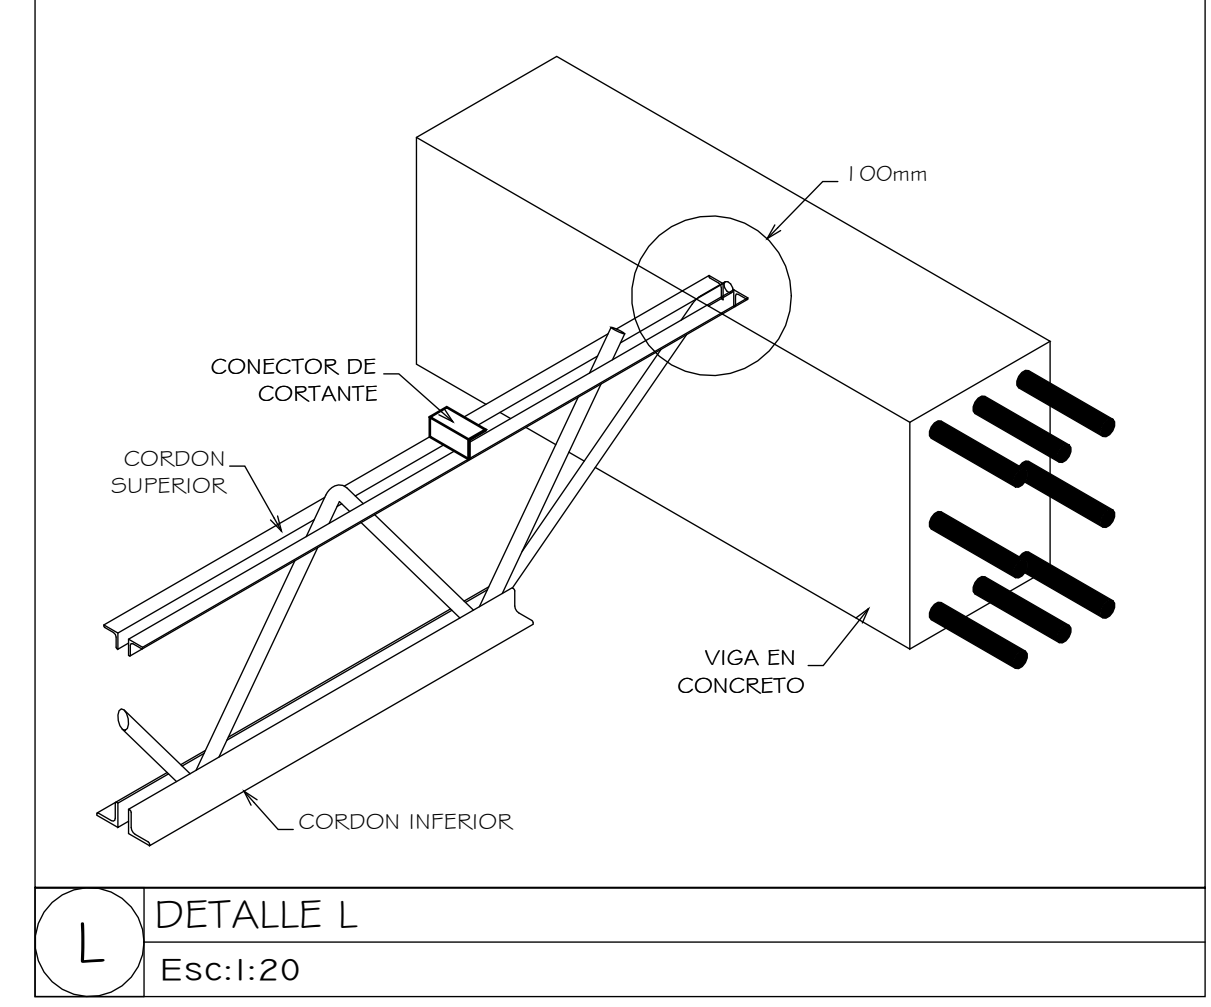


ESTE PLANO ES PROPIEDAD INTELECTUAL DE SOLARTE Y CIA. INGENIEROS CALCULISTAS S.A. SE PROHIBE SU REPRODUCCION O MODIFICACION PARCIAL O TOTAL. EN CASO DE MODIFICARSE VO UTILIZARSE INDEBIDAMENTE. LA EMPRESA QUEDA EXENTA DE CUALQUIER RESPONSABILIDAD QUE PUEDA DERIVAR DE SU UTILIZACION.

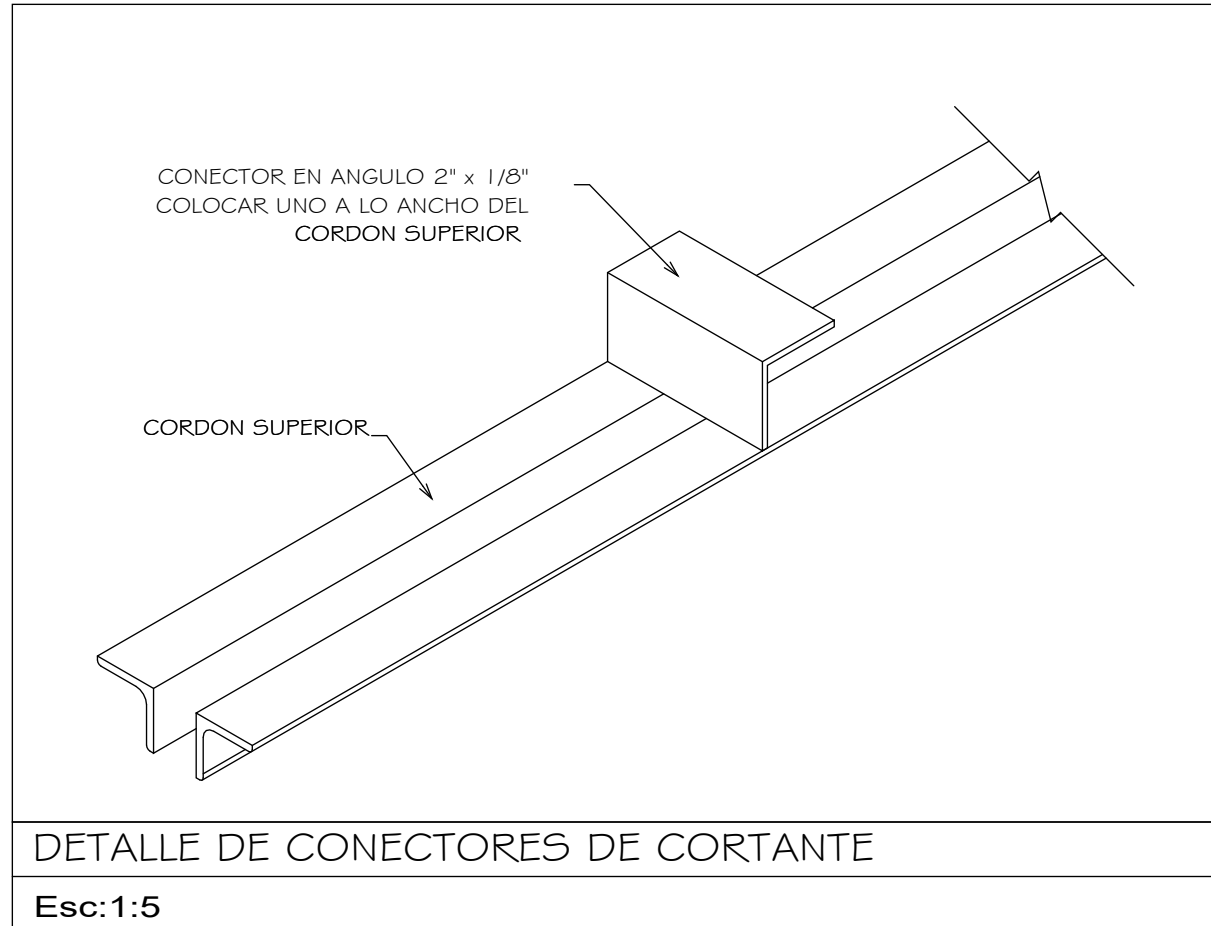

1 PISO 5
1 : 50

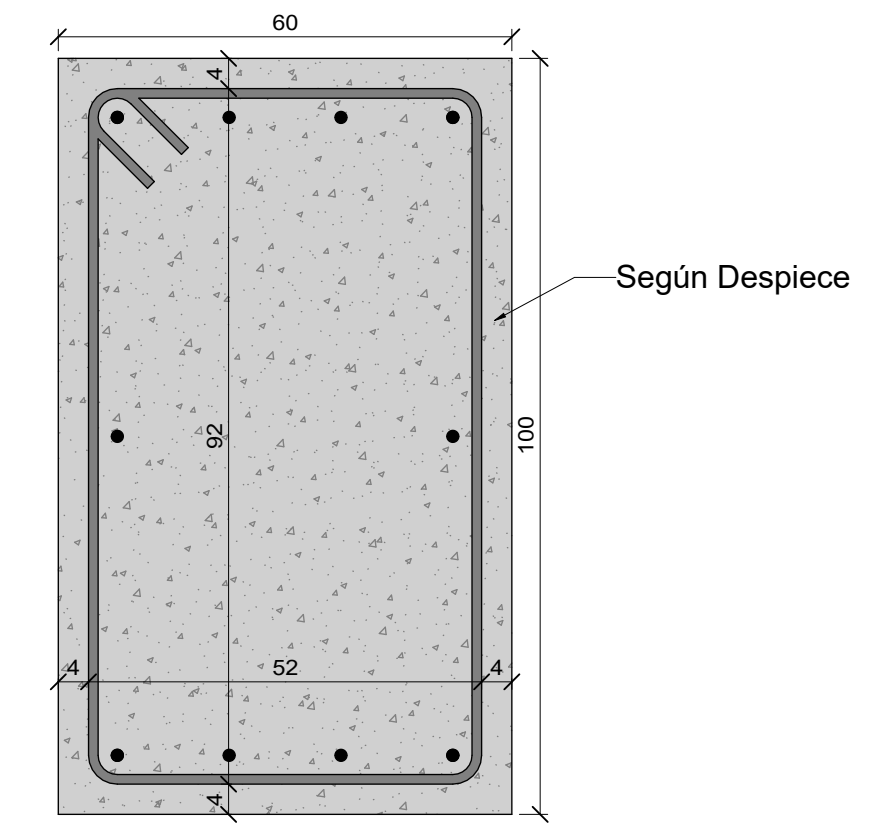

ESPECIFICACIONES DE MATERIALES			
CONCRETO:		C.5.11: El concreto debe mantenerse húmedo por lo menos 7 días después de la fundición.	
CURADO DEL CONCRETO:			
RELACION a/mc PARA MEZCLAS DE CONCRETO:		C.4.3.1: Según la clase de exposición, para garantizar durabilidad.	
AGREGADOS:		C.3.3.2: Tamaño máximo nominal del agregado grueso.	
GENERALES:		El refuerzo debe cumplir C.21.1.5 (NTC2289-NTC2043)	
BARRAS:		Fy = 420 Mpa (4200 Kg/cm²) Corrugado para diámetros iguales o mayores a #2 debe cumplir Norma ASTM A-706. C.3.5.3.4	
MALLAS:		Fy ≥ 485 Mpa (4850 Kg/cm²) C.3.5.3.5 a C.3.5.3.10 NTC 5806	
RESISTENCIA AL FUEGO			
GRUPO DE OCUPACION	CATEGORIA	ELEMENTO	TIEMPO
R2	1	Columnas - Vigas	1 (una) hora
		Losas Macizas	1 (una) hora
		Muros interiores no portantes	1 (una) hora
NORMA DISEÑO: NSR-10			

CURADURIA

Propietario:		Proyecto Estructural:	
Acción Fiduciaria S.A como vocera y administradora del Fideicomiso FA-6547 Proyecto Florentino		ING. JUAN RAUL SOLARTE G. Mat. 876 CAUCA	
Revisó:		ING. JULIAN ENRIQUEZ	
Proyecto:		Colaboró:	
EDIFICACIÓN DE VIVIENDA EN 8 PISOS Y 1 SOTANO		ING. FABIAN ROJAS	
Proyecto N°:		Dibujó:	
3772-25		RENÉ MONTAÑO BOTERO	
Unidad Estructural:		Contiene:	
EDIFICIO		PLANO NIV. 5	
Fecha:		Plano N°:	
FEBRERO 2026		105	
Escala:		Versión:	
Como se indica			