




ESTE PLANO ES PROPIEDAD INTELECTUAL DE SOLARTE Y CIA. INGENIEROS CALCULISTAS S.A. SE PROHIBE SU REPRODUCCION O MODIFICACION PARCIAL O TOTAL. EN CASO DE MODIFICARSE VO UTILIZARSE INDEBIDAMENTE. LA EMPRESA QUEDA EXENTA DE CUALQUIER RESPONSABILIDAD QUE PUEDA DERIVAR DE SU UTILIZACION.

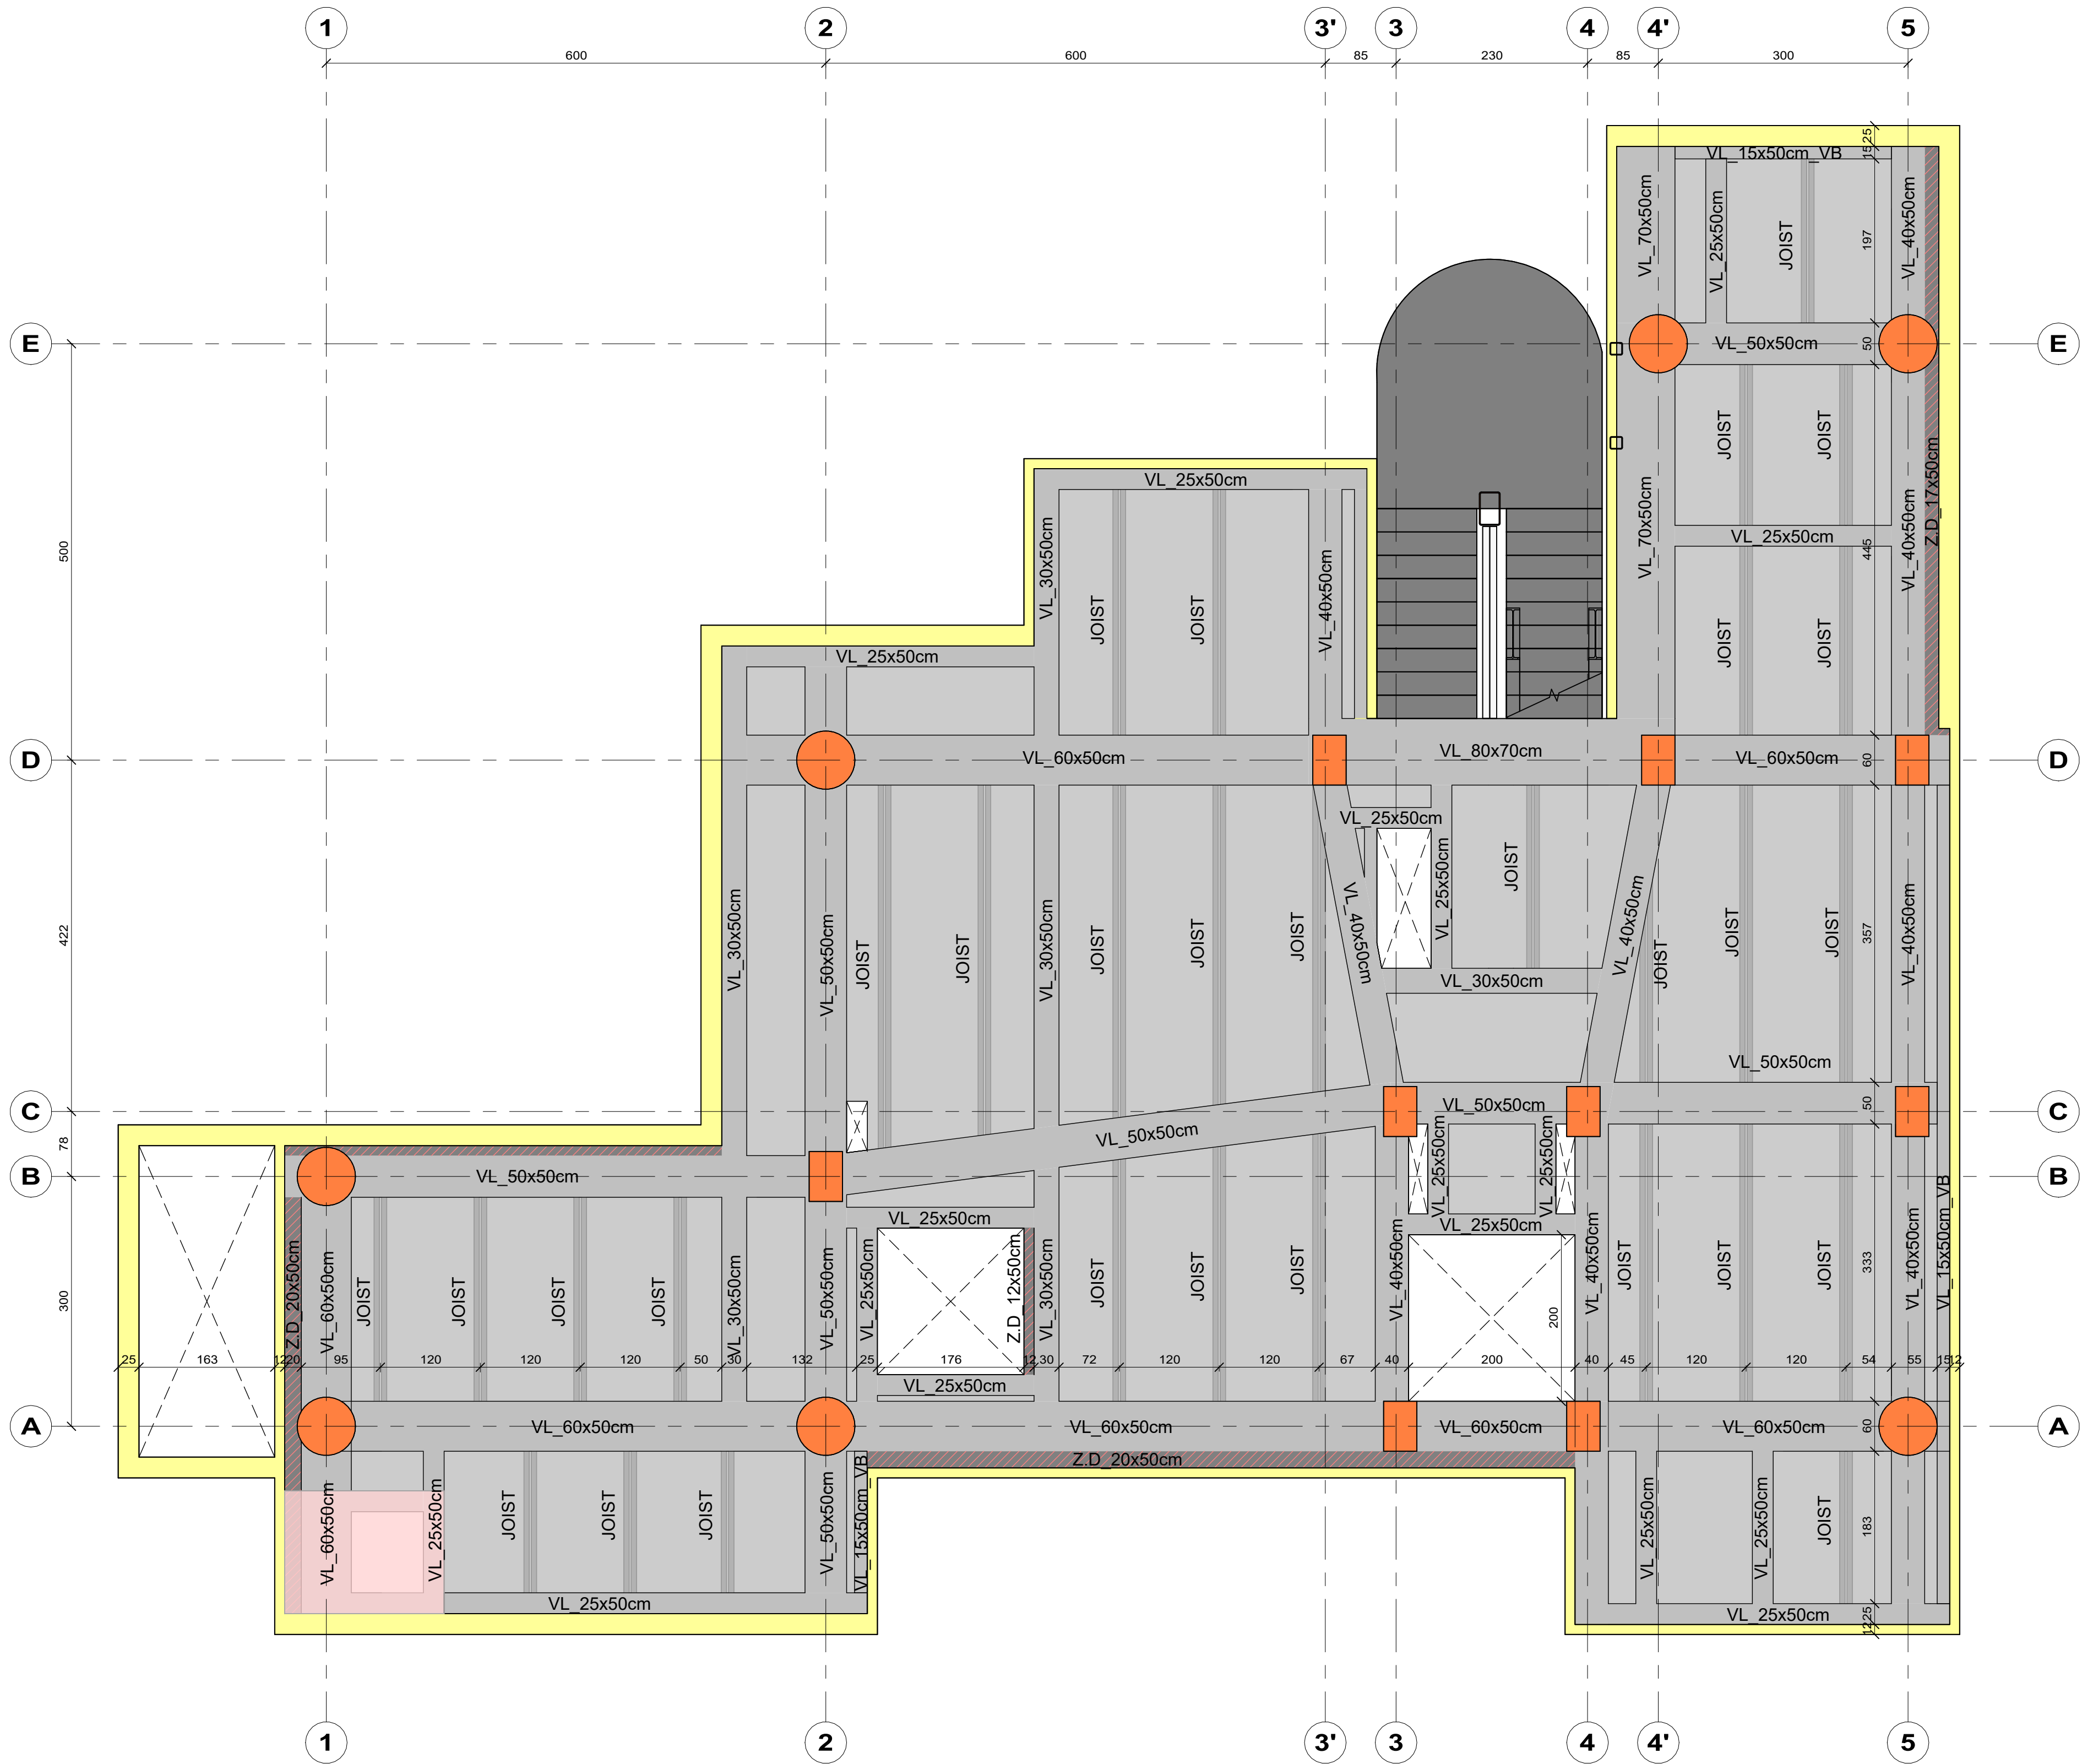

1 PISO 6
1 : 50

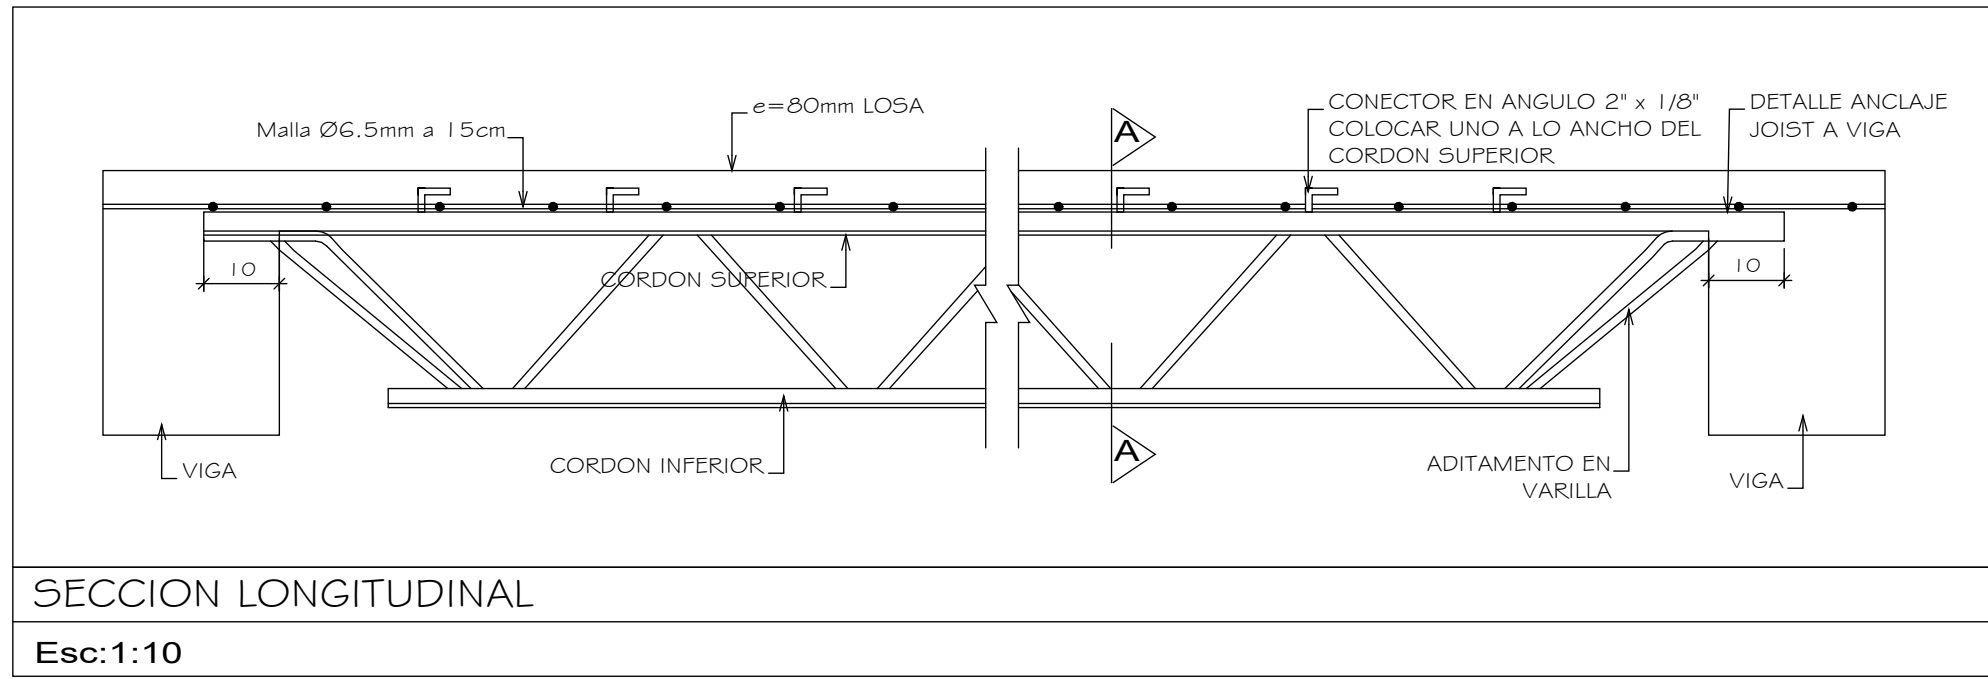

SECCION LONGITUDINAL
Esc:1:10

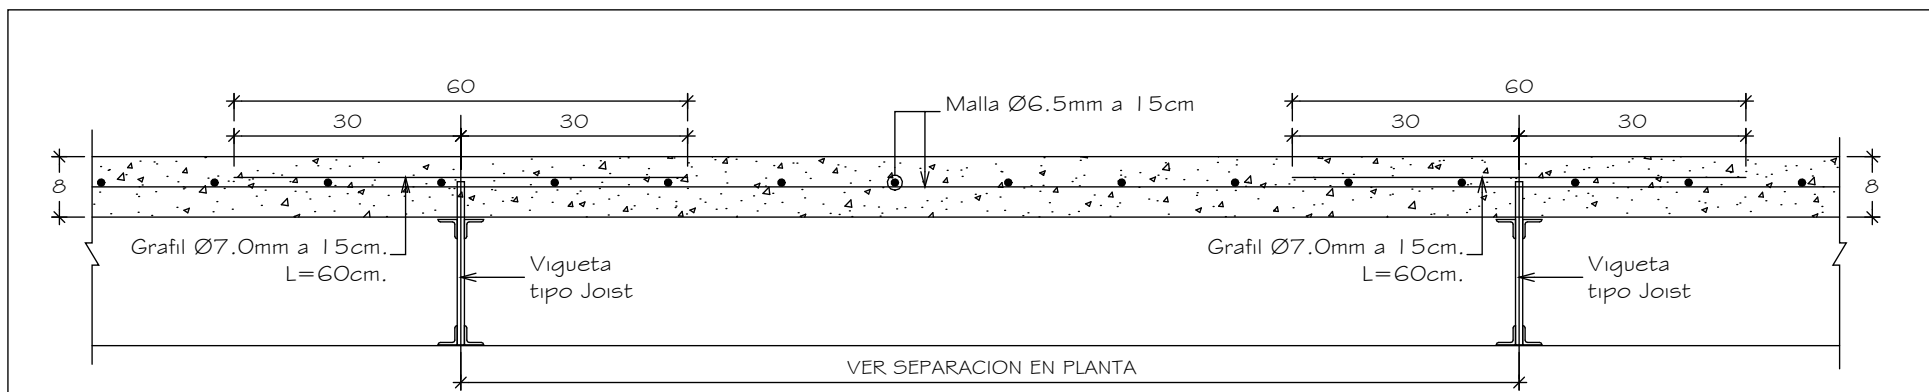

DETALLE TÍPICO DE LOSA
Esc:1:10

VERSIÓN	FECHA	REVISIONES O MODIFICACIONES	MODIFICÓ

ESPECIFICACIONES DE MATERIALES			
CONCRETO:		C.5.11: El concreto debe mantenerse húmedo por lo menos 7 días después de la fundición.	
CURADO DEL CONCRETO:		C.4.3.1: Según la clase de exposición, para garantizar durabilidad.	
RELACION a/m PARA MEZCLAS DE CONCRETO:		C.3.3.2: Tamaño máximo nominal del agregado grueso.	
AGREGADOS:		C.3.3.2: Tamaño máximo nominal del agregado grueso.	
GENERALES:		El refuerzo debe cumplir C.21.1.5 (NTC2289-NTC2043)	
BARRAS:		Fy = 420 Mpa (4200 Kg/cm²) Corrugado para diámetros iguales o mayores a #2 debe cumplir Norma ASTM A-706. C.3.5.3.4	
MALLAS:		Fy ≥ 485 Mpa (4850 Kg/cm²) C.3.5.3.5 a C.3.5.3.10 NTC 5806	
RESISTENCIA AL FUEGO			
GRUPO DE OCUPACION	CATEGORIA	ELEMENTO	TIEMPO
R2	1	Columnas - Vigas	1 (una) hora
		Losas Macizas	1 (una) hora
		Muros interiores no portantes	1 (una) hora
NORMA DISEÑO:		NSR-10	


Curaduría

Emilito Para:


Propietario:		Proyecto Estructural:	
Acción Fiduciaria S.A como vocera y administradora del Fideicomiso FA-6547 Proyecto Florentino		SOLARTE Y CIA	
Proyecto:		Revisó:	
EDIFICACIÓN DE VIVIENDA EN 8 PISOS Y 1 SOTANO		ING. JUAN RAUL SOLARTE G. Mat. 876 CAUCA	
BARRIO EL PEÑON		Diseño:	
Proyecto N°:		ING. JULIAN ENRIQUEZ	
Unidad Estructural:		Colaboró:	
3772-25		ING. FABIAN ROJAS	
Dibujó:		RENÉ MONTAÑO BOTERO	
Fecha:		PLANO NIV. 6	
FEBRERO 2026		Plano N°:	
Escala:		106	
Como se indica		Versión:	

3772-25


EDIFICACIÓN DE VIVIENDA EN 8 PISOS Y 1 SOTANO

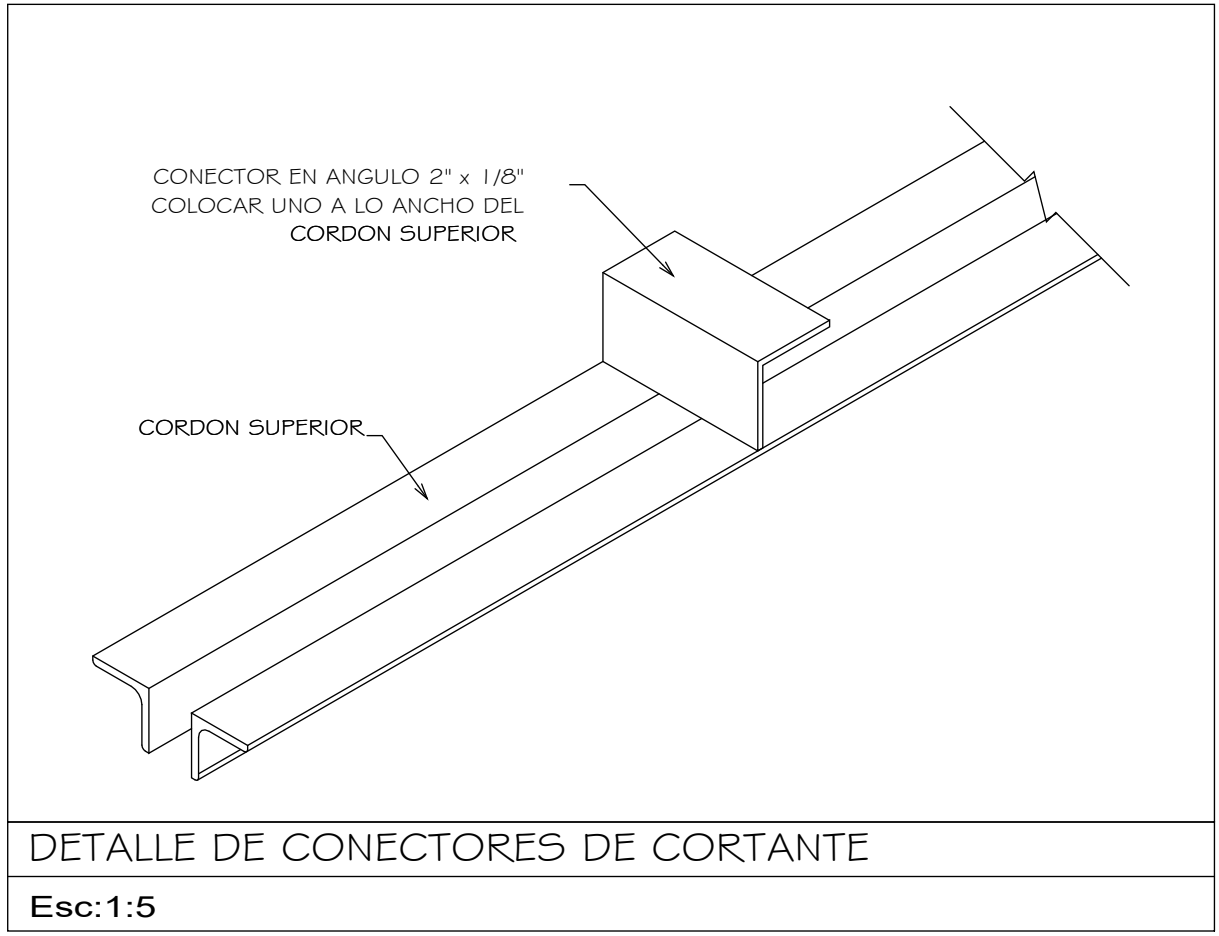

DETALLE DE CONECTORES DE CORTANTE
Esc:1:5

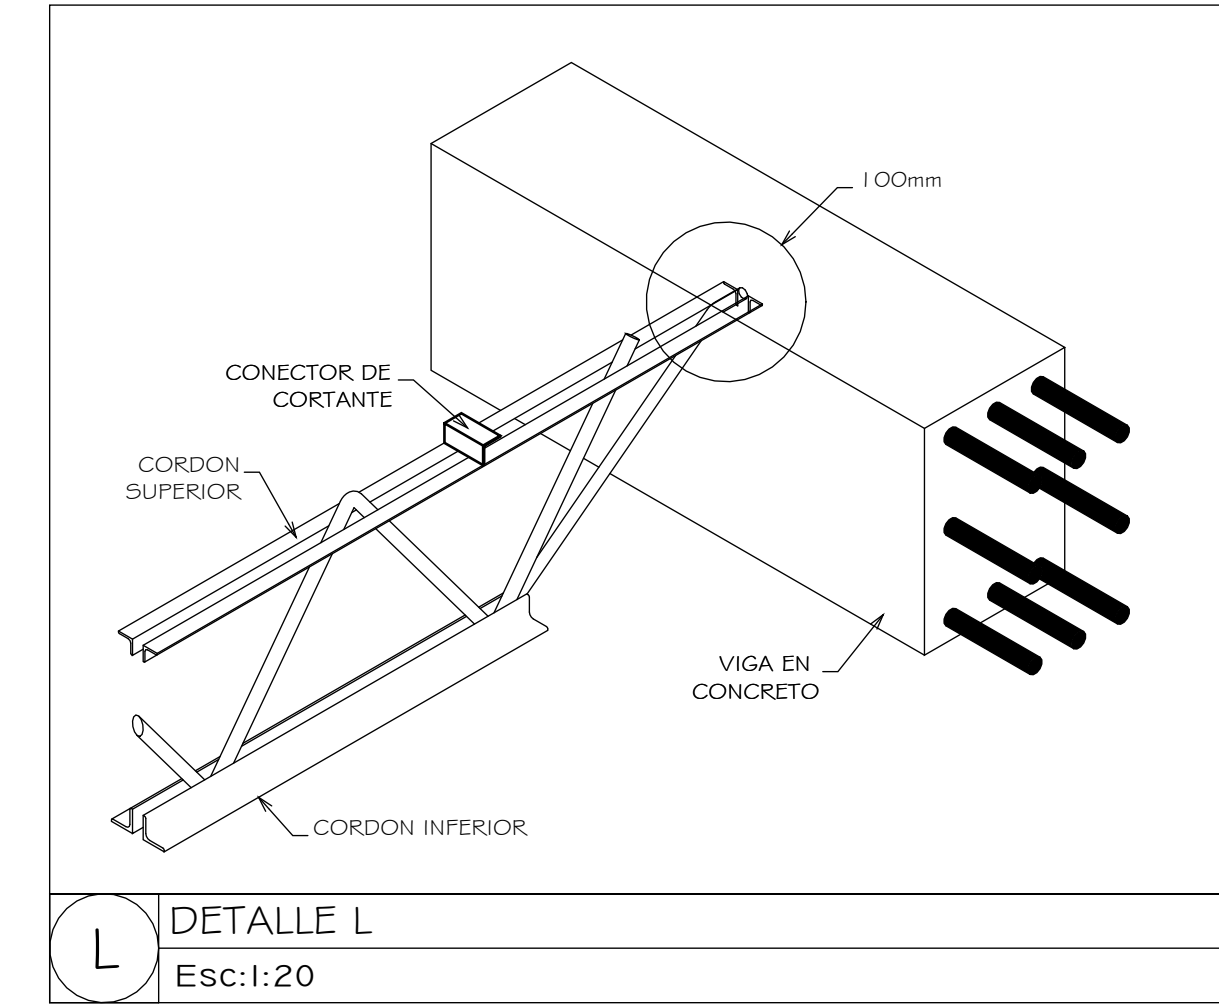

DETALLE L
Esc:1:20

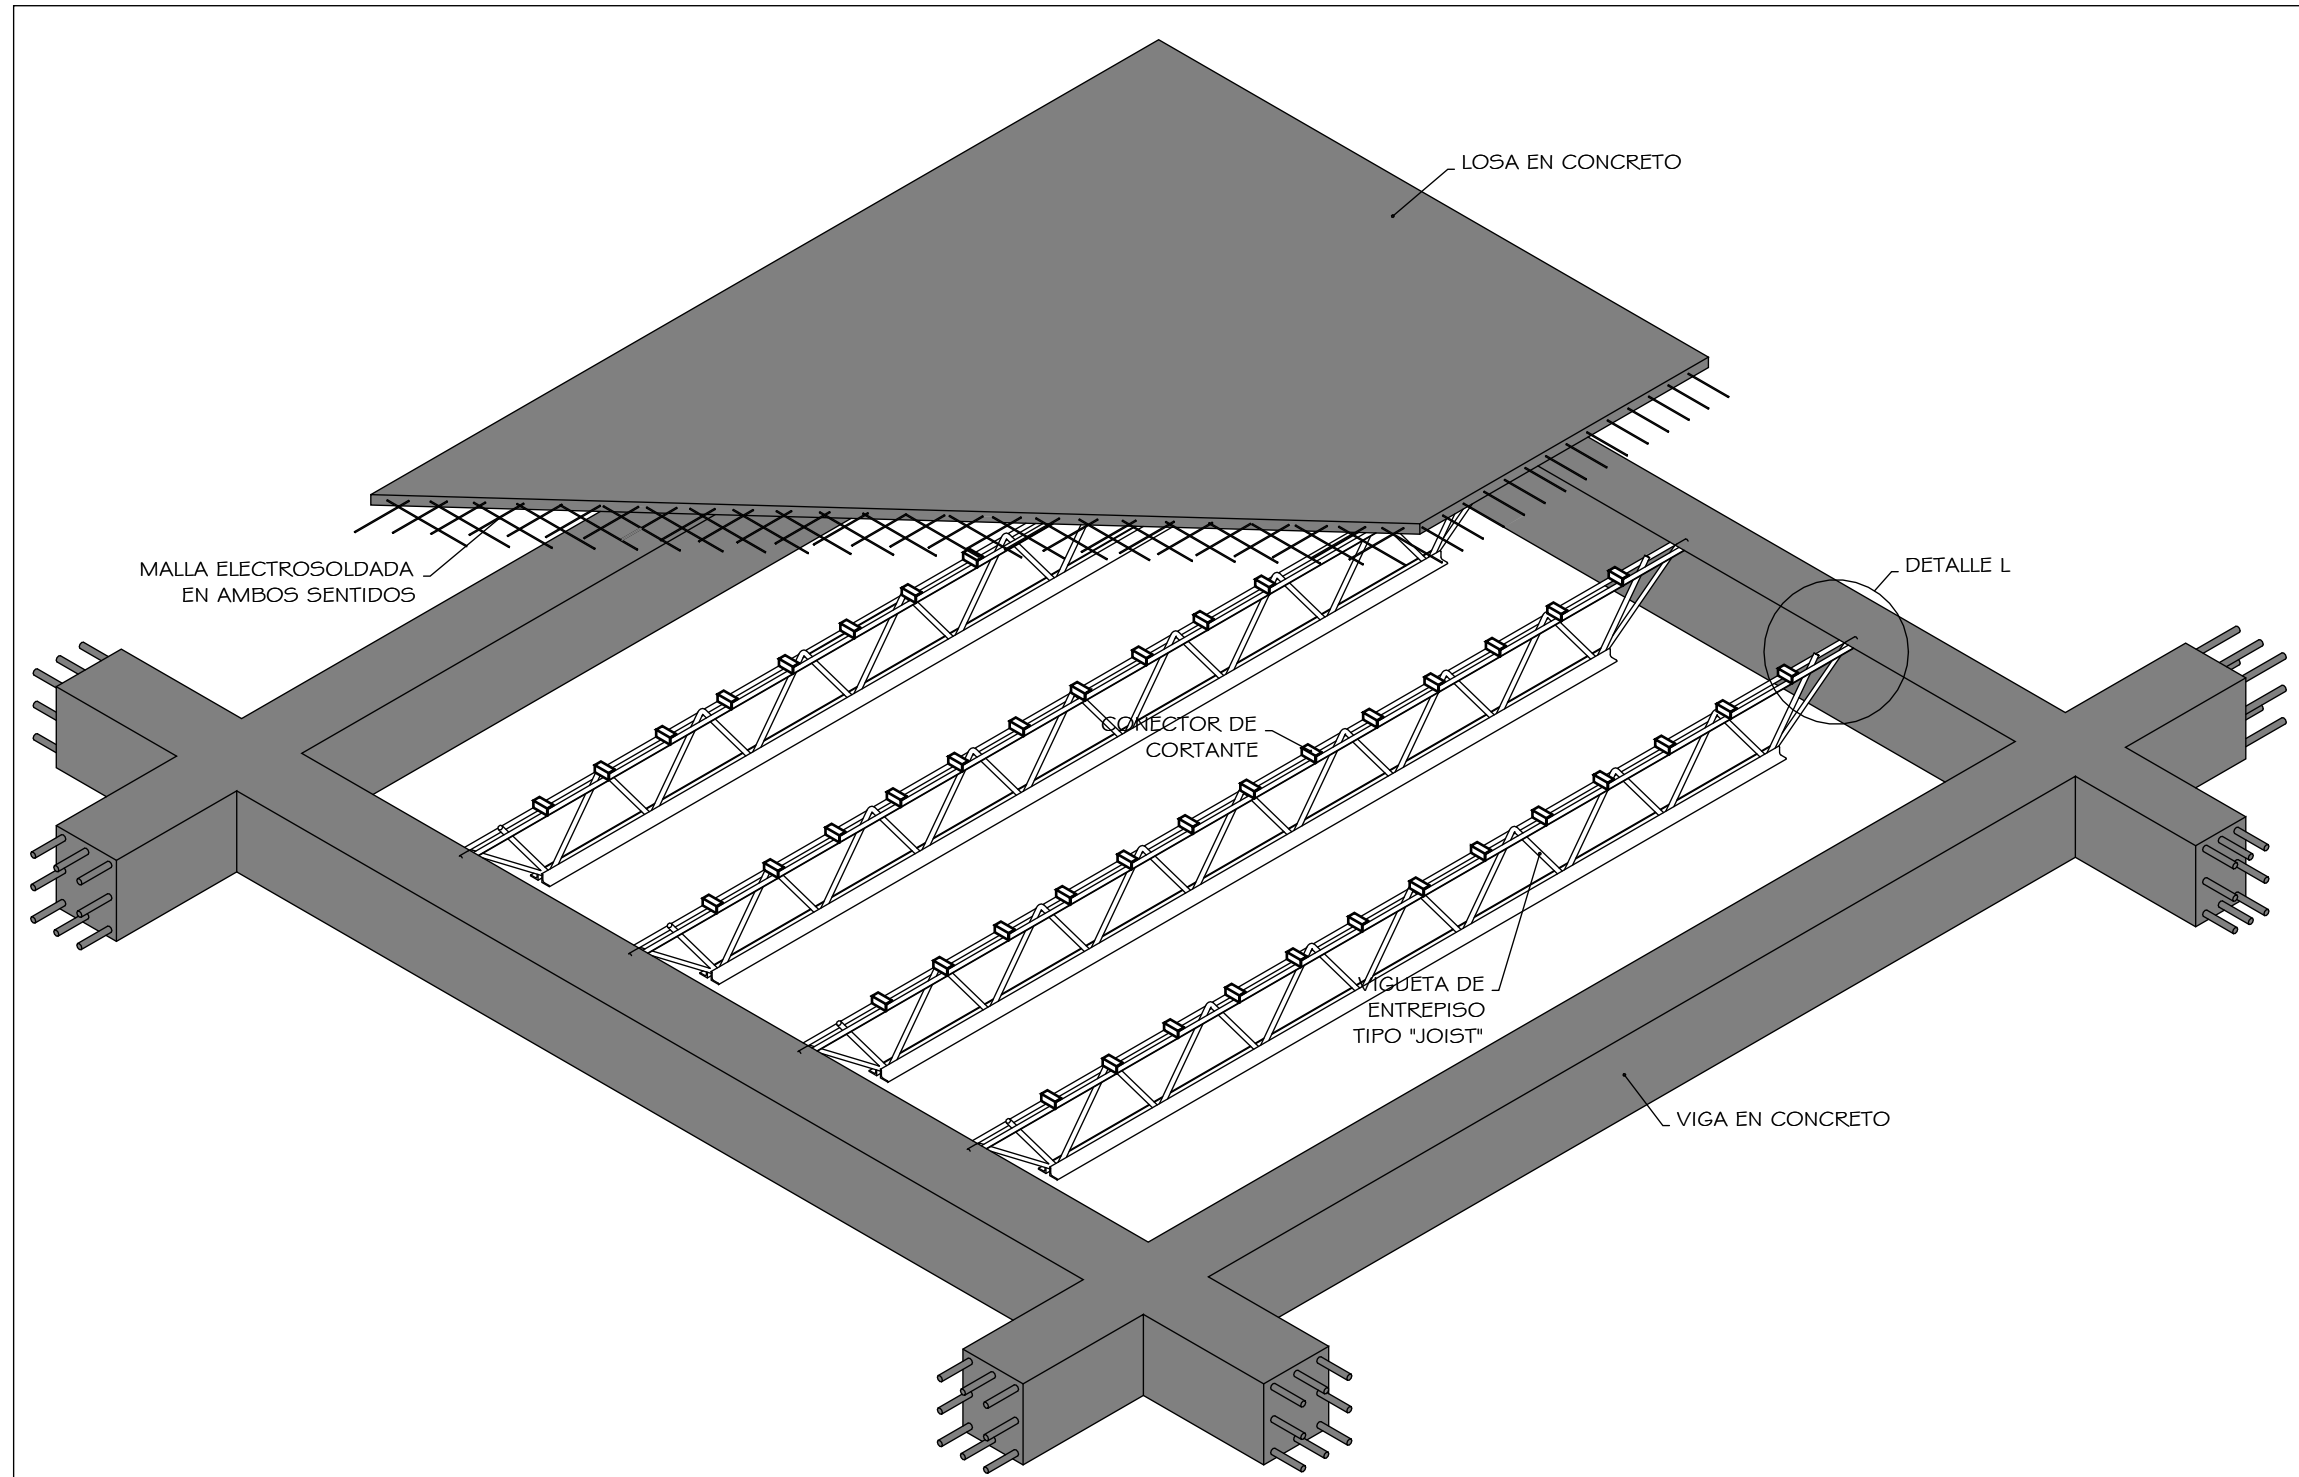

ISOMETRIA LOSA MACIZA SOPORTADA CON JOIST
Esc:1:50