

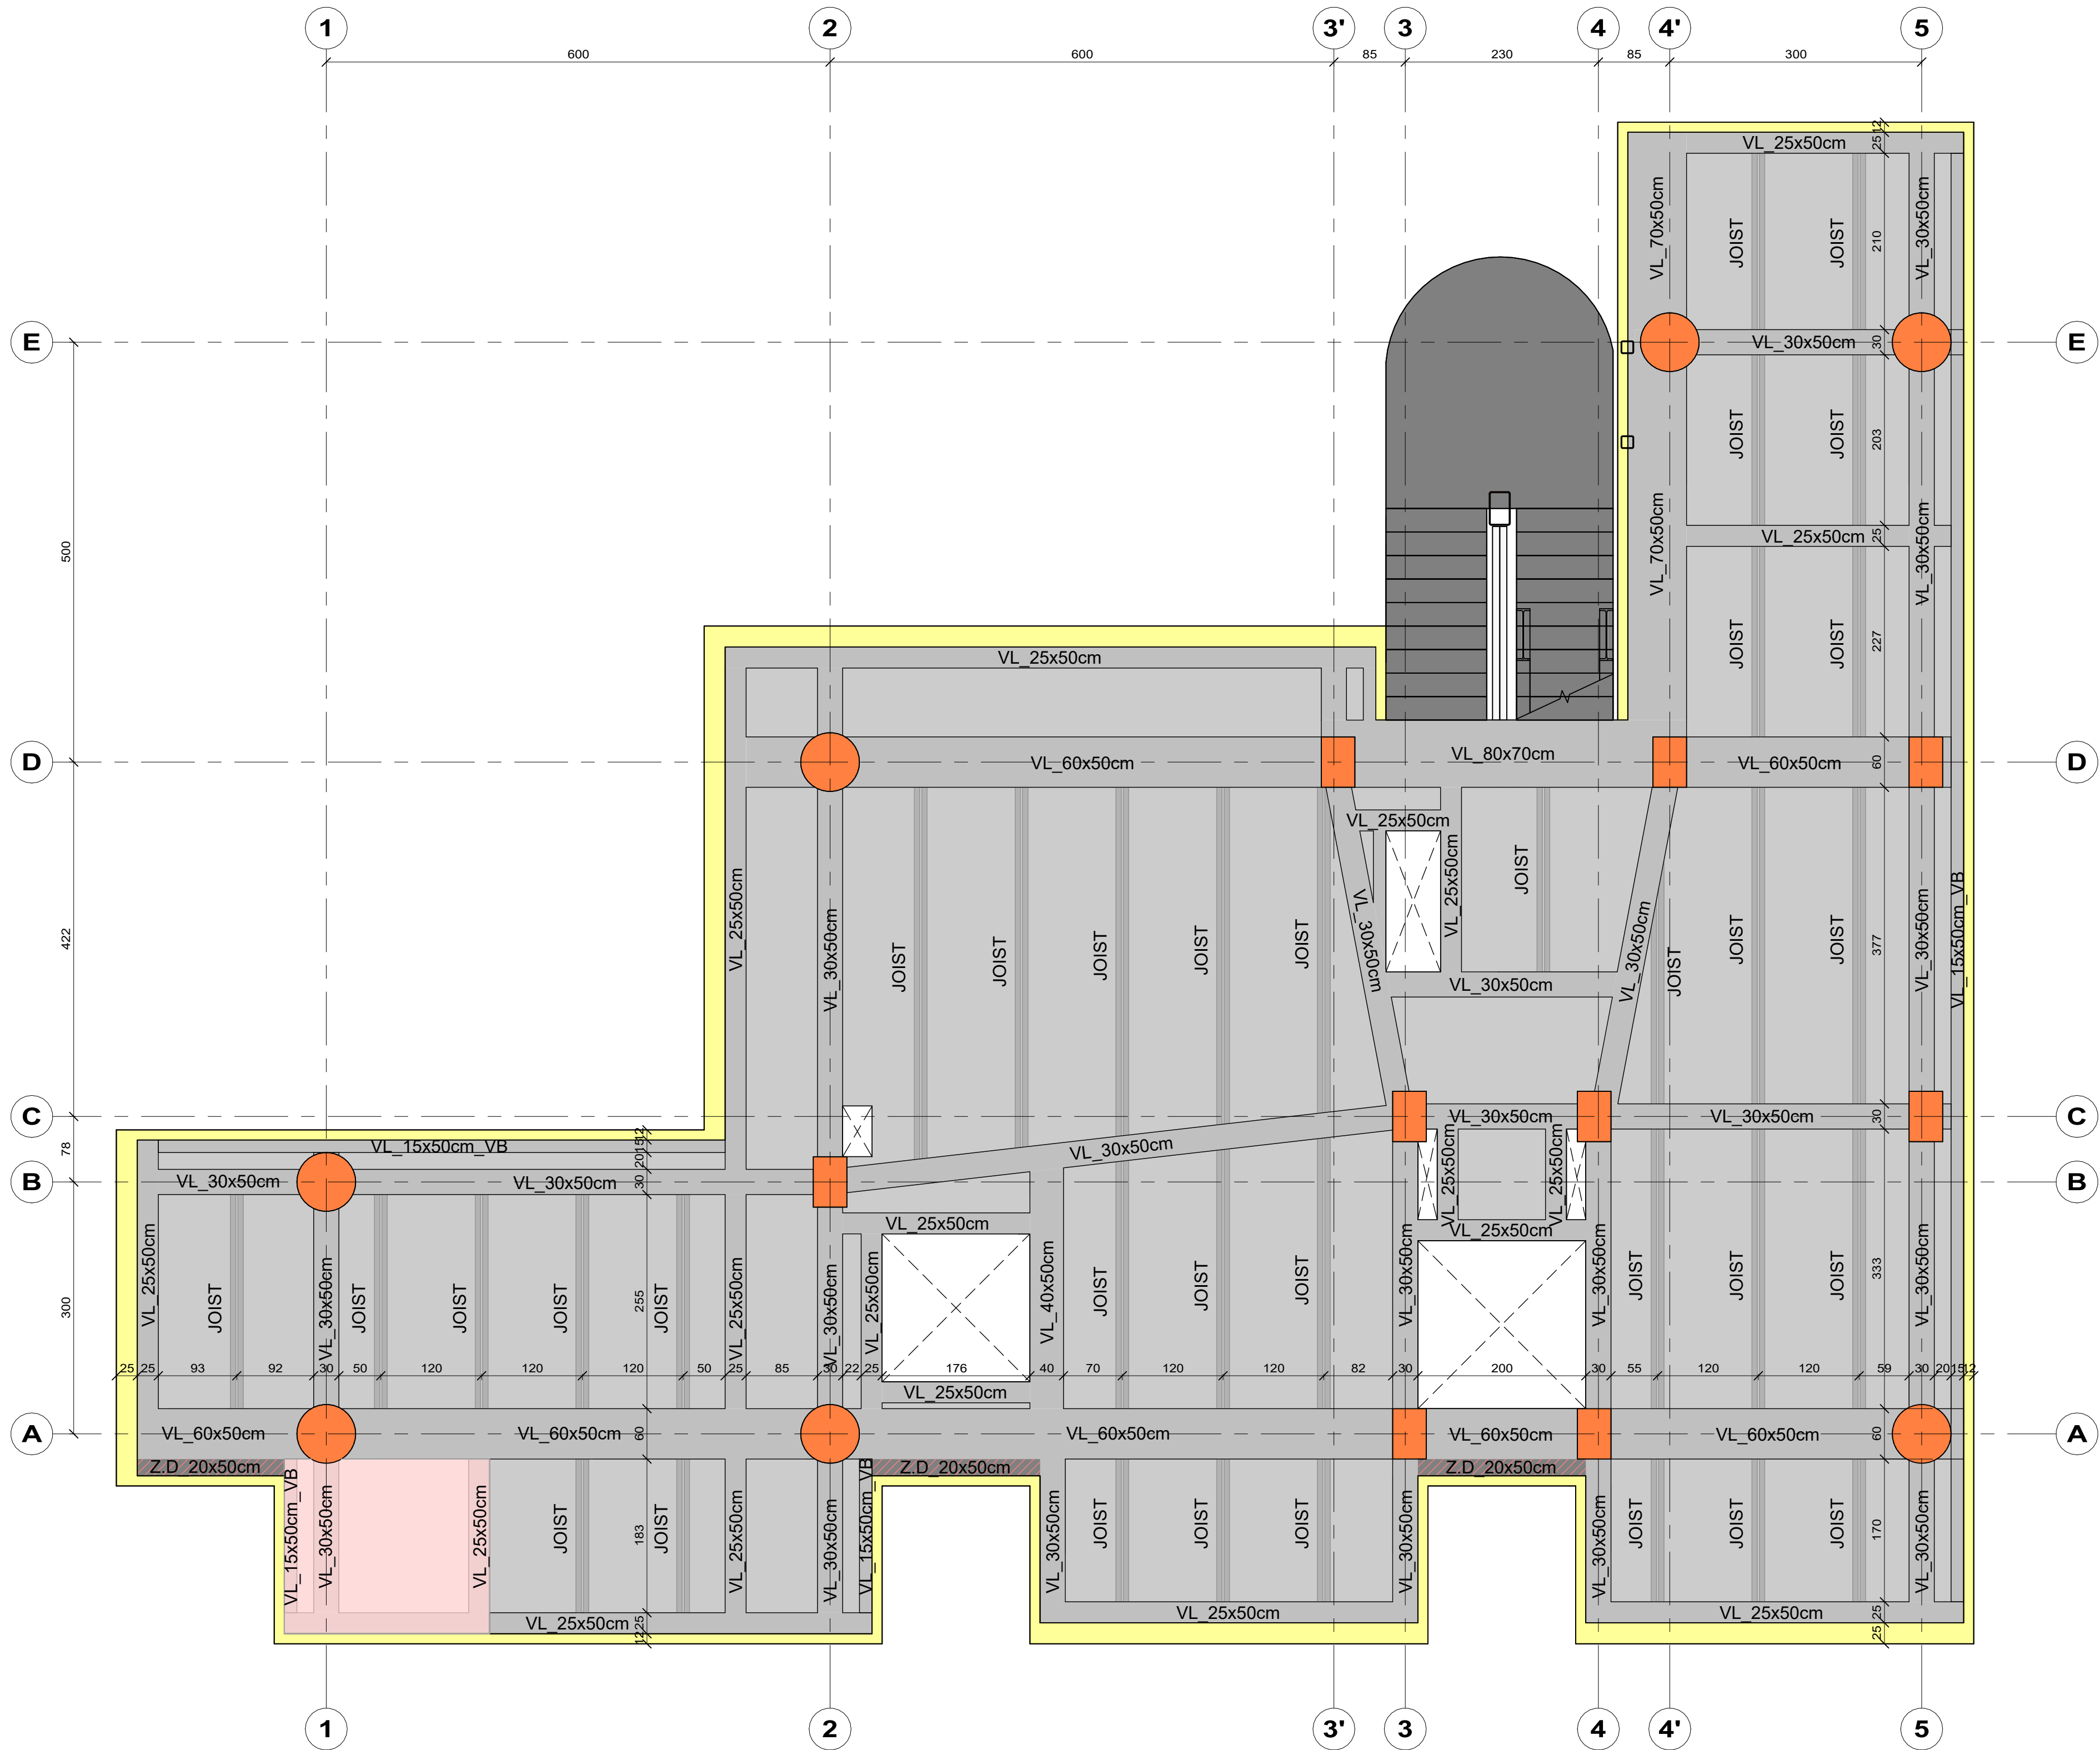
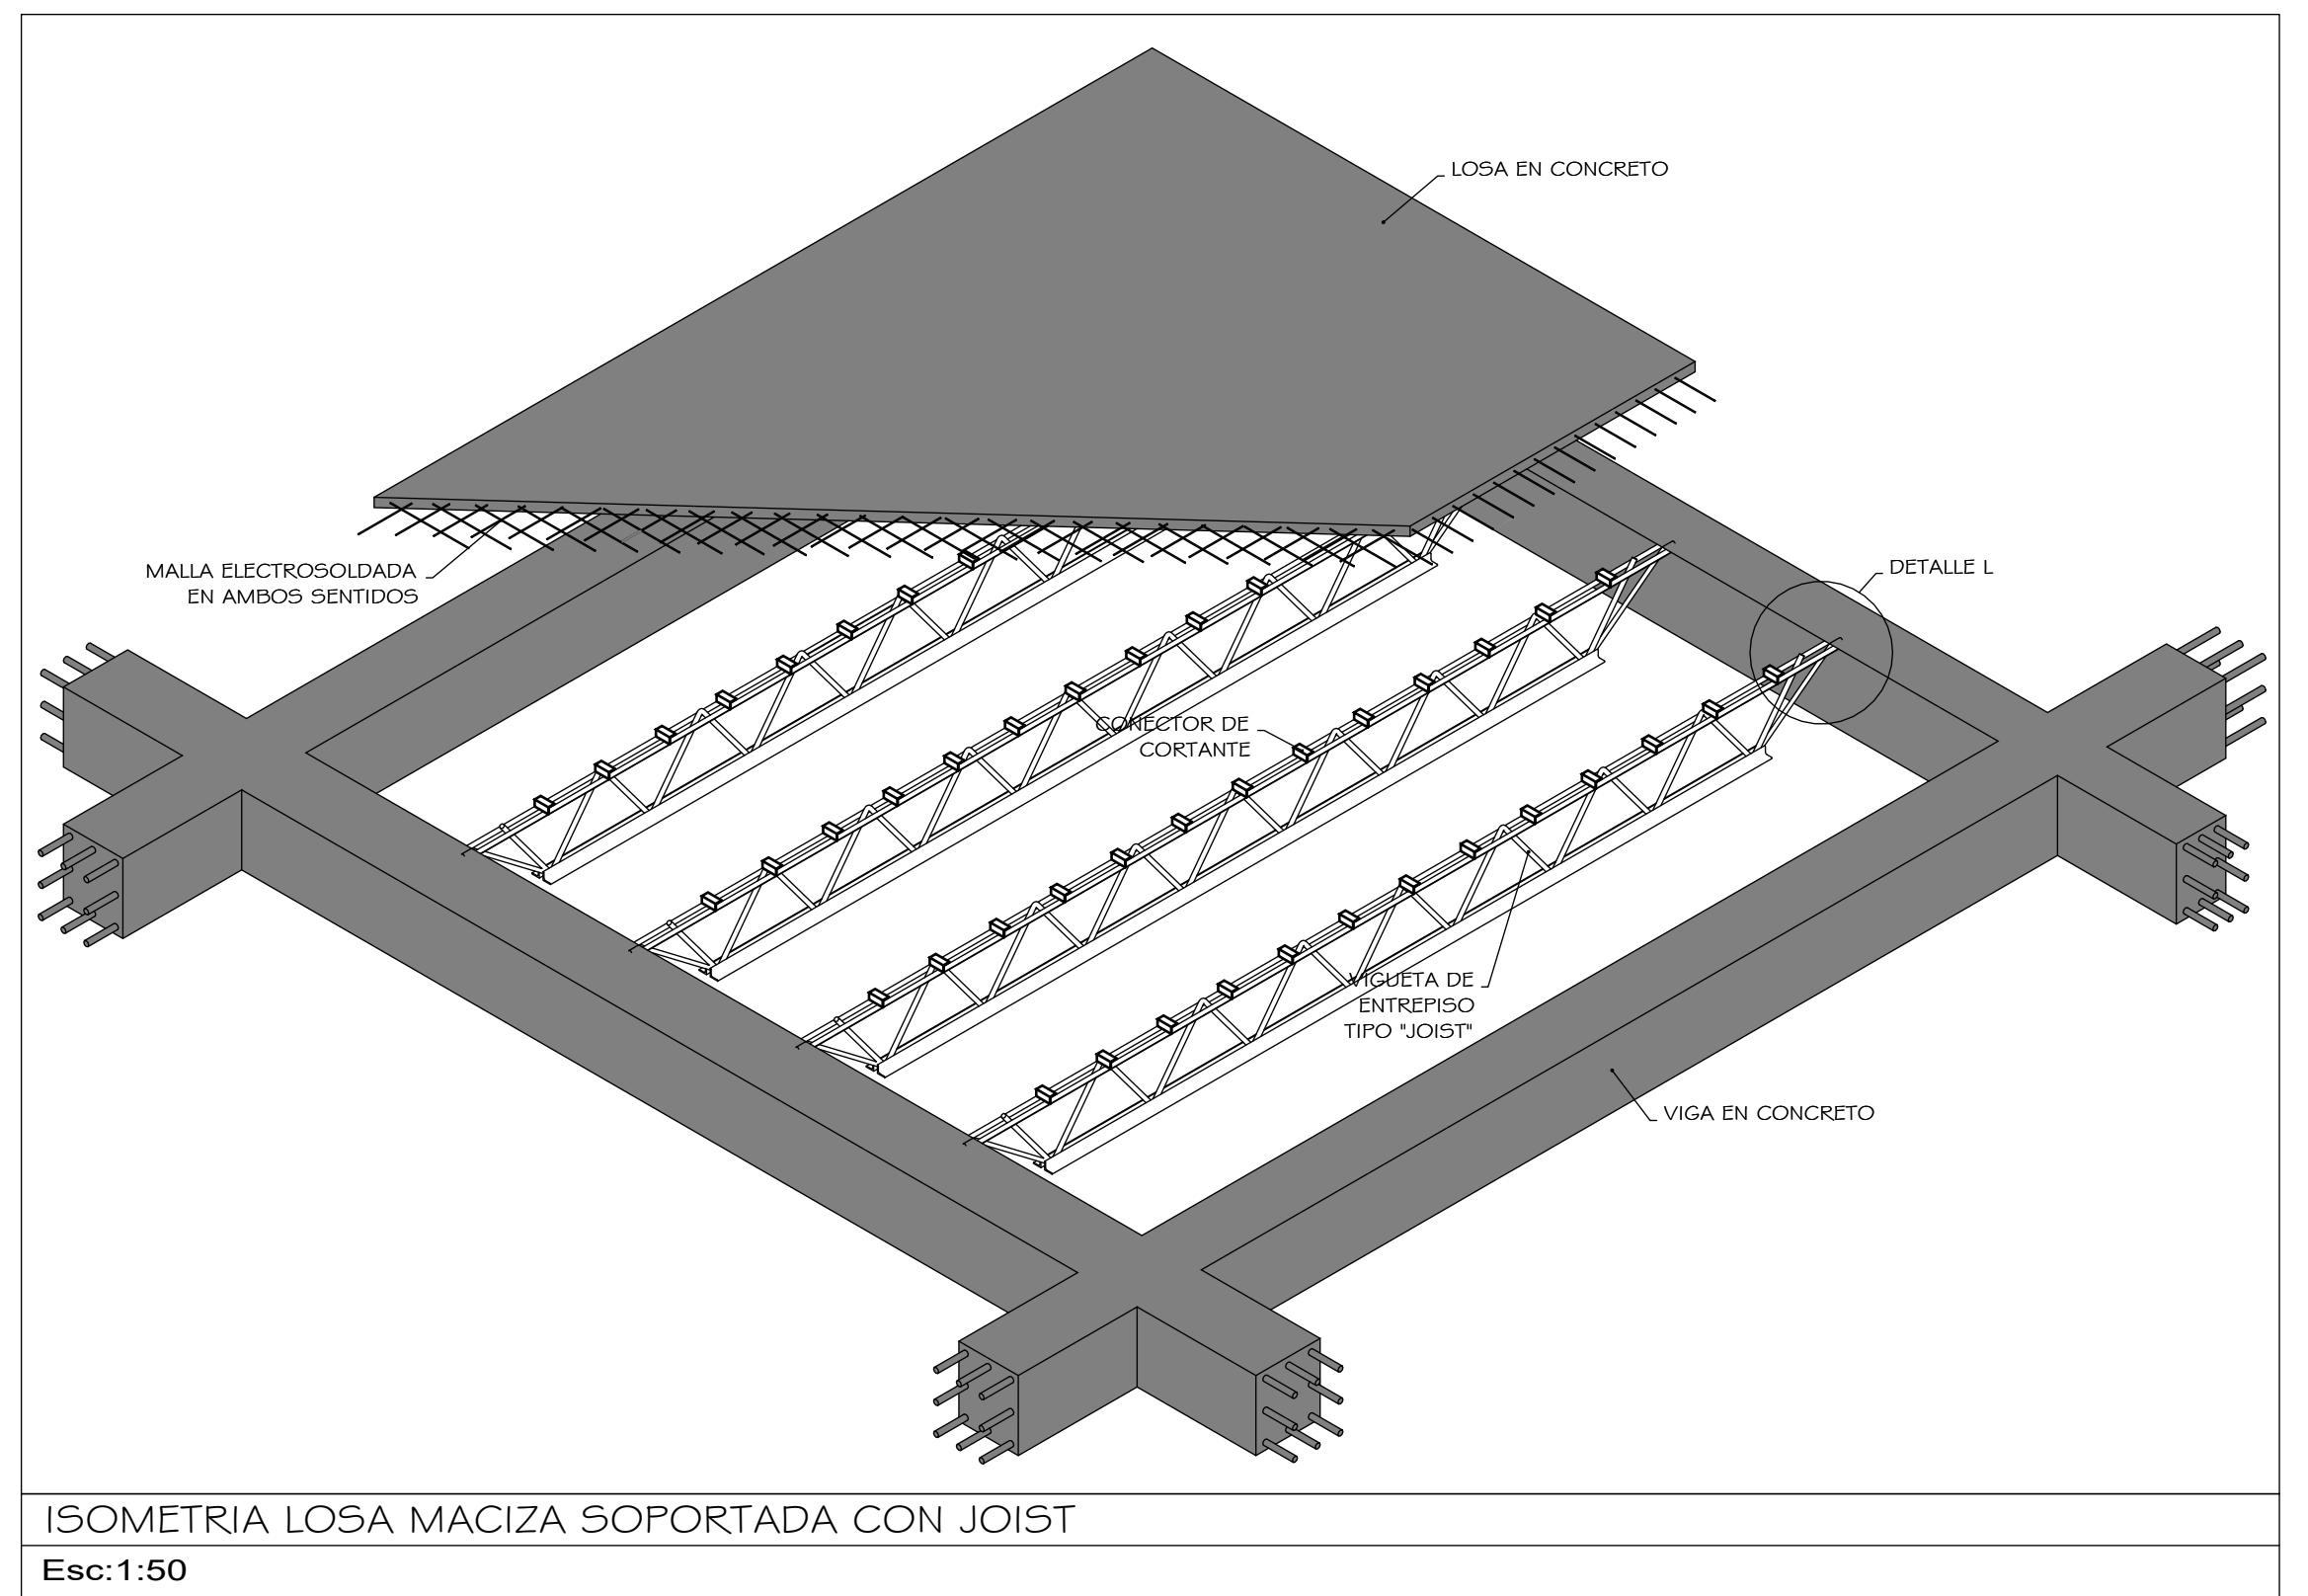
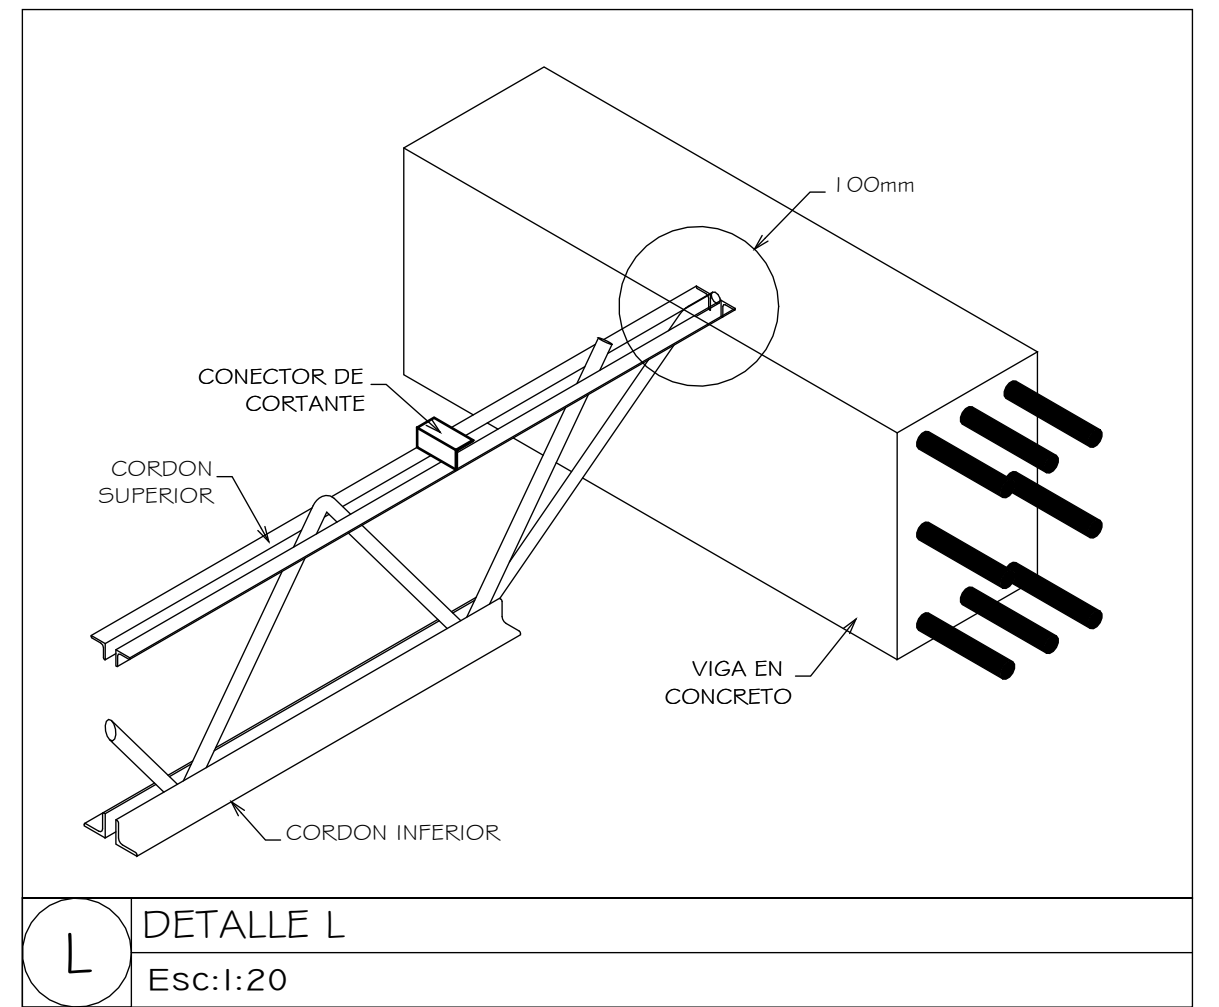
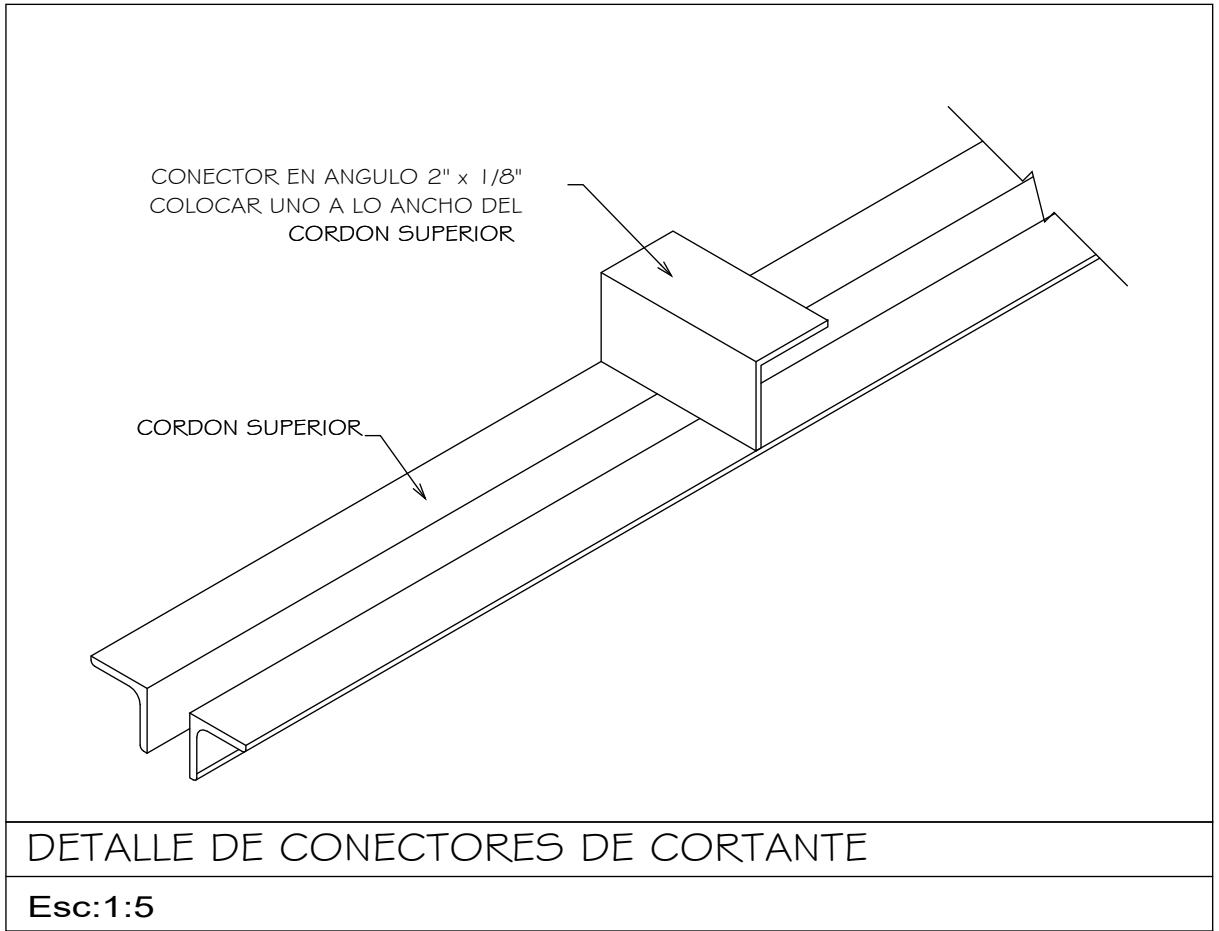
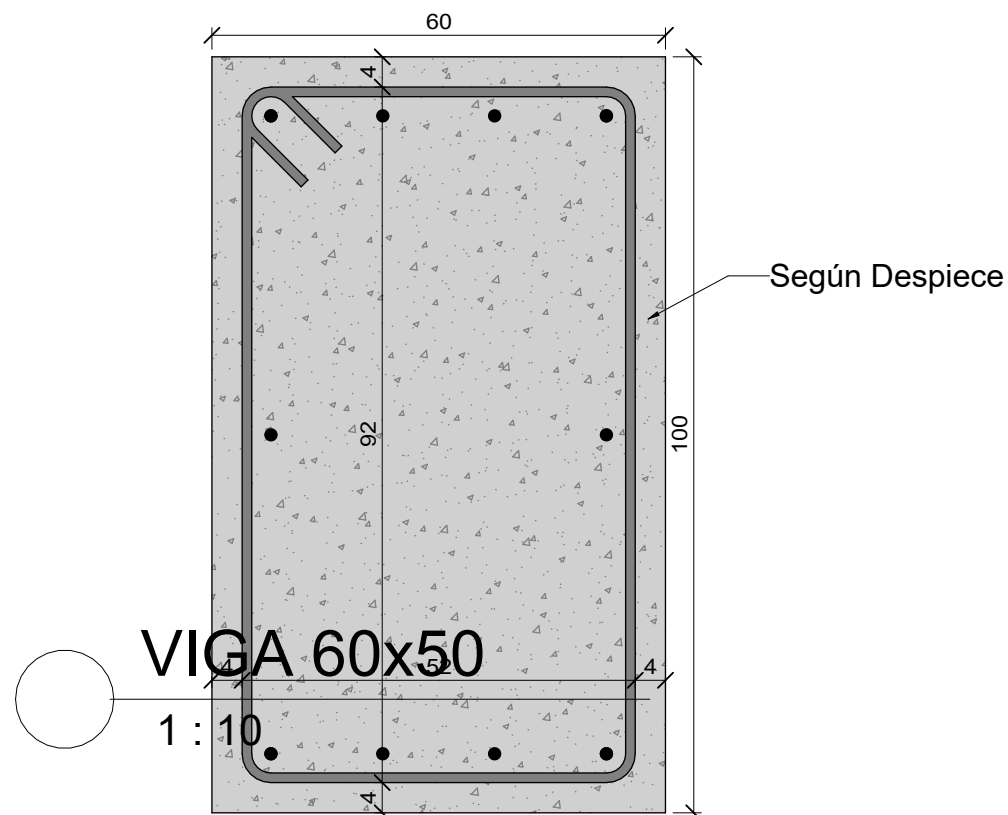


ESTE PLANO ES PROPIEDAD INTELECTUAL DE SOLARTE Y CIA. INGENIEROS CALCULISTAS S.A. SE PROHIBE SU REPRODUCCION O MODIFICACION PARCIAL O TOTAL. EN CASO DE MODIFICARSE VO UTILIZARSE INDEBIDAMENTE. LA EMPRESA QUEDA EXENTA DE CUALQUIER RESPONSABILIDAD QUE PUEDA DERIVAR DE SU UTILIZACION.

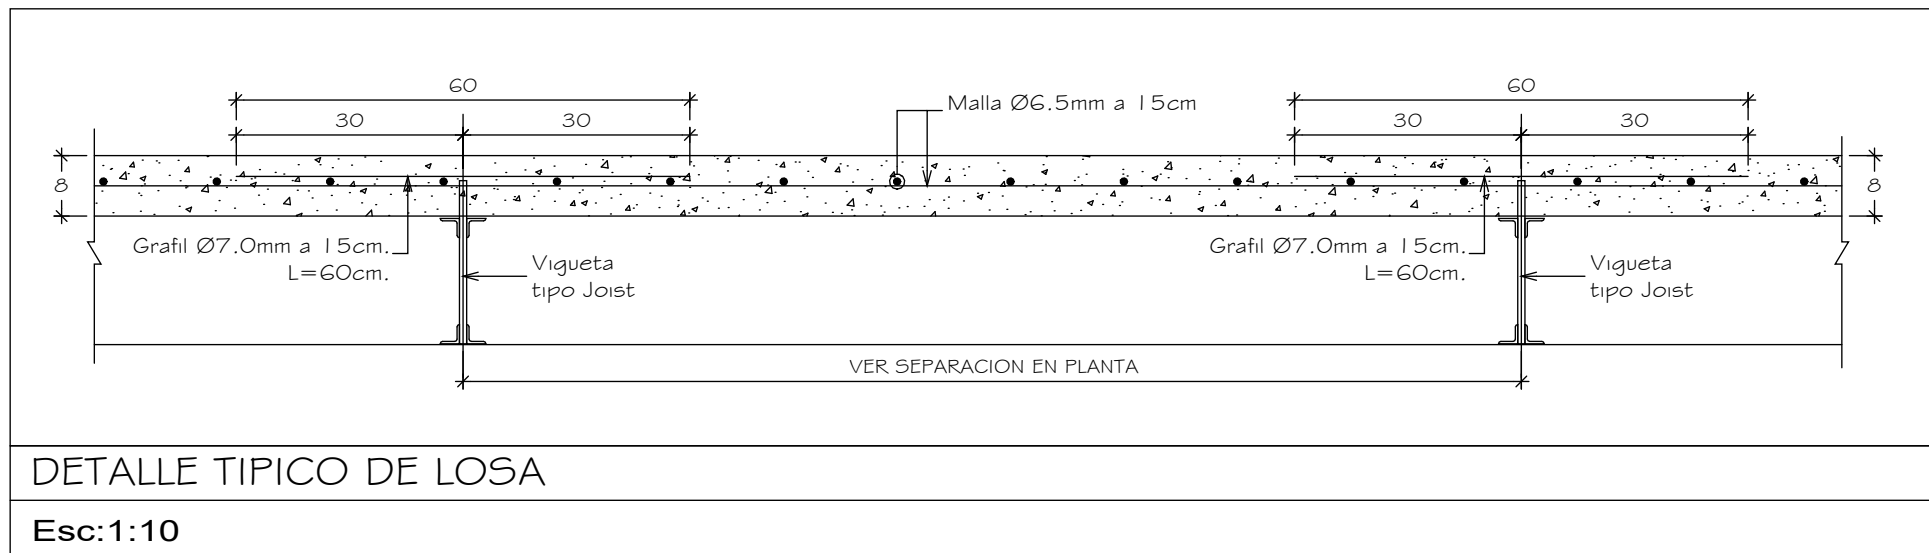

PISO 7
1 : 50

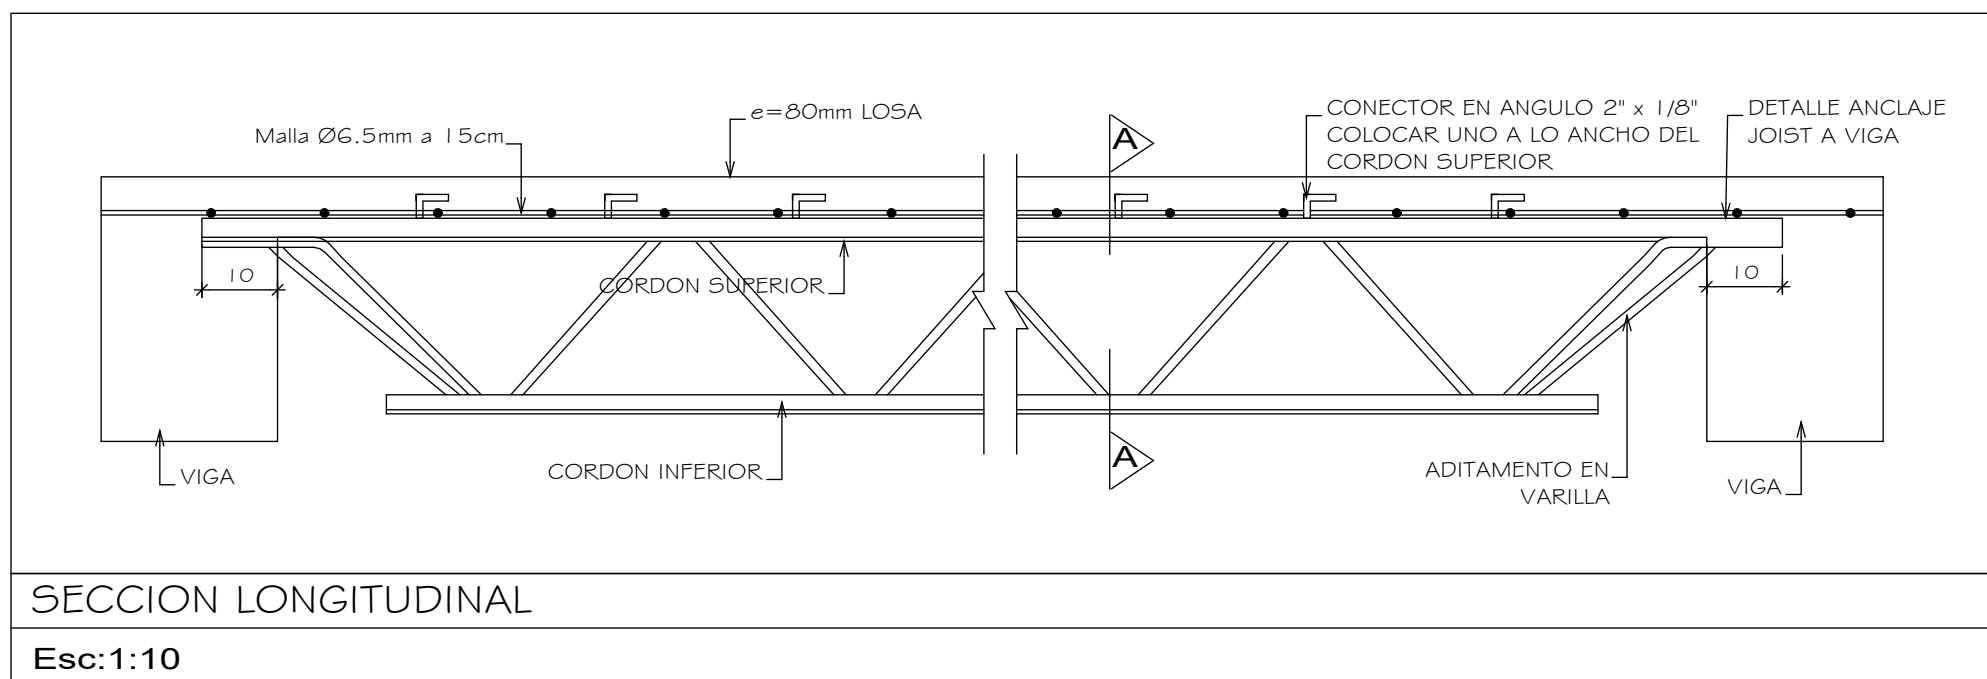

ESPECIFICACIONES DE MATERIALES

CONCRETO:		C.5.11: El concreto debe mantenerse húmedo por lo menos 7 días después de la fundición.	
CURADO DEL CONCRETO:		C.4.3.1: Según la clase de exposición, para garantizar durabilidad.	
RELACION a/mc PARA MEZCLAS DE CONCRETO:		C.3.3.2: Tamaño máximo nominal del agregado grueso.	
AGREGADOS:		C.3.3.2: Tamaño máximo nominal del agregado grueso.	
GENERALES:		El refuerzo debe cumplir C.21.1.5 (NTC2289-NTC2043)	
BARRAS:		Fy = 420 Mpa (4200 Kg/cm²) Corrugado para diámetros iguales o mayores a #2 debe cumplir Norma ASTM A-706. C.3.5.3.4	
MALLAS:		Fy ≥ 485 Mpa (4850 Kg/cm²) C.3.5.3.5 a C.3.5.3.10 NTC 5806	

RESISTENCIA AL FUEGO

GRUPO DE OCUPACION	CATEGORIA	ELEMENTO	TIEMPO
R2	1	Columnas - Vigas	1 (una) hora
		Losas Macizas	1 (una) hora
		Muros interiores no portantes	1 (una) hora
NORMA DISEÑO: NSR-10			

CURADURIA

Propietario:

Acción Fiduciaria S.A como vocera y administradora del Fideicomiso FA-6547 Proyecto Florentino

Proyecto:

EDIFICACIÓN DE VIVIENDA EN 8 PISOS Y 1 SOTANO
BARRIO EL PEÑON

Proyecto N°:

3772-25

Unidad Estructural:

EDIFICIO

Fecha:

FEBRERO 2026

Escala:

Como se indica

Proyecto Estructural:



Revisó:

ING. JUAN RAUL SOLARTE G.
Mat. 876 CAUCA

Diseño:

ING. JULIAN ENRIQUEZ

Colaboró:

ING. FABIAN ROJAS

Dibujó:

RENÉ MONTAÑO BOTERO

Contiene:

PLANO NIV. 7

Plano N°:

107

Versión: