
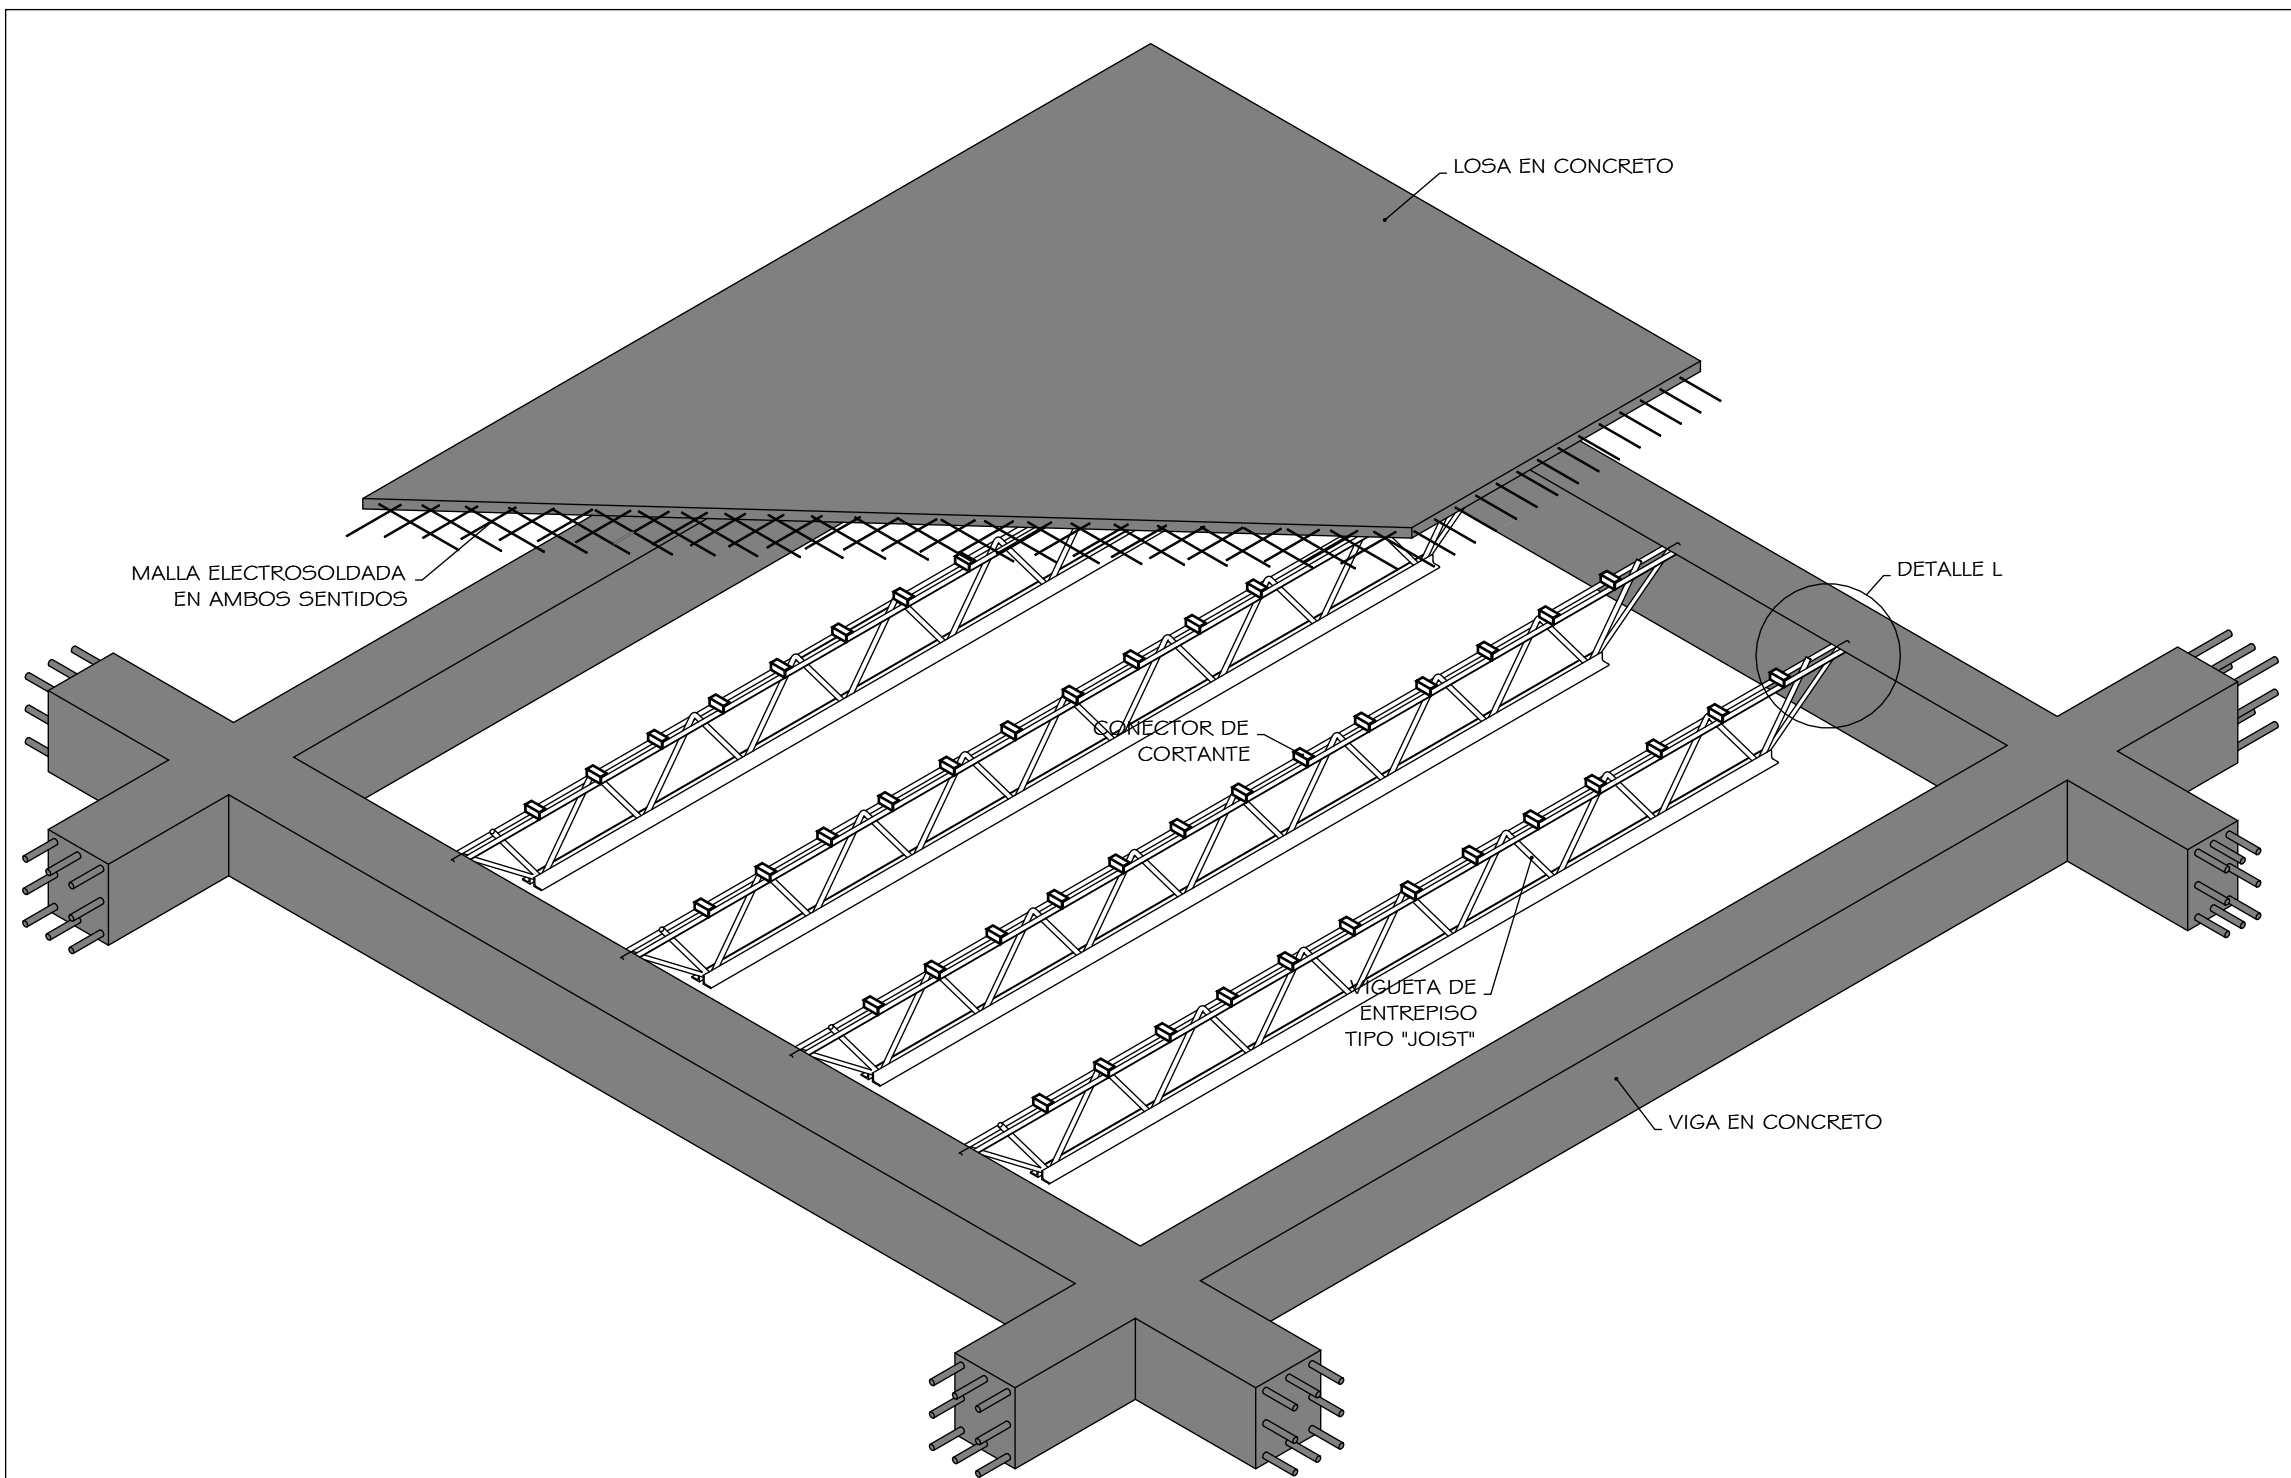
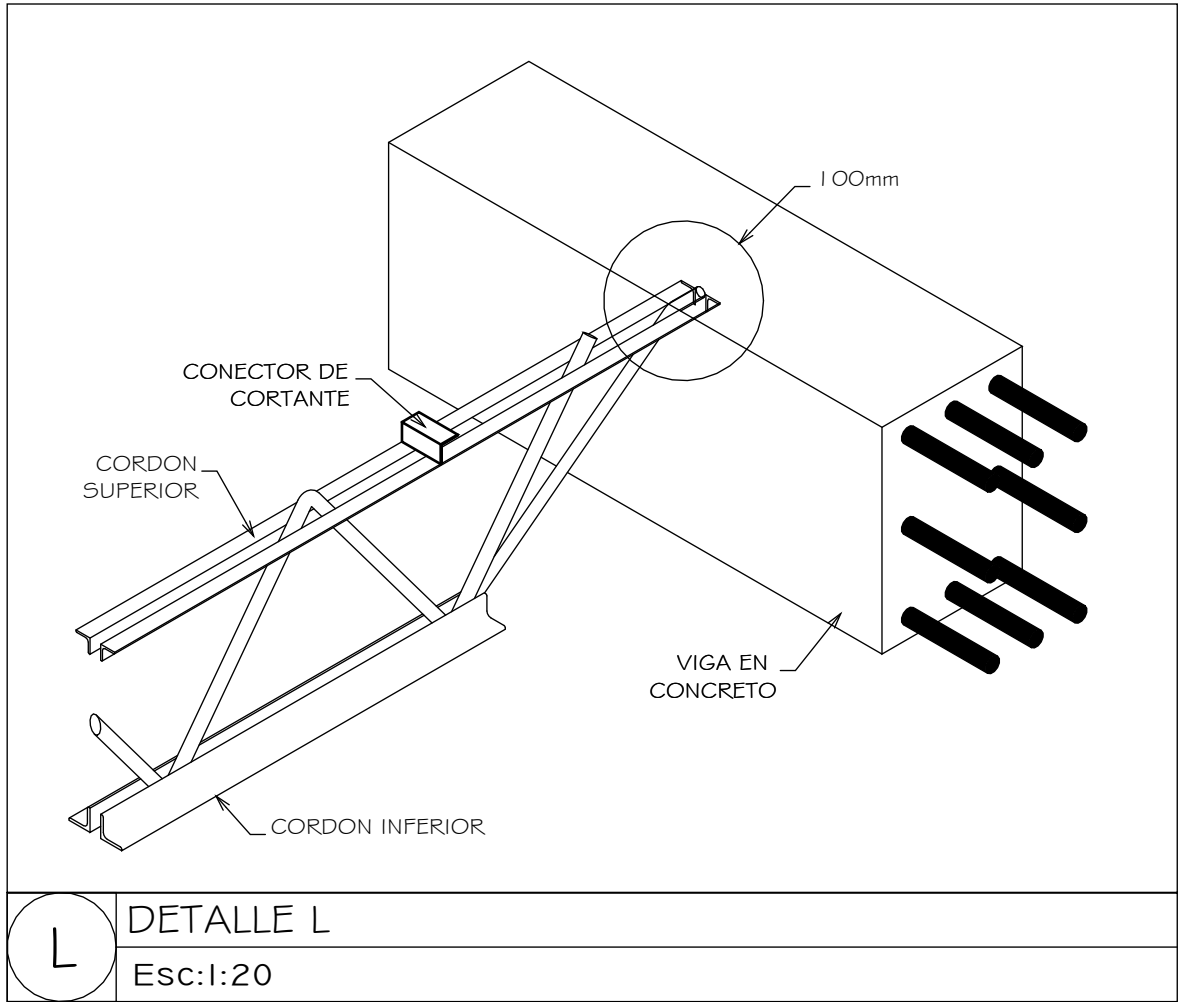
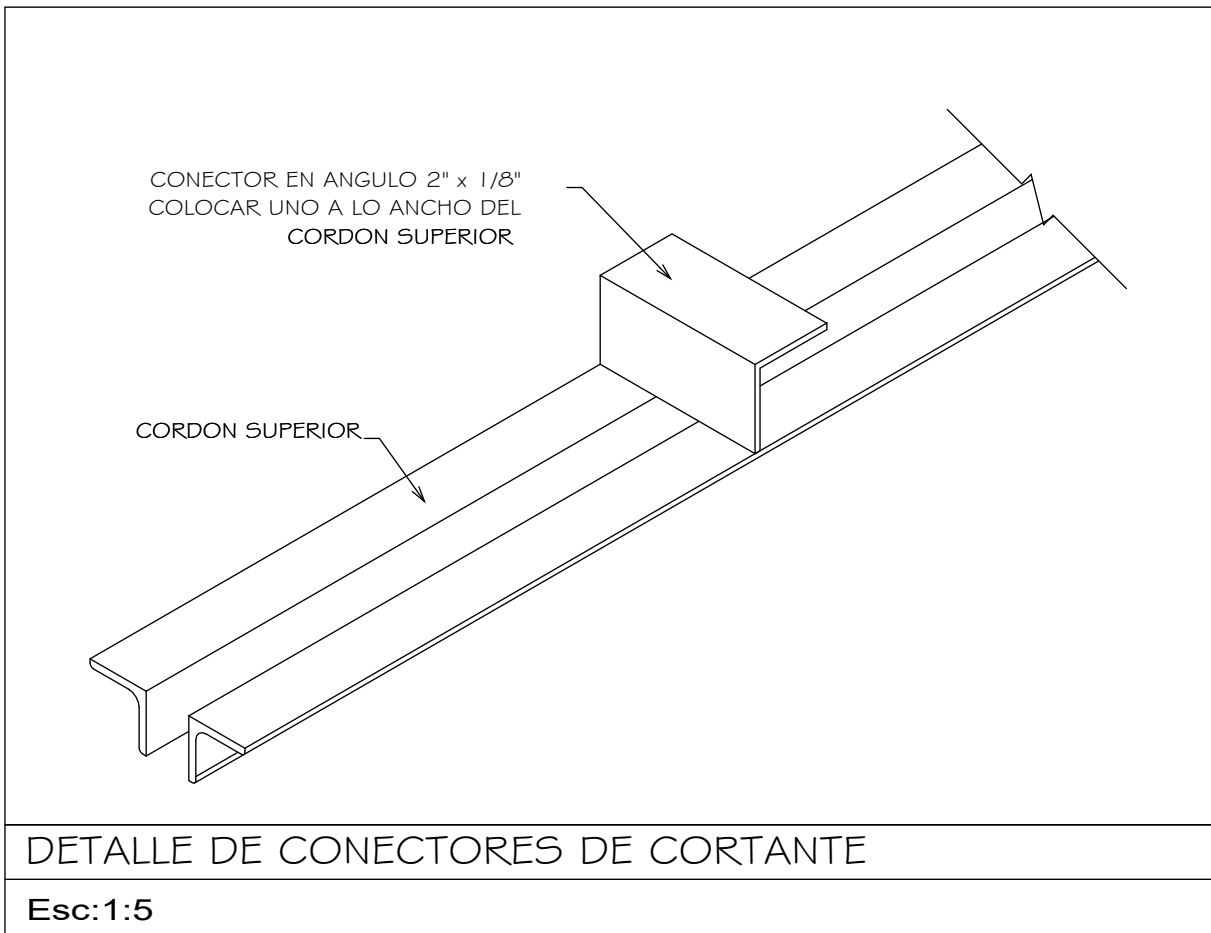
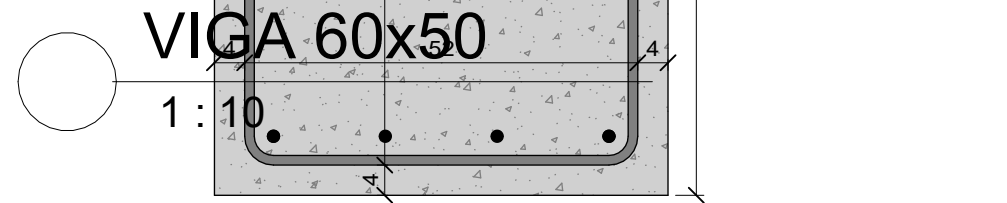


ESTE PLANO ES PROPIEDAD INTELECTUAL DE SOLARTE Y CIA. INGENIEROS CALCULISTAS S.A. SE PROHIBE SU REPRODUCCION O MODIFICACION PARCIAL O TOTAL. EN CASO DE MODIFICARSE VO UTILIZARSE INDEBIDAMENTE. LA EMPRESA QUEDA EXENTA DE CUALQUIER RESPONSABILIDAD QUE PUEDA DERIVAR DE SU UTILIZACION.



3772-25

EDIFICACIÓN DE VIVIENDA EN 8 PISOS Y 1 SOTANO

108 PLANO NIV. 8

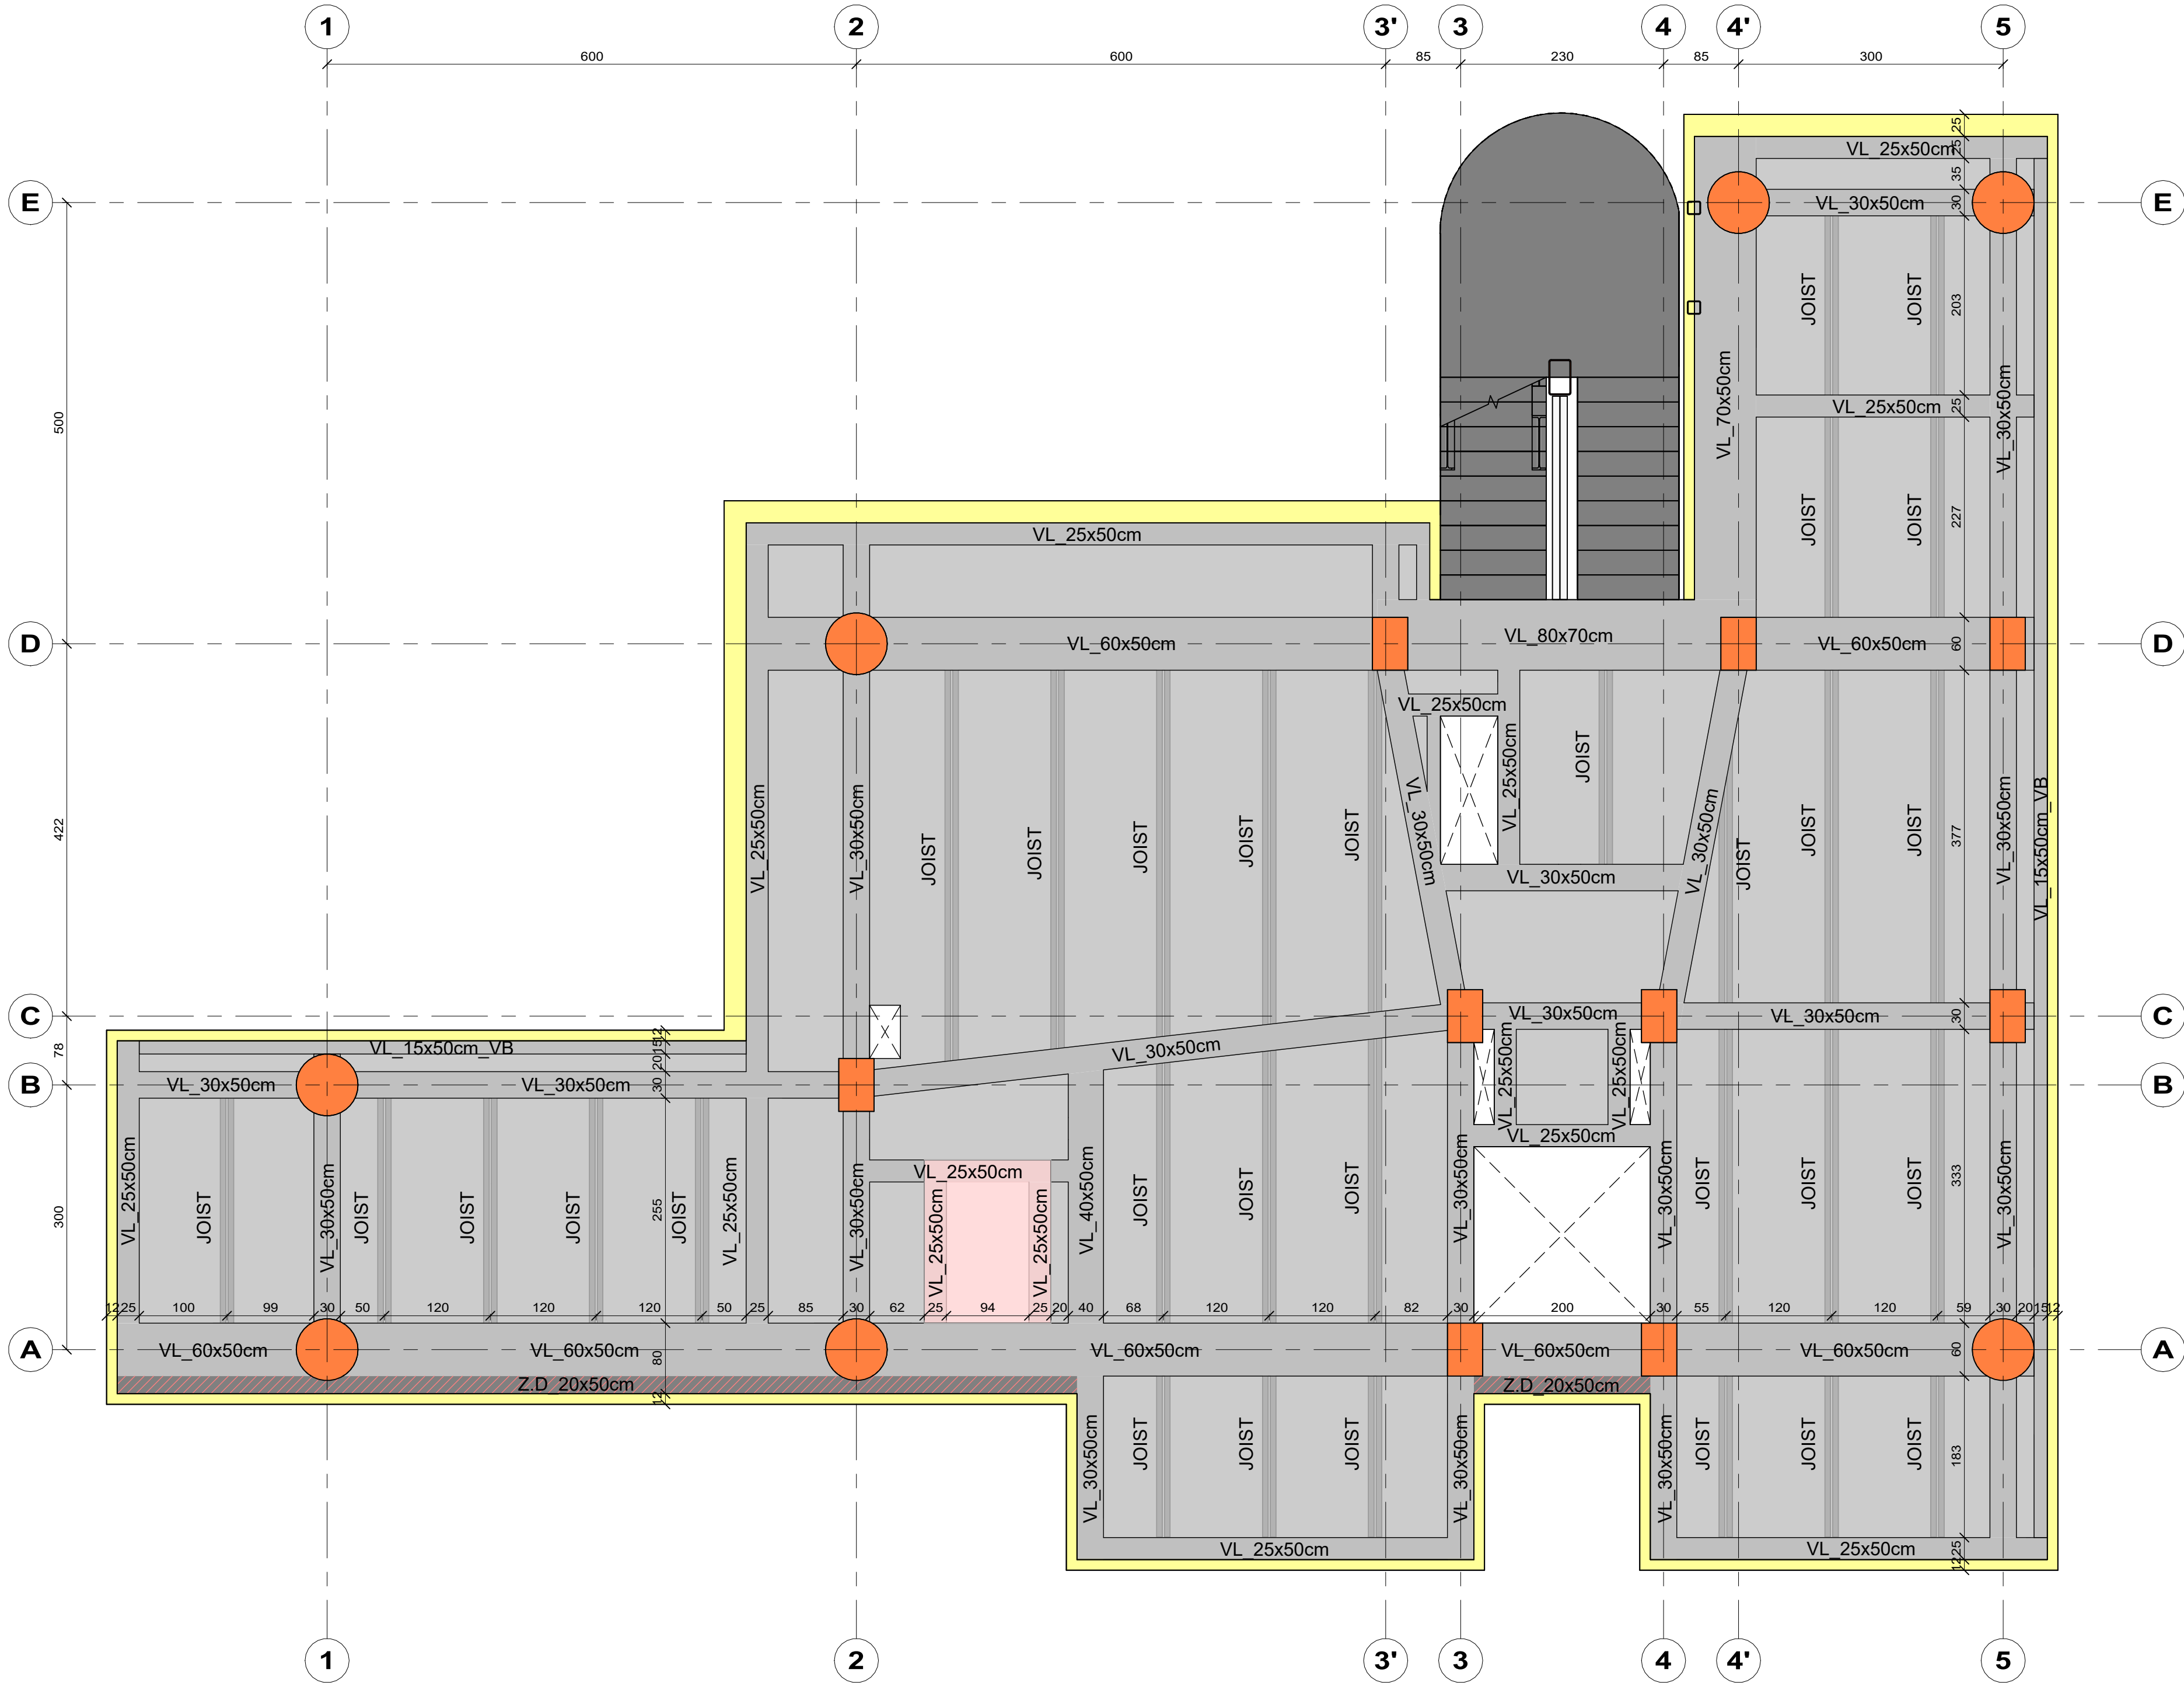

1 PISO 8
1:50

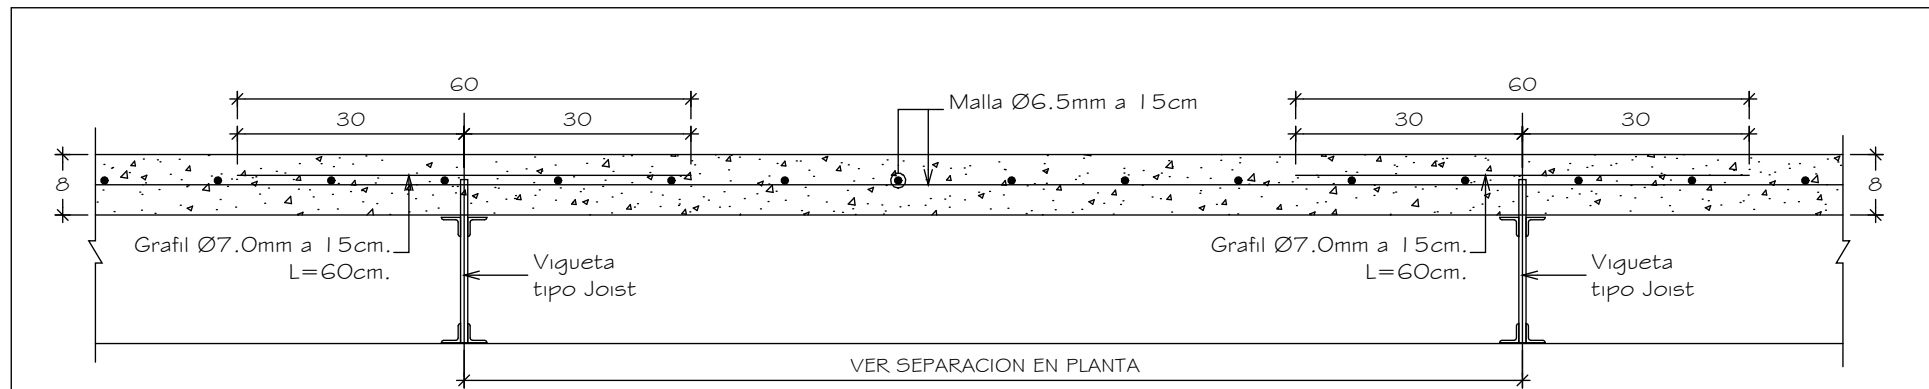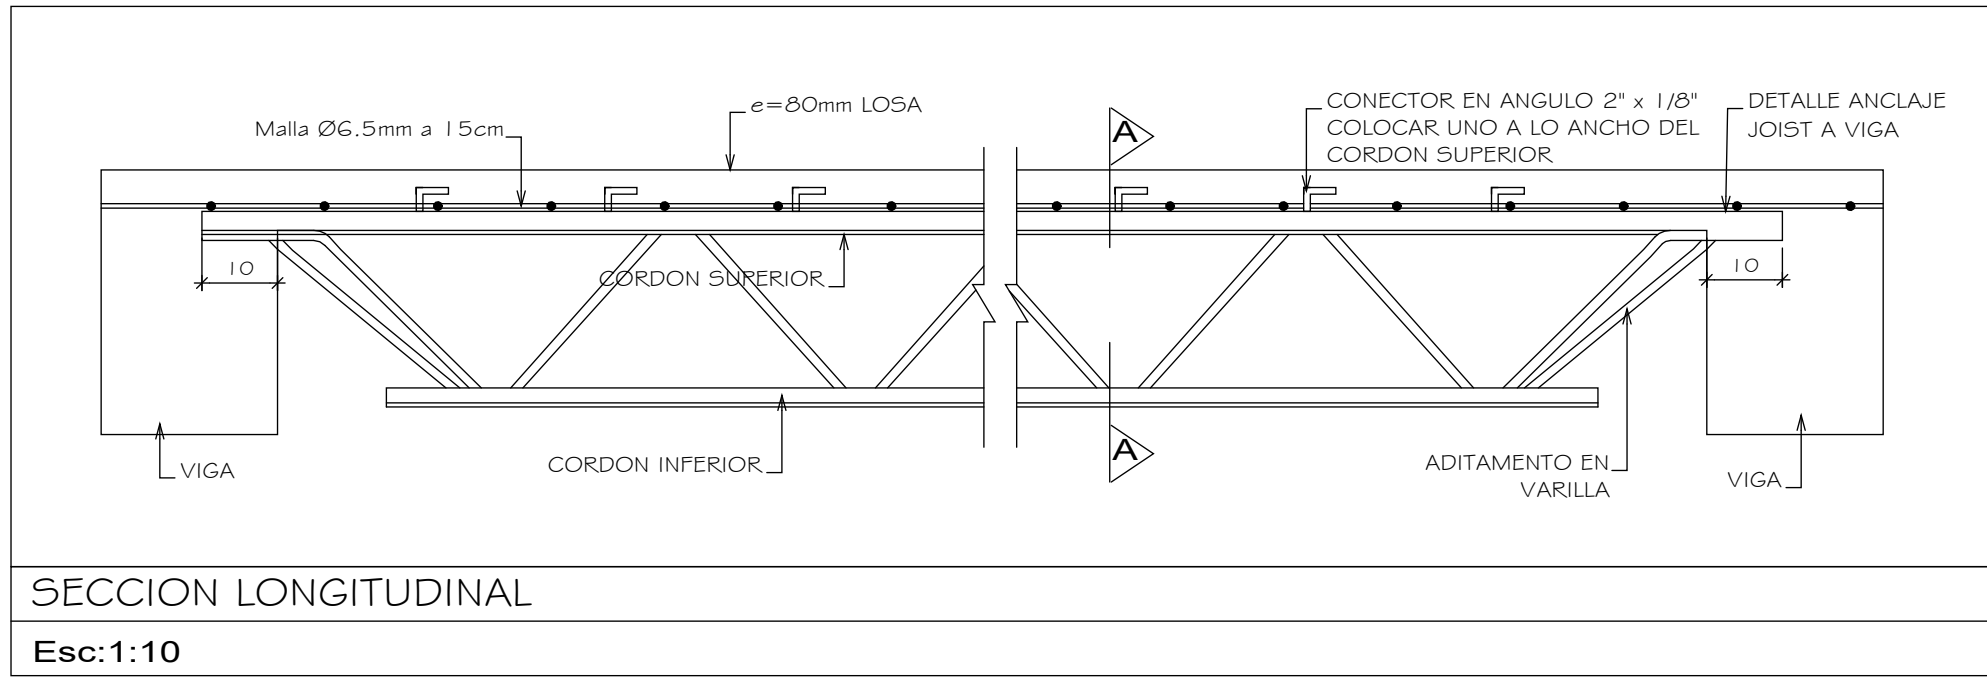

ESPECIFICACIONES DE MATERIALES

CONCRETO:
CURADO DEL CONCRETO:
RELACION a/mc PARA MEZCLAS DE CONCRETO:
AGREGADOS:
GENERALES:
BARRAS:
MALLAS:

RESISTENCIA AL FUEGO			
GRUPO DE EXPOSICION	CATEGORIA	ELEMENTO	TIEMPO
R2	1	Columnas - Vigas	1 (una) hora
		Losas Macizas	1 (una) hora
		Muros interiores no portantes	1 (una) hora

NORMA DISEÑO: NSR-10

CURADURIA

Propietario: Acción Fiduciaria S.A como vocera y administradora del Fideicomiso FA-6547 Proyecto Florentino		Proyecto Estructural: SOLARTE Y CIA	
Proyecto: EDIFICACIÓN DE VIVIENDA EN 8 PISOS Y 1 SOTANO BARRIO EL PEÑON		Revisó: ING. JUAN RAUL SOLARTE G. Mat. 876 CAUCA	
Proyecto N°: 3772-25		Diseño: ING. JULIAN ENRIQUEZ	
Unidad Estructural: EDIFICIO		Colaboró: ING. FABIAN ROJAS	
Fecha: FEBRERO 2026		Dibujó: RENÉ MONTAÑO BOTERO	
Escala: Como se indica		Contiene: PLANO NIV. 8	
		Plano N°: 108	
		Versión:	