




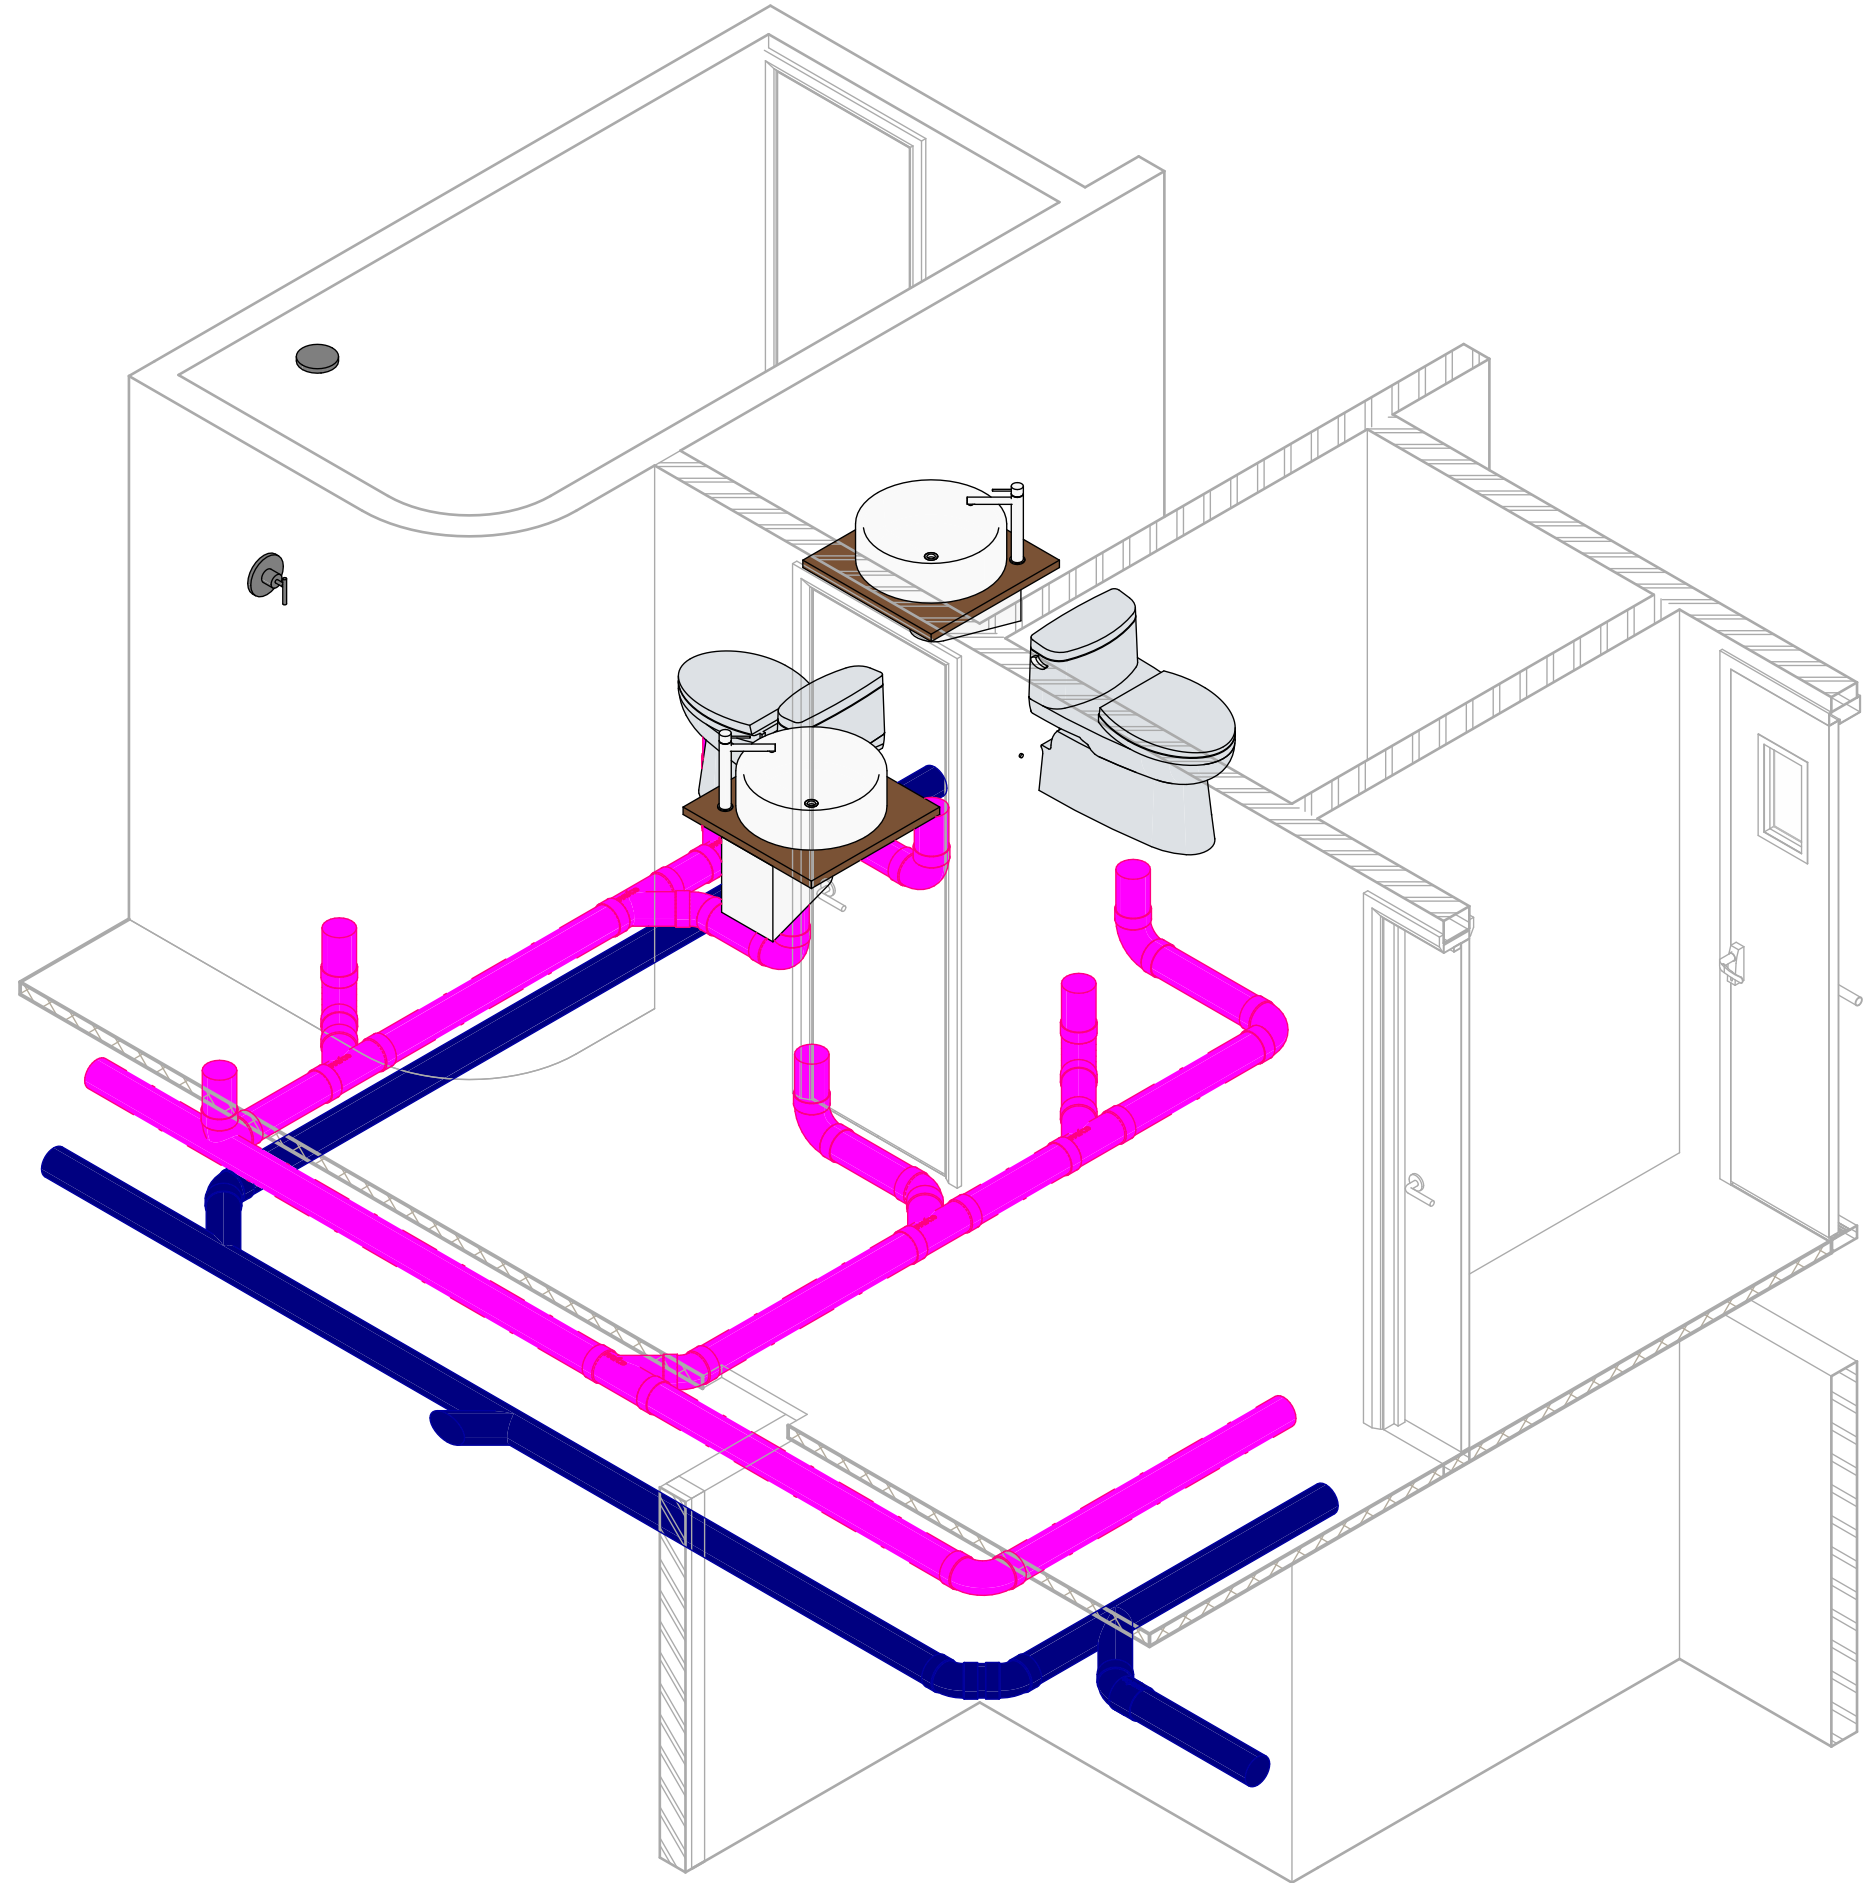


2 3D_CL_PISO 2 - SANITARIO

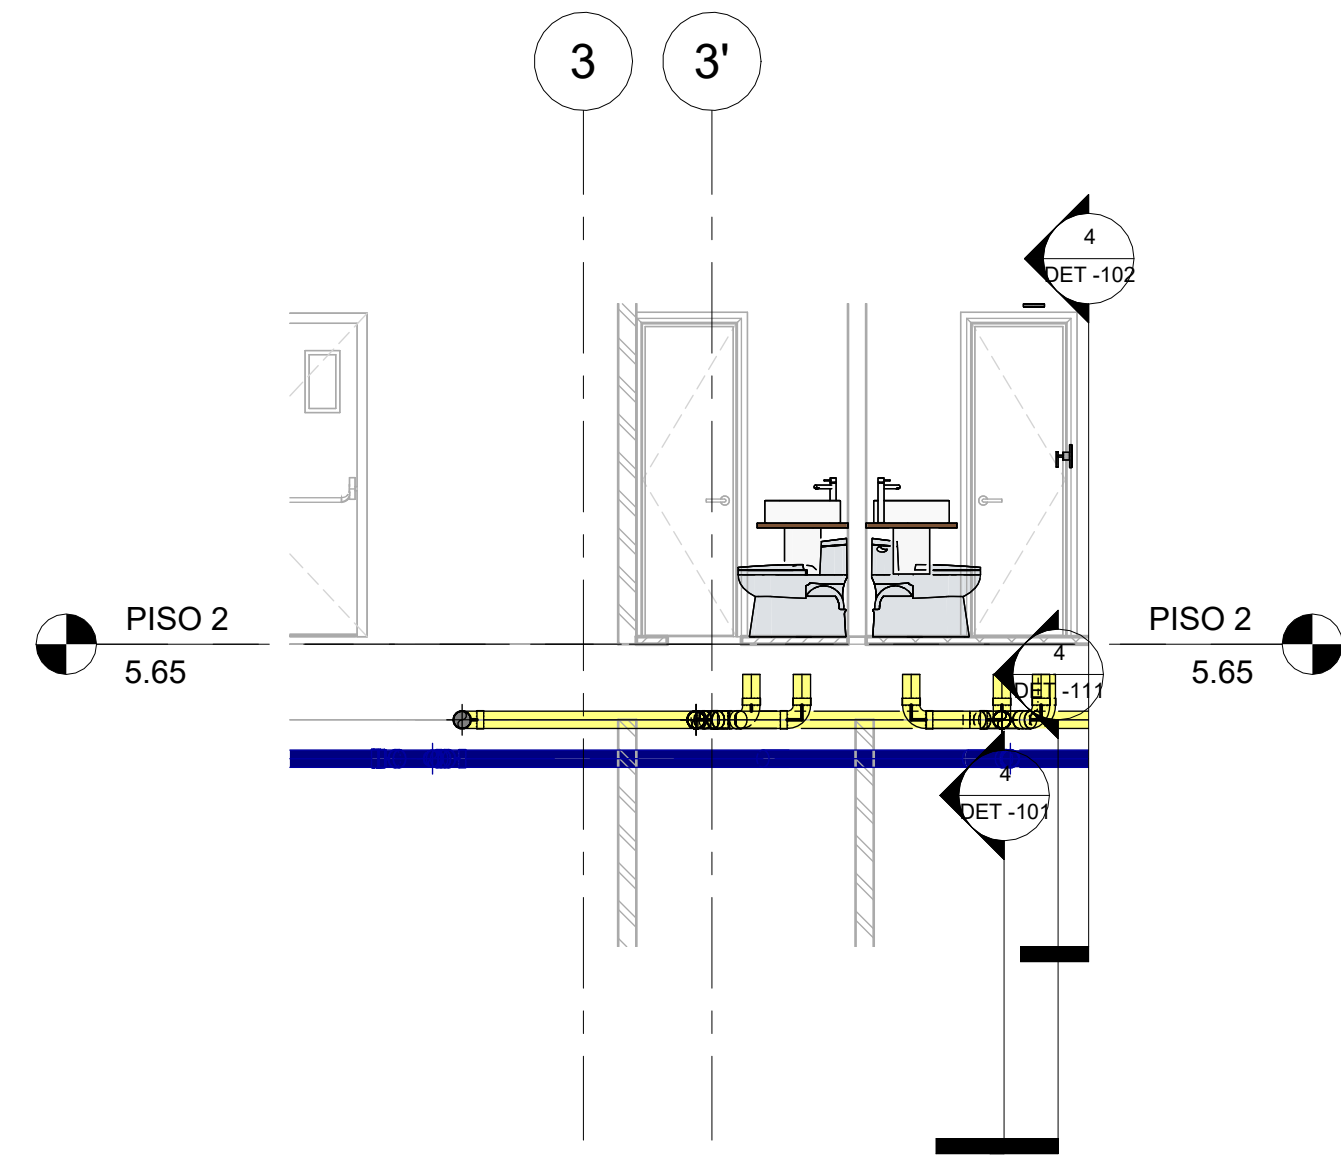

3 SEC_Long_CL_PISO 2 - SANITARIO
1 : 50

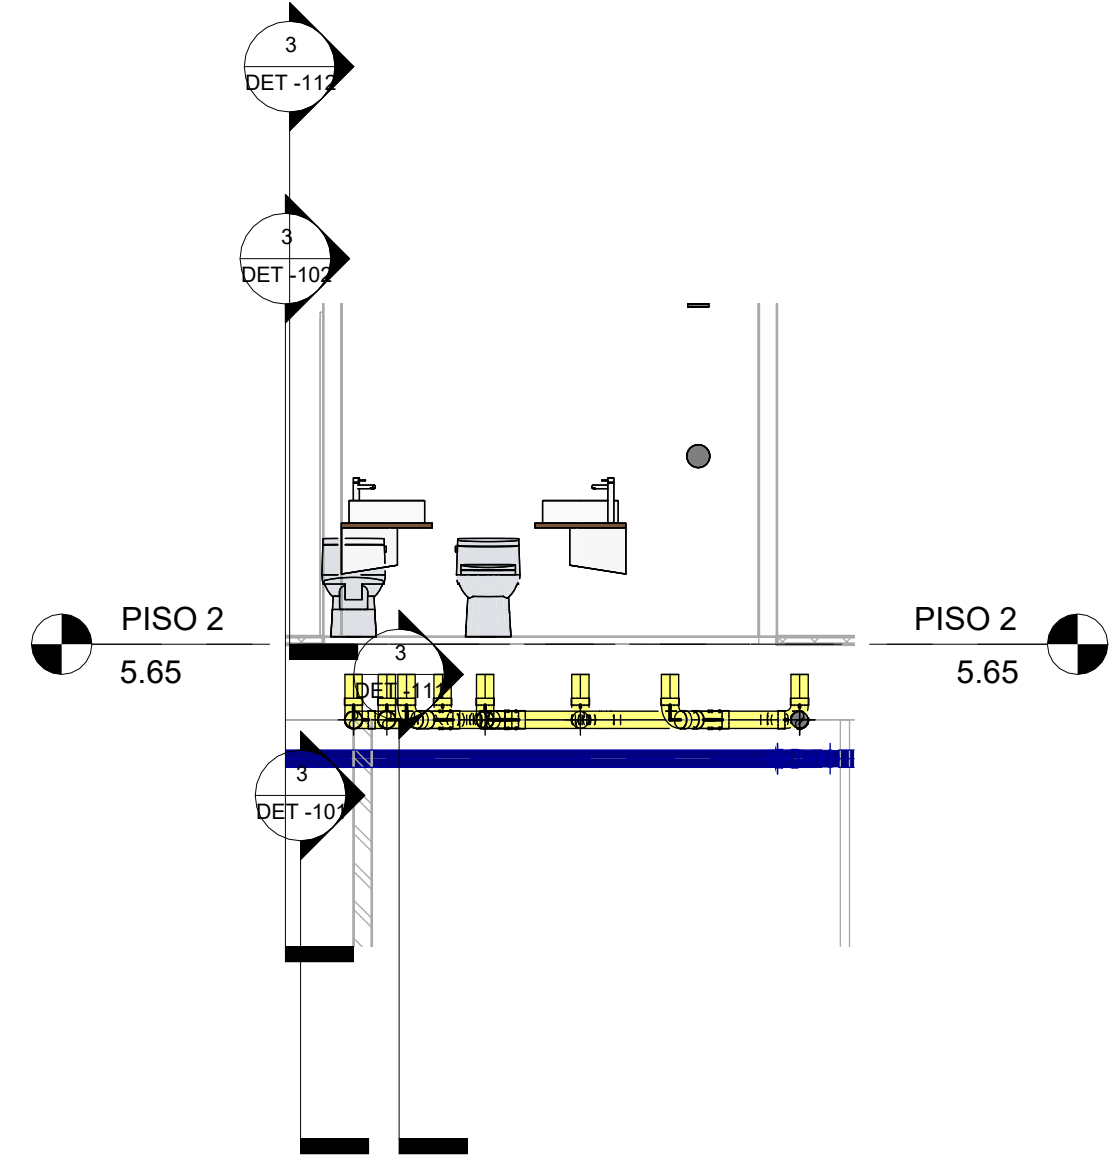

4 SEC_Trans_CL_PISO 2 - SANITARIO
1 : 50

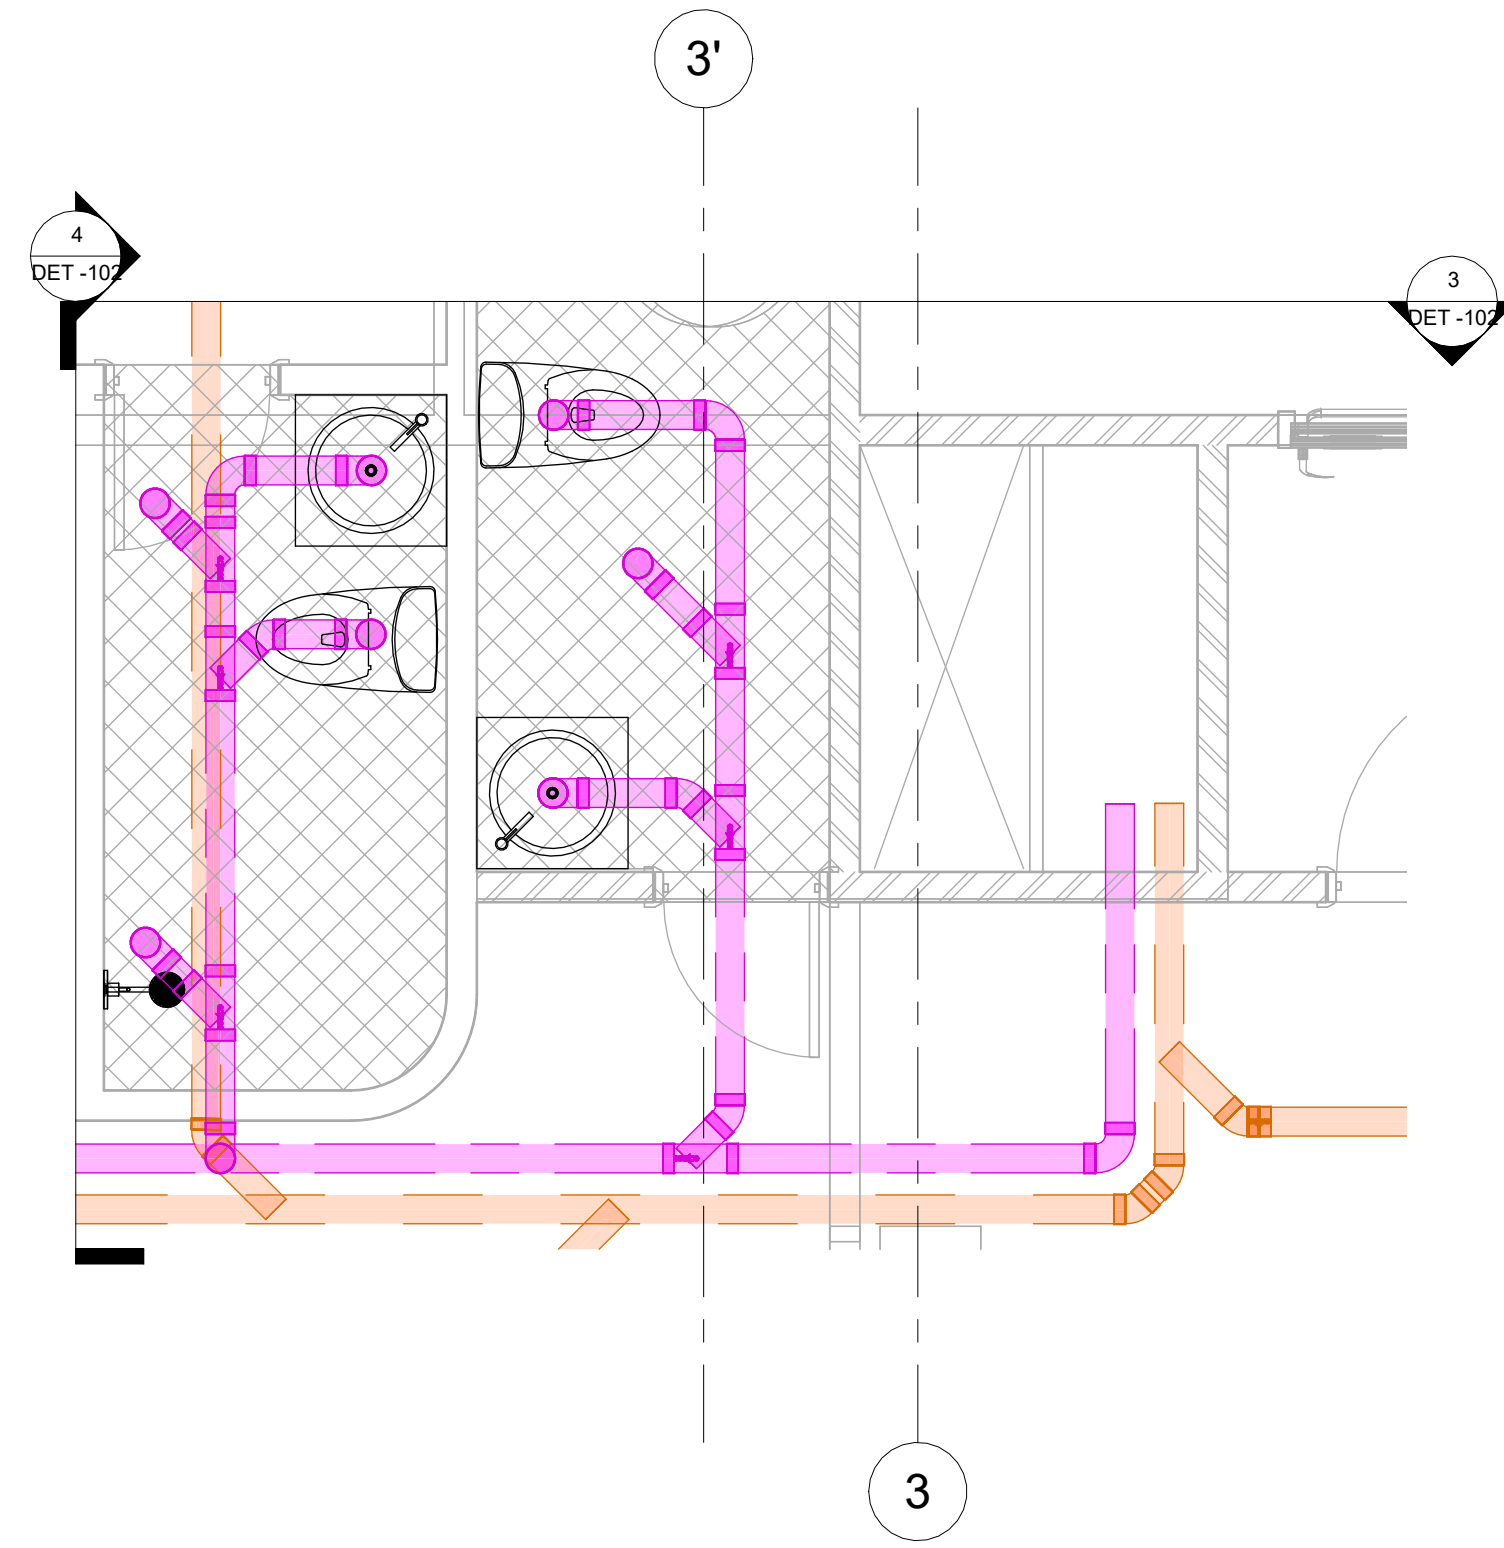

1 CL_PISO 2 - SANITARIO
1 : 30

EMCALI		GERENCIA DE UEN ACUEDUCTO Y ALCANTARILLADO	
		UNIDAD DE INGENIERIA	
FLORENTINO LIVING			
DETALLE 2			
PROYECTO	Designer	CALCULO:	Checker
PRESUPUESTO No.		DIBUJO:	Author
		REVISO:	Checker
ESCALA:	Como se indica	APROBO:	Approver
FECHA:	SEPTIEMBRE 2025	ARCHIVO:	

FECHA	REVISIONES	REVISO	APROBO