




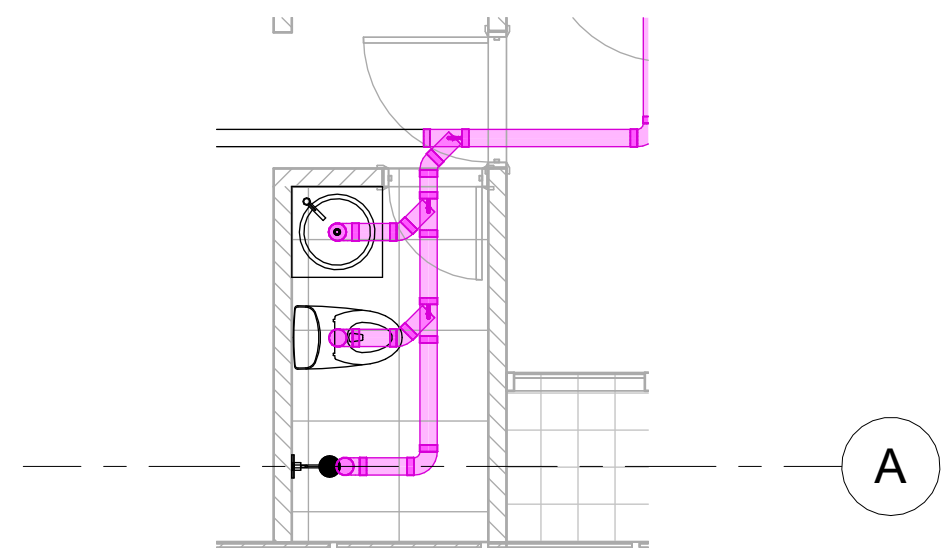


1 CL_PISO 3 - SANITARIO
1 : 50

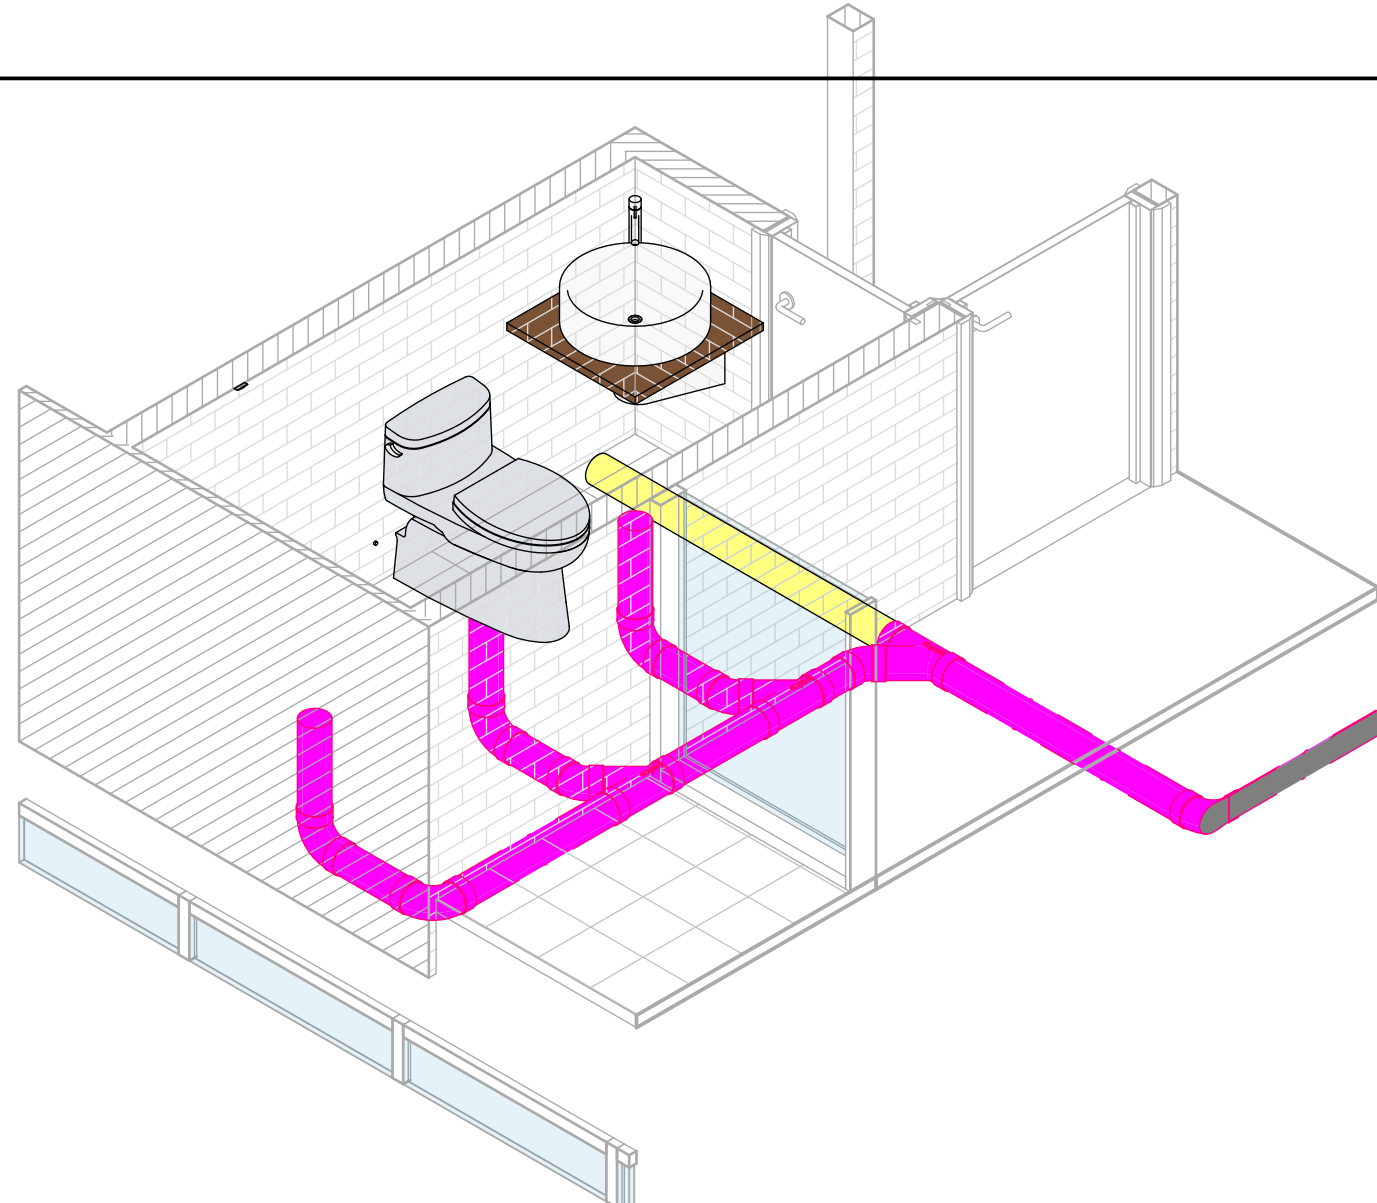


2 3D_CL_PISO 3 - SANITARIO

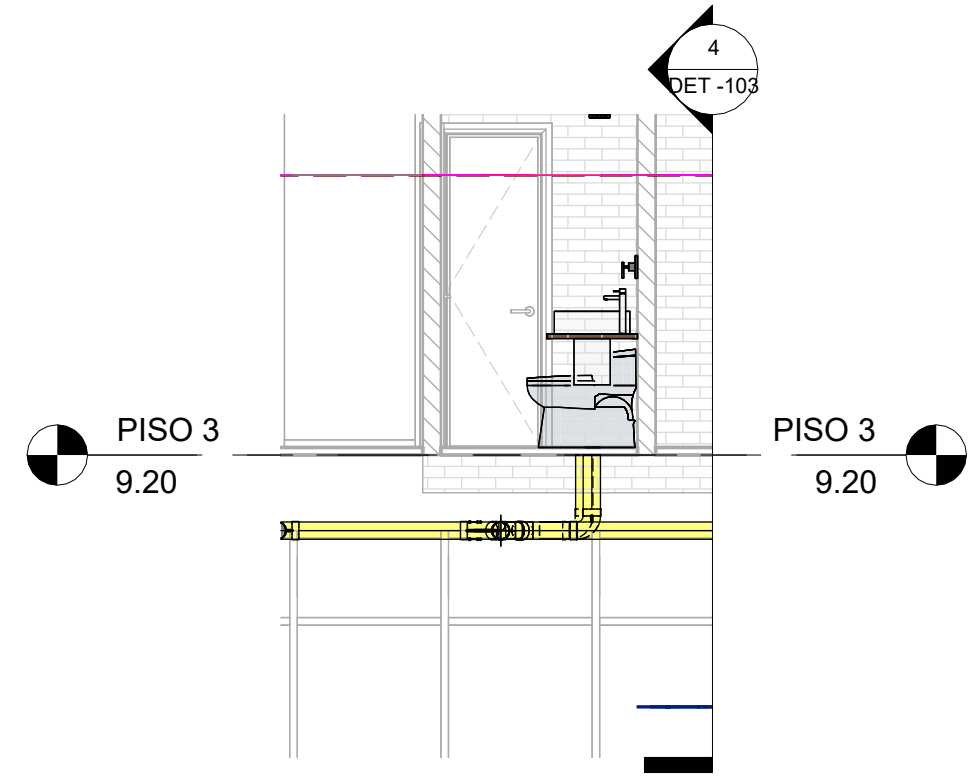


3 SEC_Long_CL_PISO 3 - SANITARIO
1 : 50

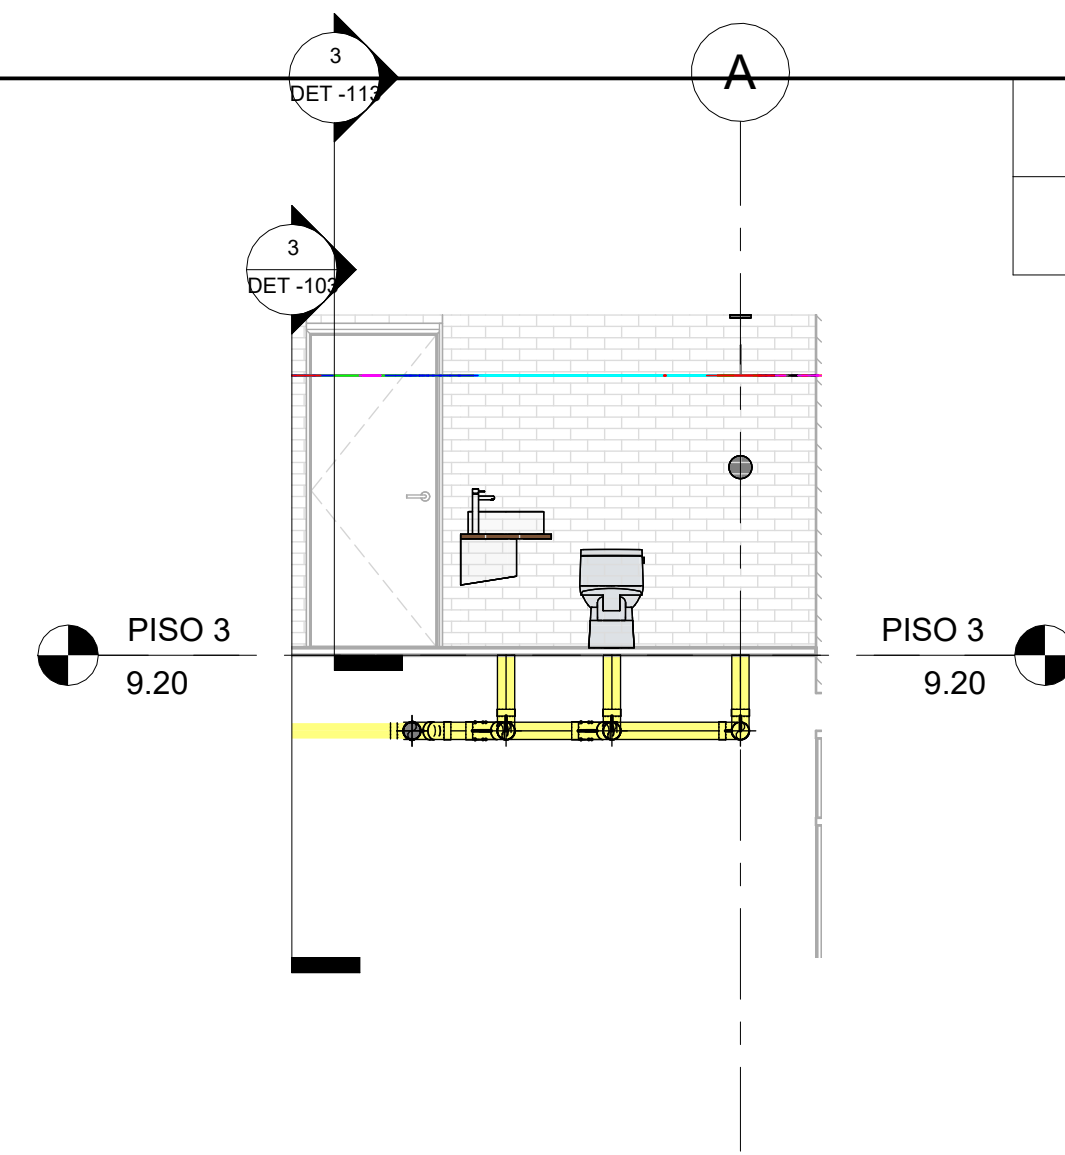


4 SEC_Trans_CL_PISO 3 - SANITARIO
1 : 50

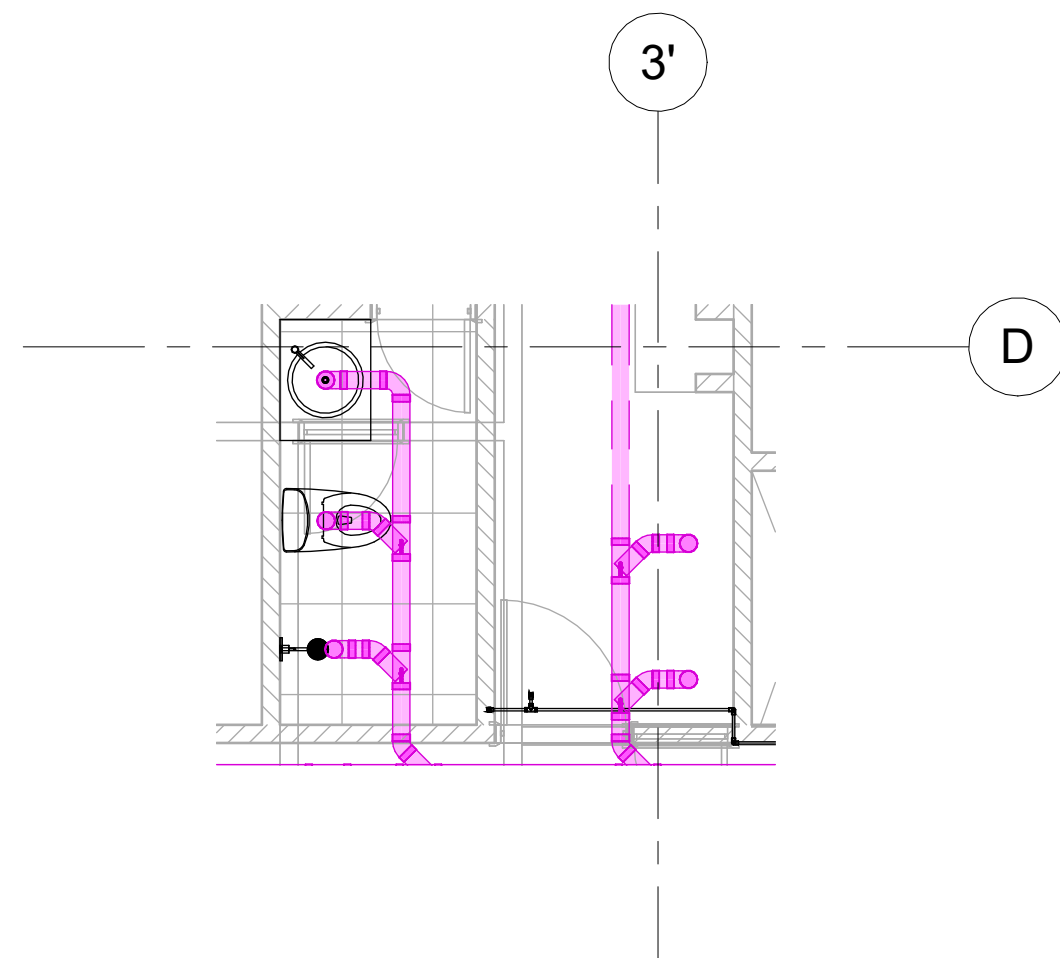


5 CL_PISO 3 - SANITARIO_2
1 : 50

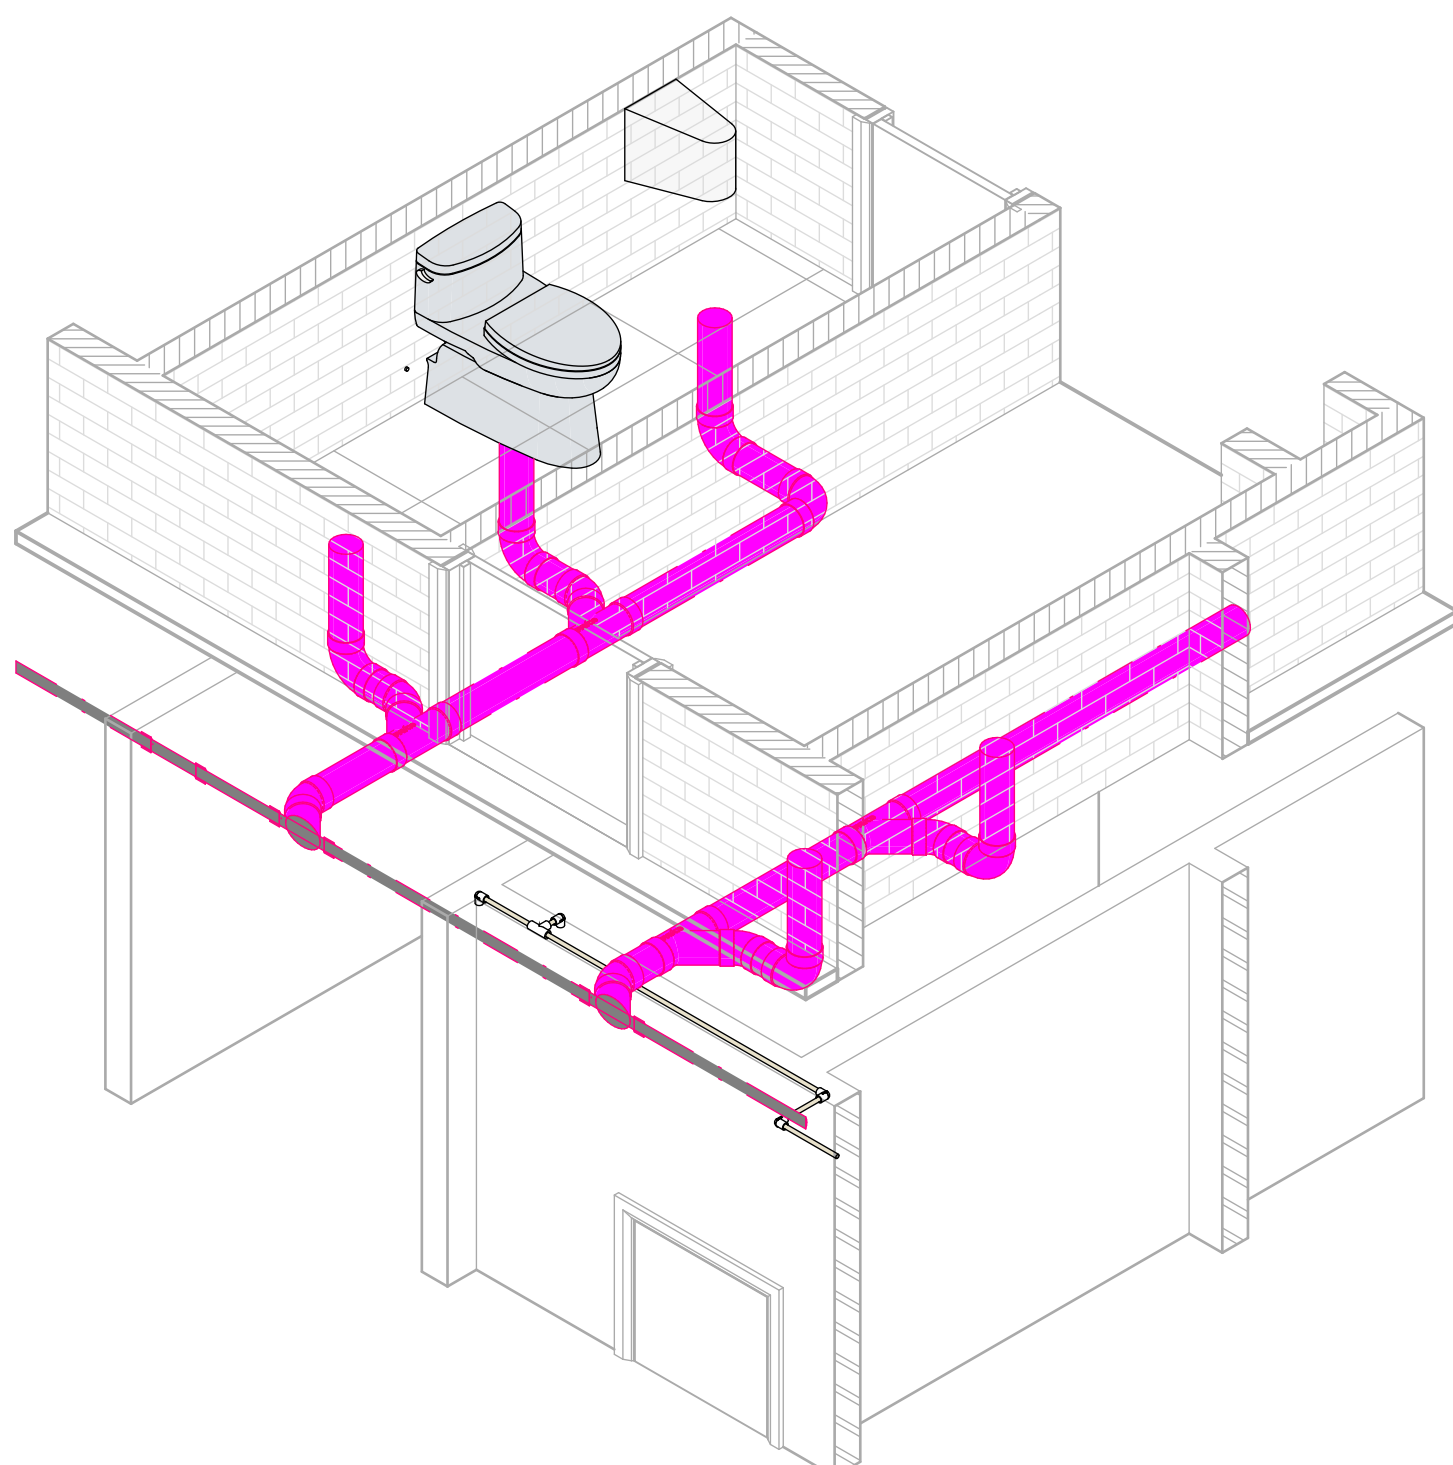


6 3D_CL_PISO 3 - SANITARIO_2

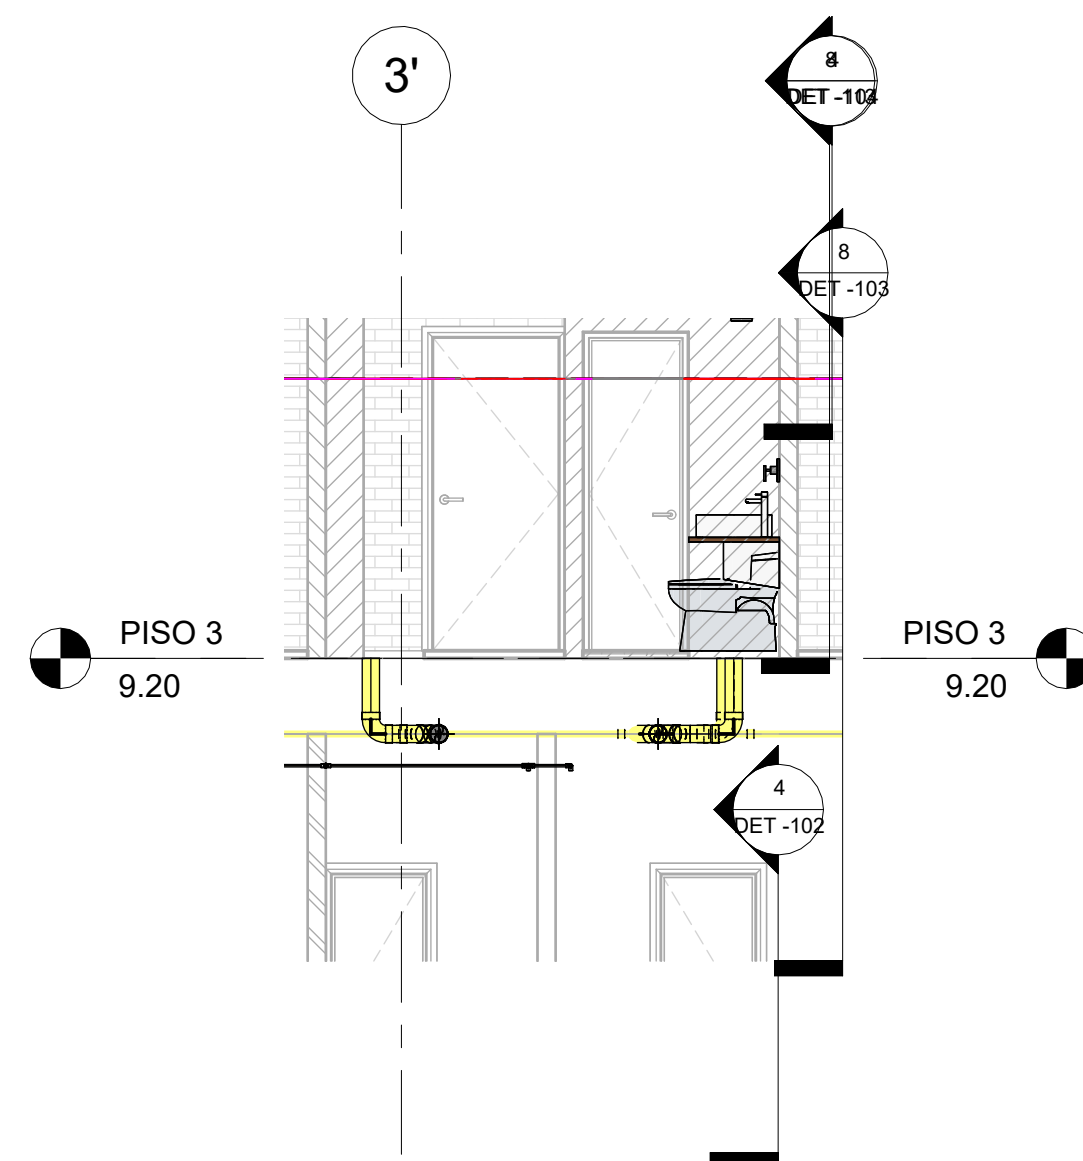


7 SEC_Long_CL_PISO 3 - SANITARIO_2
1 : 50

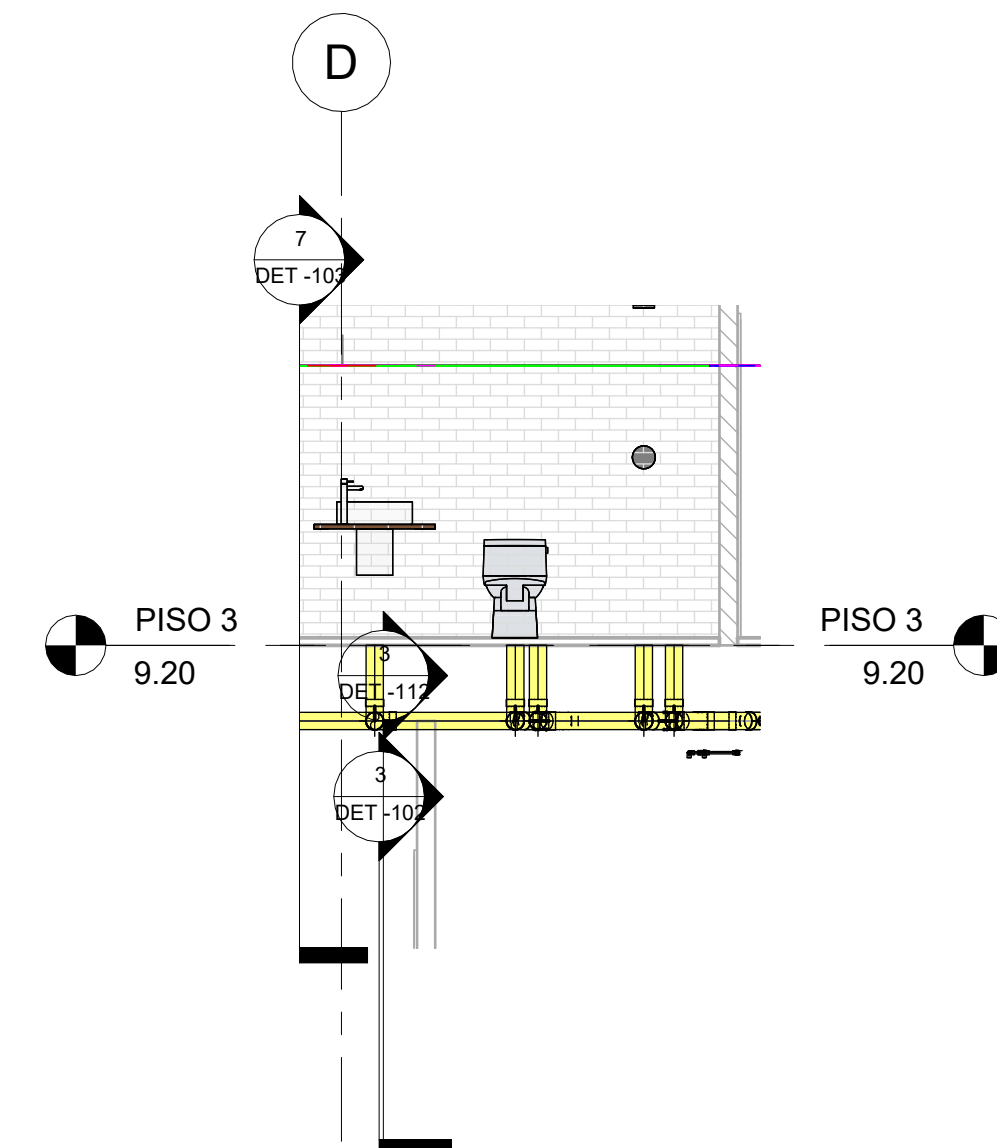


8 SEC_Trans_CL_PISO 3 - SANITARIO_2
1 : 50

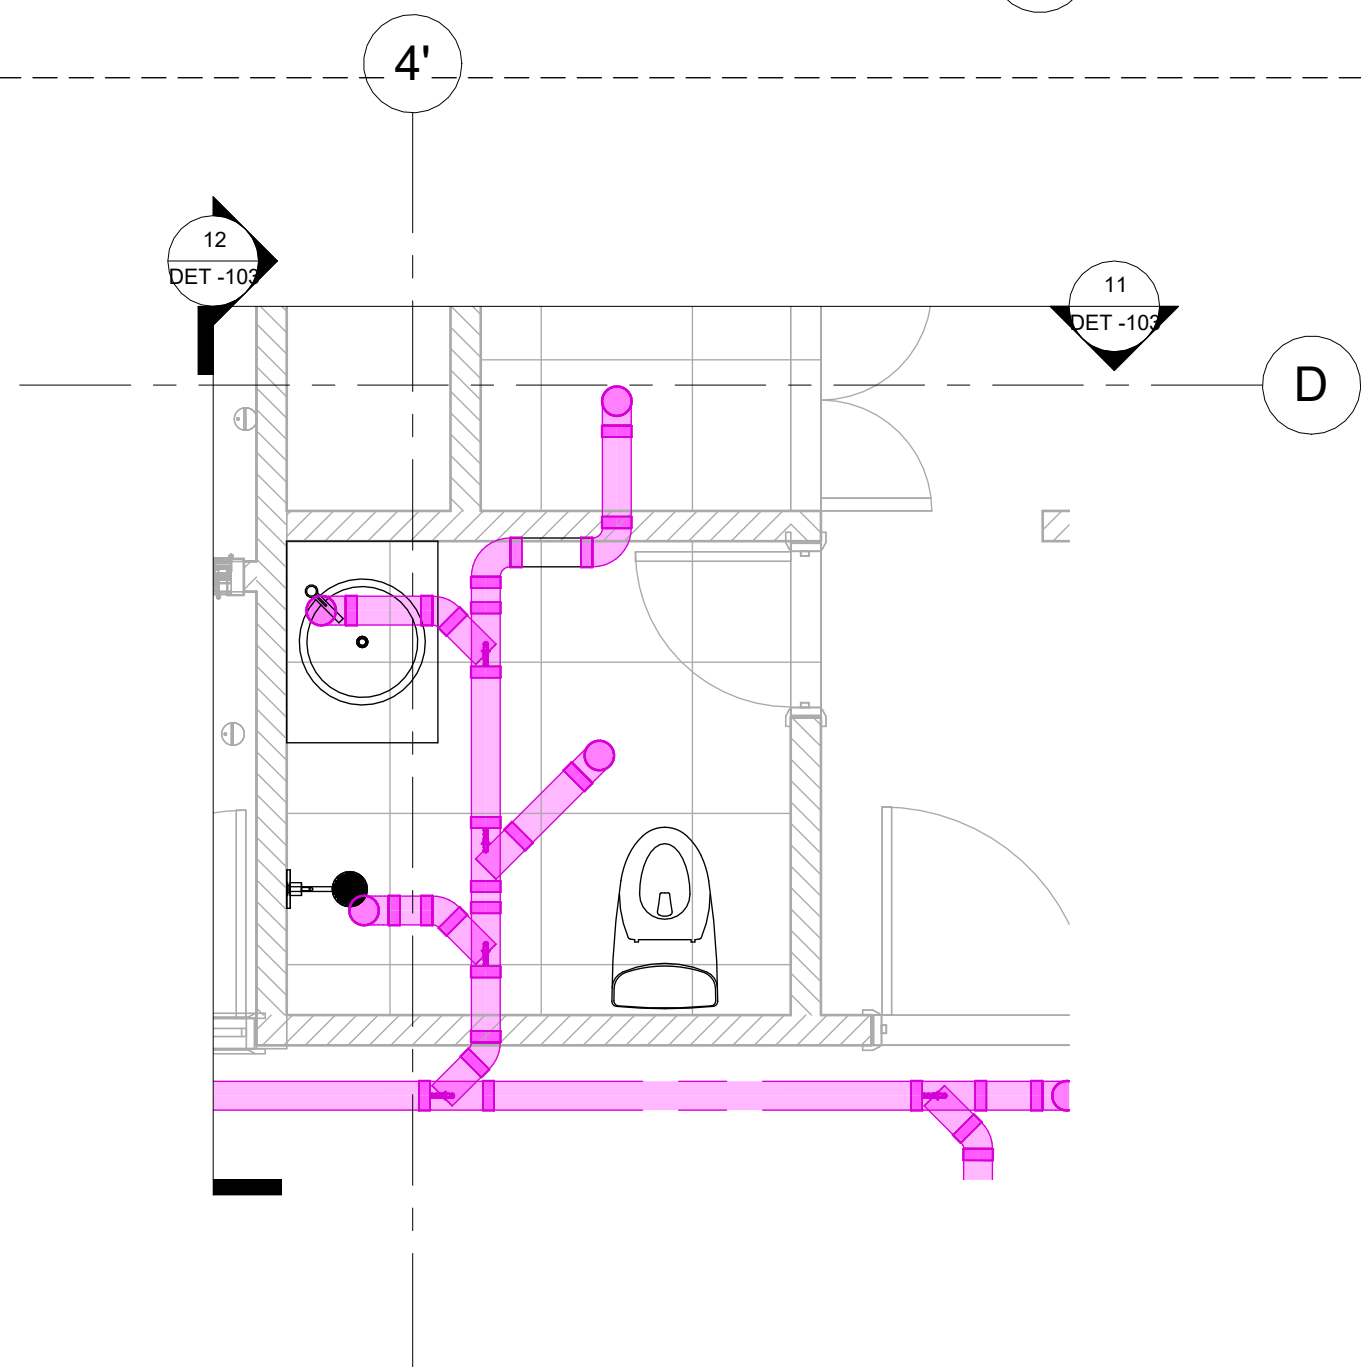


9 CL_PISO 3 - SANITARIO_3
1 : 30

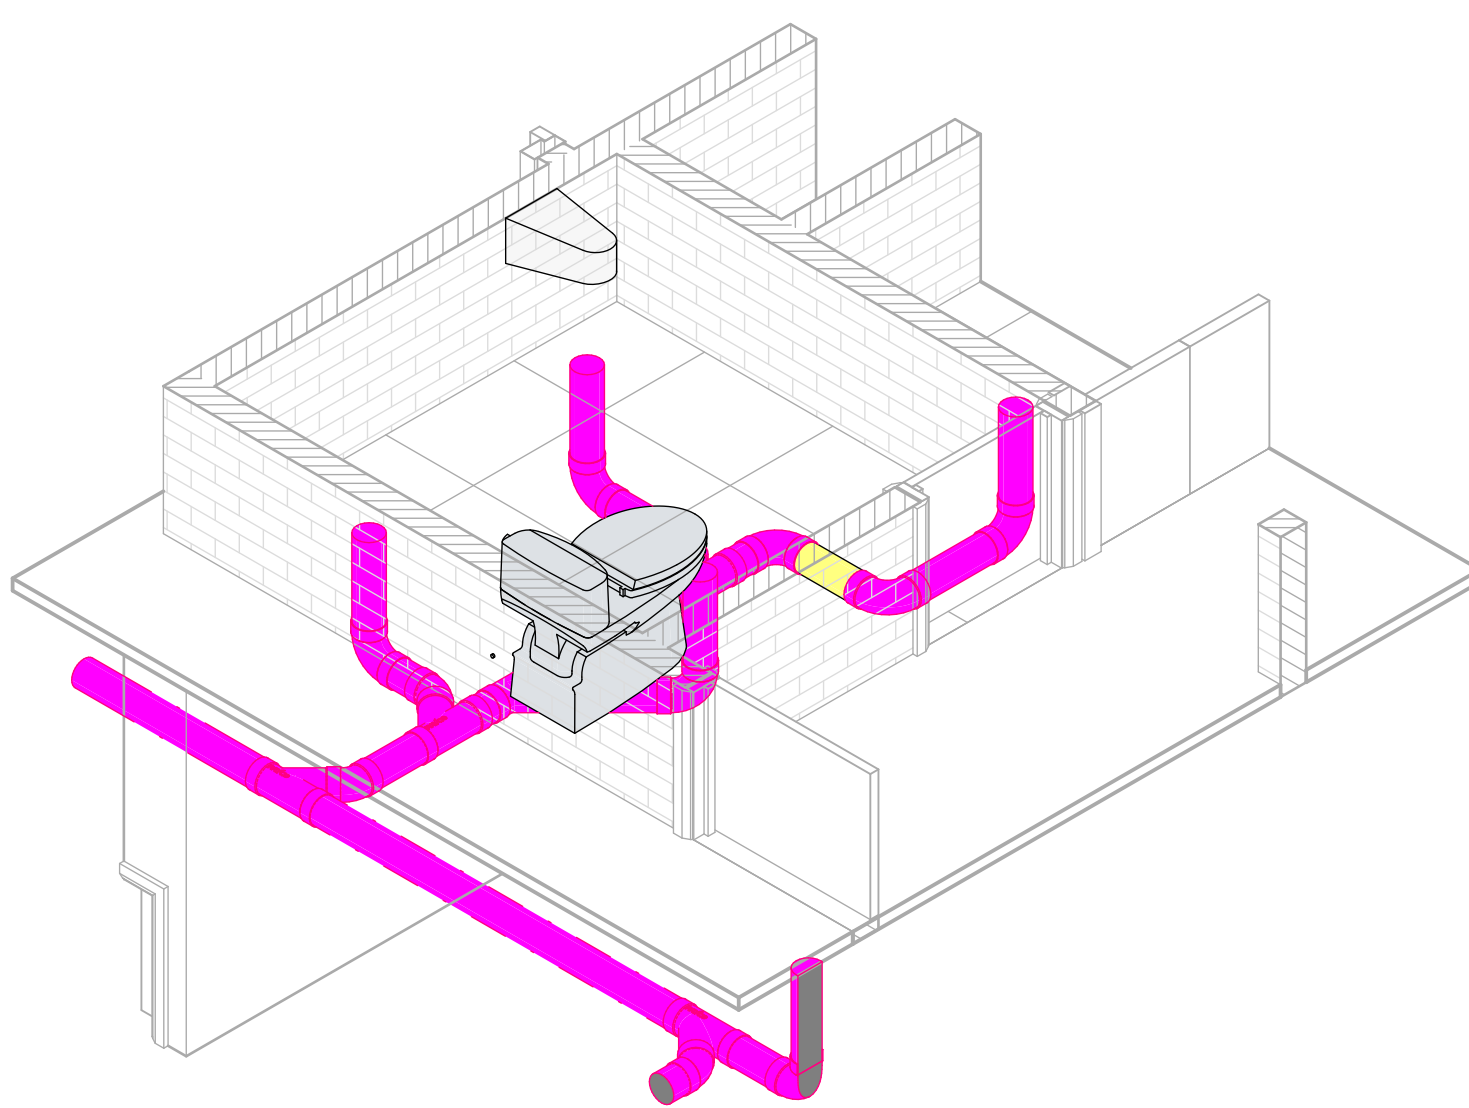

10 3D_CL_PISO 3 - SANITARIO_3

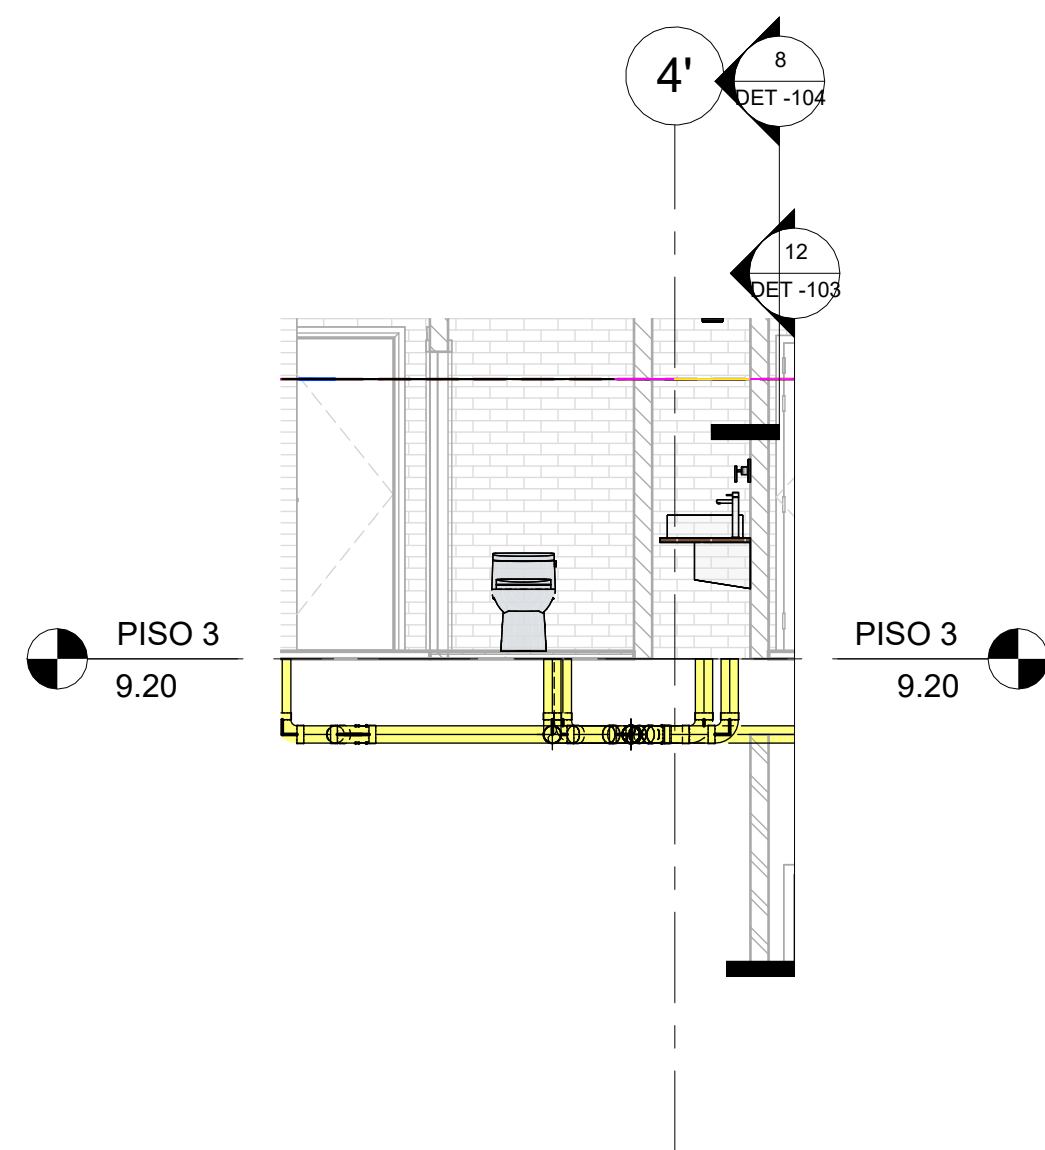

11 SEC_Long_CL_PISO 3 - SANITARIO_3
1 : 50

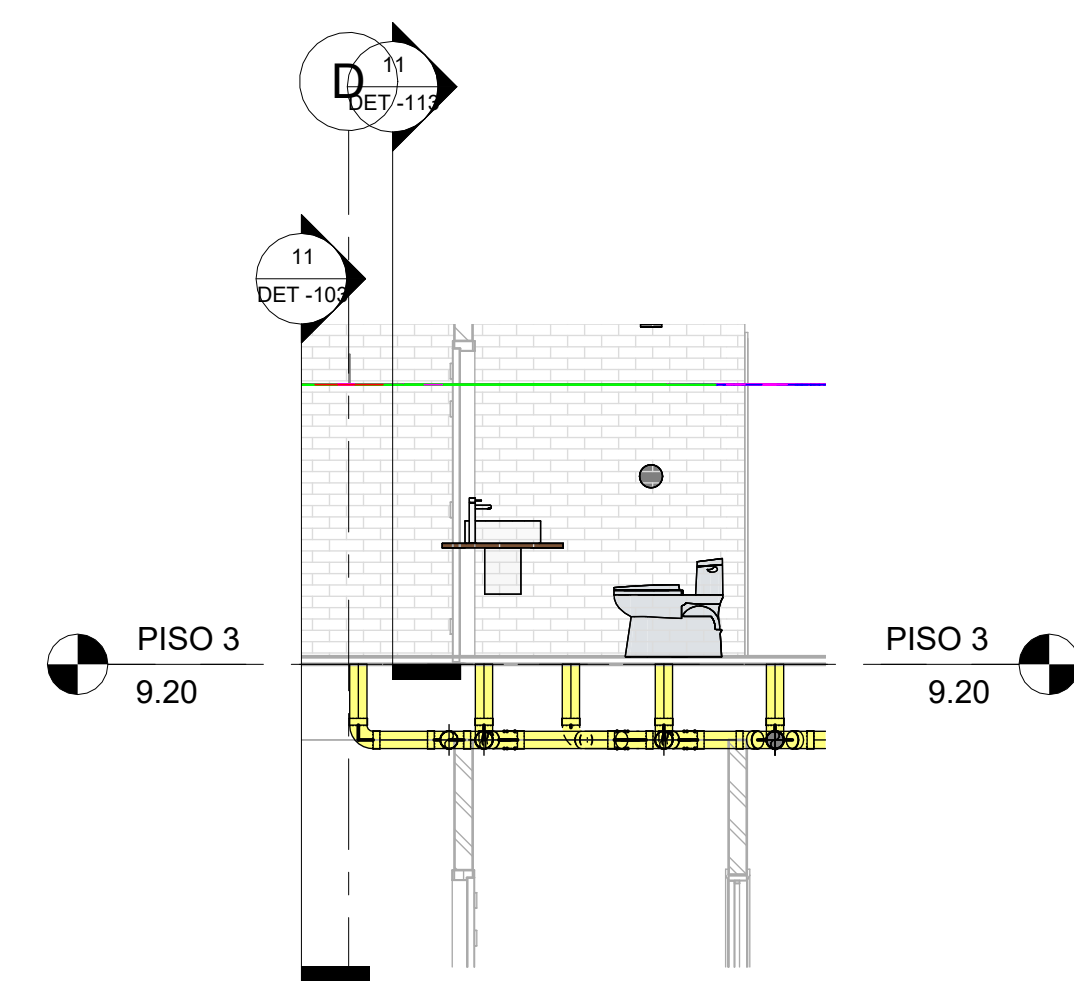

12 SEC_Trans_CL_PISO 3 - SANITARIO_3
1 : 50

GERENCIA DE VIVIENDA, AGUAS Y ALCANTARILLADO UNIDAD DE INGENIERIA			
FLORENTINO LIVING			
DETALLE 3			
PROYECTO	Designer	CALCULO:	Checker
PRESUPUESTO No.		DIBUJO:	Author
		REVISO:	Checker
ESCALA:	Como se indica	APROBO:	Approver
FECHA:	SEPTIEMBRE 2025	ARCHIVO:	

FECHA	REVISIONES	REVISO	APROBO