




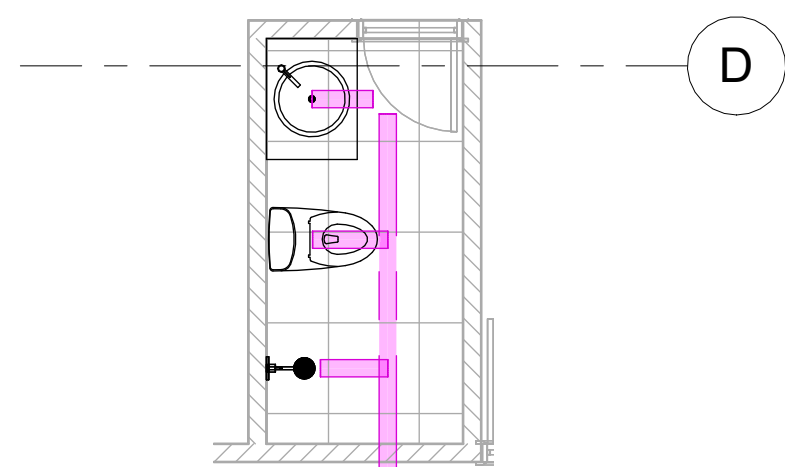


1 CL_PISO 4 - SANITARIO
1 : 50

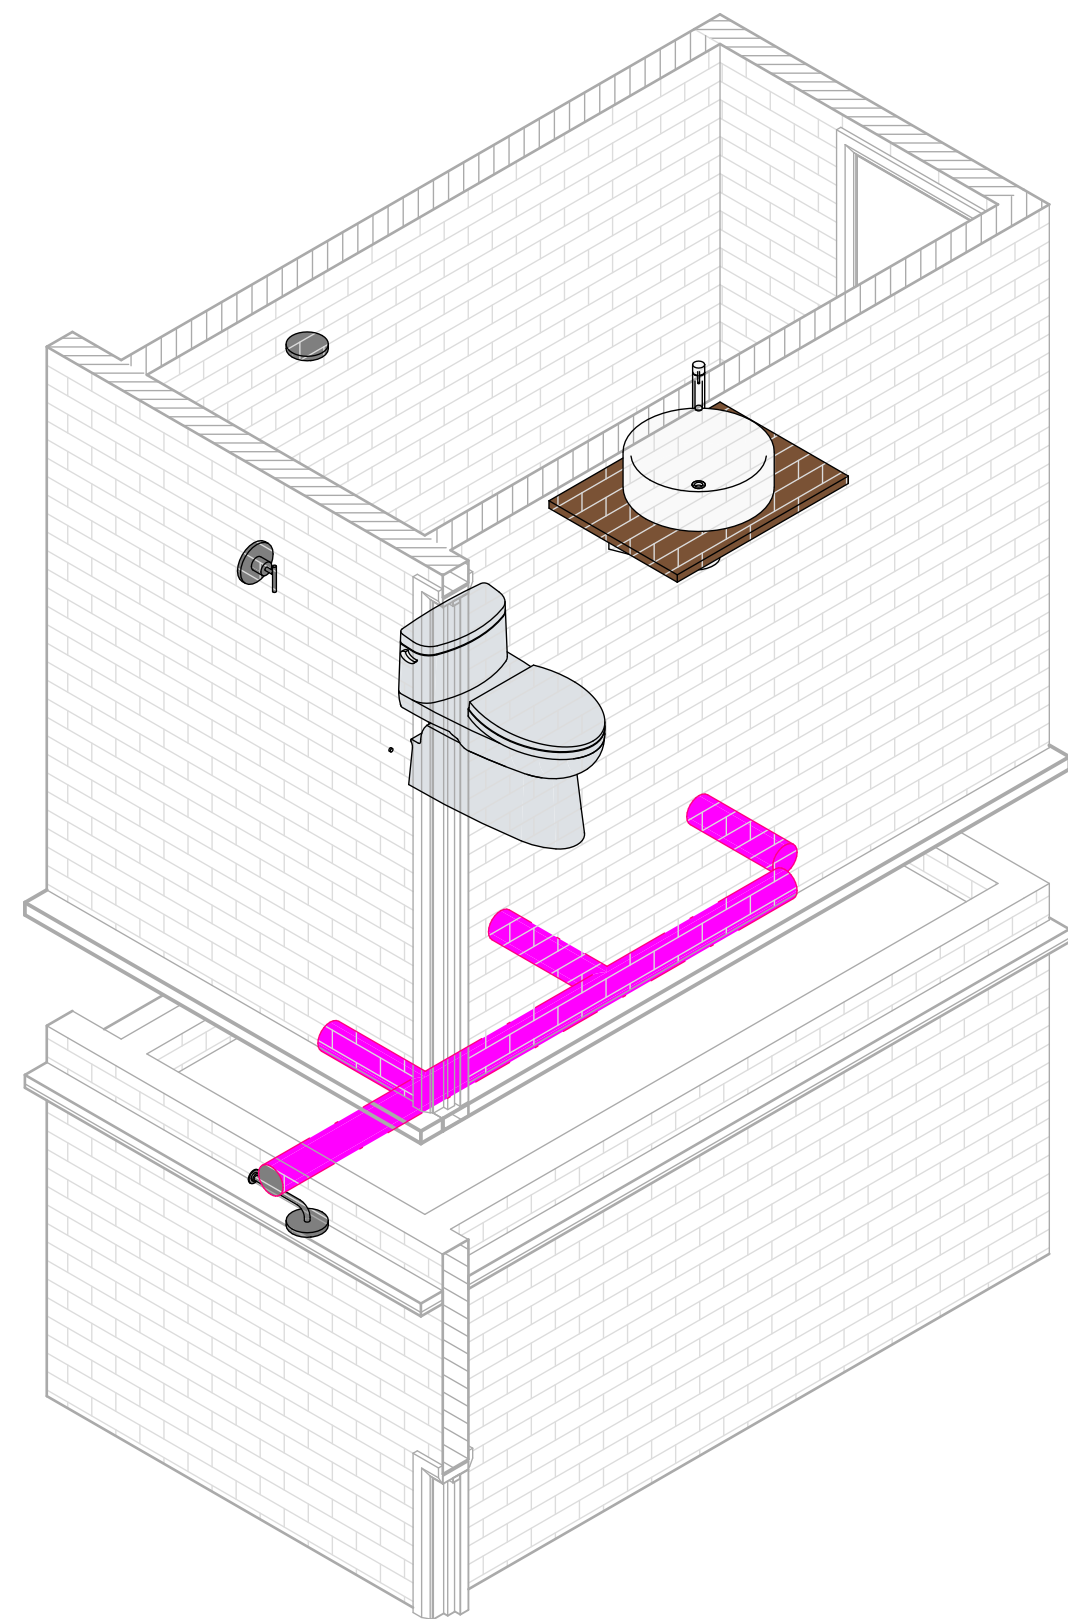


2 3D_CL_PISO 4 - SANITARIO

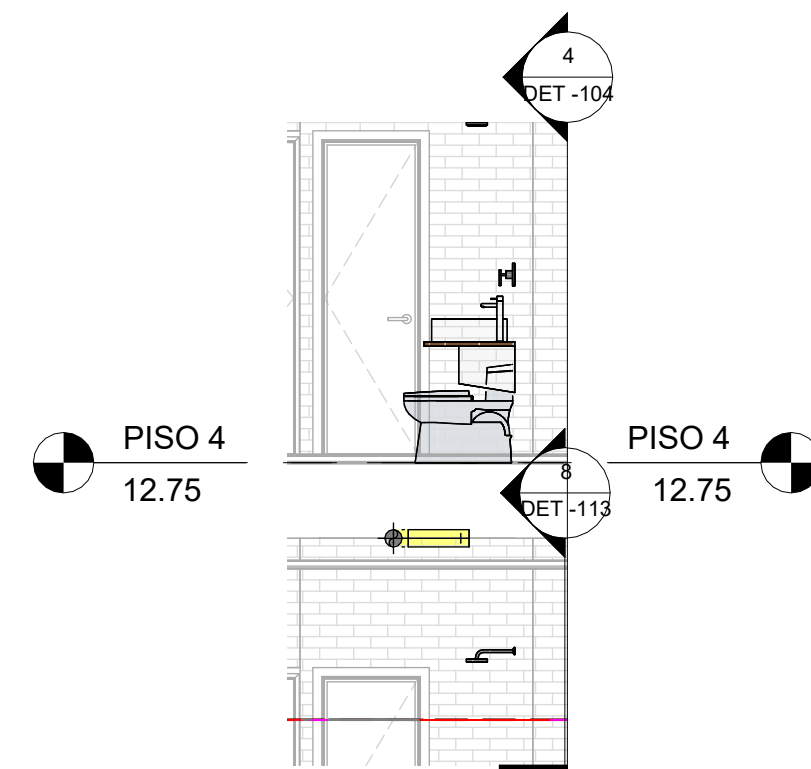


3 SEC_Long_CL_PISO 4 - SANITARIO
1 : 50

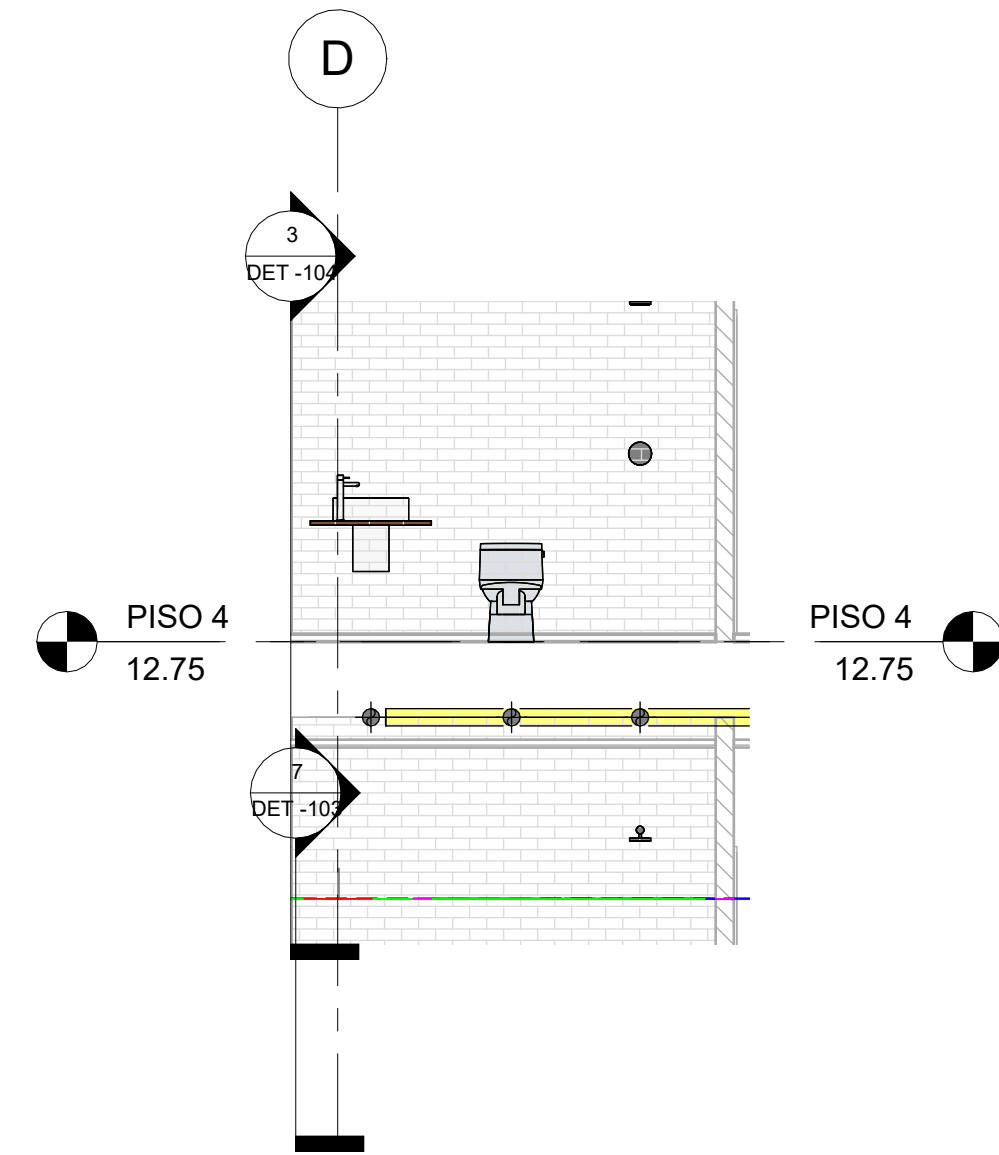


4 SEC_Trans_CL_PISO 4 - SANITARIO
1 : 50

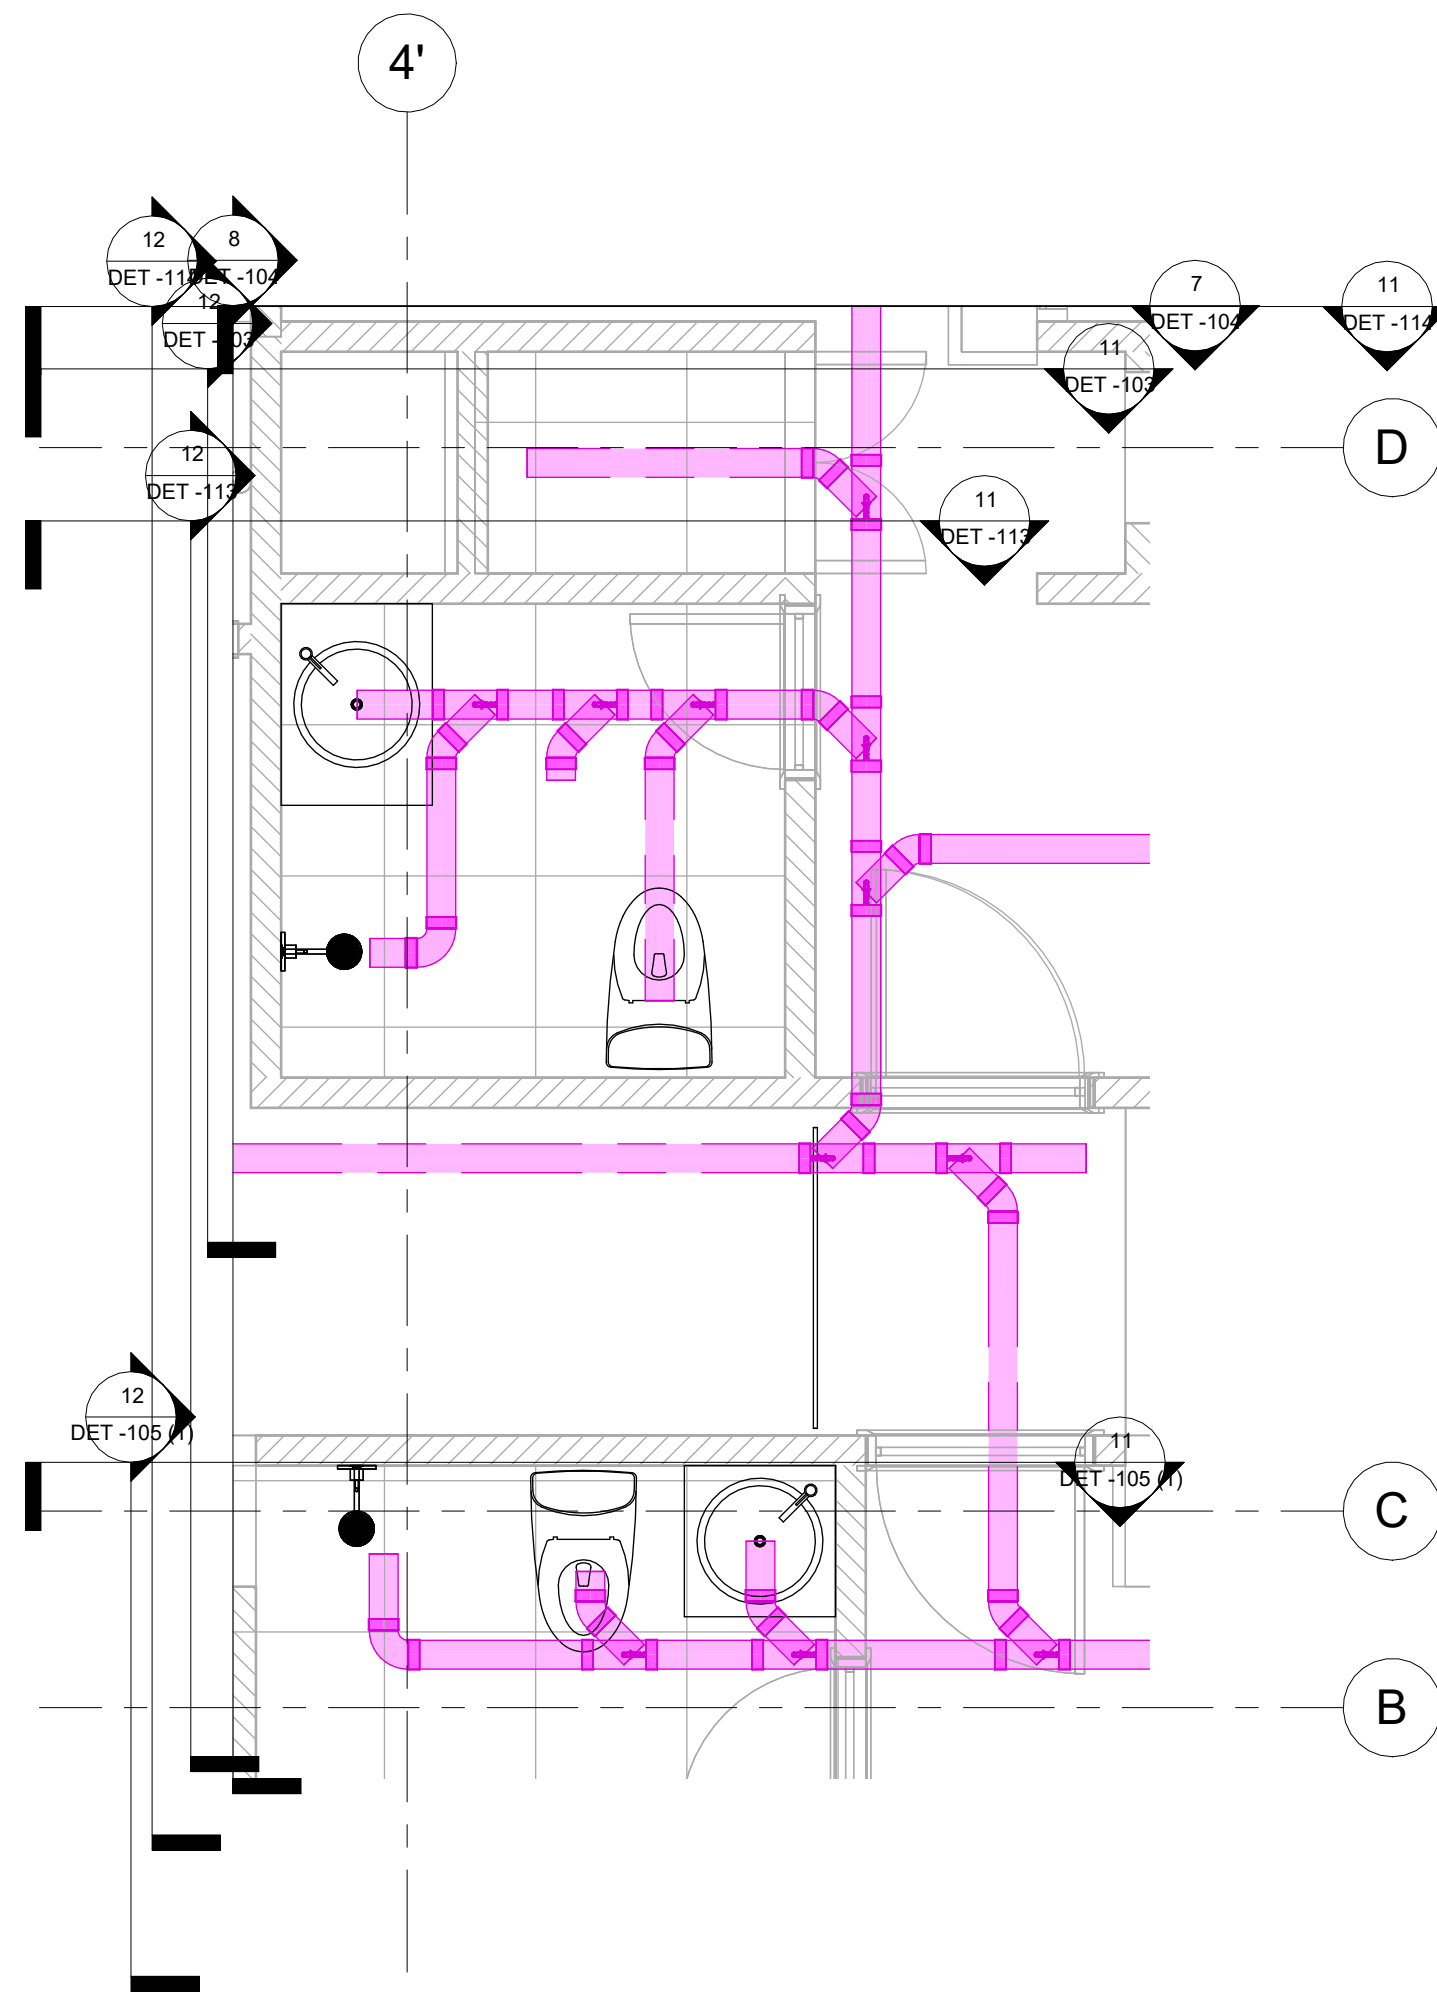


5 CL_PISO 4 - SANITARIO_2
1 : 30

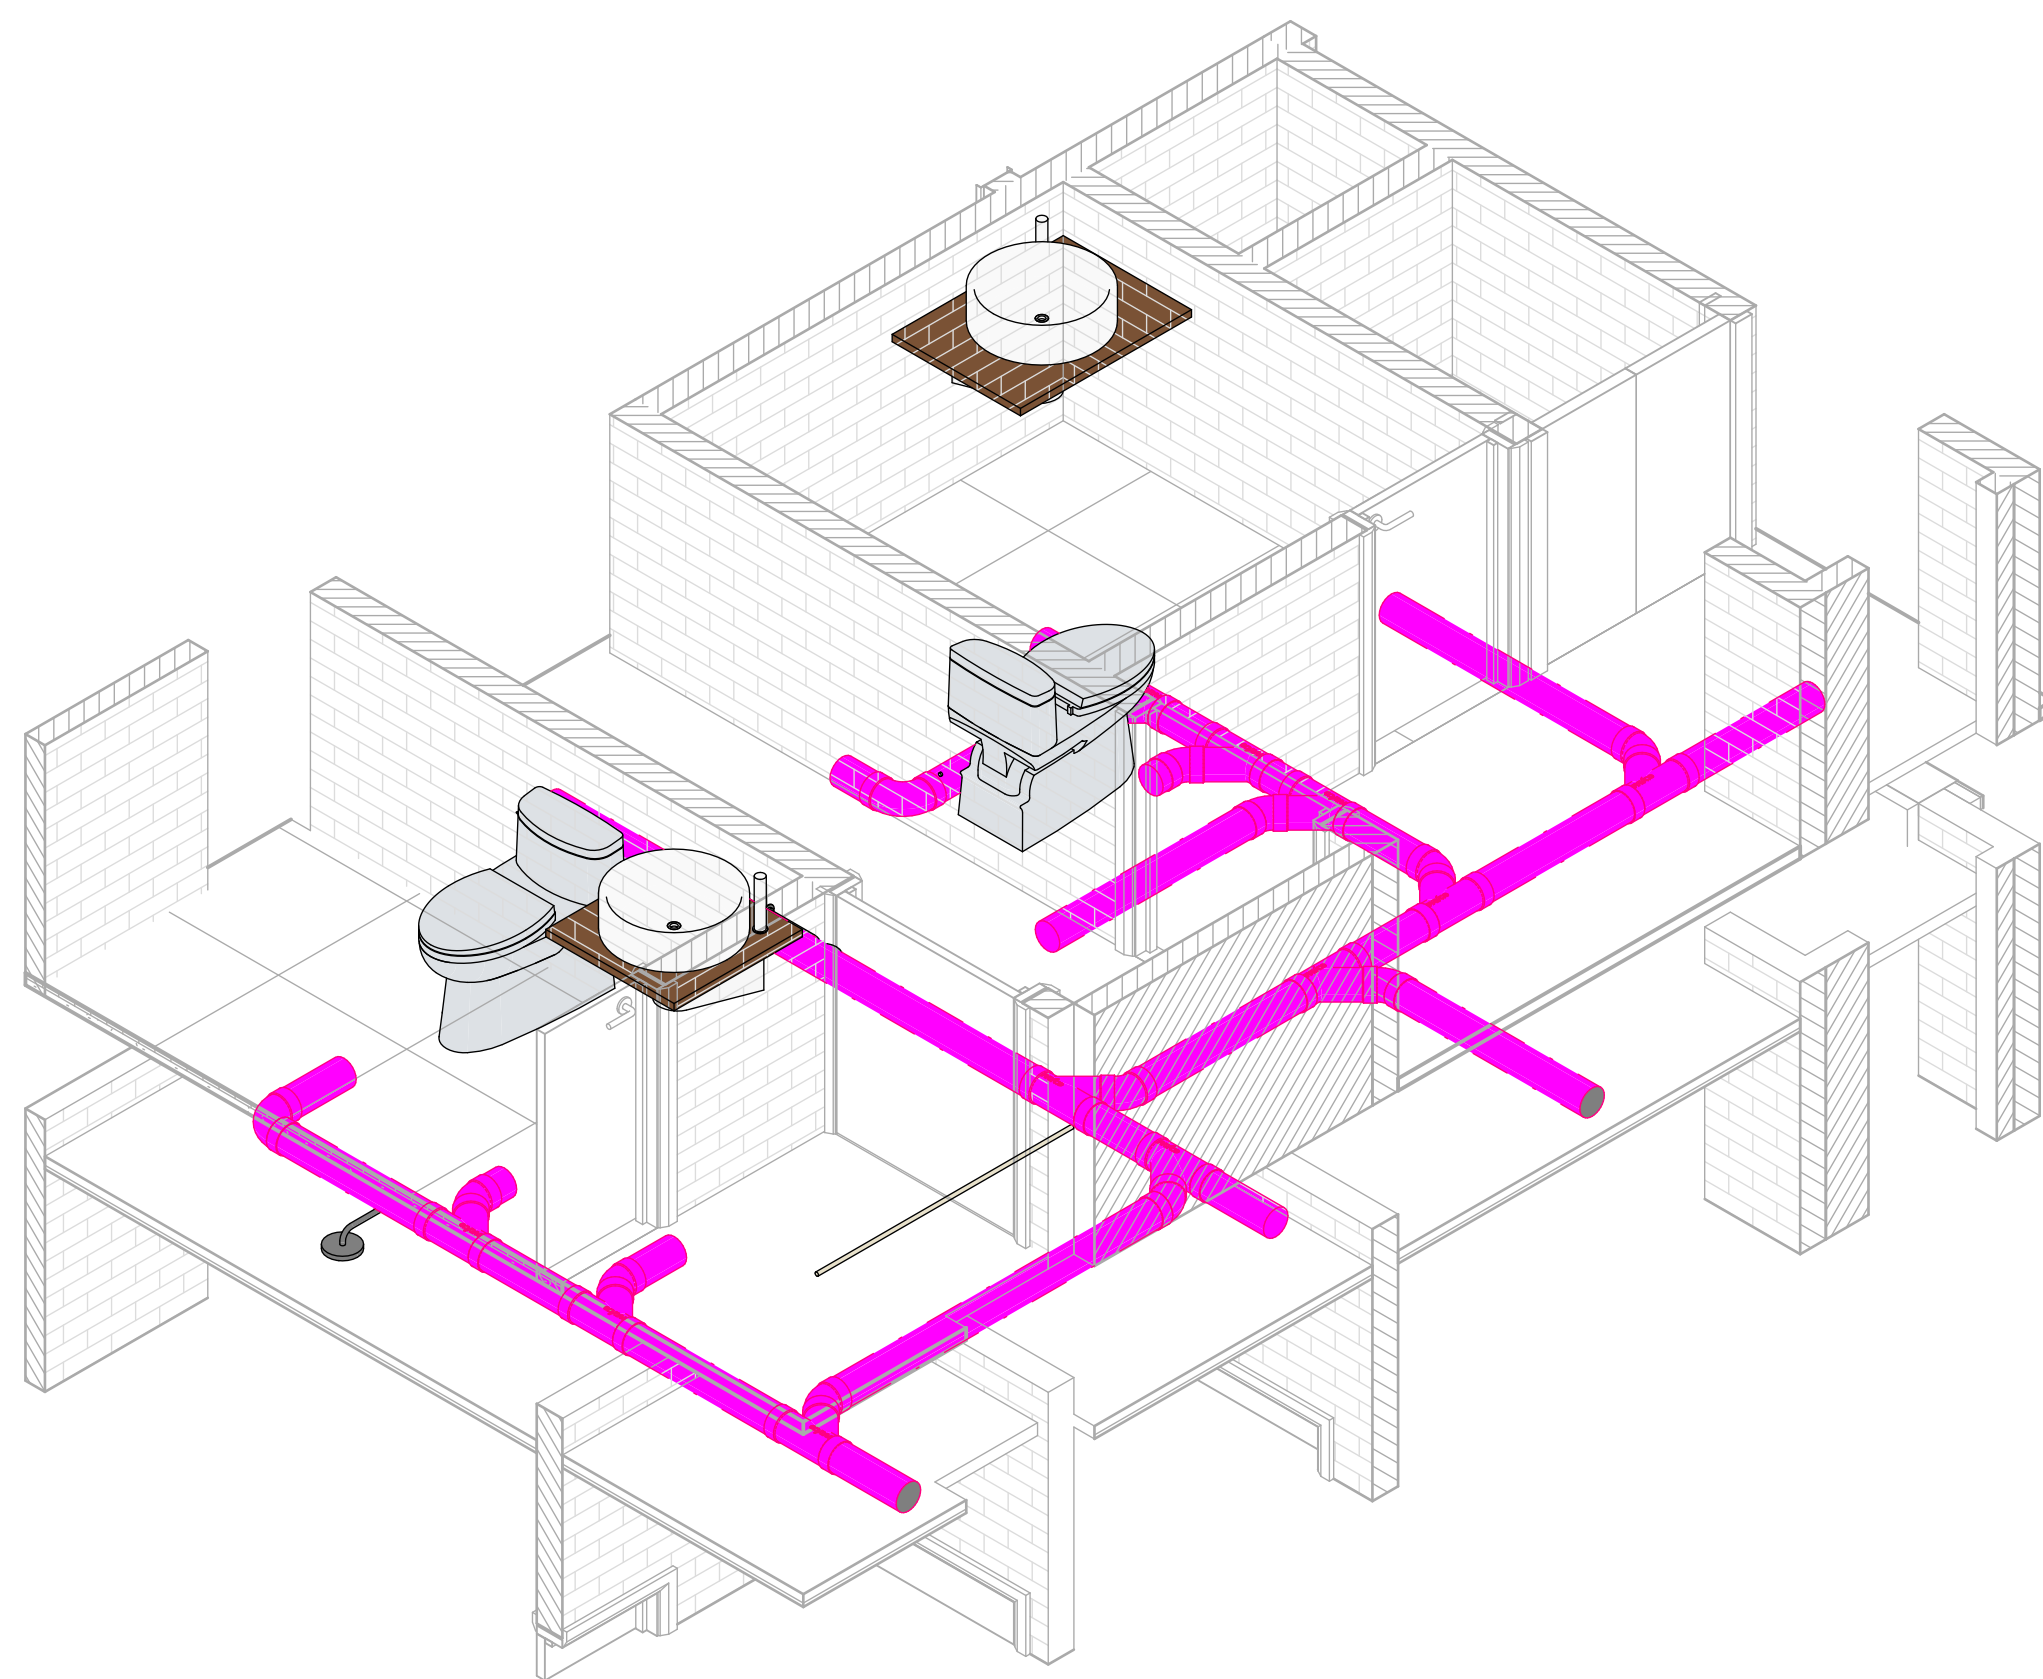

6 3D_CL_PISO 4 - SANITARIO_2

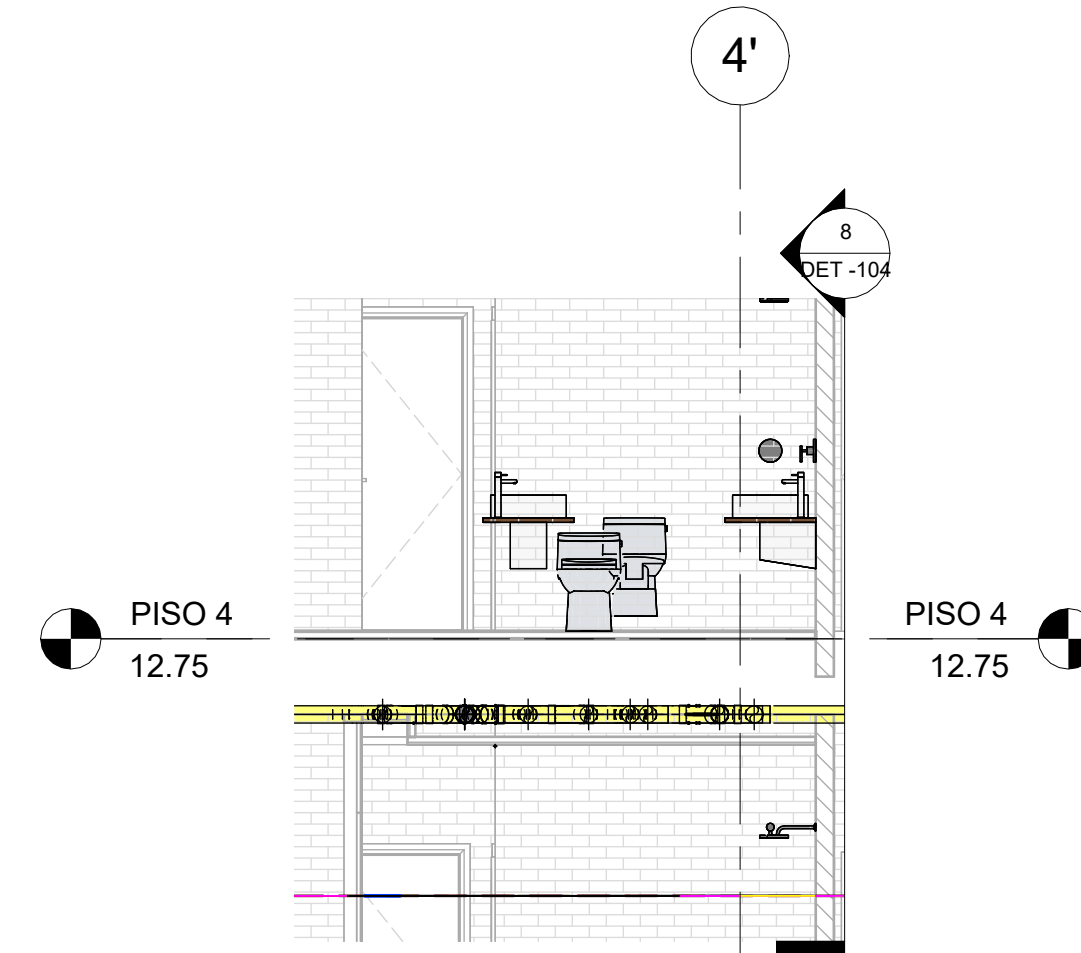

7 SEC_Long_CL_PISO 4 - SANITARIO_2
1 : 50

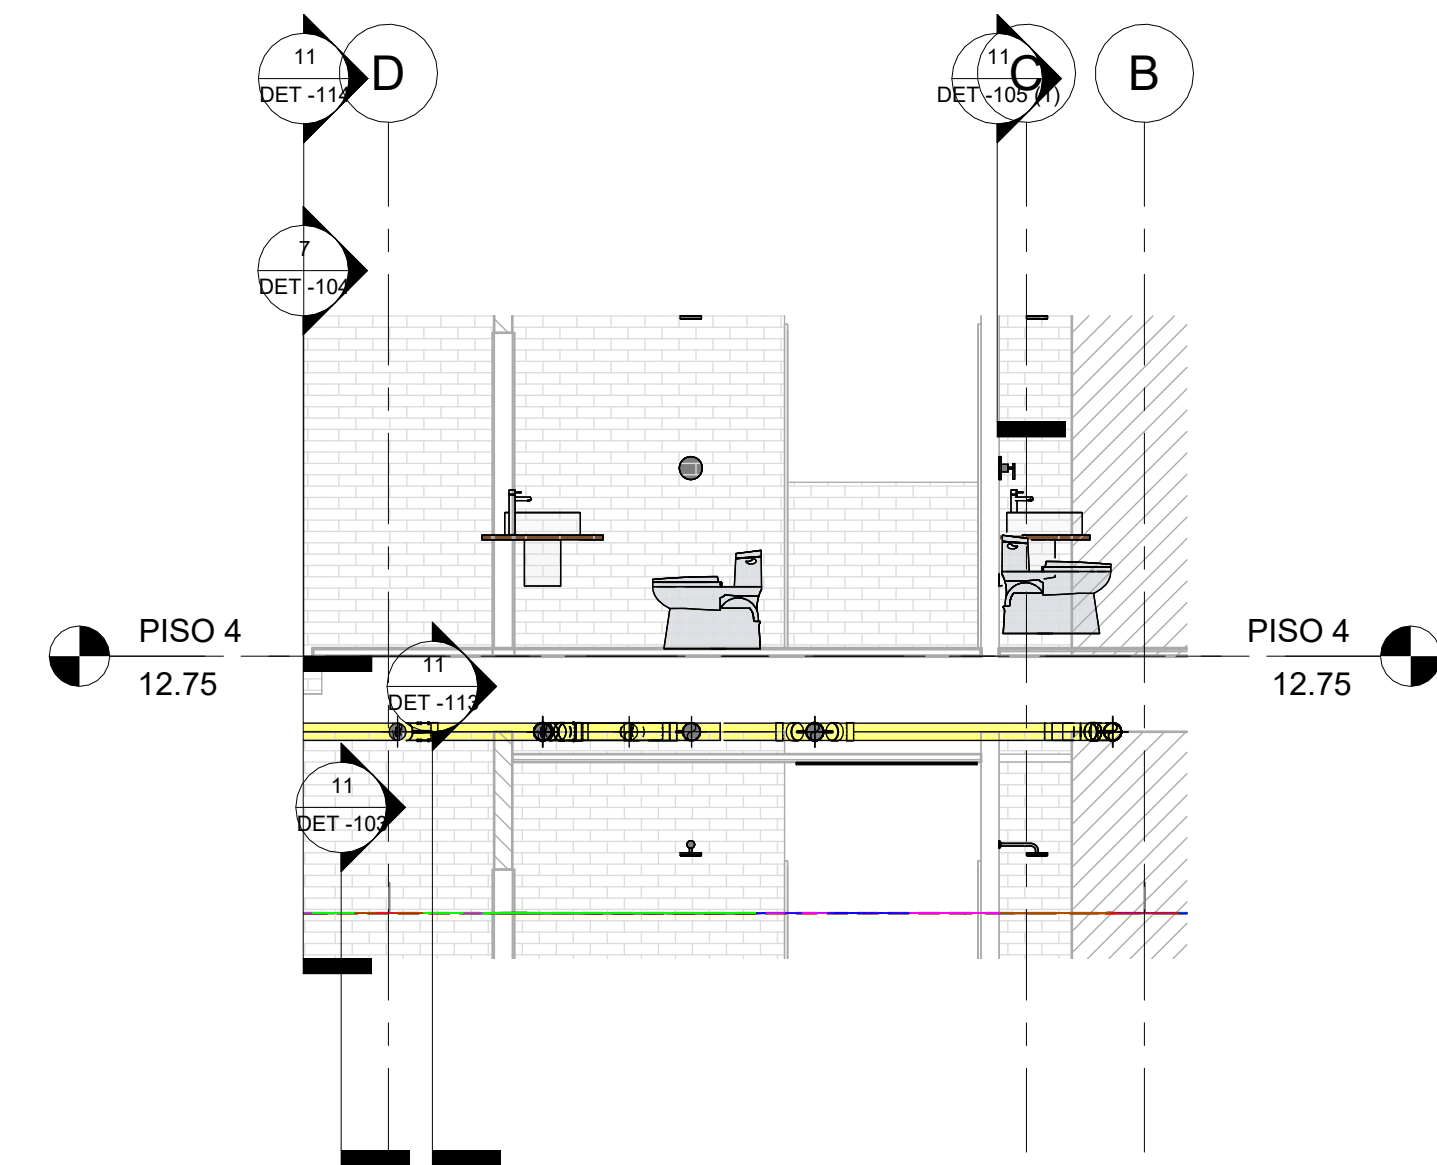

8 SEC_Trans_CL_PISO 4 - SANITARIO_2
1 : 50

EMCALI GERENCIA DE UEN ACUEDUCTO Y ALCANTARILLADO UNIDAD DE INGENIERIA	
FLORENTINO LIVING	
DETALLE 4	
PROYECTO Designer	CALCULO: Checker
PRESUPUESTO No.	DIBUJO: Author
REVISO: Checker	APROBO: Approver
FECHA: SEPTIEMBRE 2025	ARCHIVO: