




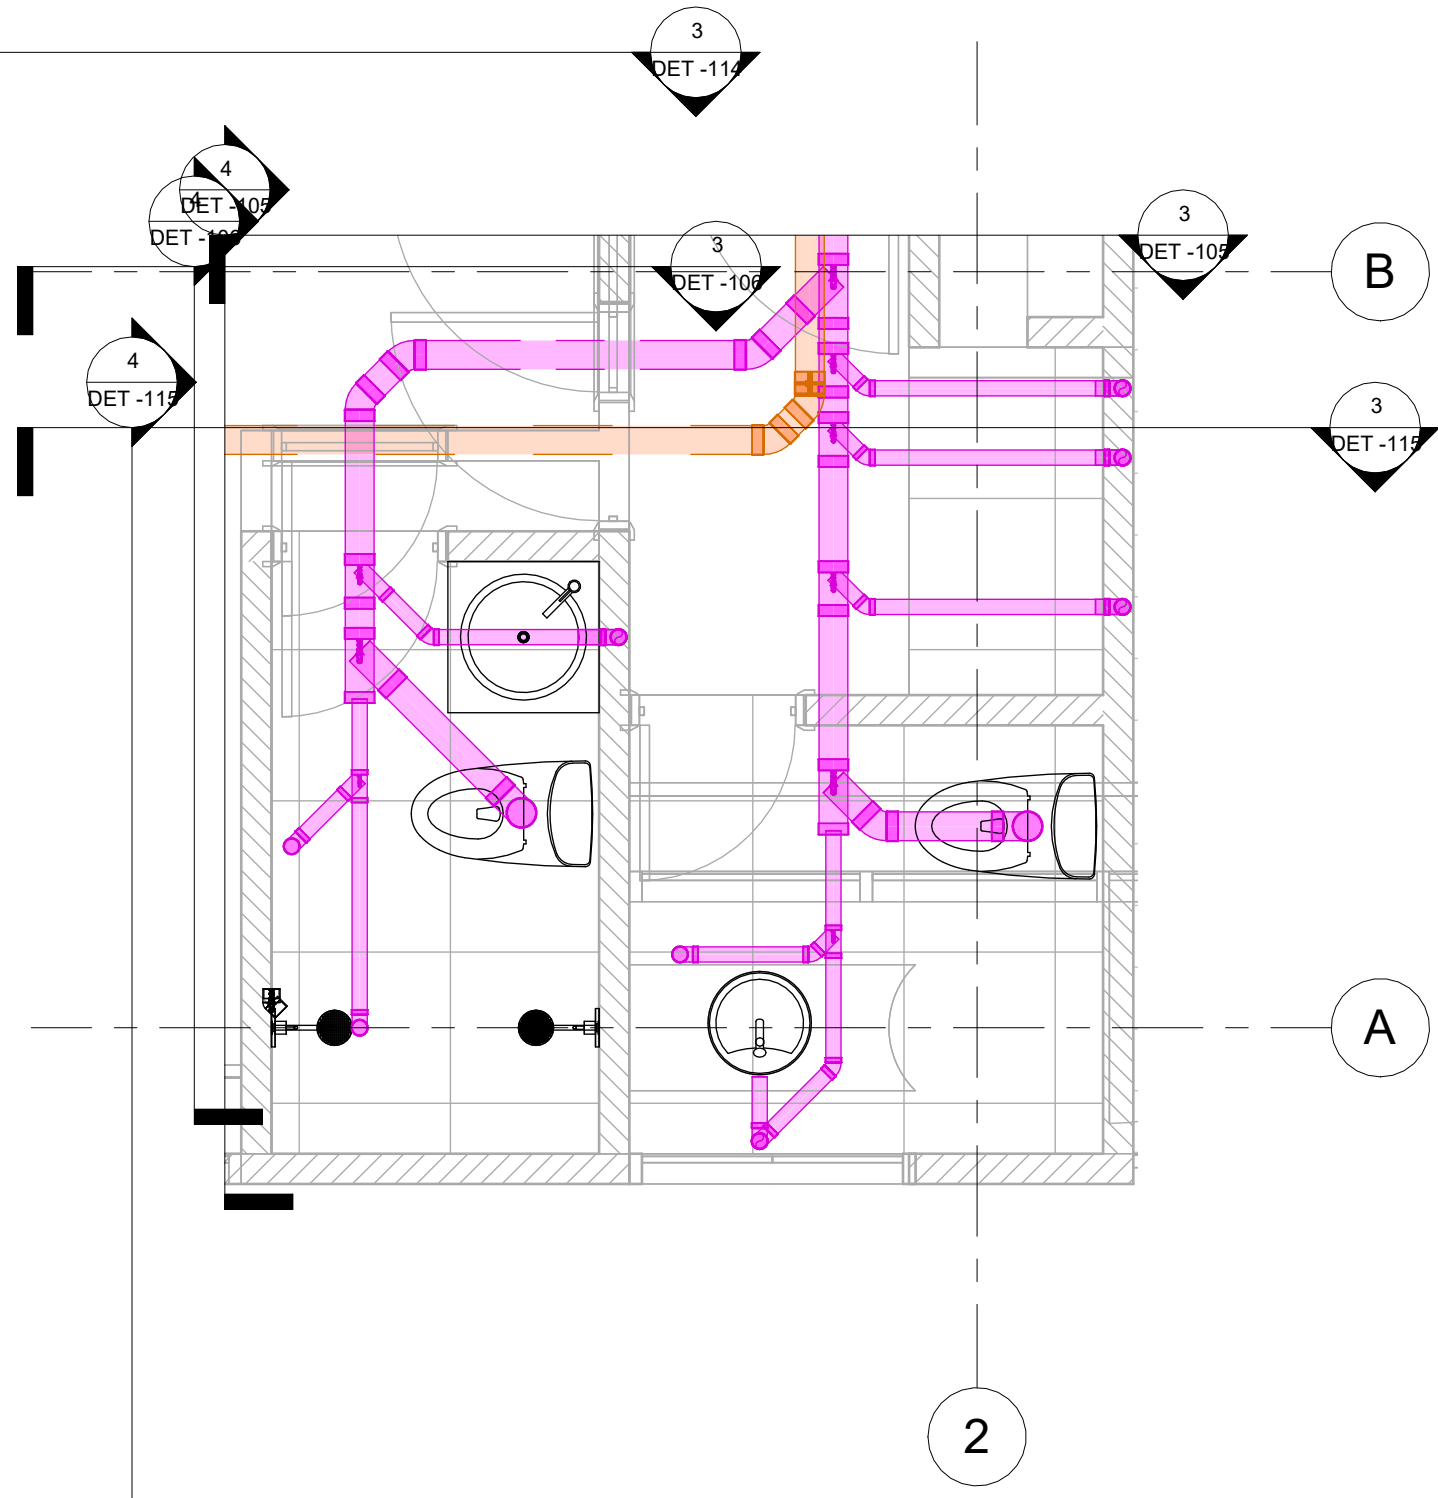


1 CL_PISO 5 - SANITARIO
1 : 30

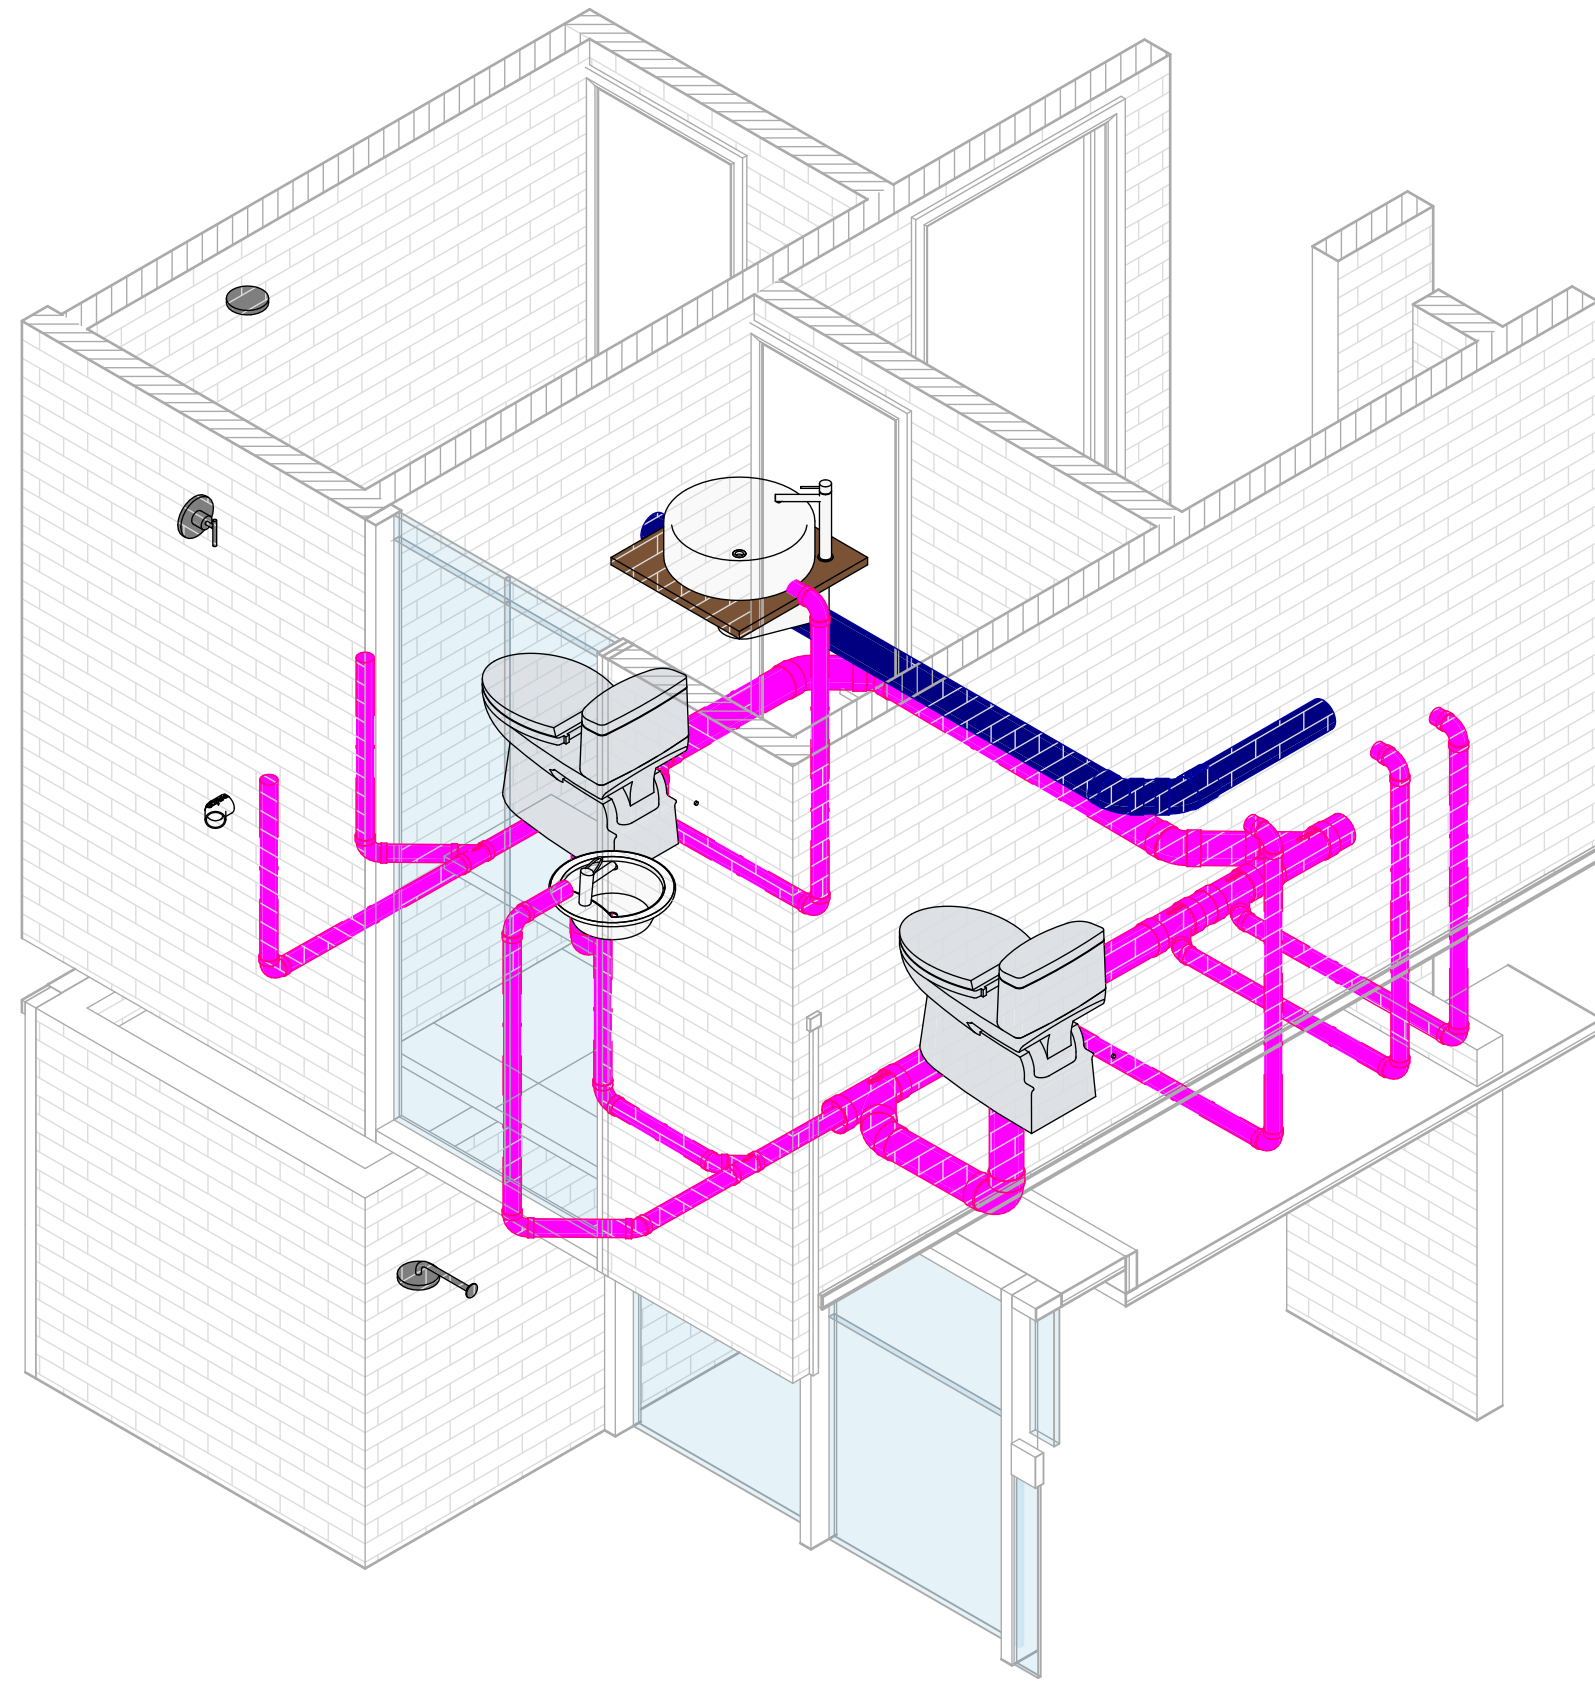


2 3D_CL_PISO 5 - SANITARIO

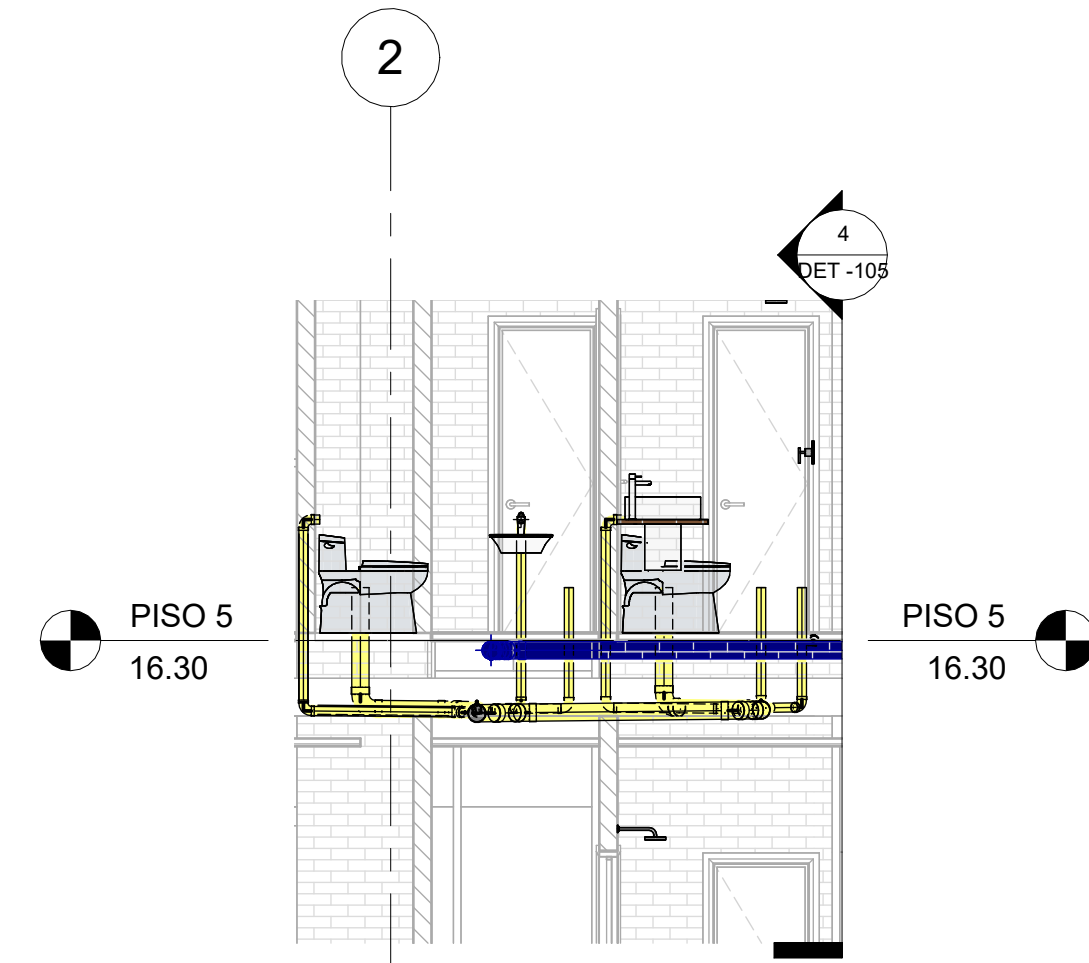


3 SEC_Long_CL_PISO 5 - SANITARIO
1 : 50

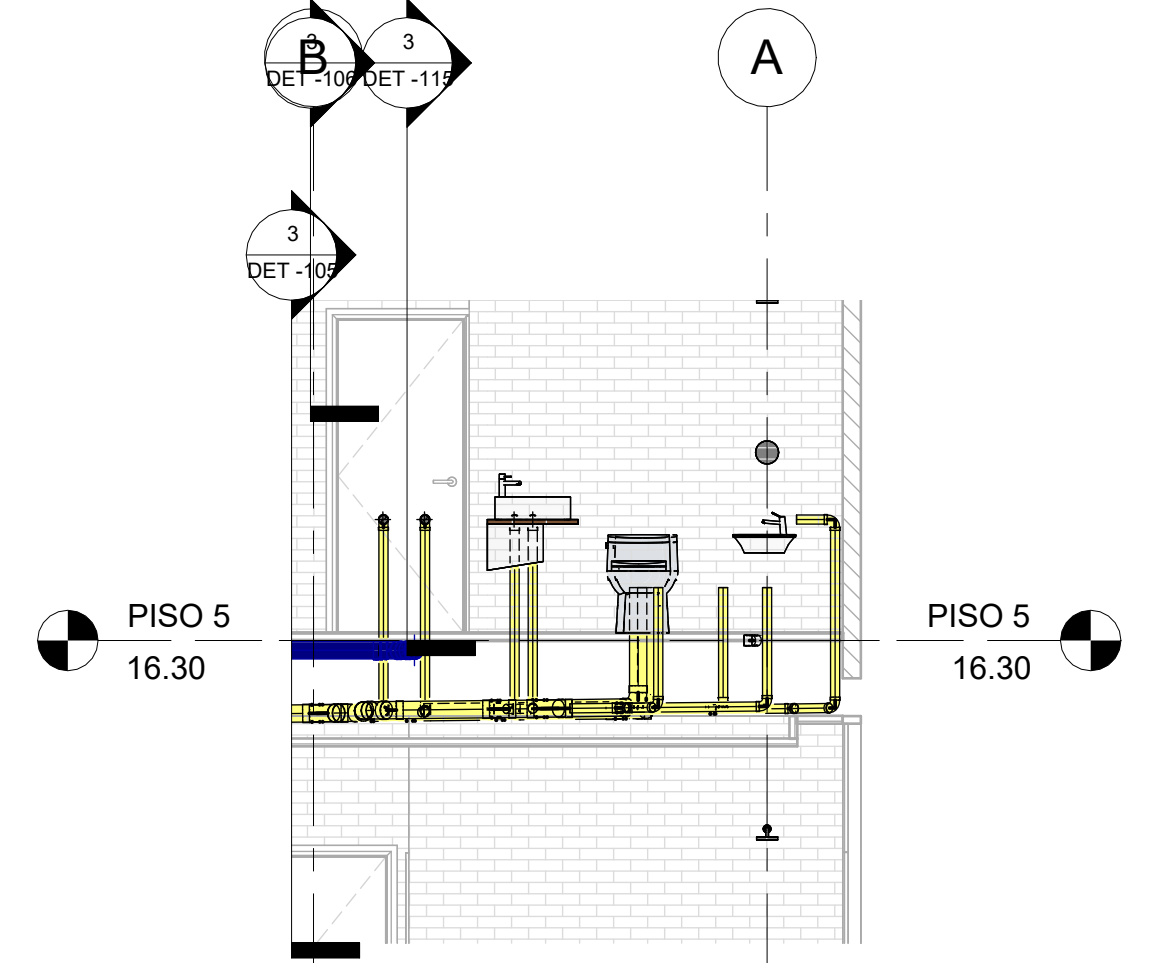


4 SEC_Trans_CL_PISO 5 - SANITARIO
1 : 50

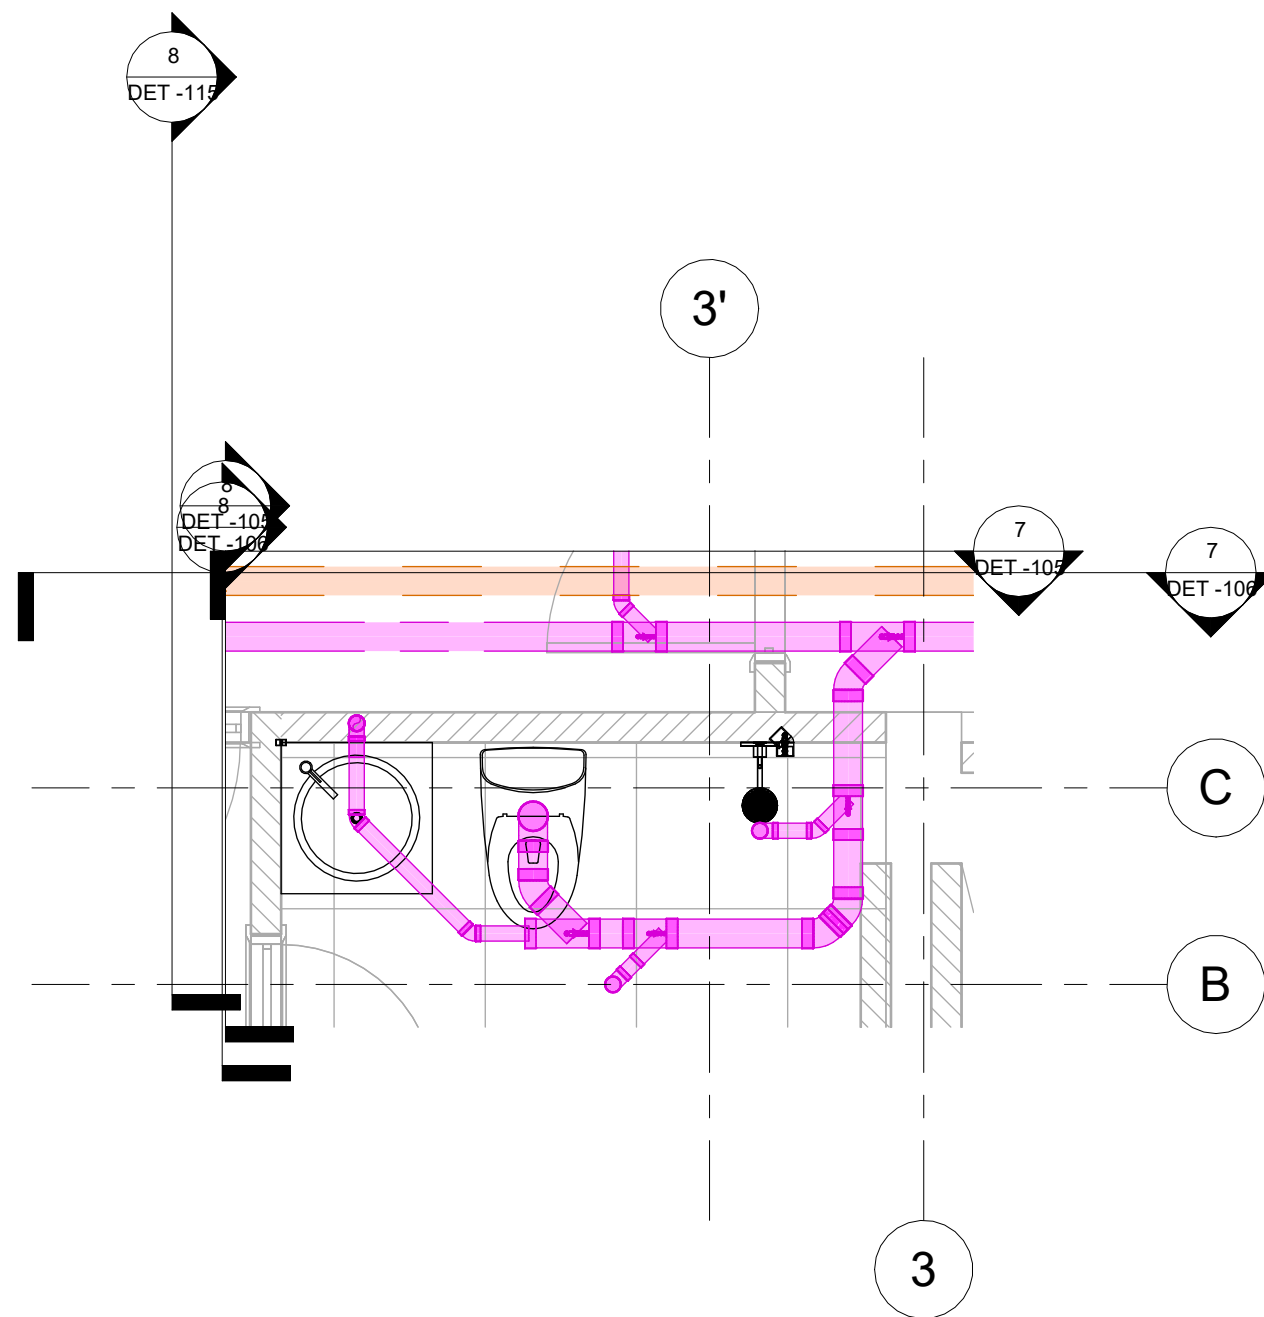


5 CL_PISO 5 - SANITARIO_2
1 : 30

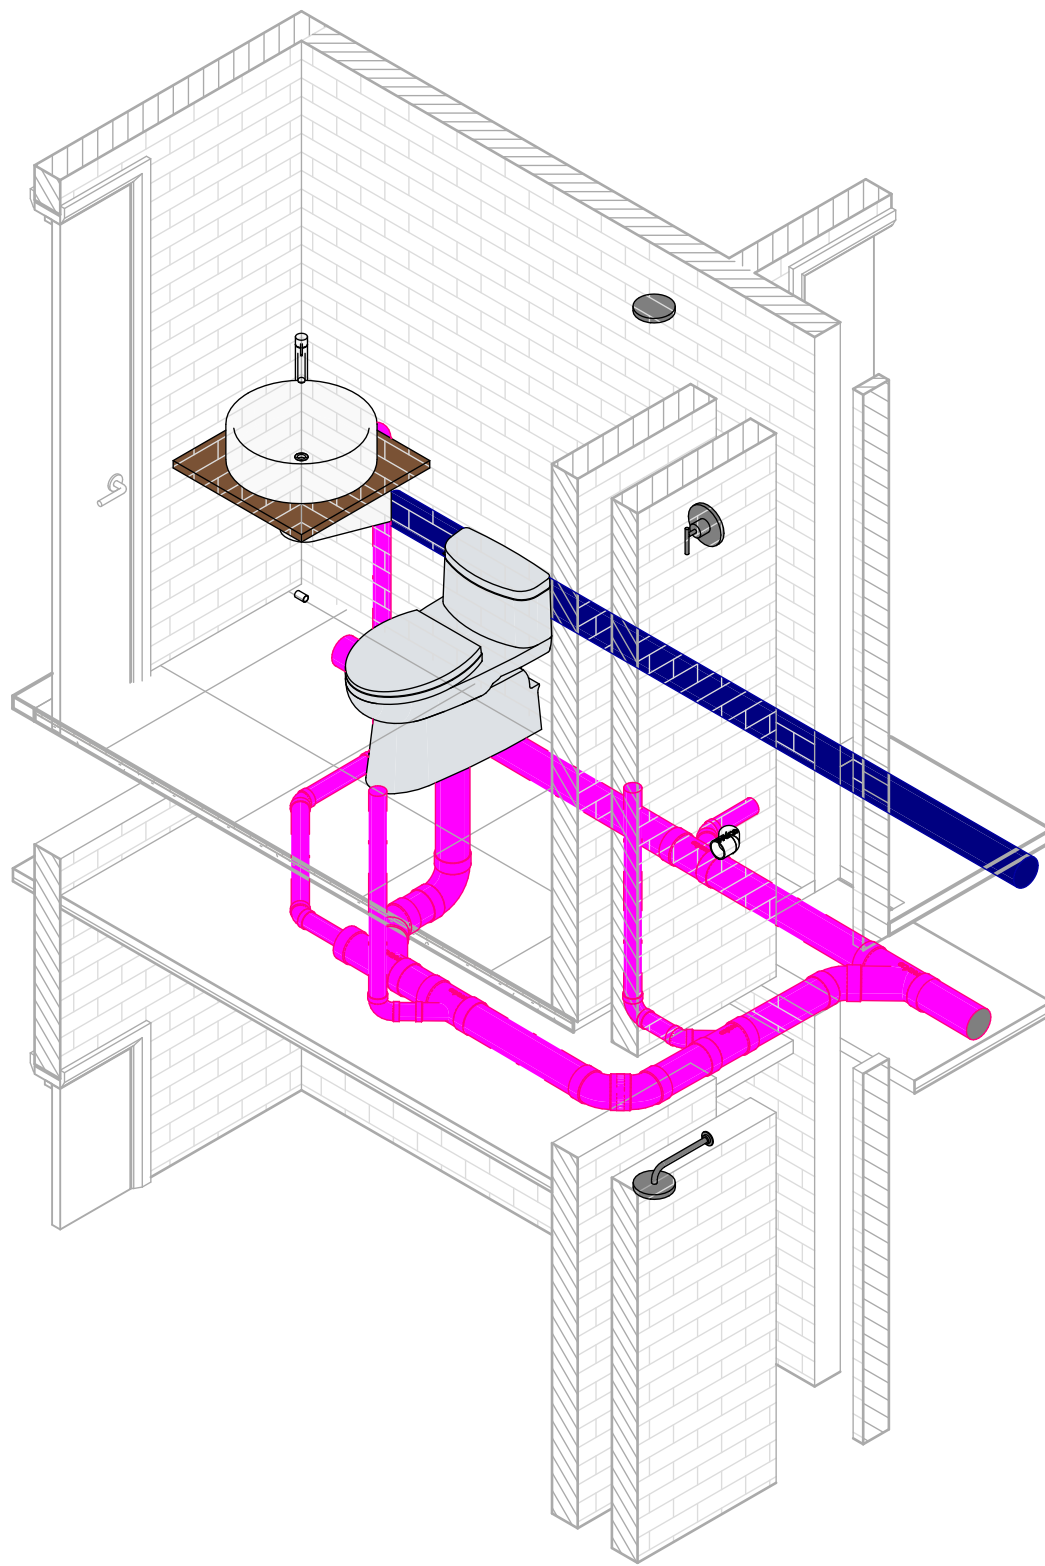

6 3D_CL_PISO 5 - SANITARIO_2

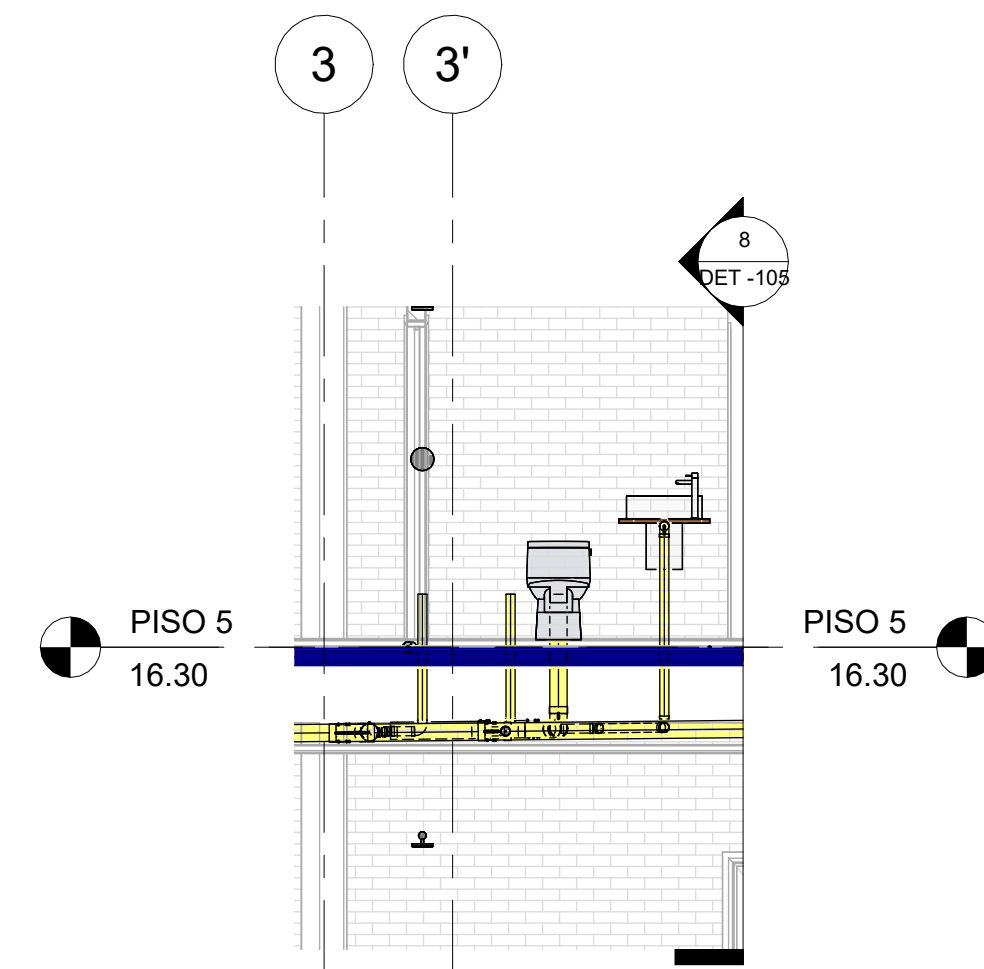

7 SEC_Long_CL_PISO 5 - SANITARIO_2
1 : 50

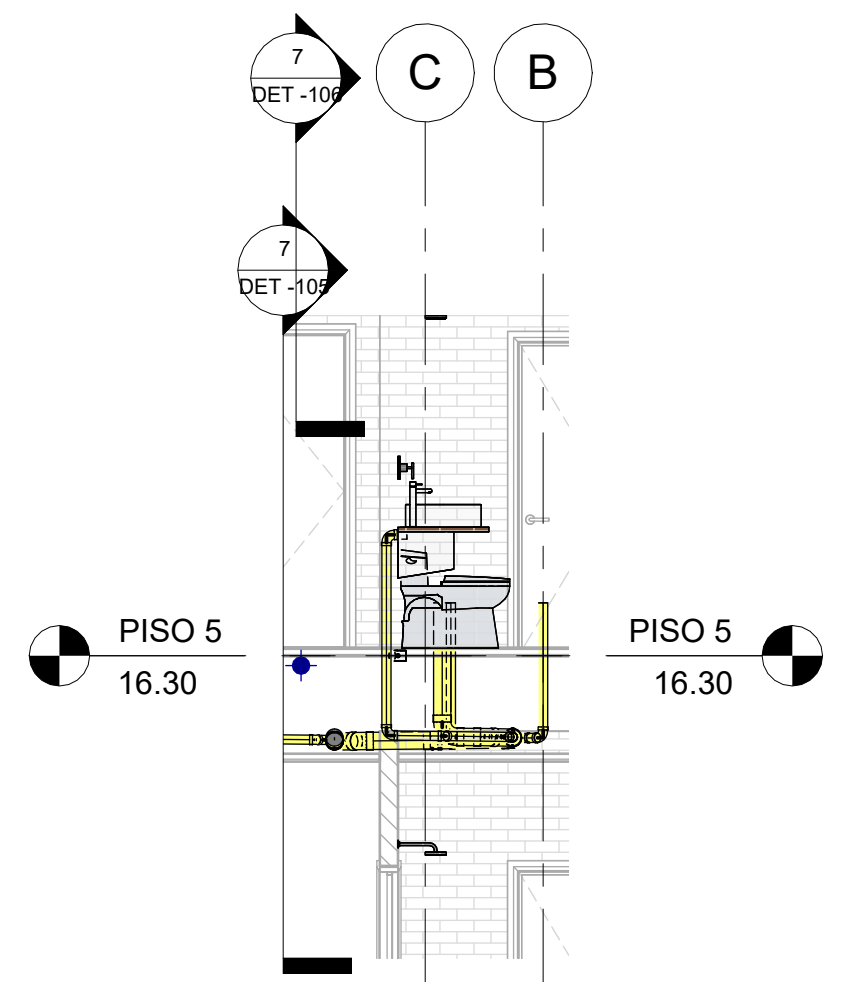

8 SEC_Trans_CL_PISO 5 - SANITARIO_2
1 : 50

EMCALI GERENCIA DE UEN ACUEDUCTO Y ALCANTARILLADO UNIDAD DE INGENIERIA			
FLORENTINO LIVING			
DETALLE 5			
PROYECTO Designer		CALCULO: Checker	
PRESUPUESTO No.		DIBUJO: Author	
		REVISO: Checker	
ESCALA: Como se indica		APROBO: Approver	
FECHA:		ARCHIVO: SEPTIEMBRE 2025	

FECHA	REVISIONES	REVISO	APROBO