



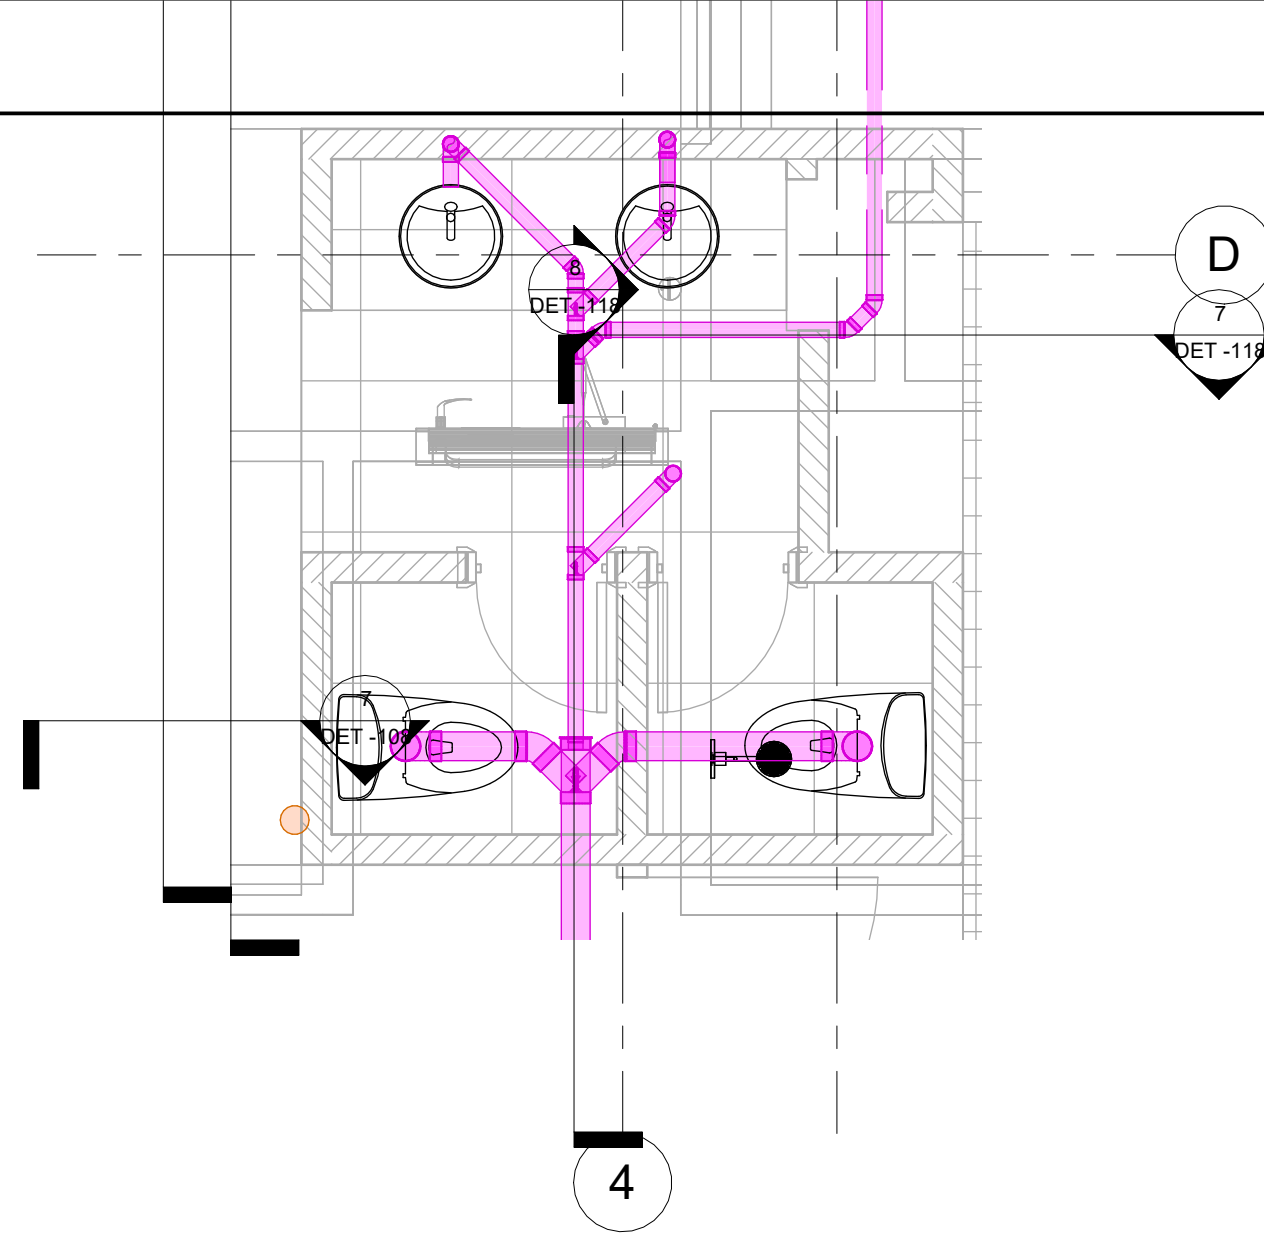


1 CL_TERRAZA - SANITARIO
1 : 30

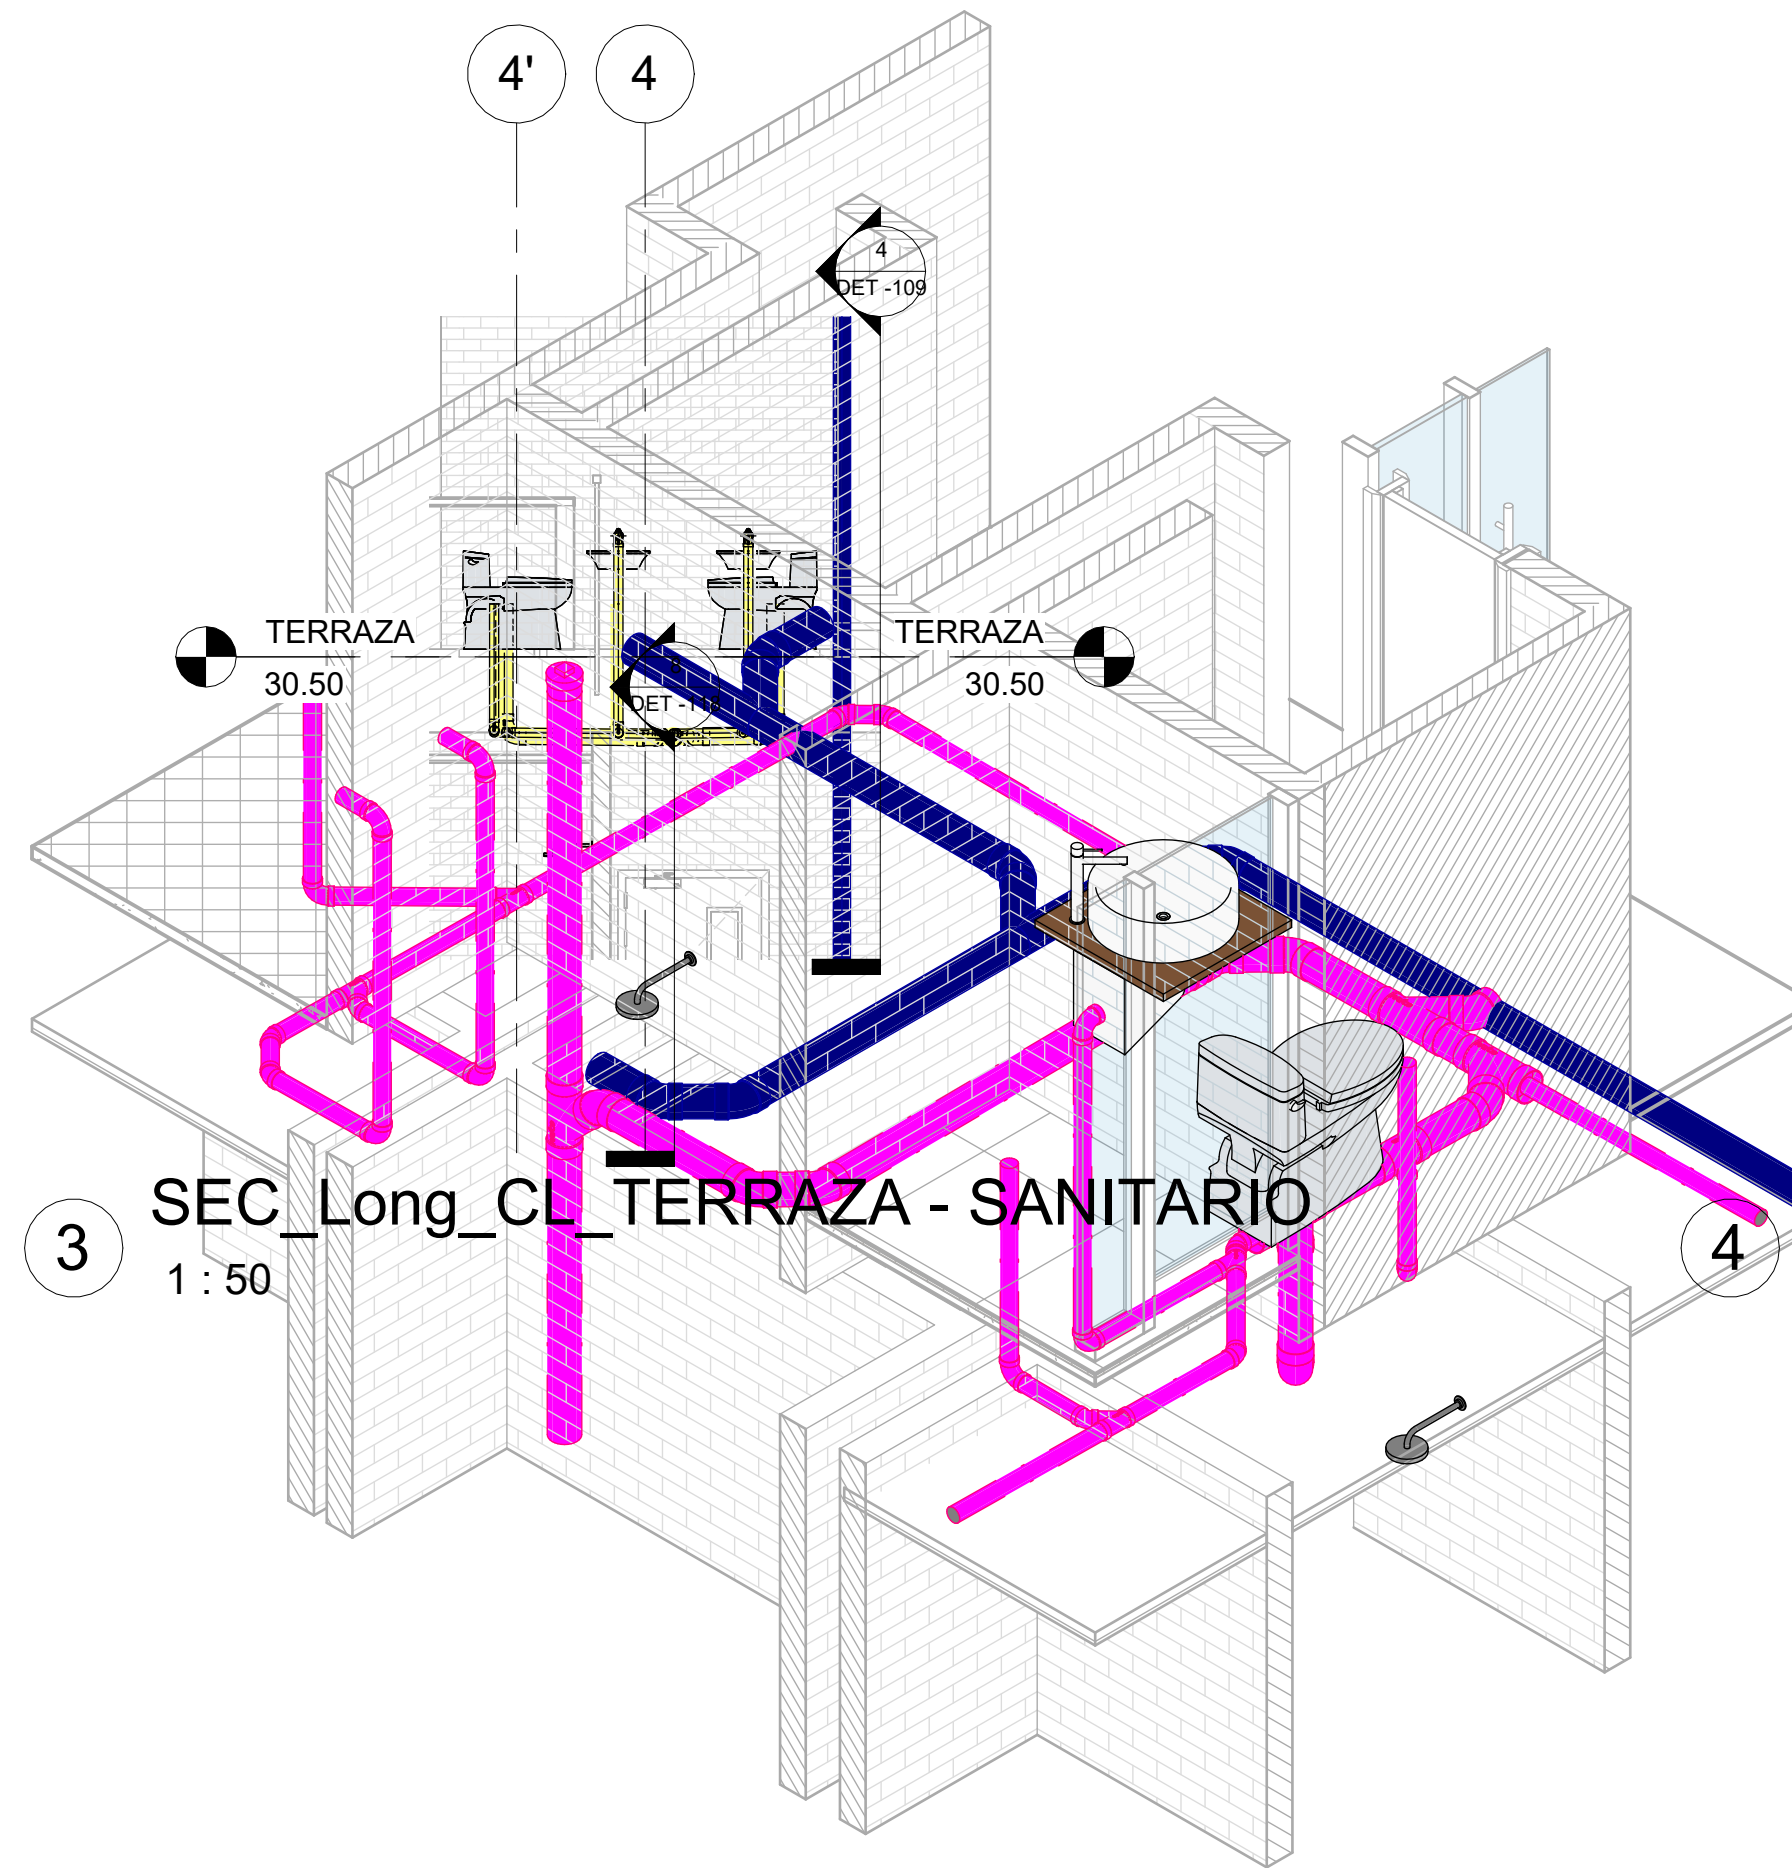


2 3D_CL_TERRAZA - SANITARIO

3 SEC_Long_CL_TERRAZA - SANITARIO
1 : 50

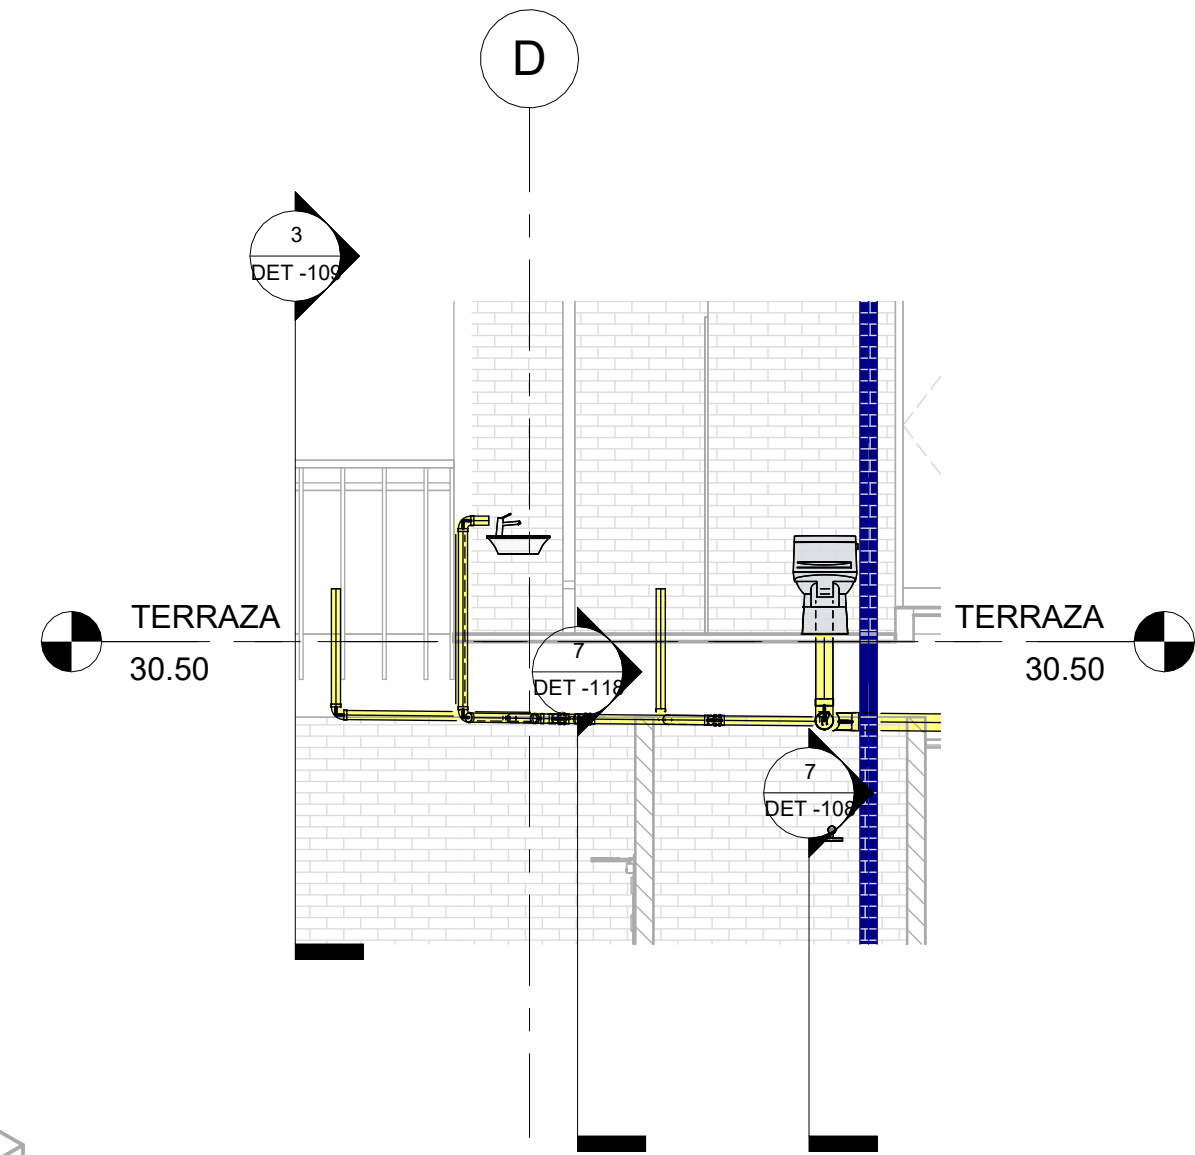


4 SEC_Trans_CL_TERRAZA - SANITARIO
1 : 50

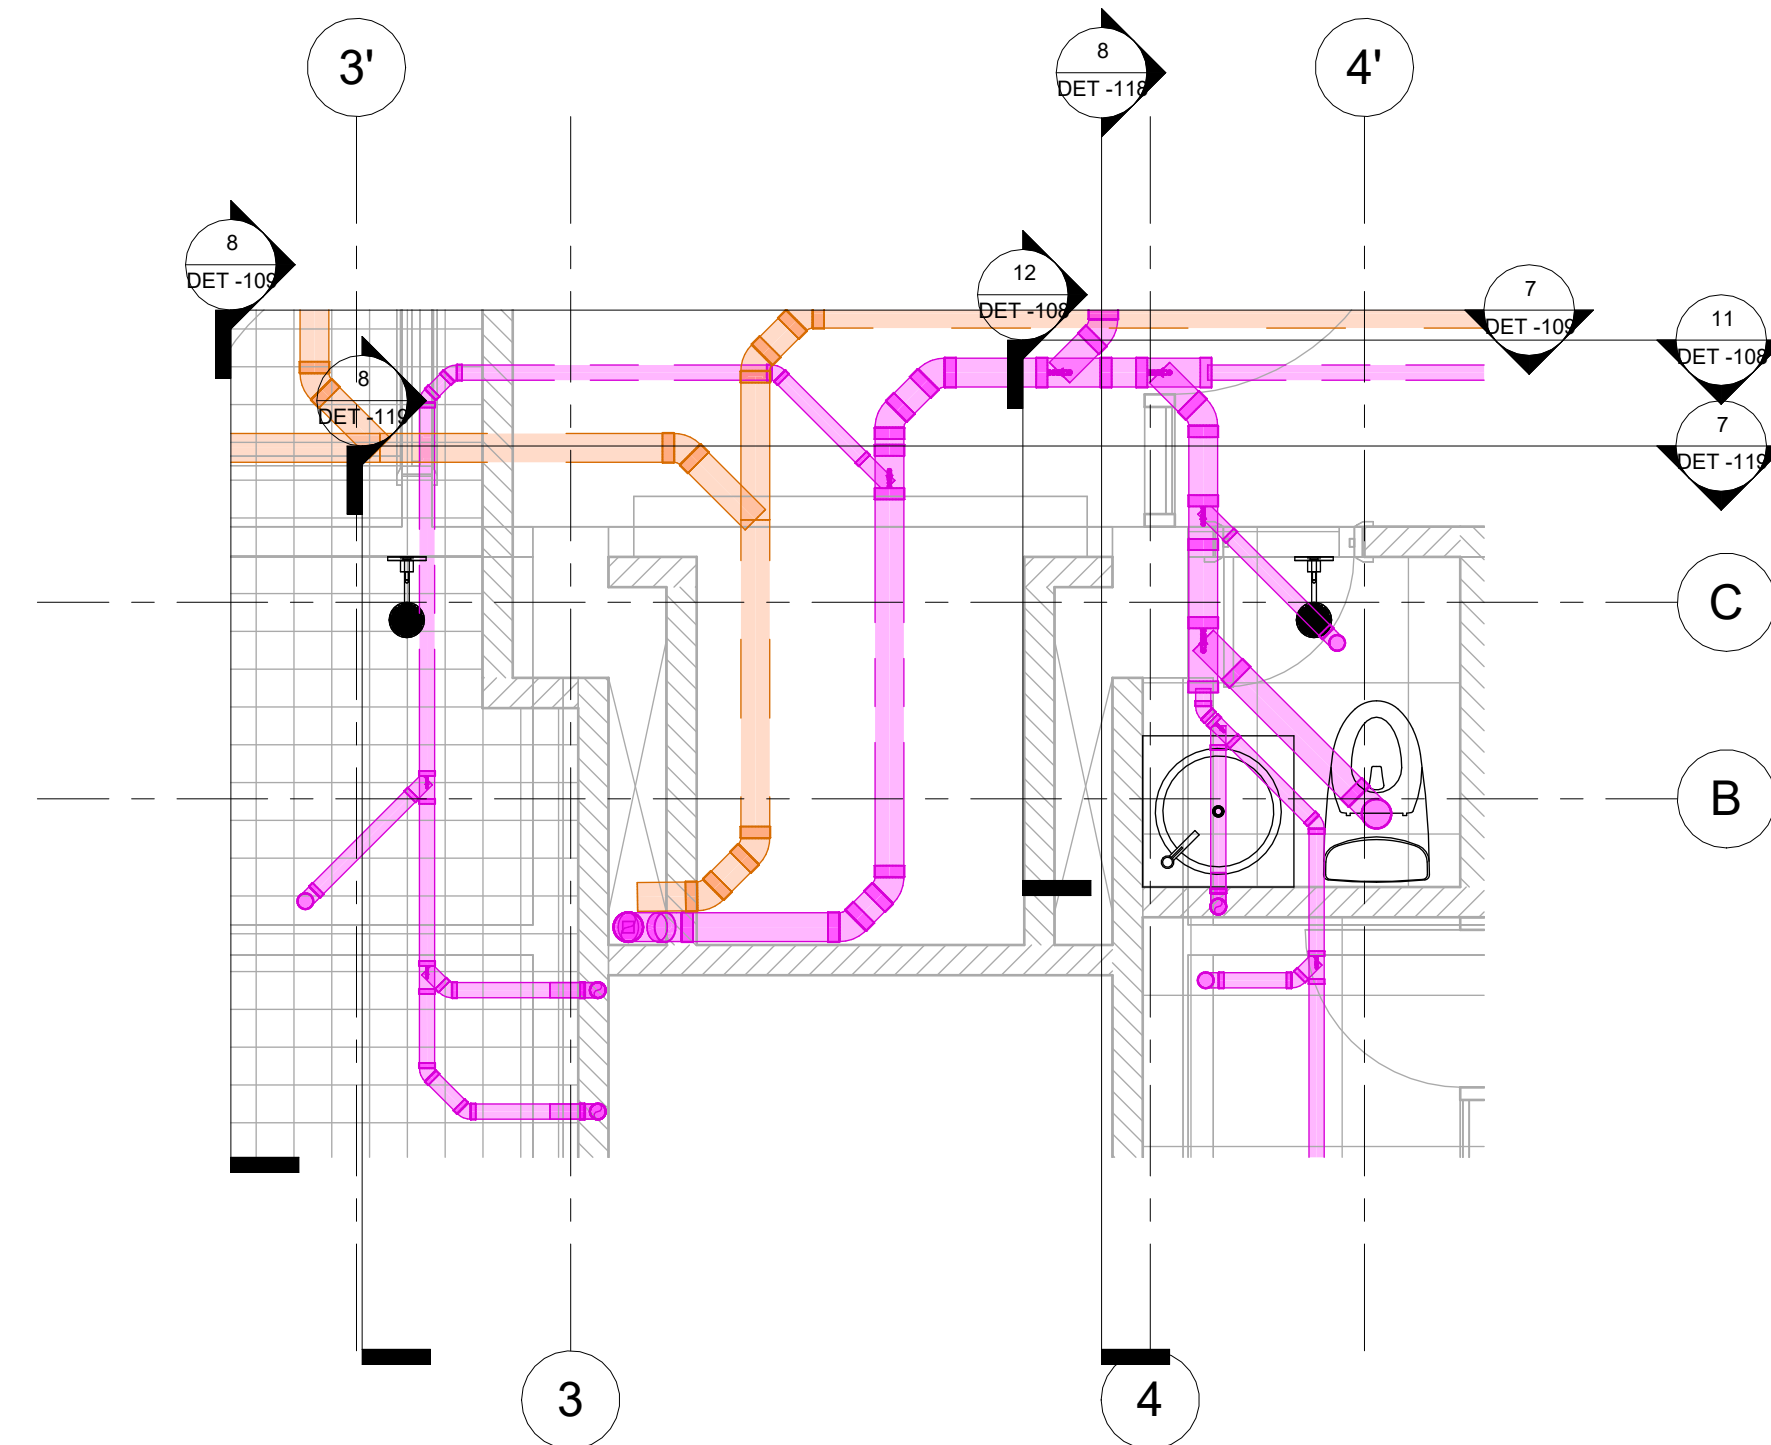


5 CL_TERRAZA - SANITARIO_2
1 : 30

6 3D_CL_TERRAZA - SANITARIO_2

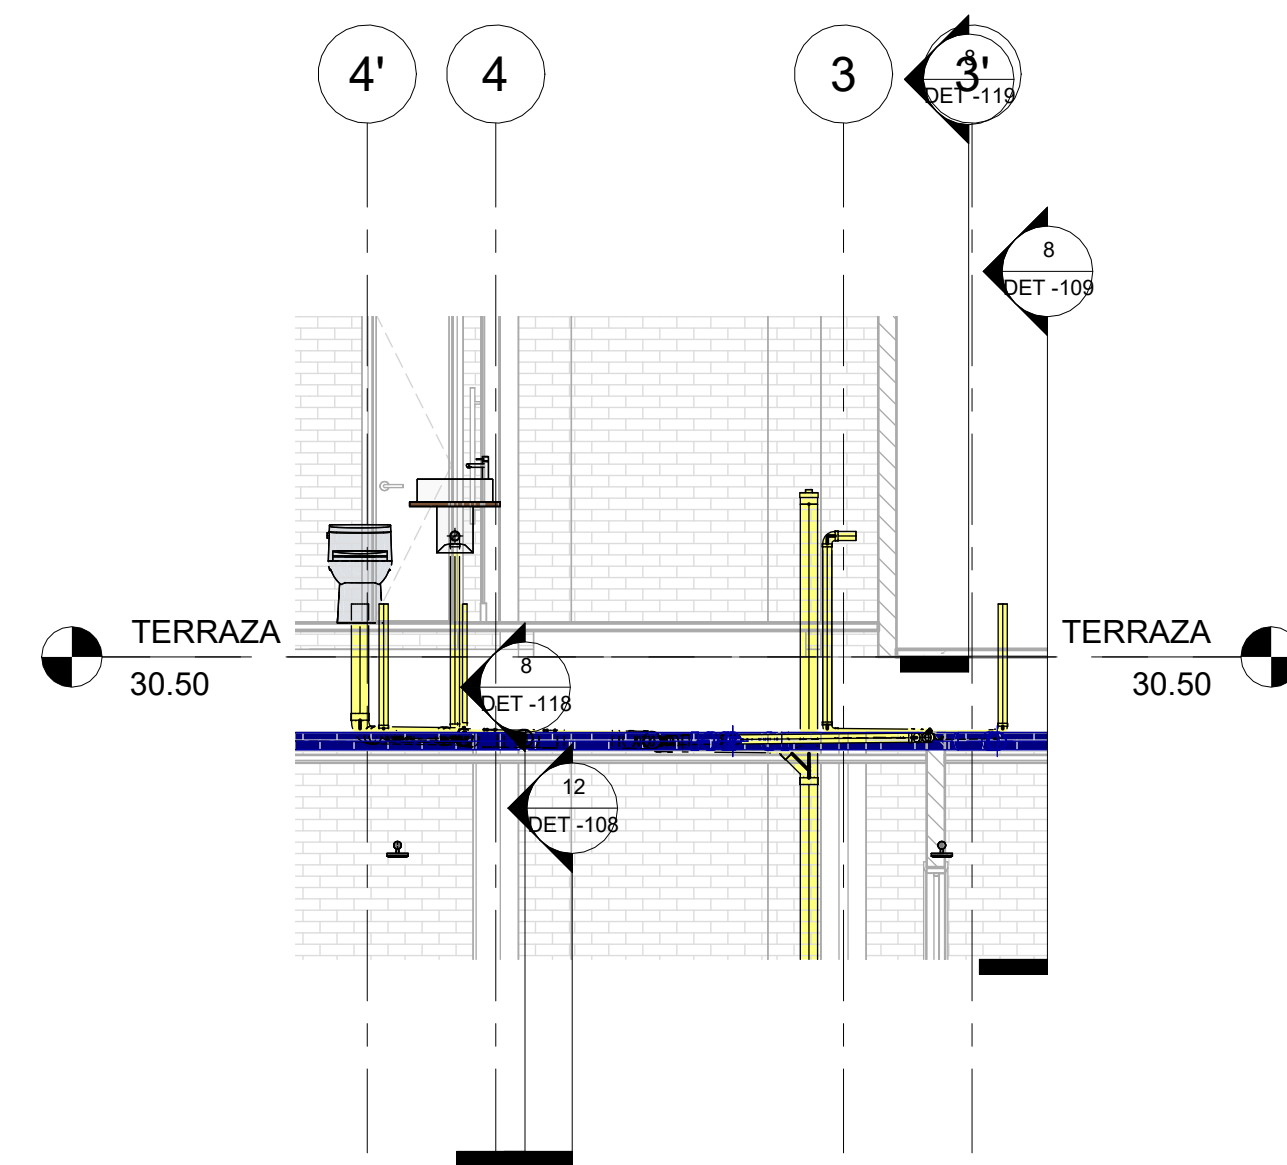

7 SEC_Long_CL_TERRAZA - SANITARIO_2
1 : 50

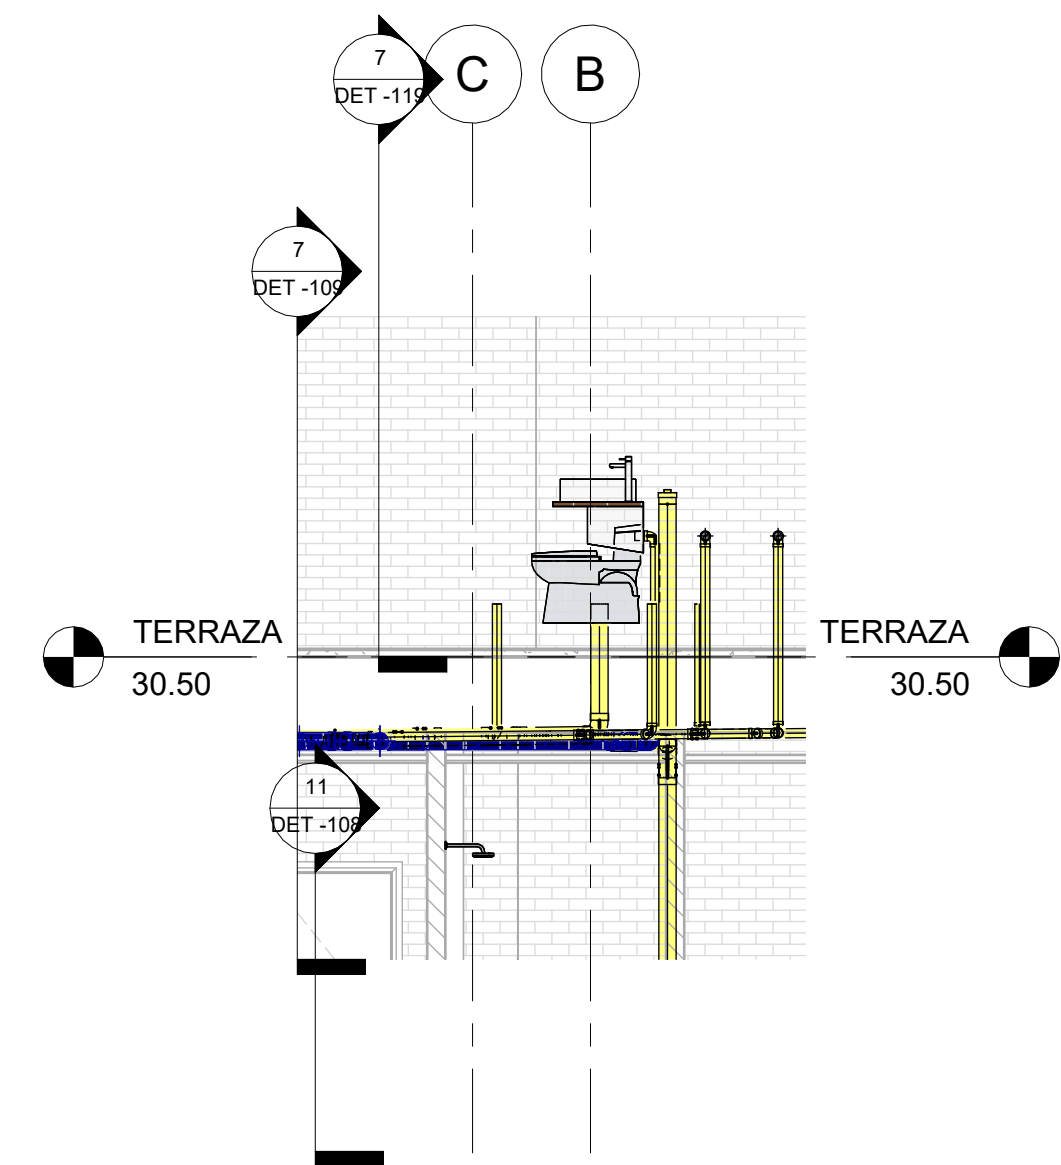

8 SEC_Trans_CL_TERRAZA - SANITARIO_2
1 : 50

EMCALI GERENCIA DE UEN ACUEDUCTO Y ALCANTARILLADO UNIDAD DE INGENIERIA	
FLORENTINO LIVING	
DETALLE 9	
PROYECTO Designer	CALCULO: Checker
PRESUPUESTO No.	DIBUJO: Author
REVISOR: Checker	REVISOR: Checker
ESCALA: Como se indica	APROBO: Approver
FECHA: SEPTIEMBRE 2025	ARCHIVO:

FECHA	REVISIONES	REVISOR	APROBO