




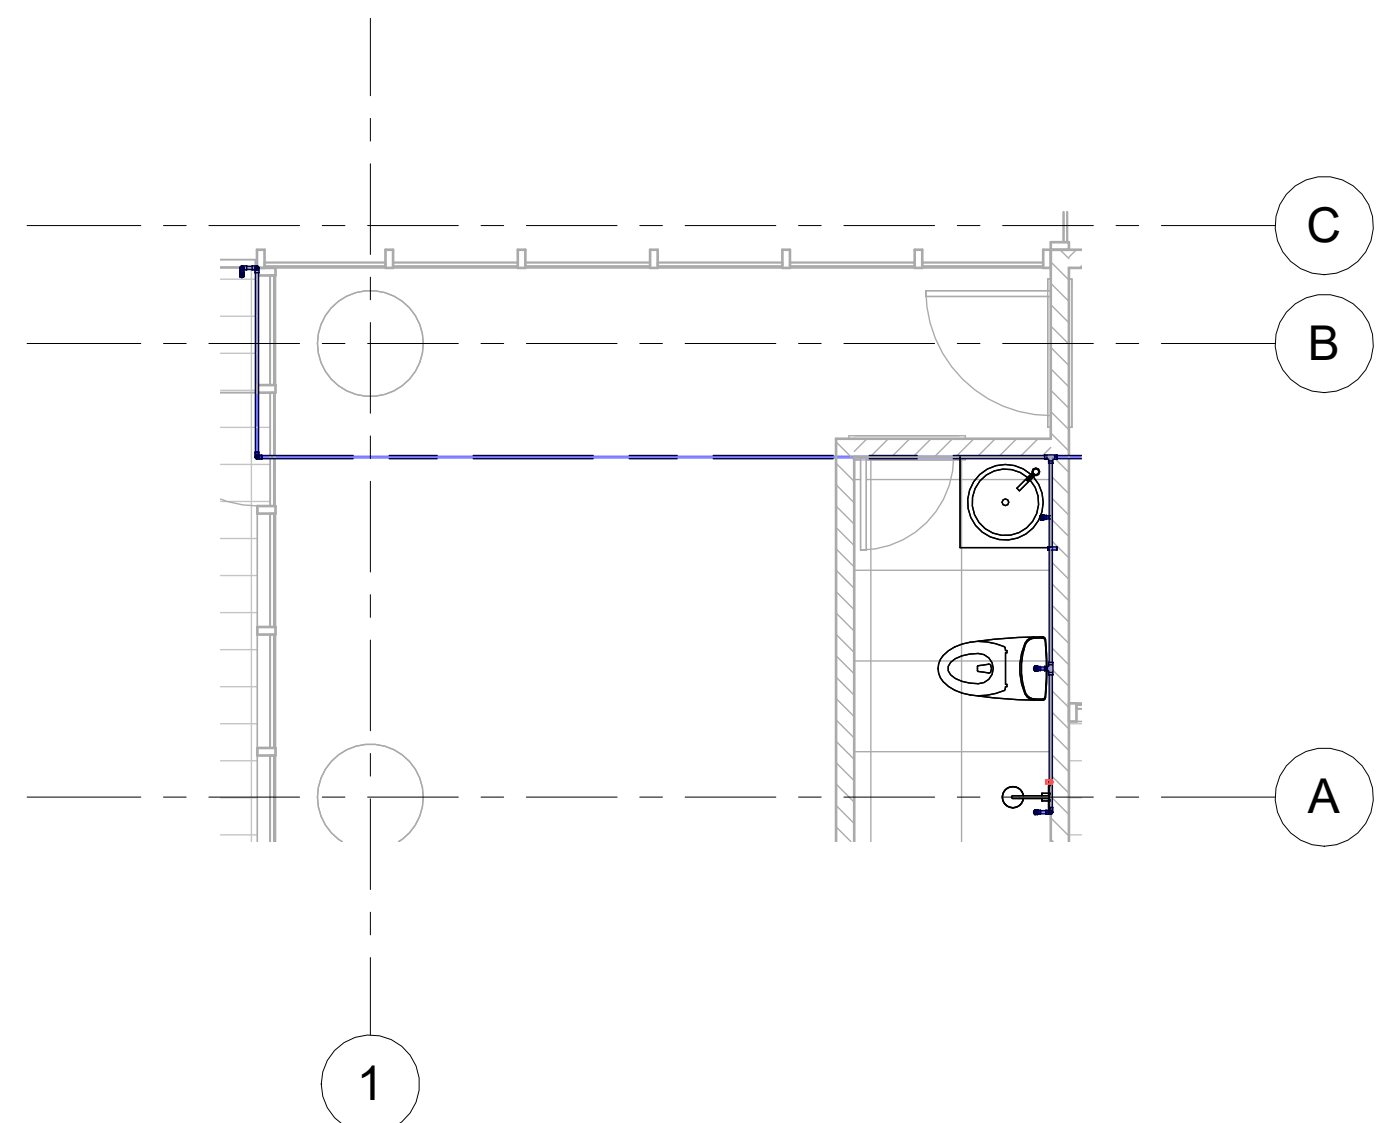


1 CL_PISO 4 - HIDRAULICO
1 : 50

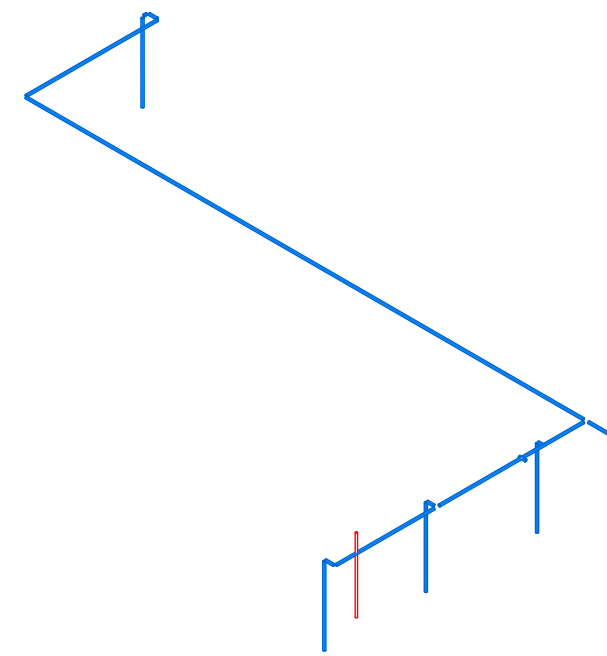


2 3D_CL_PISO 4 - HIDRAULICO

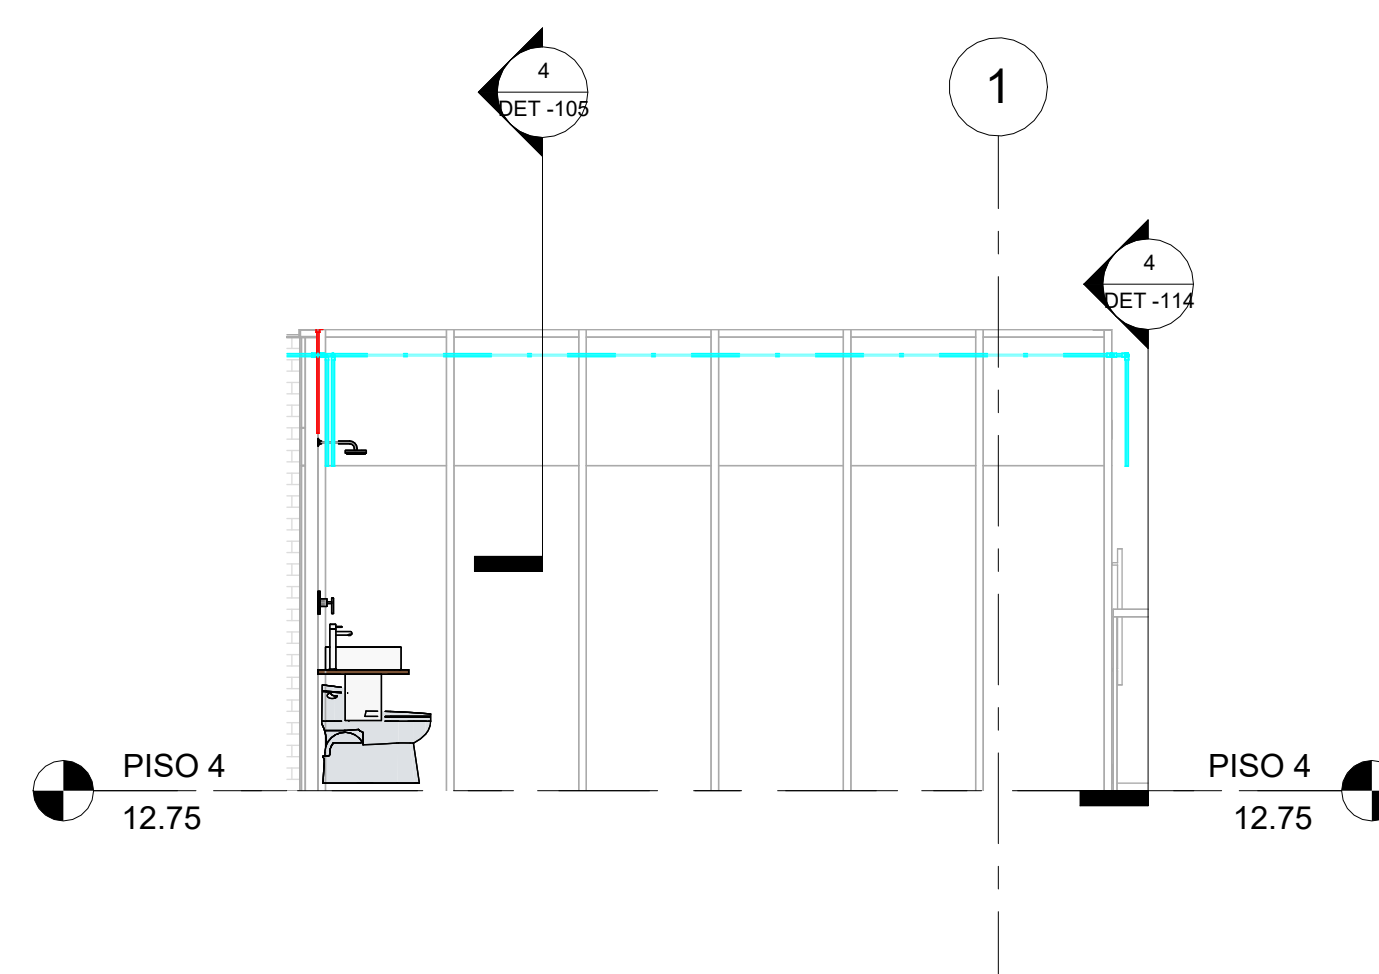


3 SEC_Long_CL_PISO 4 - HIDRAULICO
1 : 50

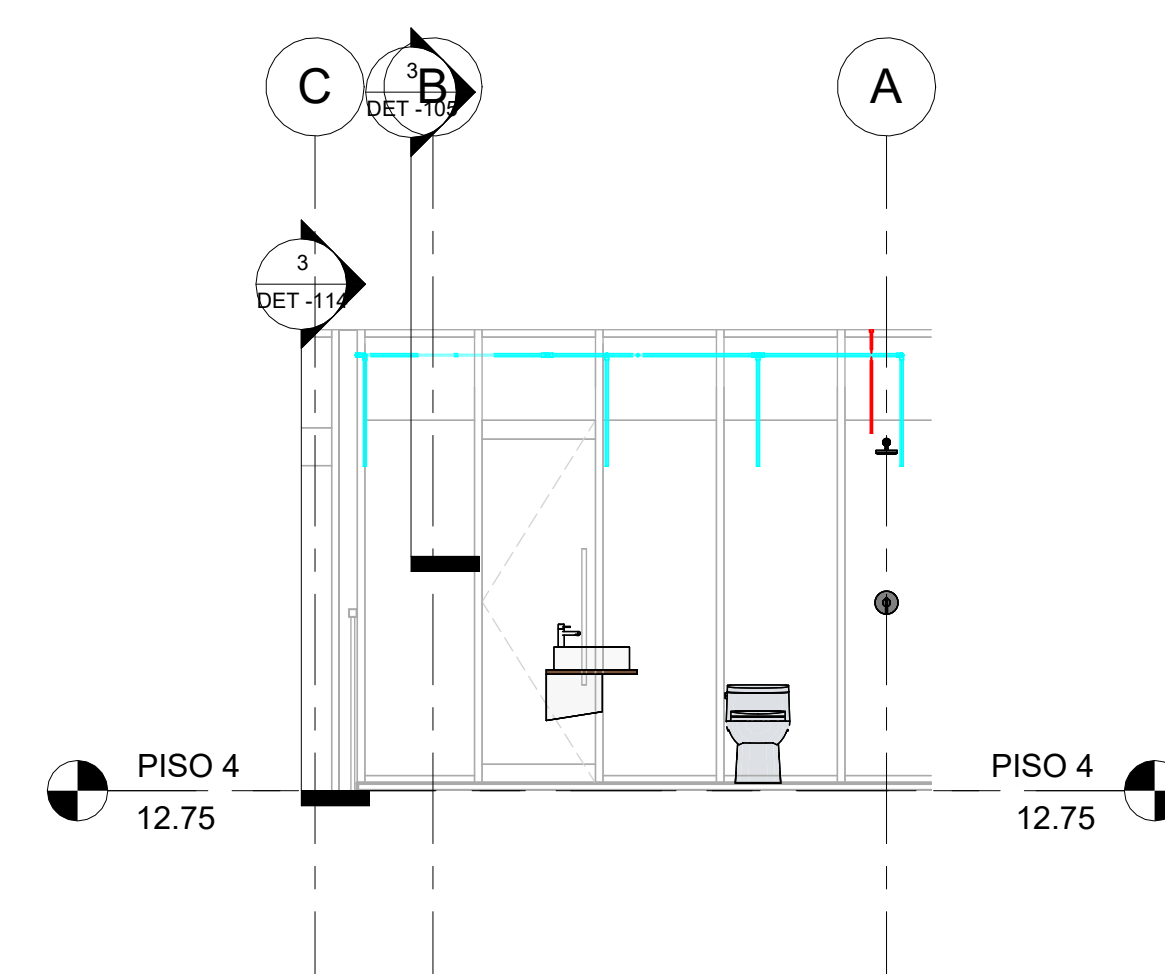


4 SEC_Trans_CL_PISO 4 - HIDRAULICO
1 : 50

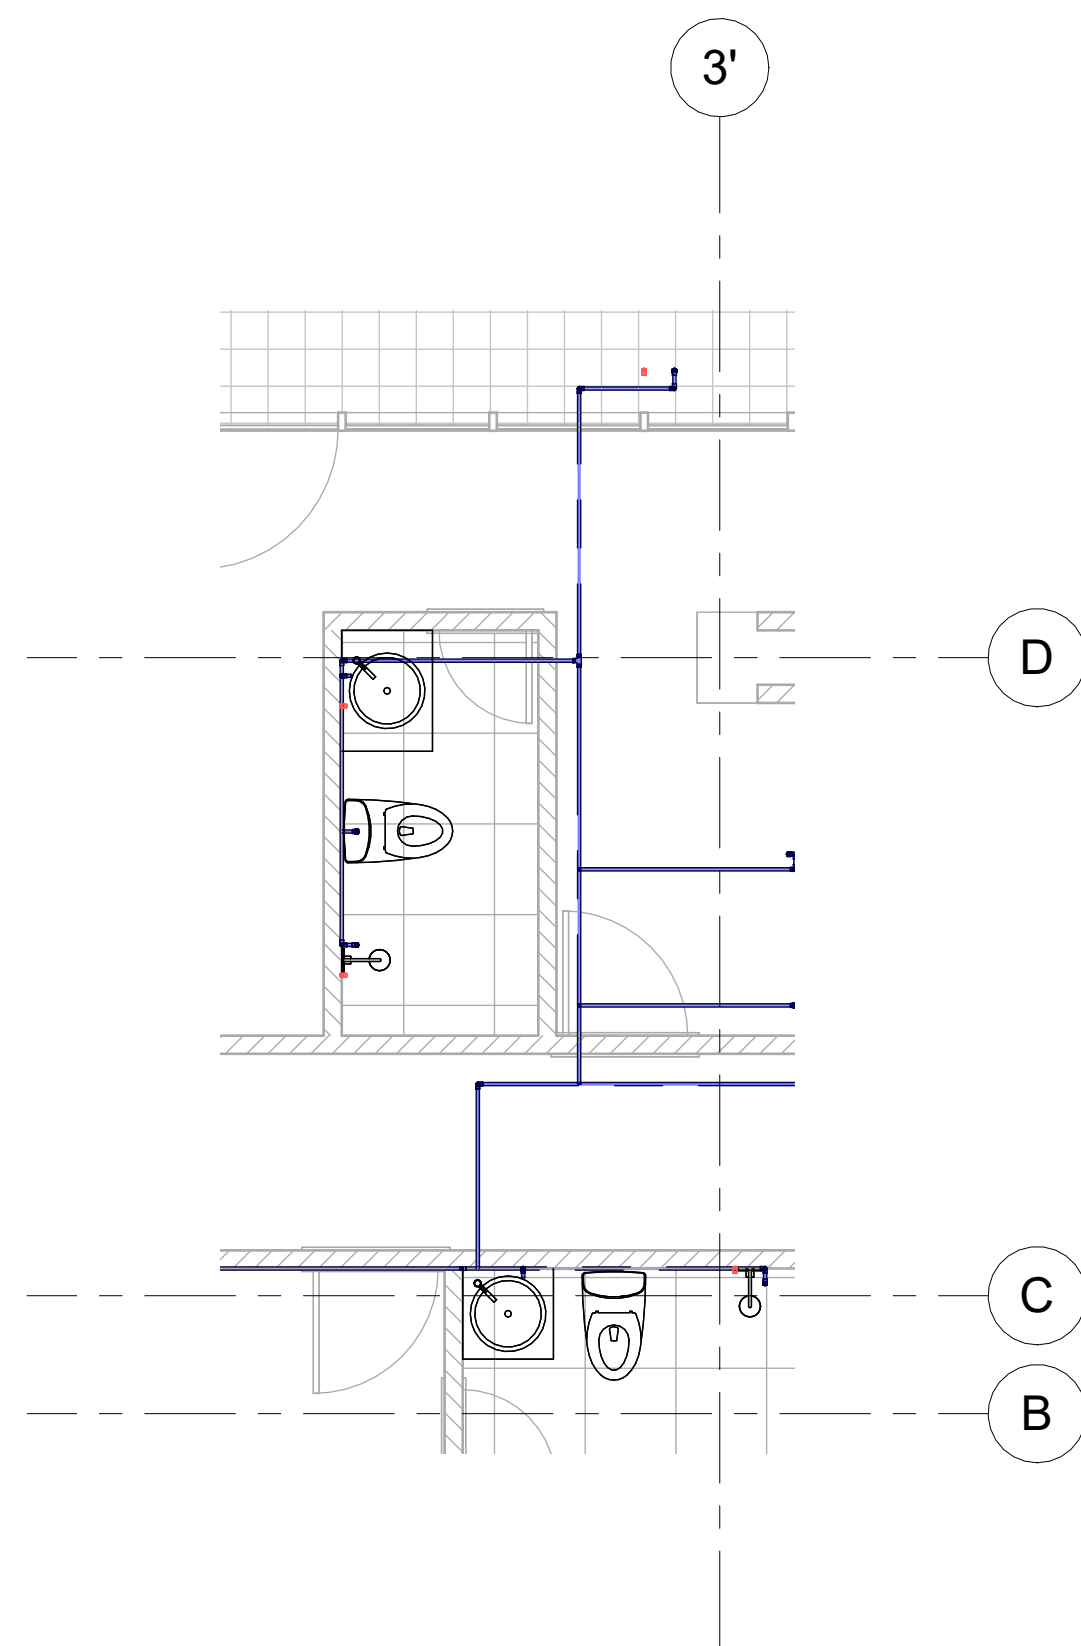


5 CL_PISO 4 - HIDRAULICO_2
1 : 50

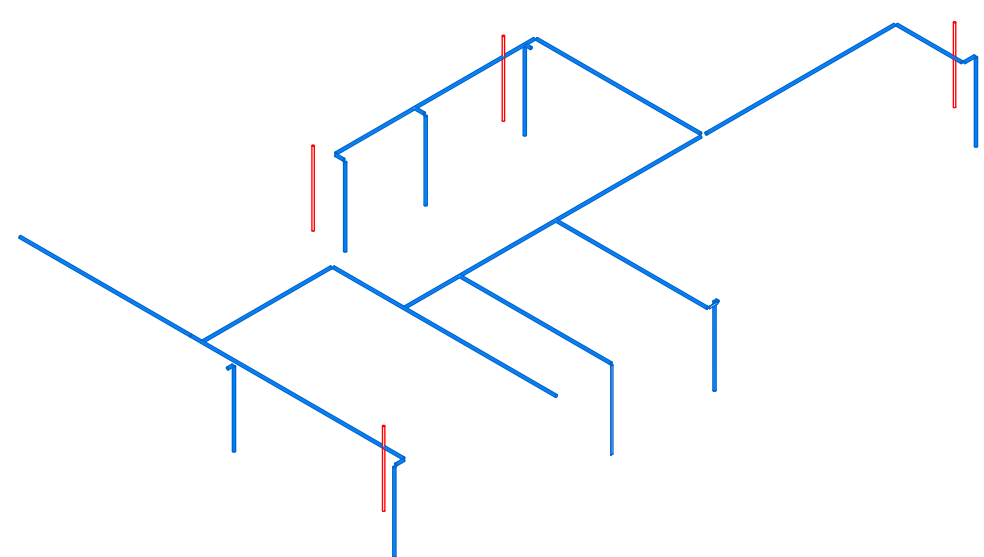


6 3D_CL_PISO 4 - HIDRAULICO_2

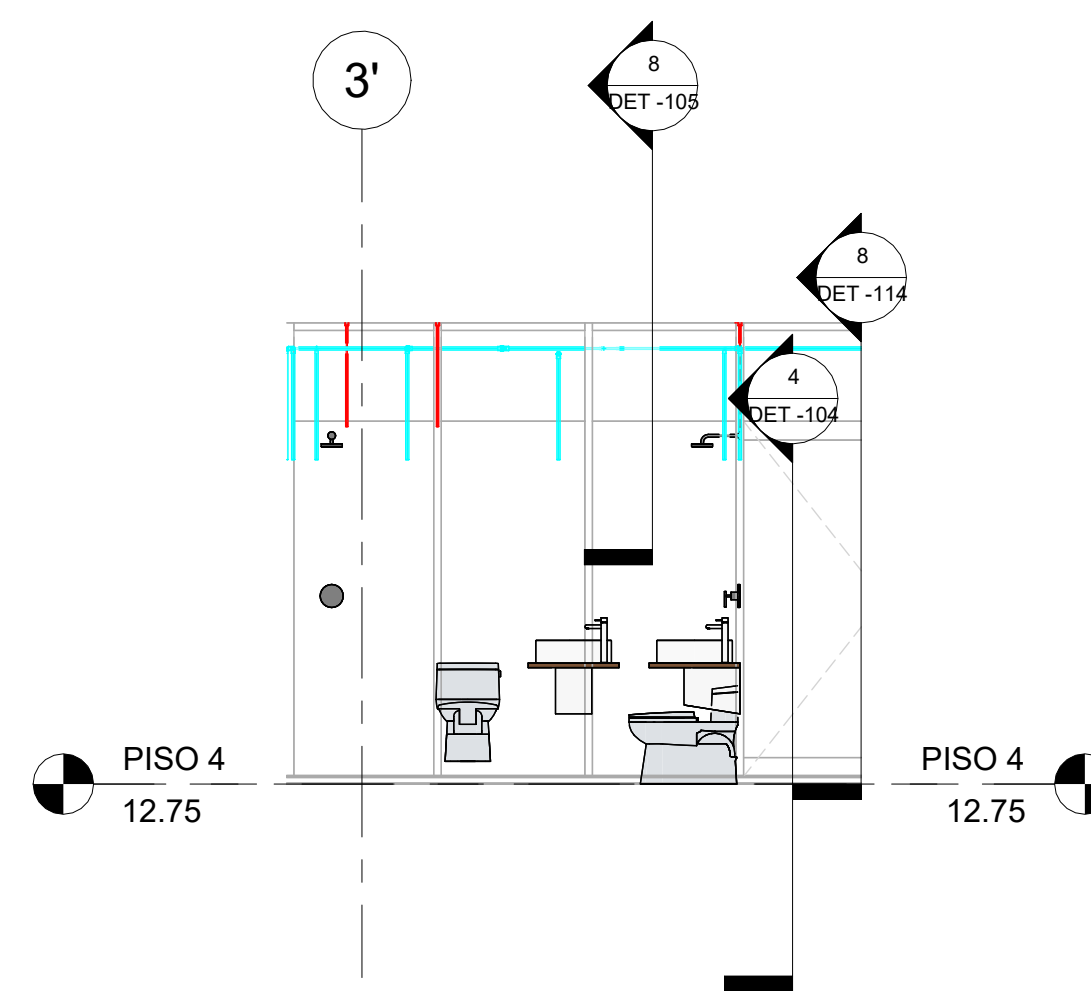


7 SEC_Long_CL_PISO 4 - HIDRAULICO_2
1 : 50

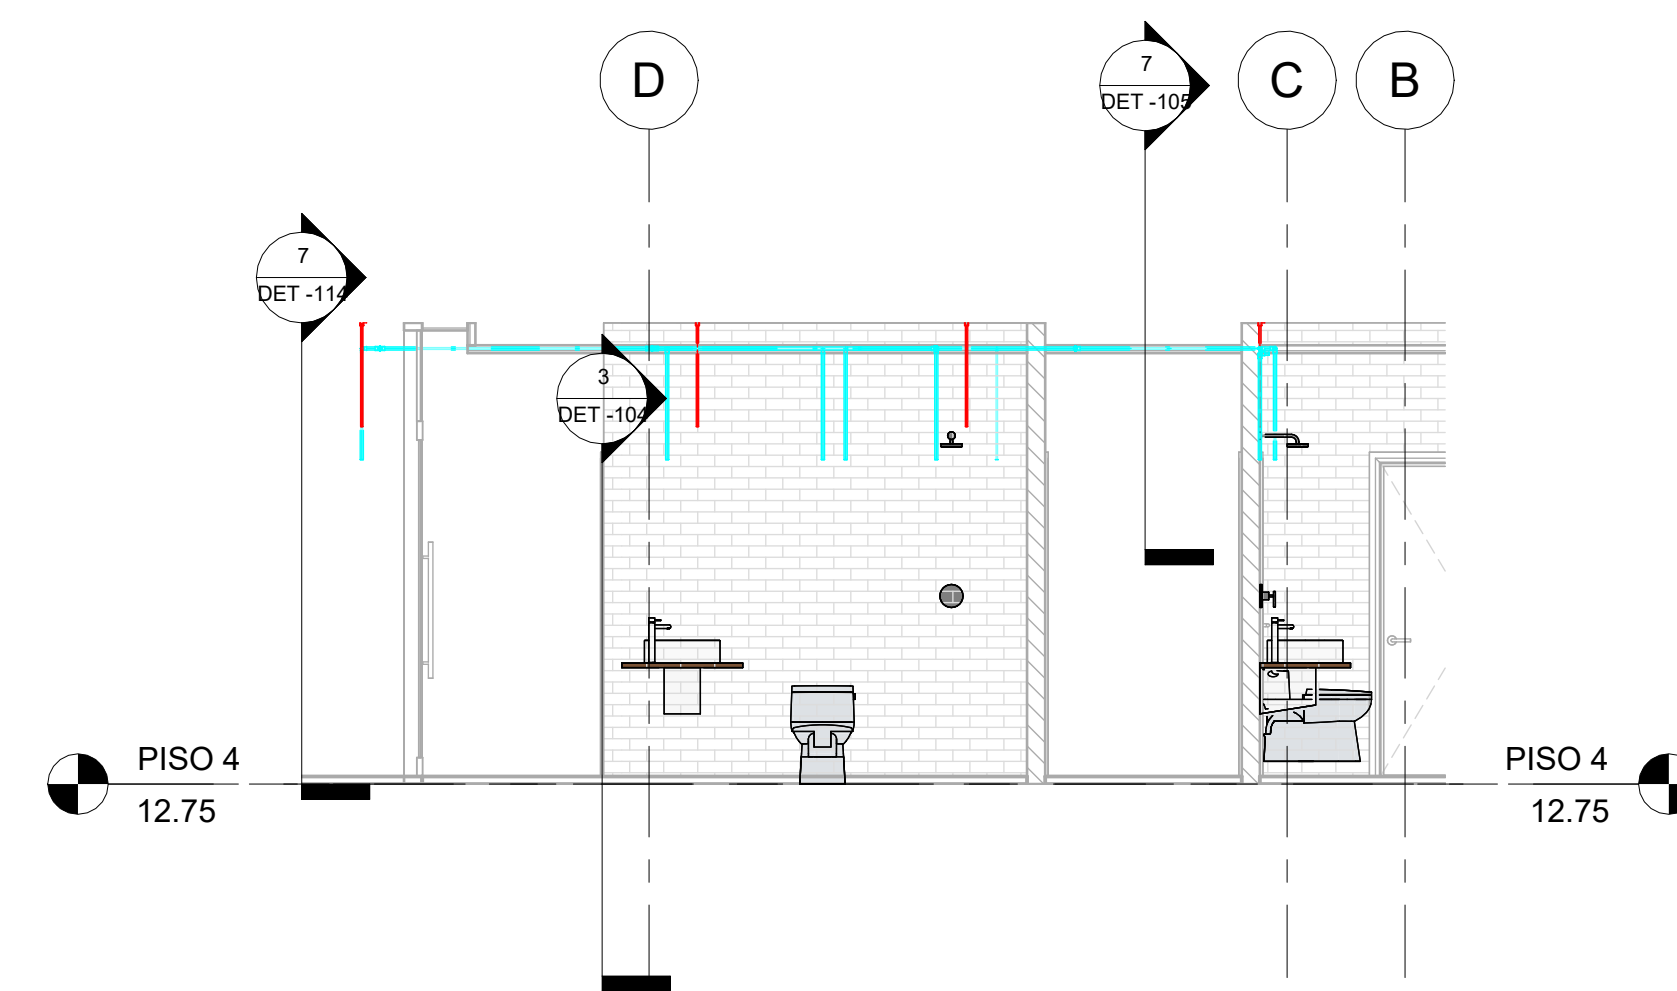


8 SEC_Trans_CL_PISO 4 - HIDRAULICO_2
1 : 50

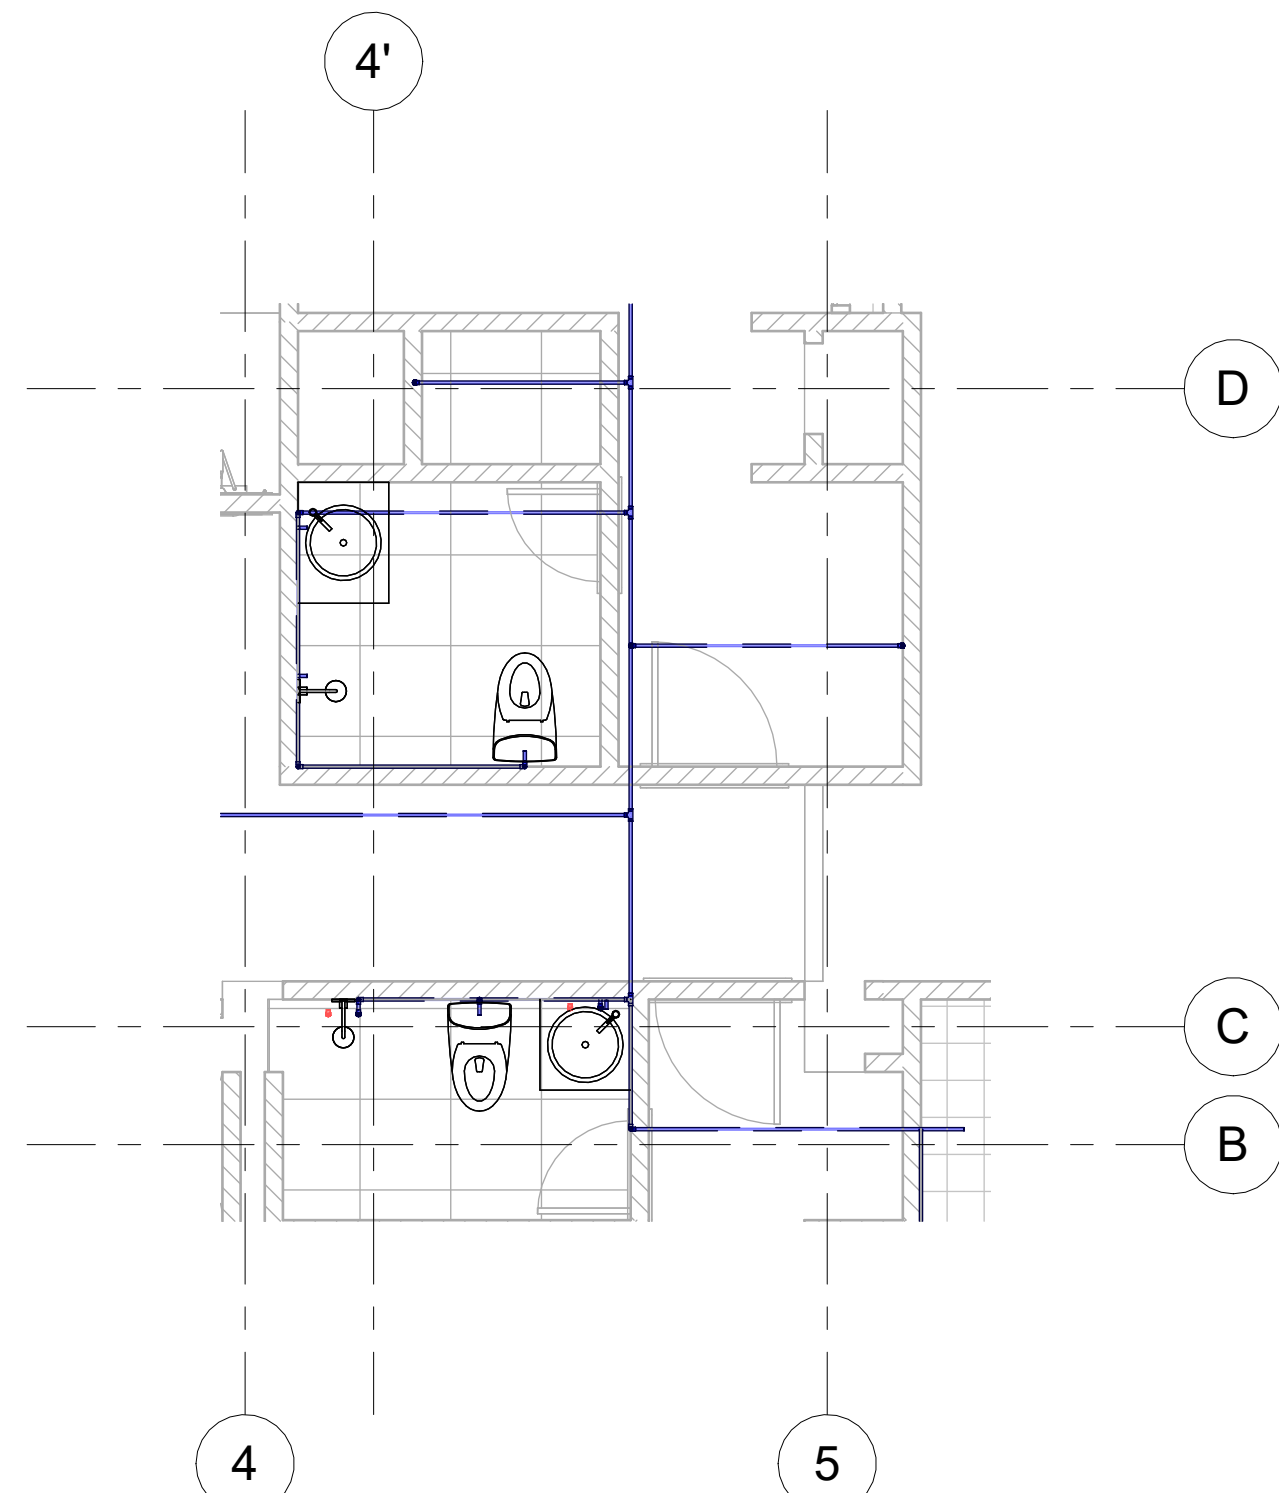


9 CL_PISO 4 - HIDRAULICO_3
1 : 50

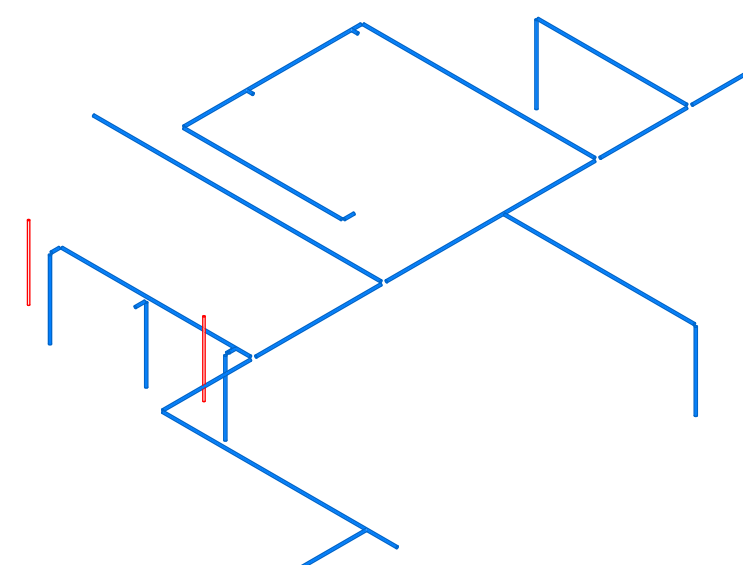

10 3D_CL_PISO 4 - HIDRAULICO_3

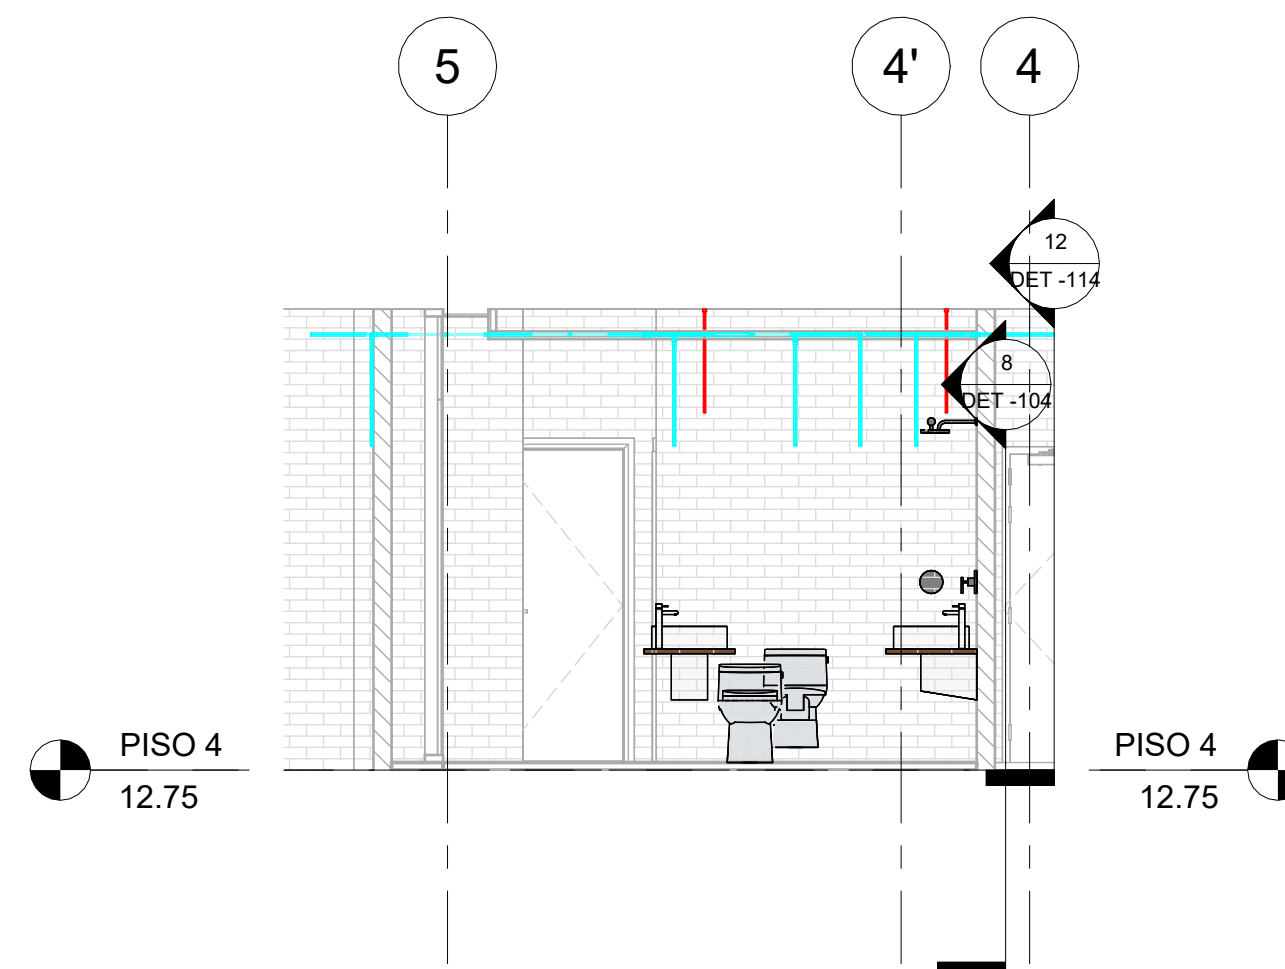

11 SEC_Long_CL_PISO 4 - HIDRAULICO_3
1 : 50

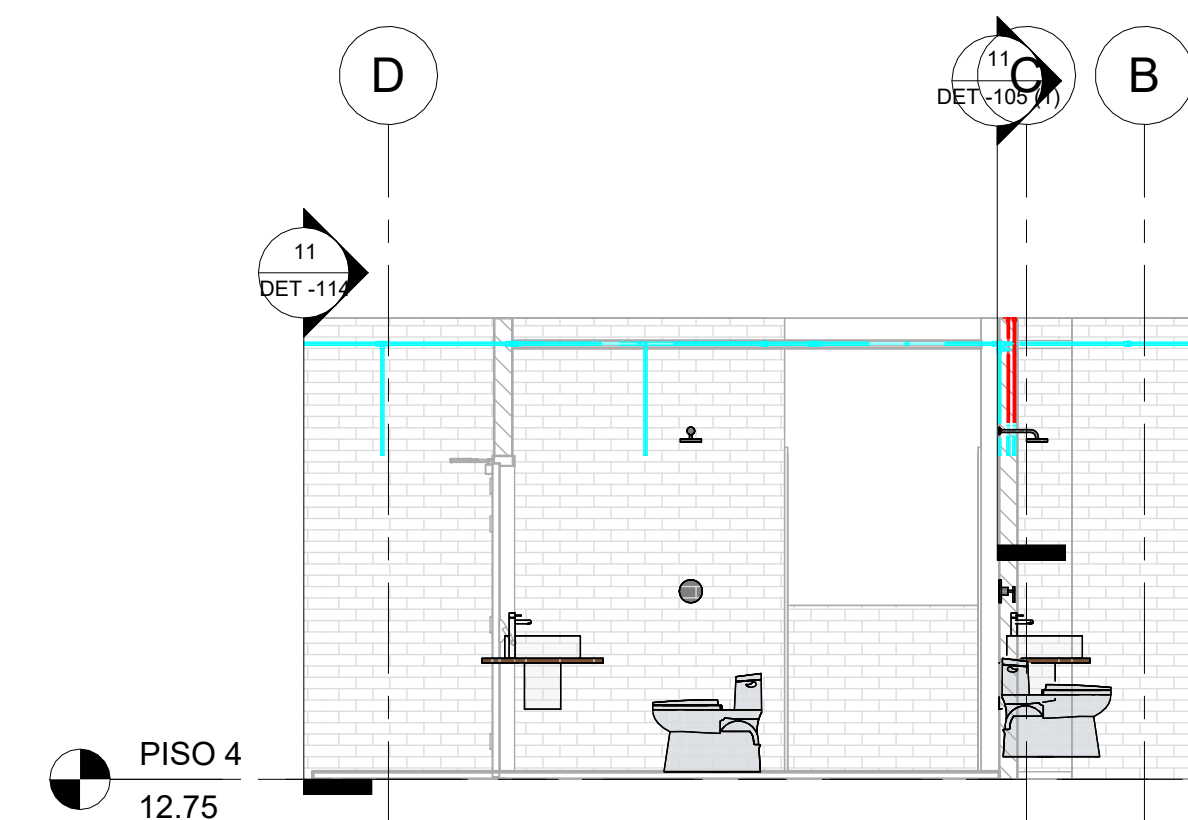

12 SEC_Trans_CL_PISO 4 - HIDRAULICO_3
1 : 50

EMCALI GERENCIA DE UEN ACUEDUCTO Y ALCANTARILLADO UNIDAD DE INGENIERIA			
FLORENTINO LIVING			
PISO 4 12.75 DETALLE 14			
PROYECTO	Designer	CALCULO:	Checker
PRESUPUESTO No.		DIBUJO:	Author
		REVISO:	Checker
ESCALA:	1 : 50	APROBO:	Approver
FECHA:	SEPTIEMBRE 2025	ARCHIVO:	