




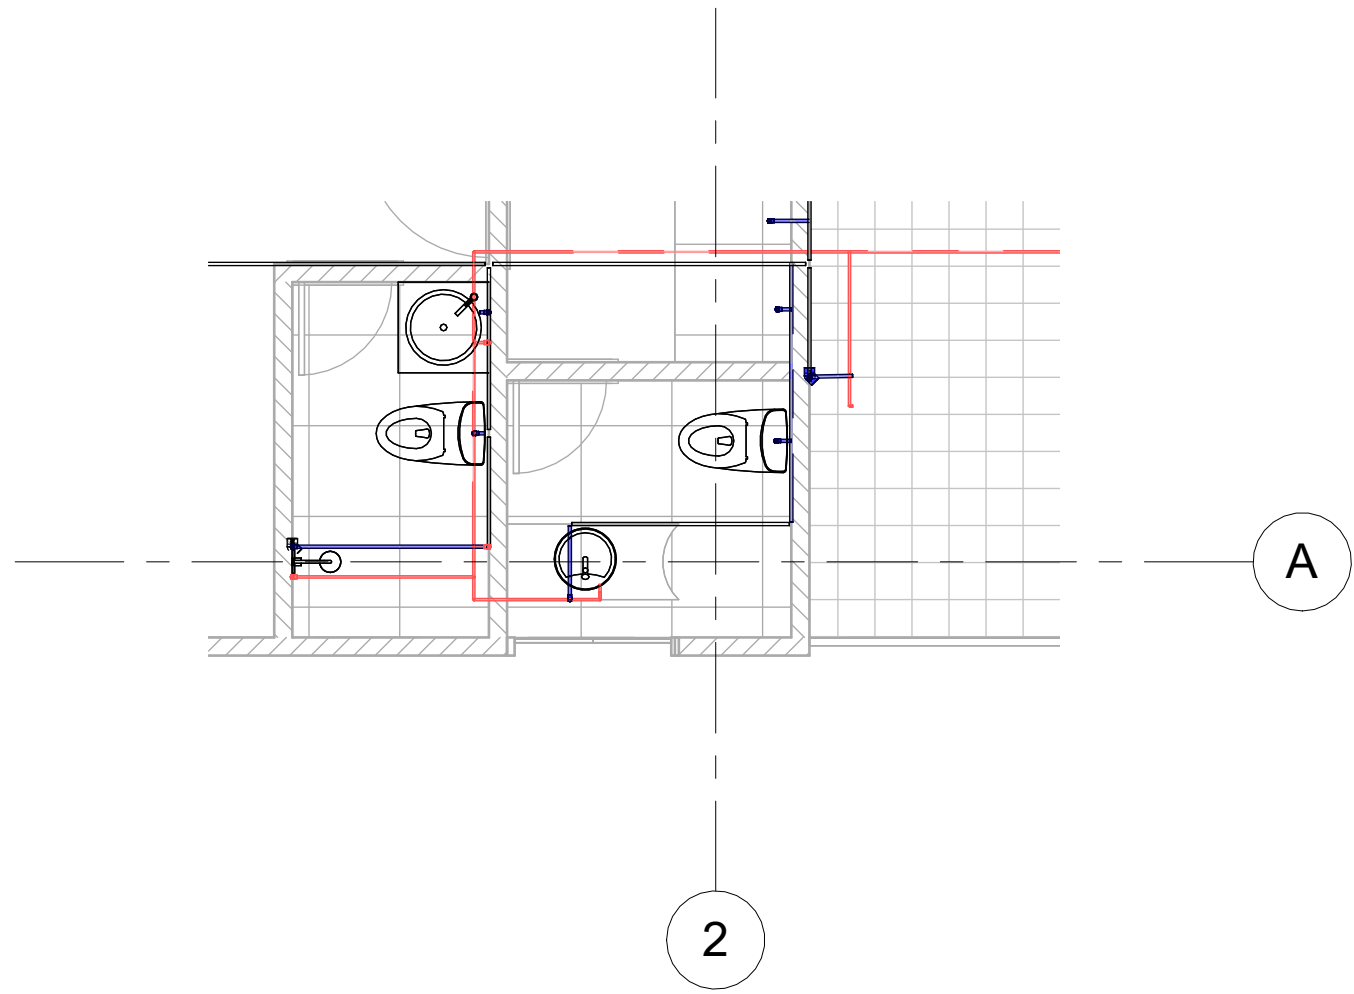


1 CL_PISO 5 - HIDRAULICO
1 : 50

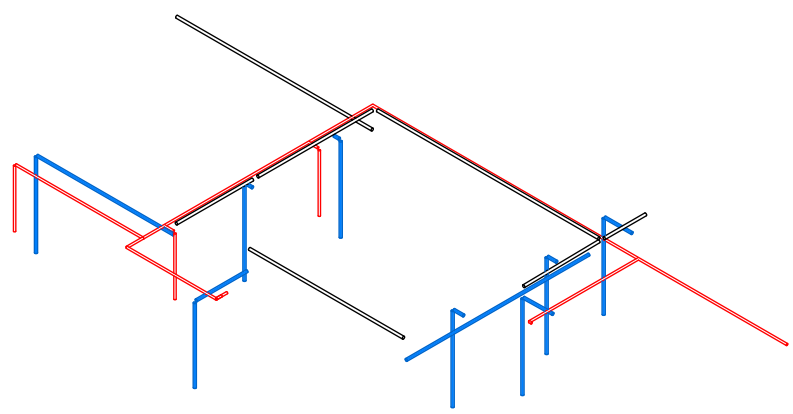


2 3D_CL_PISO 5 - HIDRAULICO

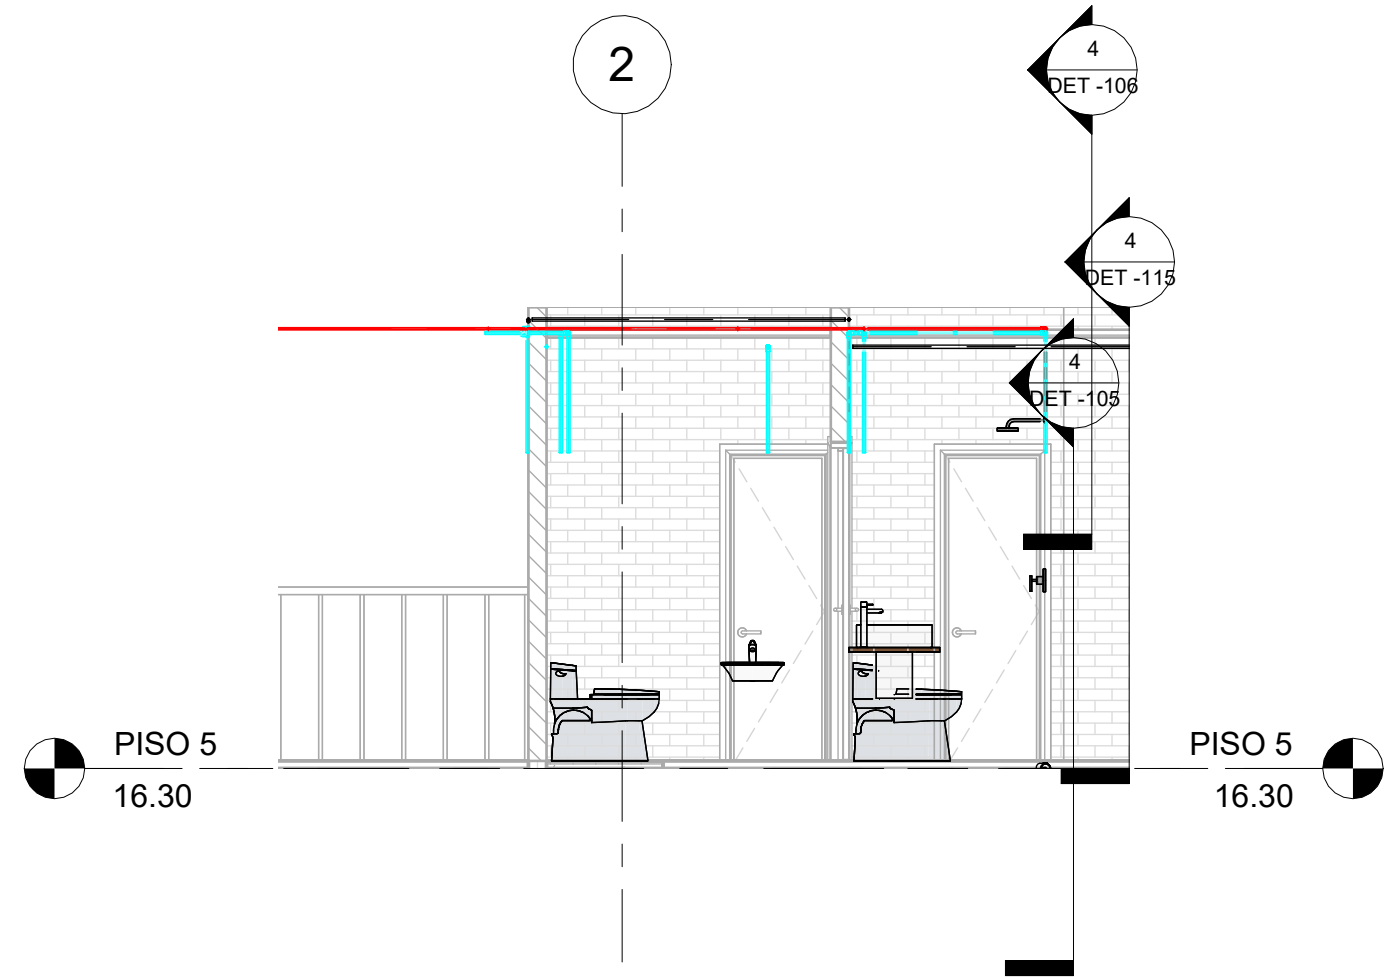


3 SEC_Long_CL_PISO 5 - HIDRAULICO
1 : 50

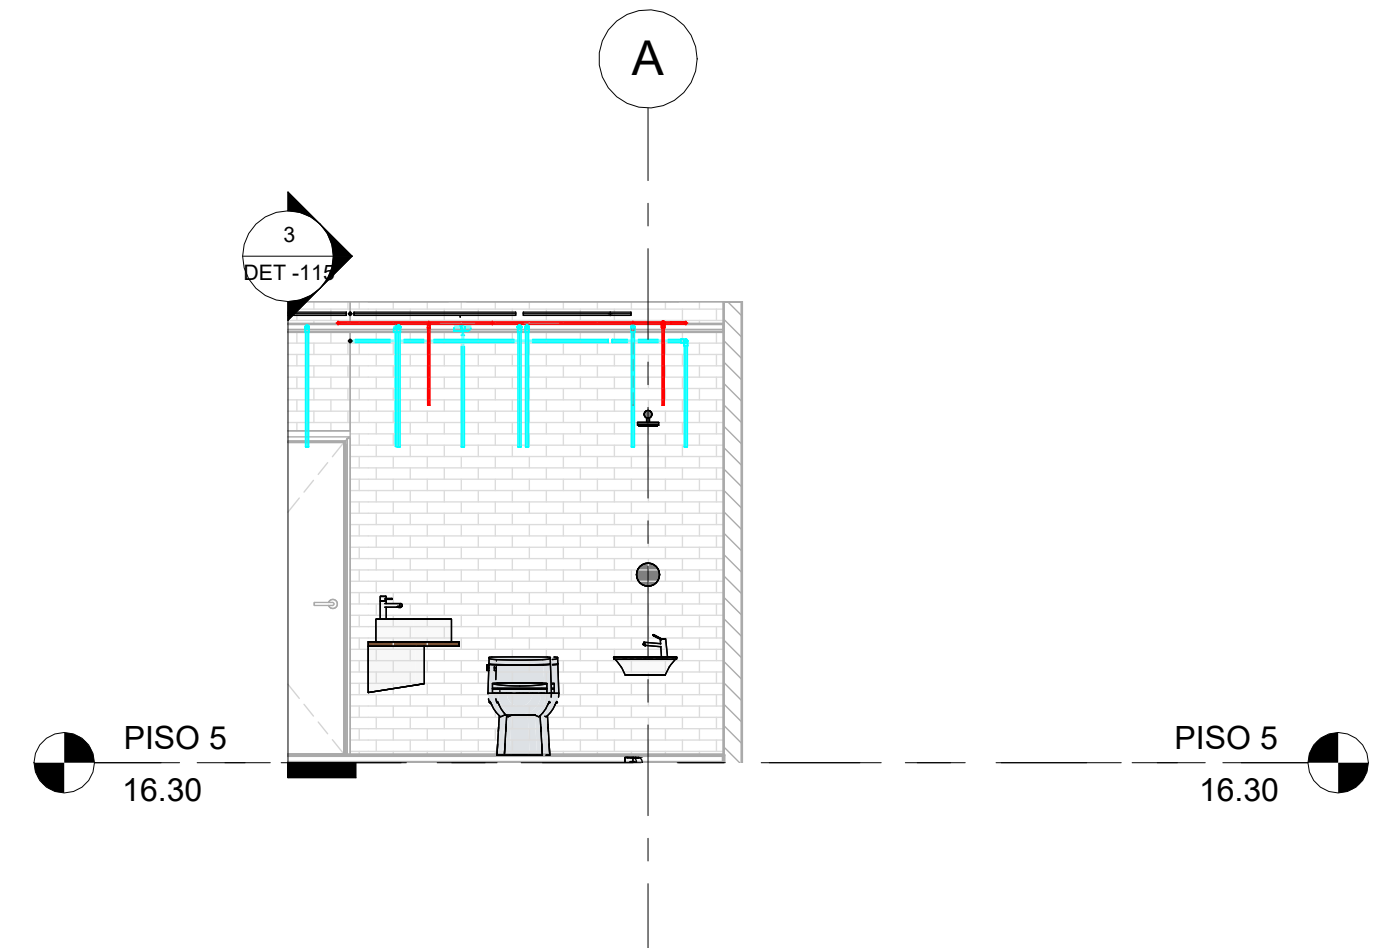


4 SEC_Trans_CL_PISO 5 - HIDRAULICO
1 : 50

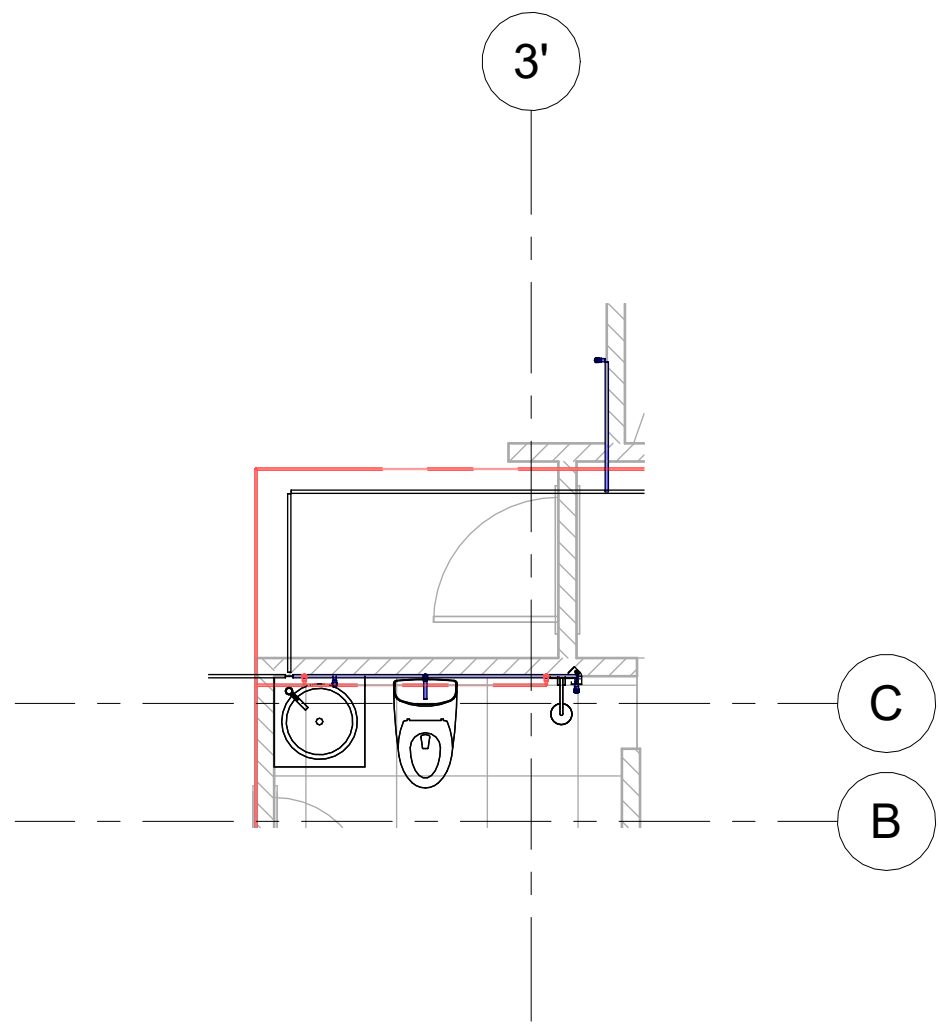


5 CL_PISO 5 - HIDRAULICO_2
1 : 50

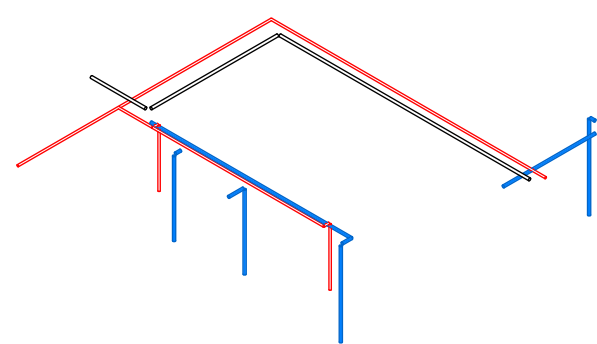


6 3D_CL_PISO 5 - HIDRAULICO_2

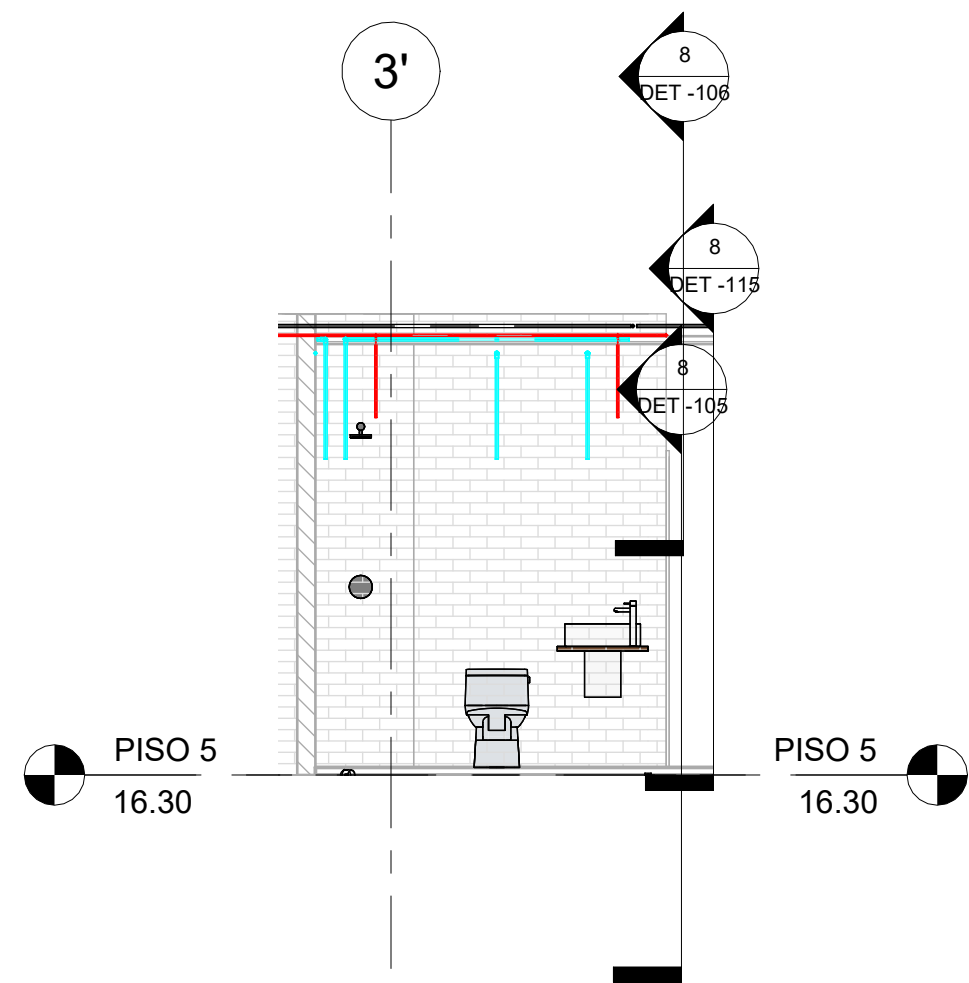


7 SEC_Long_CL_PISO 5 - HIDRAULICO_2
1 : 50

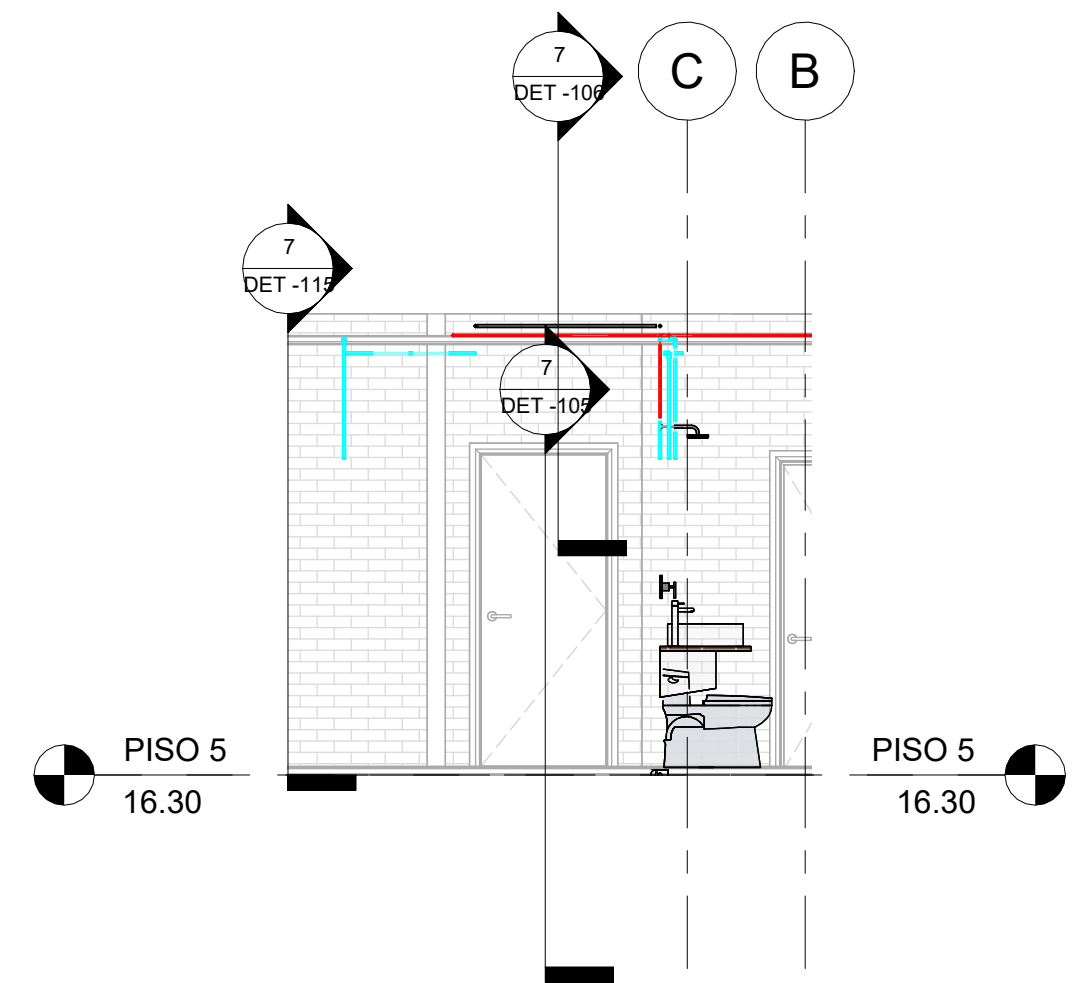


8 SEC_Trans_CL_PISO 5 - HIDRAULICO_2
1 : 50

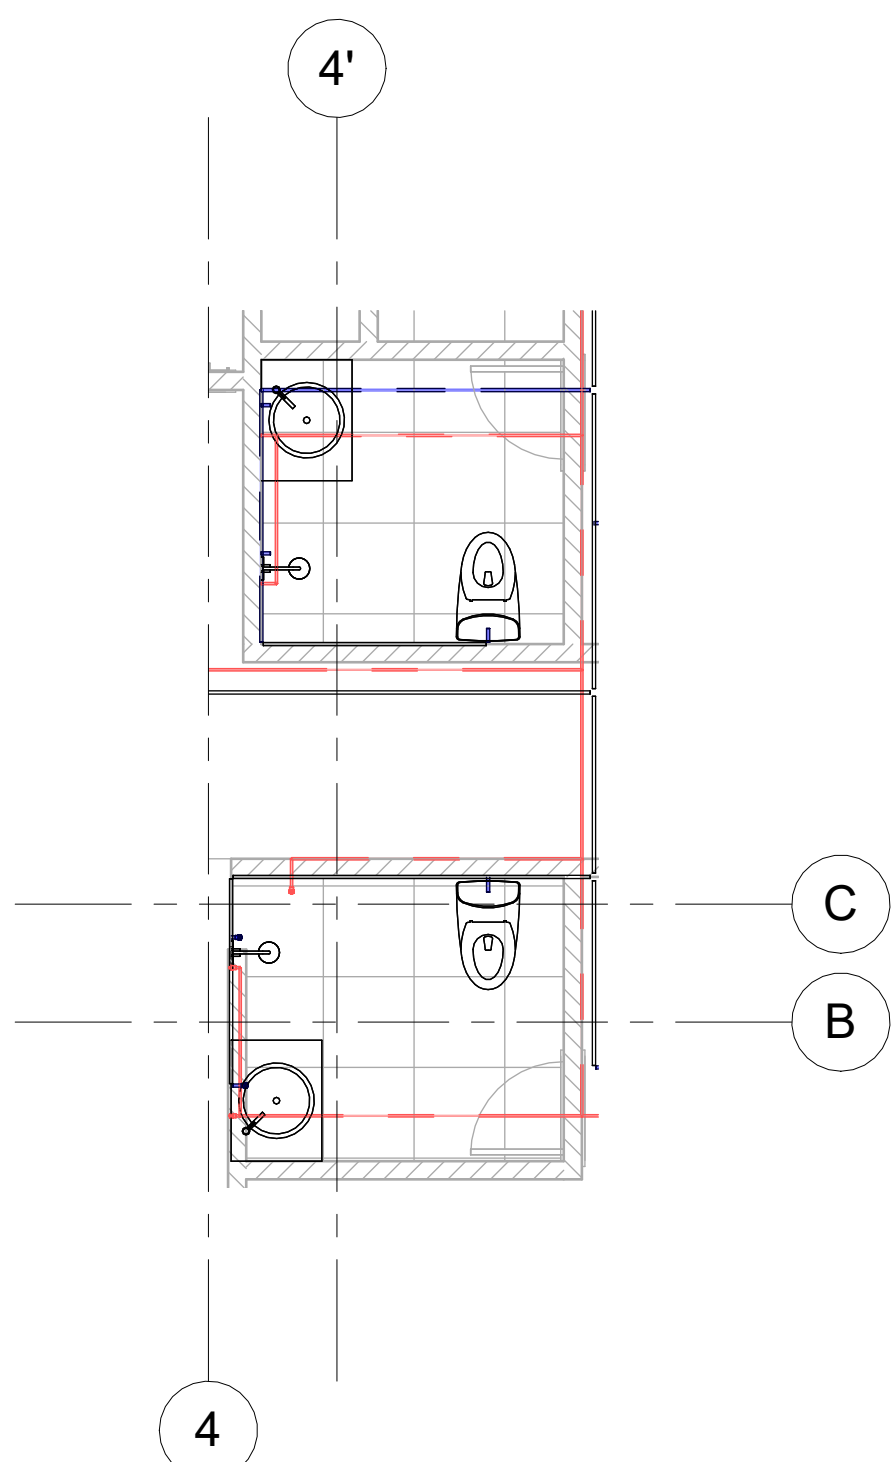


9 CL_PISO 5 - HIDRAULICO_3
1 : 50

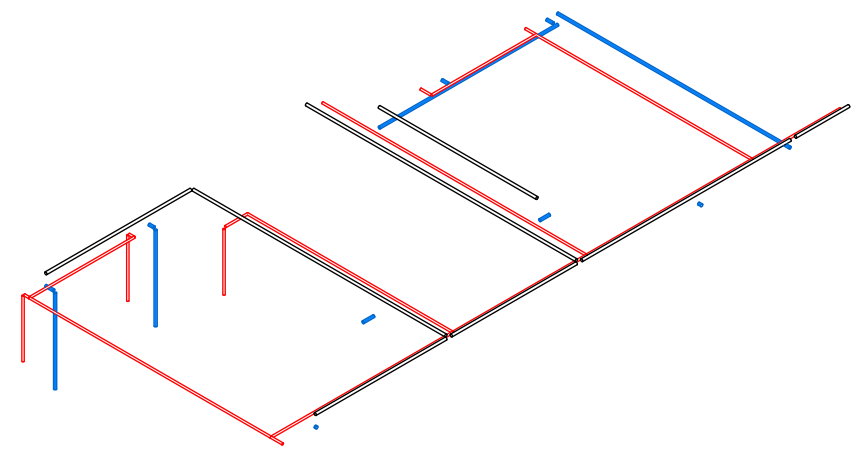

10 3D_CL_PISO 5 - HIDRAULICO_3

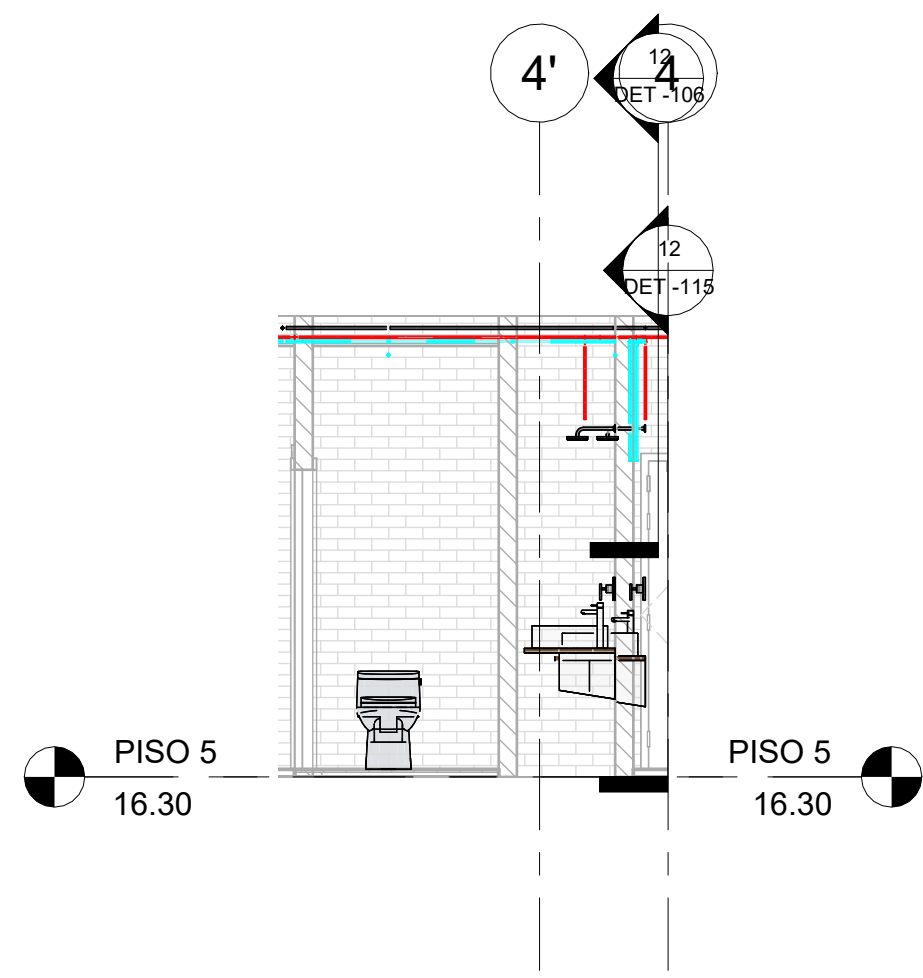

11 SEC_Long_CL_PISO 5 - HIDRAULICO_3
1 : 50

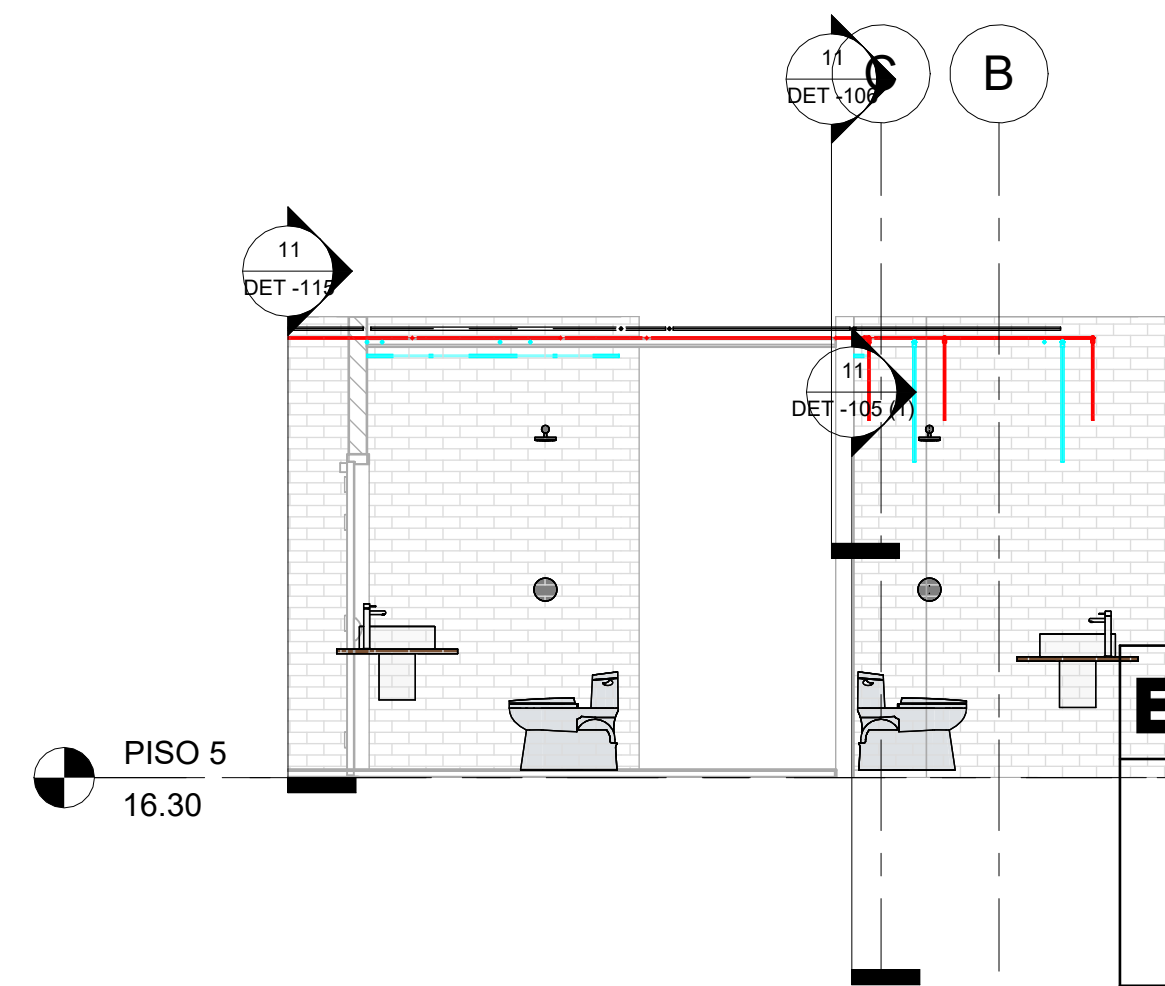

12 SEC_Trans_CL_PISO 5 - HIDRAULICO_3
1 : 50

EMCALI GERENCIA DE UEN ACUEDUCTO Y ALCANTARILLADO
UNIDAD DE INGENIERIA
PISO 5
FLORENTINO LIVING

DETALLE 15

PROYECTO	Designer	CALCULO:	Checker
DISEÑO	Author	DIBUJO:	Author
REVISOR:	Checker	REVISOR:	Checker
ESCALA:	1 : 50	APROBO:	Approver
FECHA:	SEPTIEMBRE 2025	ARCHIVO:	