




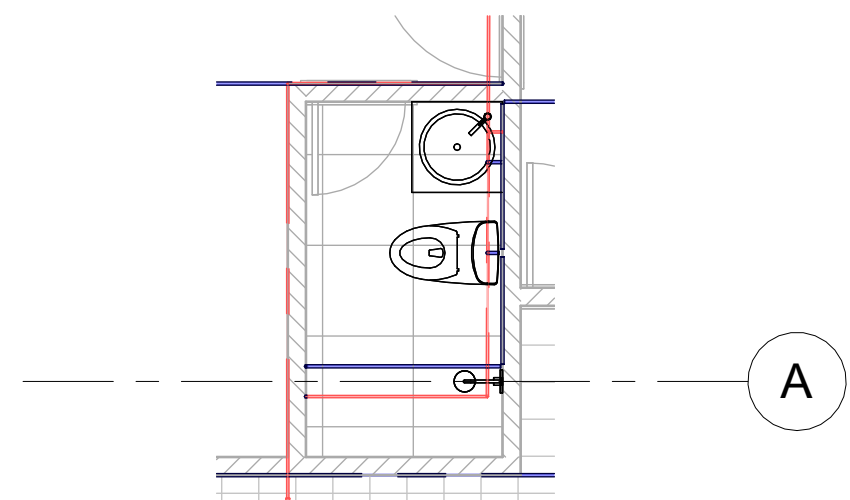


1 CL_PISO 7 - HIDRAULICO
1 : 50

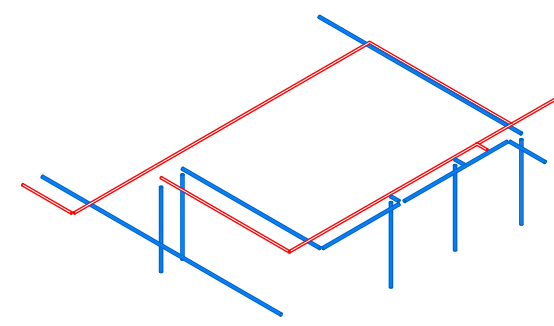


2 3D_CL_PISO 7 - HIDRAULICO

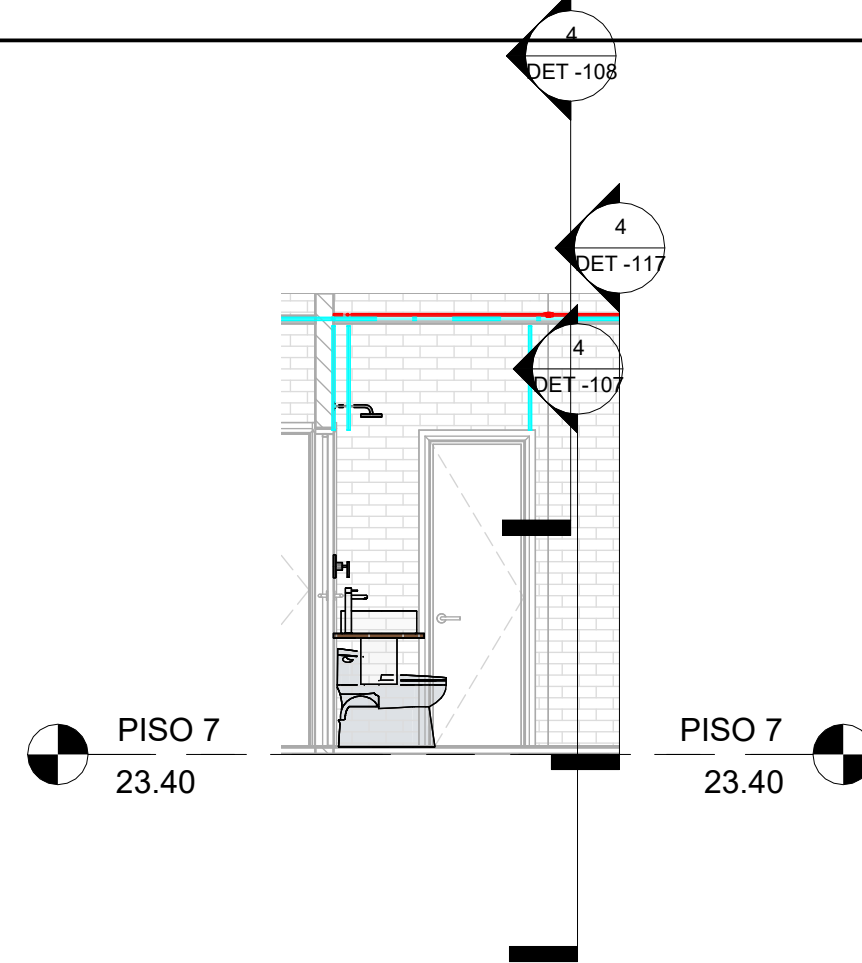


3 SEC_Long_CL_PISO 7 - HIDRAULICO
1 : 50

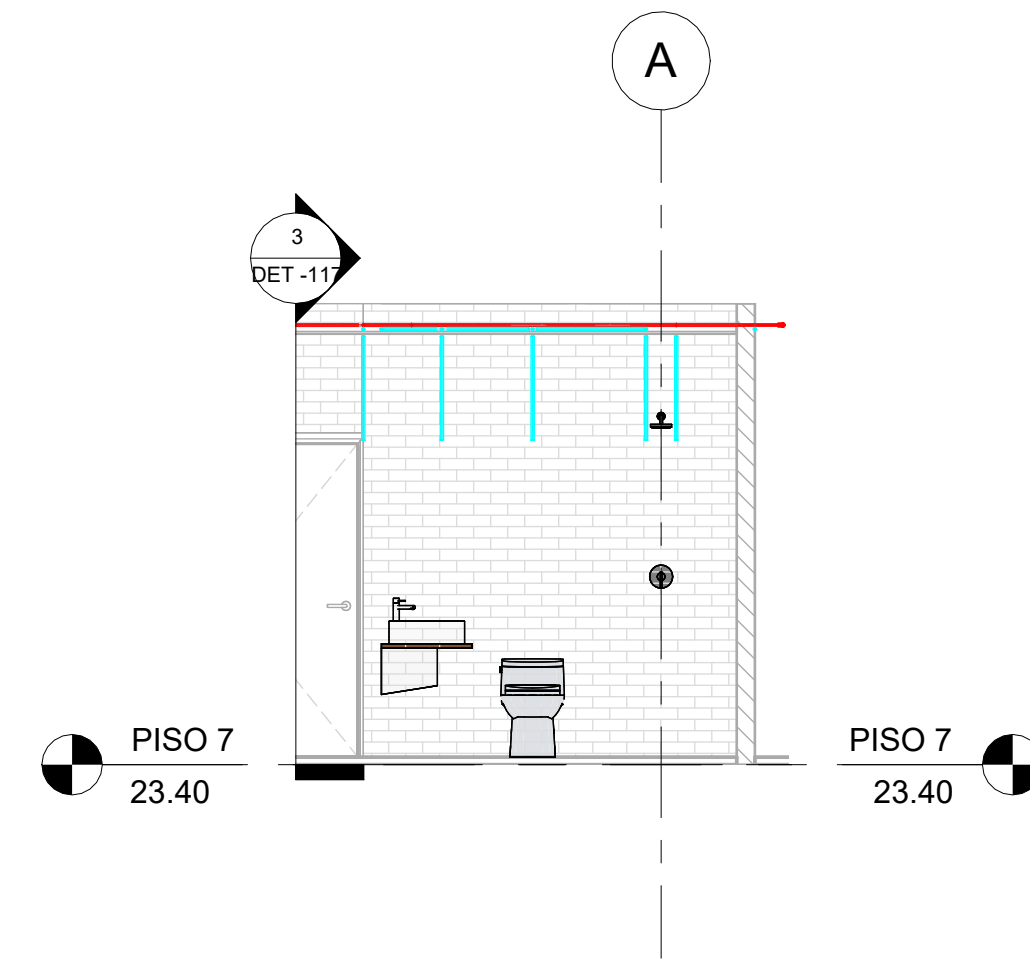


4 SEC_Trans_CL_PISO 7 - HIDRAULICO
1 : 50

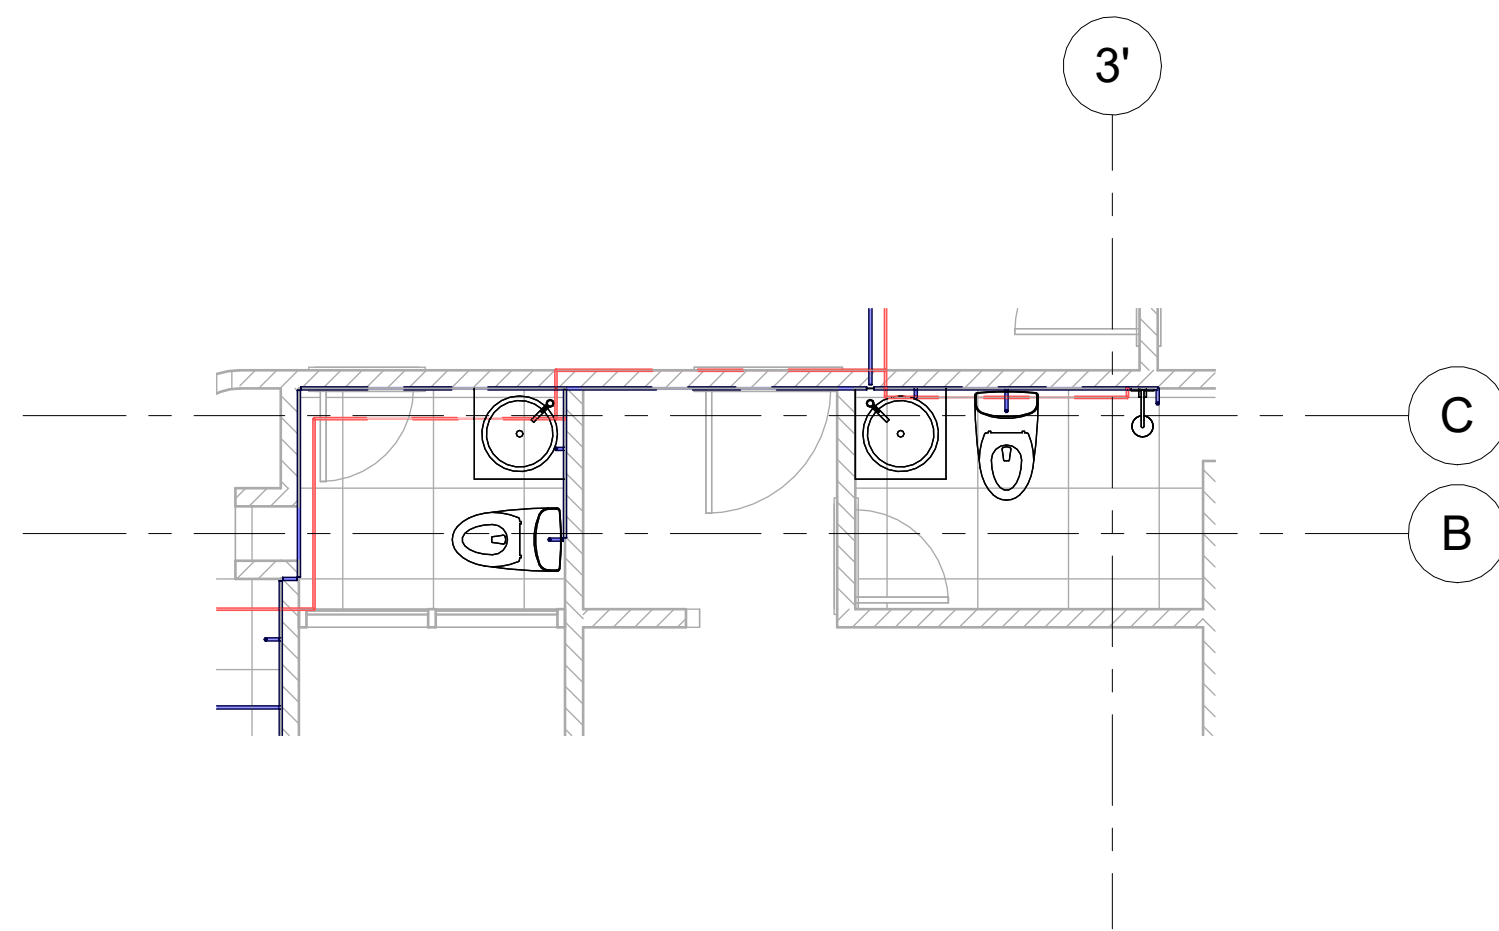


5 CL_PISO 7 - HIDRAULICO_2
1 : 50

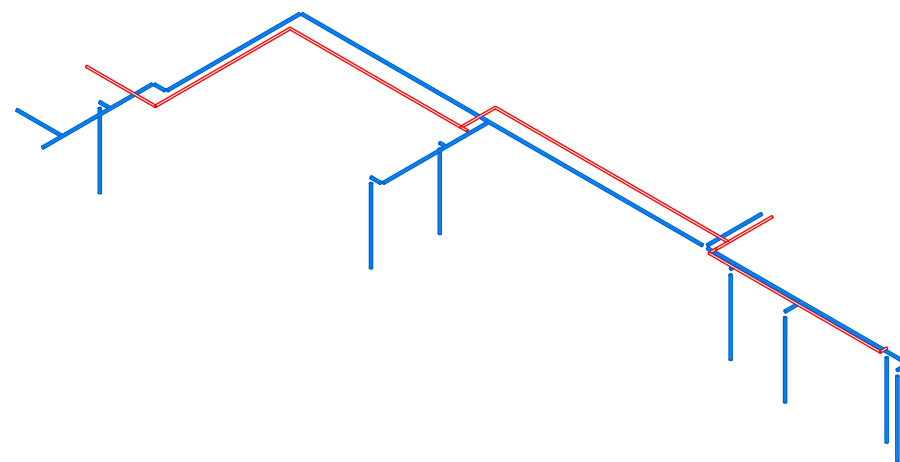


6 3D_CL_PISO 7 - HIDRAULICO_2

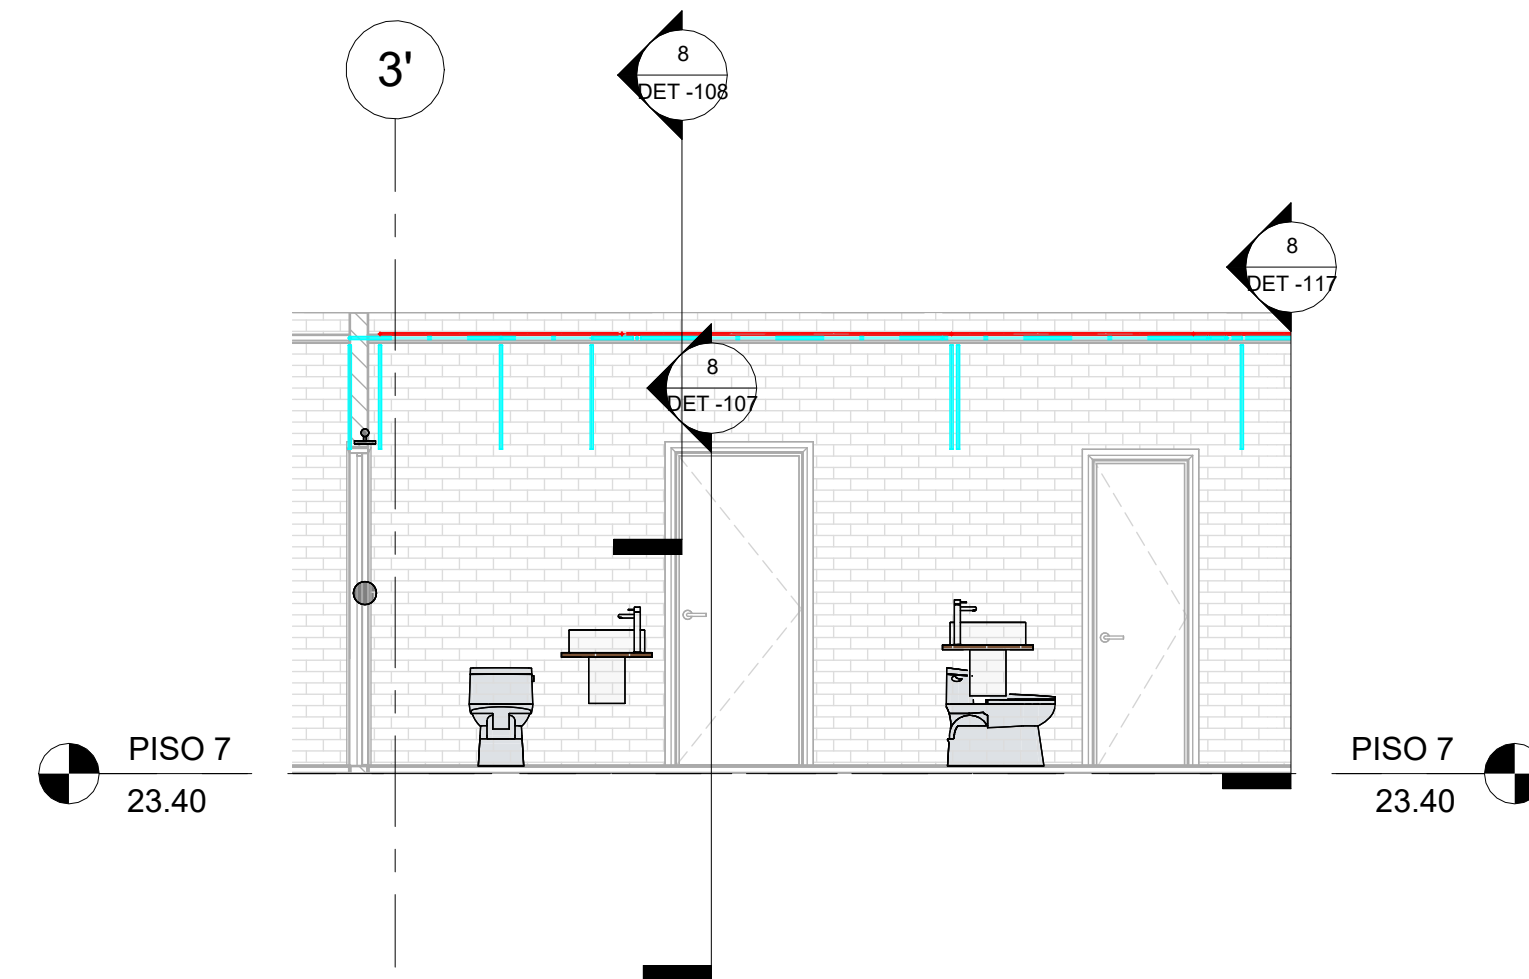


7 SEC_Long_CL_PISO 7 - HIDRAULICO_2
1 : 50

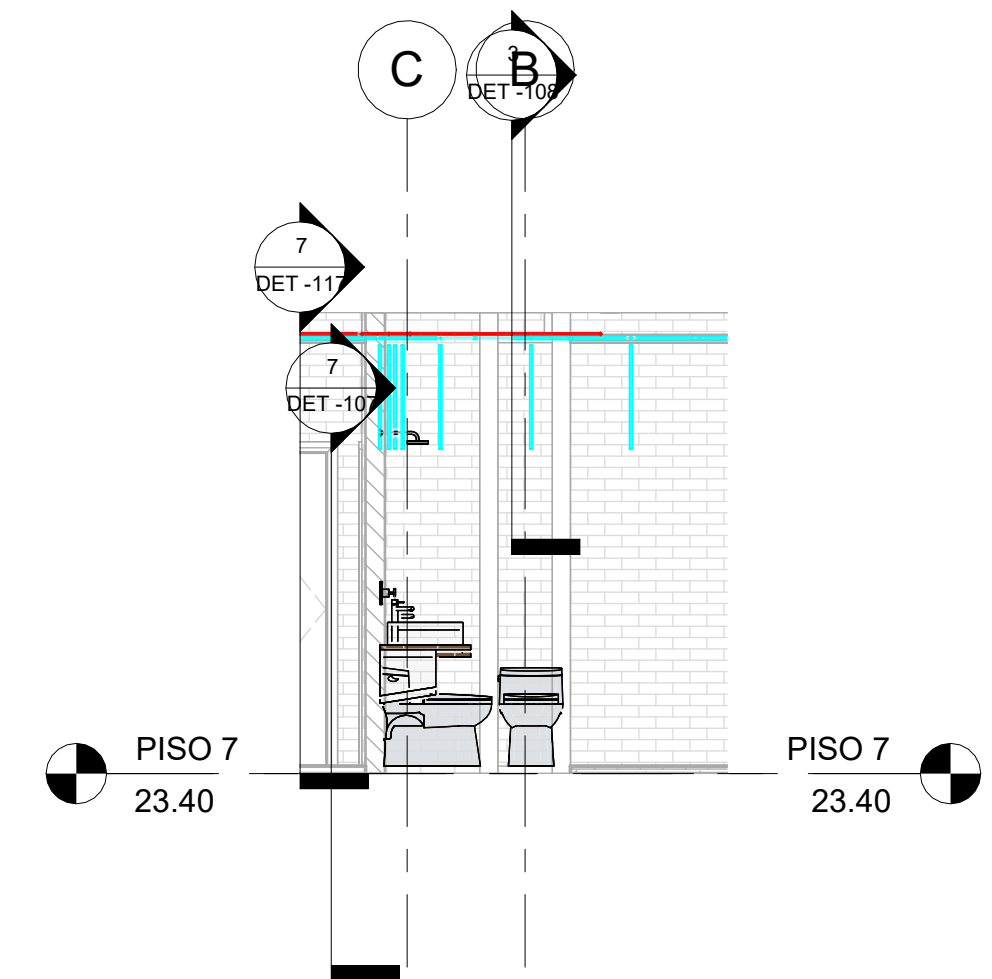


8 SEC_Trans_CL_PISO 7 - HIDRAULICO_2
1 : 50

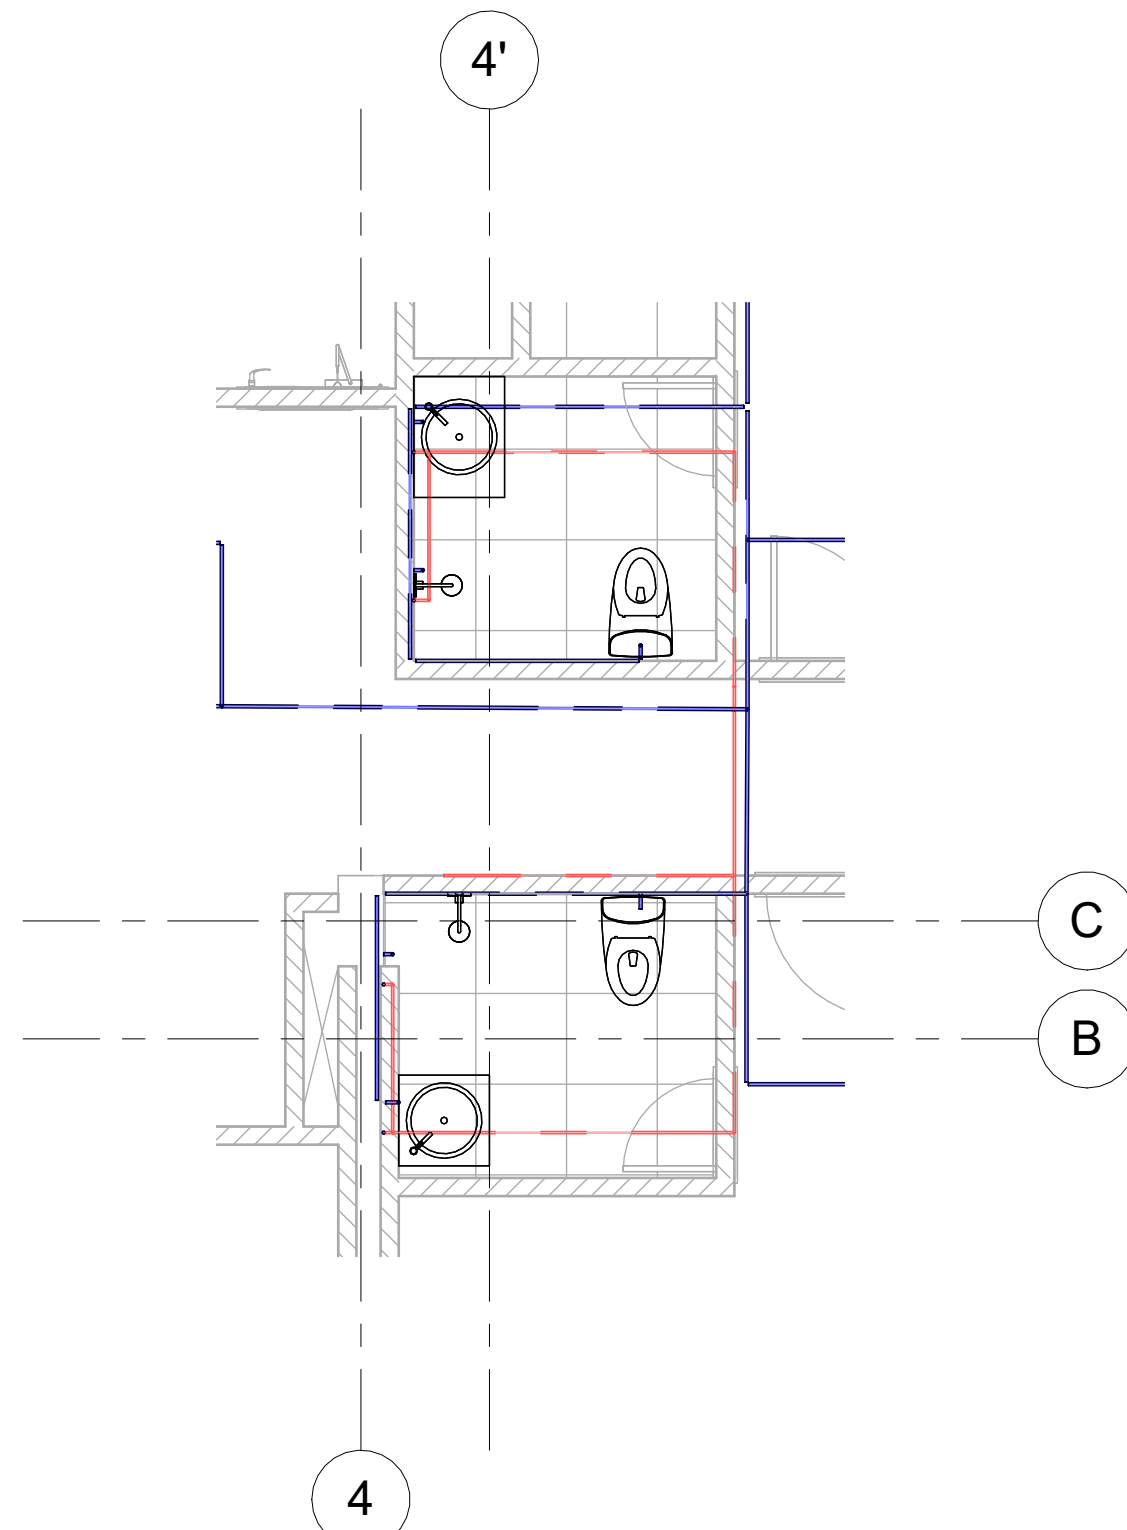


9 CL_PISO 7 - HIDRAULICO_3
1 : 50

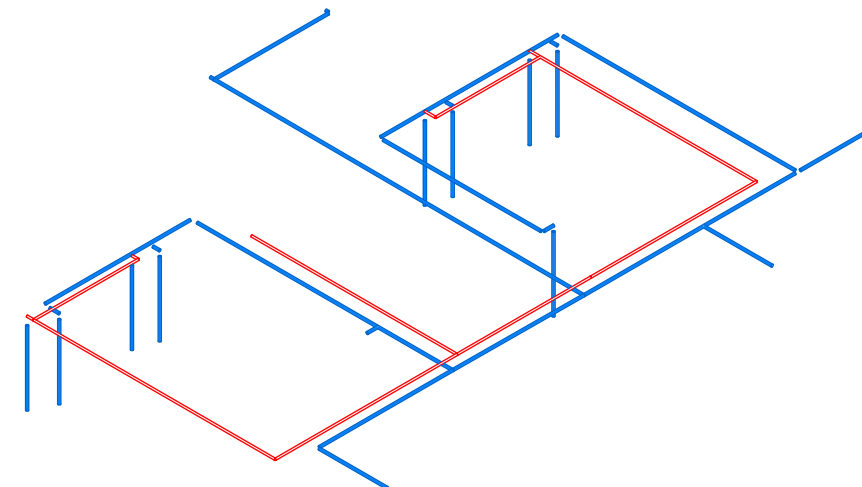

10 3D_CL_PISO 7 - HIDRAULICO_3

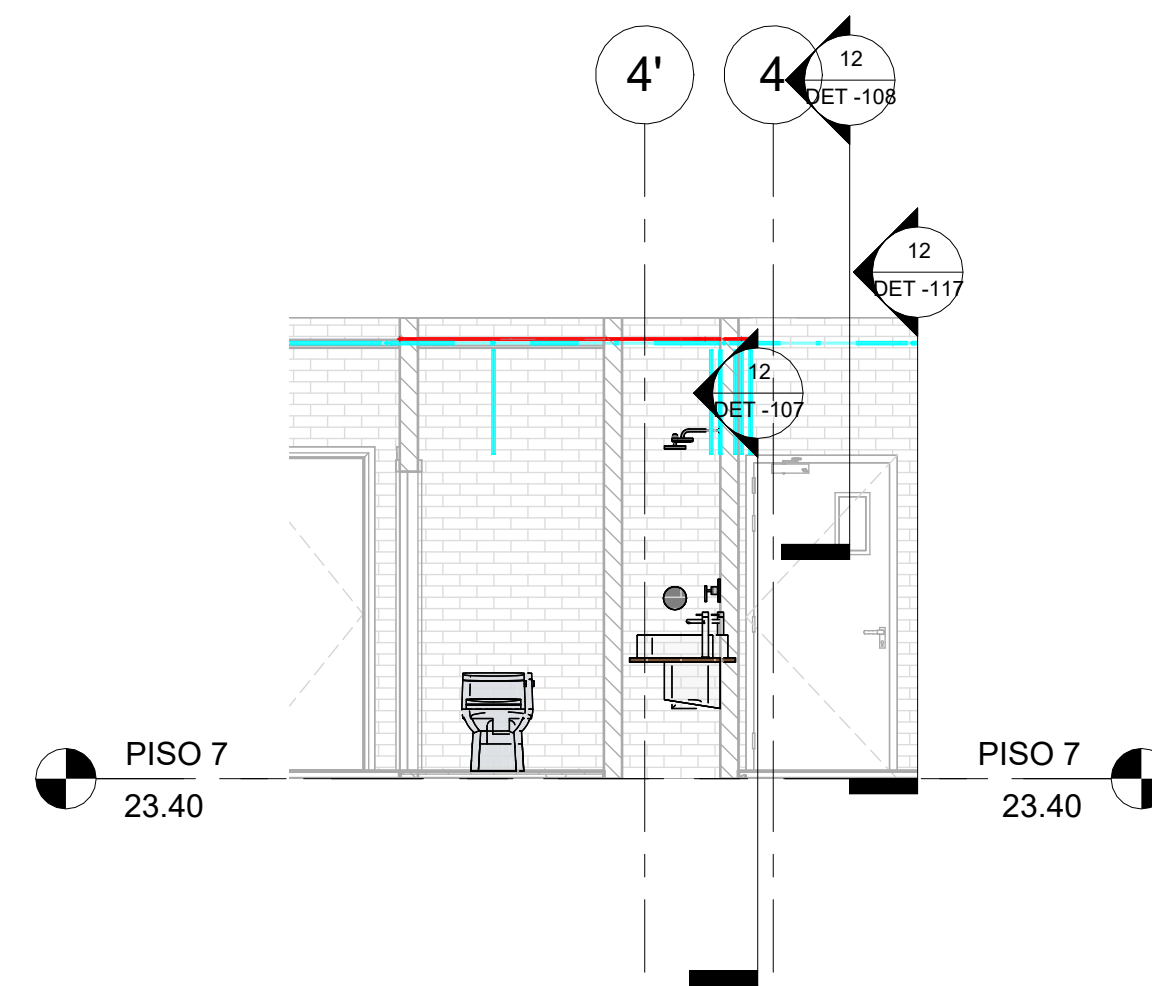

11 SEC_Long_CL_PISO 7 - HIDRAULICO_3
1 : 50

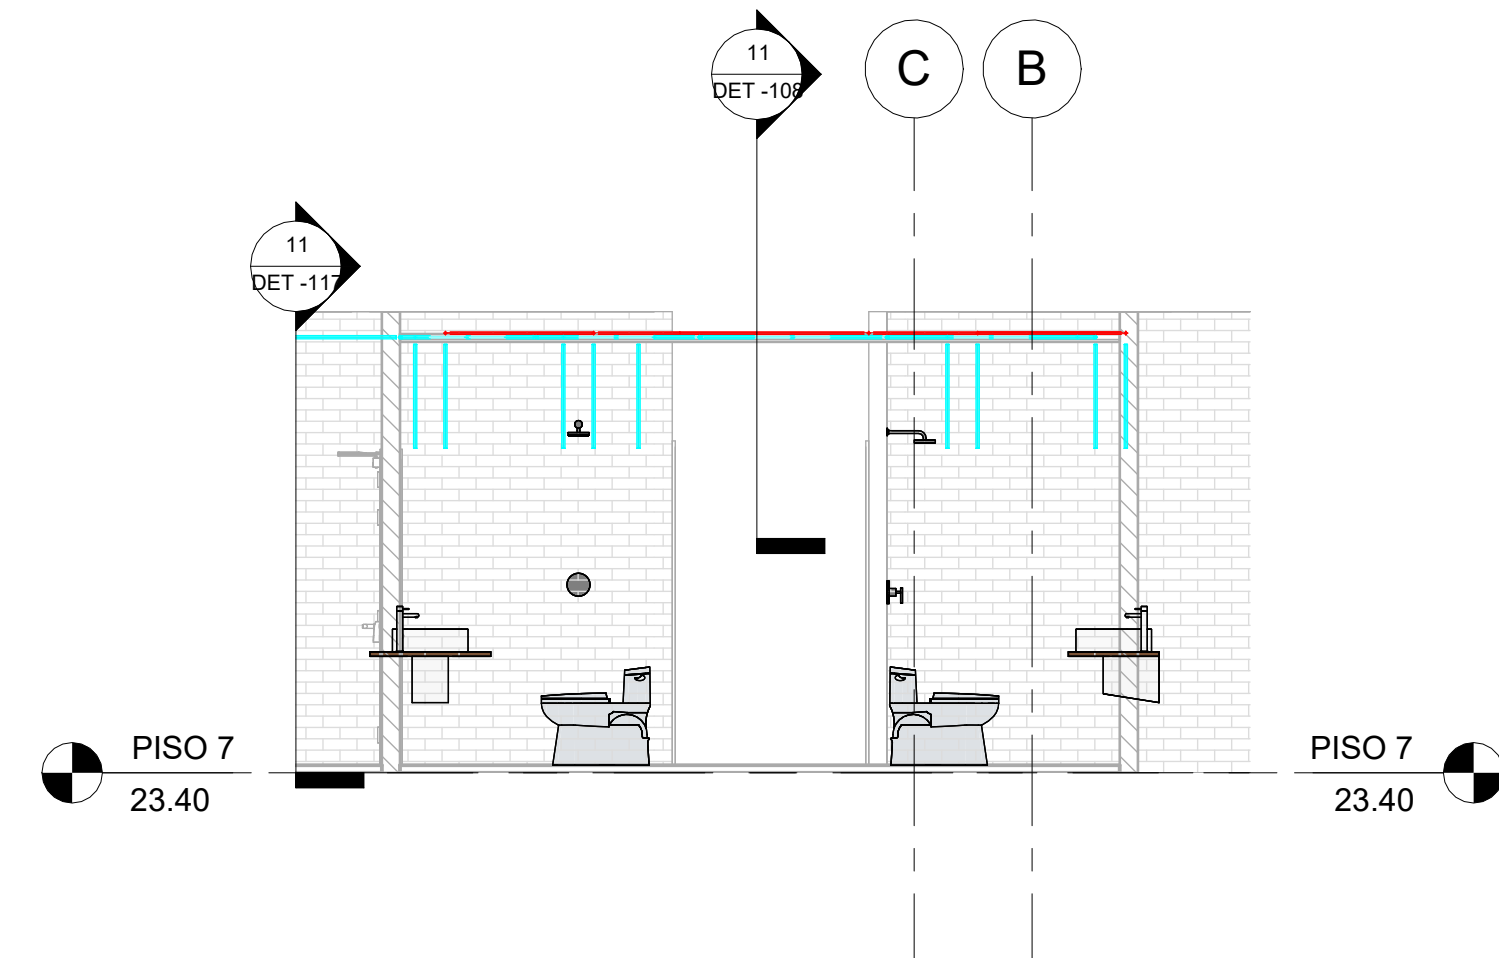

12 SEC_Trans_CL_PISO 7 - HIDRAULICO_3
1 : 50

EMCALI GERENCIA DE UEN ACUEDUCTO Y ALCANTARILLADO UNIDAD DE INGENIERIA	
FLORENTINO LIVING	
DETALLE 17	
PROYECTO Designer	CALCULO: Checker
PRESUPUESTO No.	DIBUJO: Author
REVISO: Checker	APROBO: Approver
FECHA: SEPTIEMBRE 2025	ARCHIVO:

FECHA	REVISIONES	REVISO	APROBO