




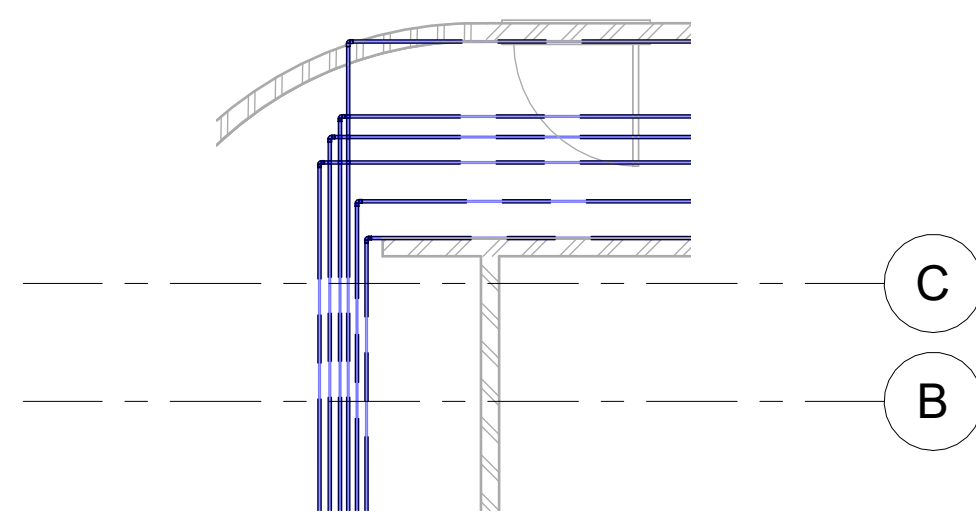


1 CL_SOTANO - HIDRAULICO
1 : 50

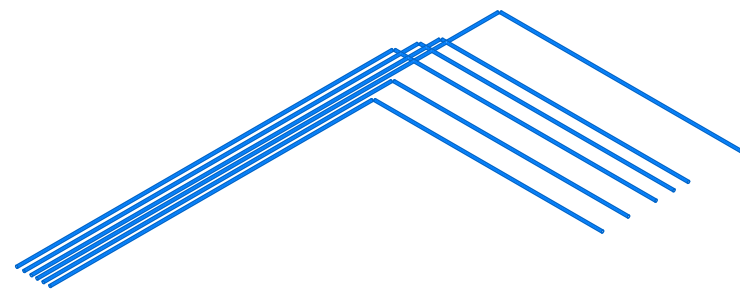


2 3D_CL_SOTANO - HIDRAULICO

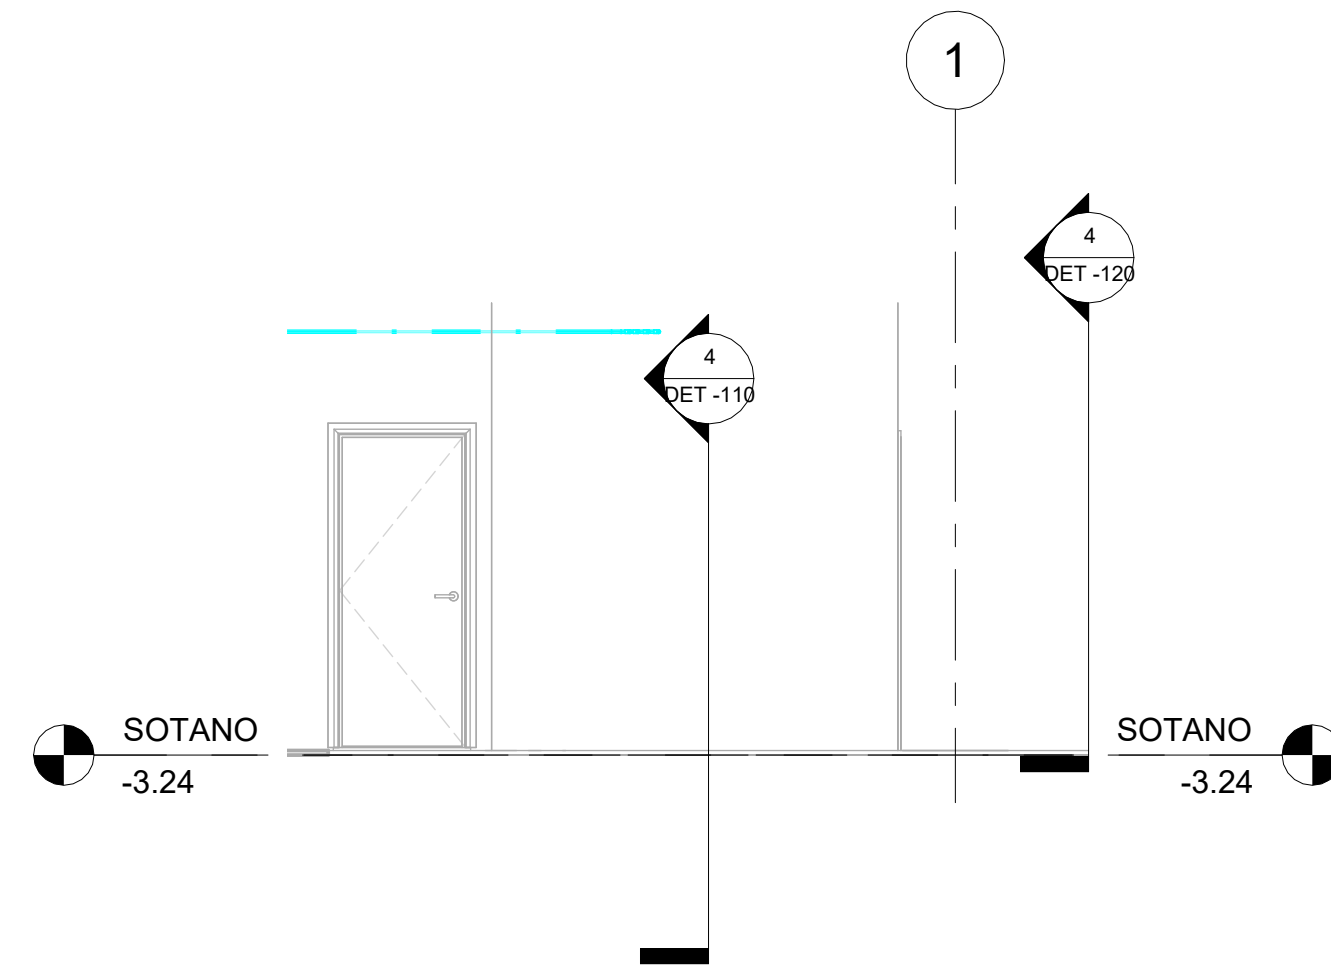


3 SEC_Long_CL_SOTANO - HIDRAULICO
1 : 50

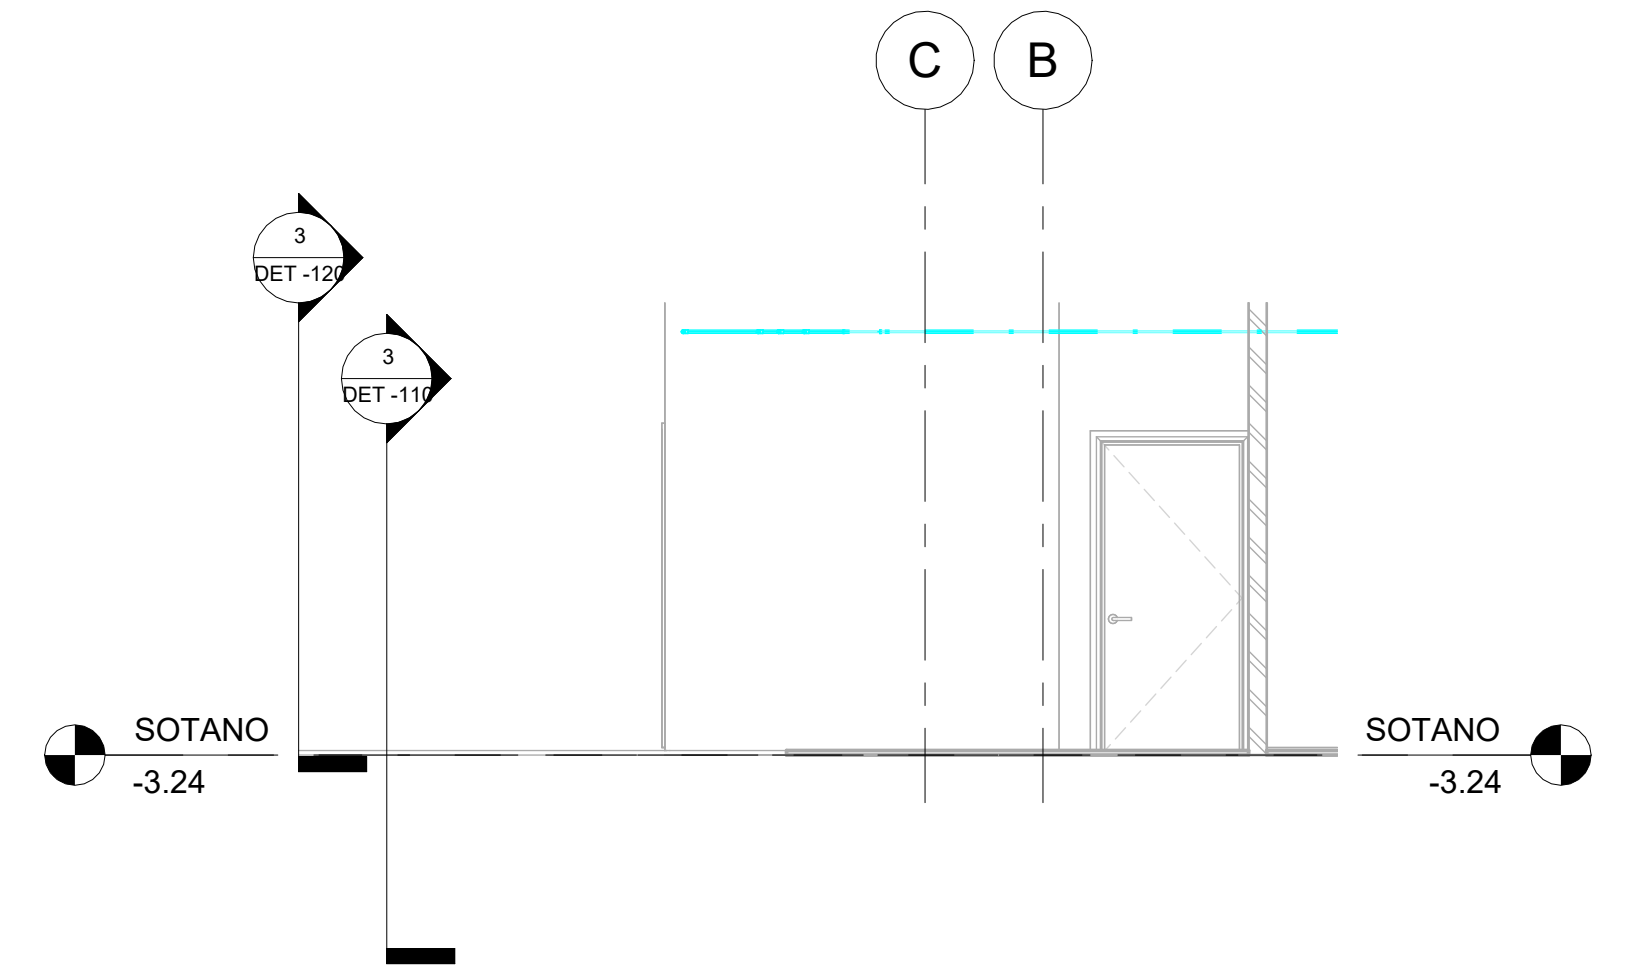


4 SEC_Trans_CL_SOTANO - HIDRAULICO
1 : 50

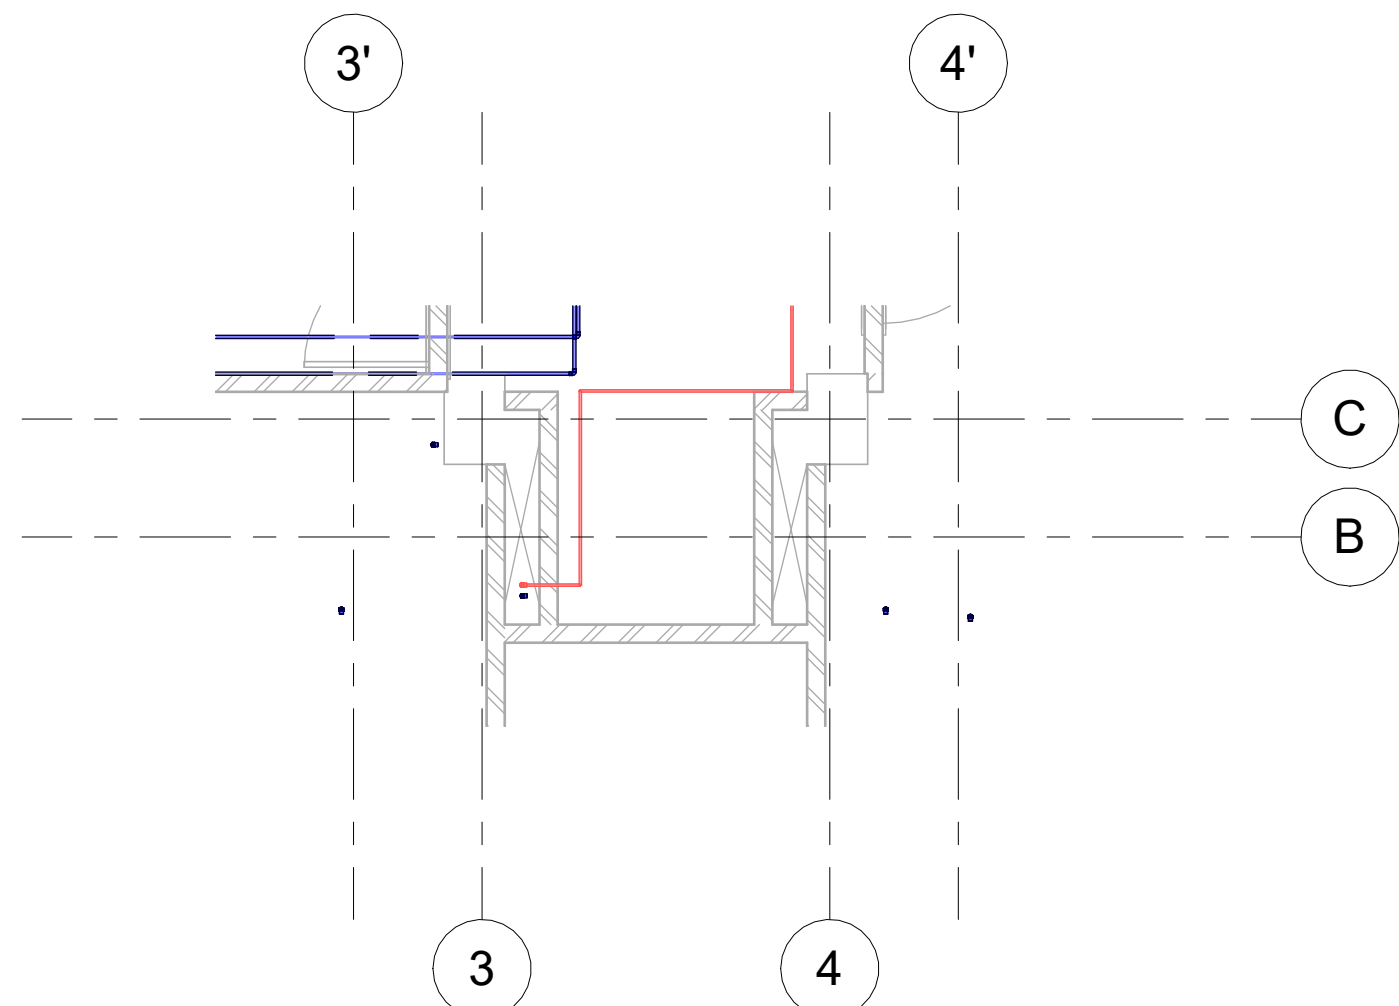


5 CL_SOTANO - HIDRAULICO_2
1 : 50

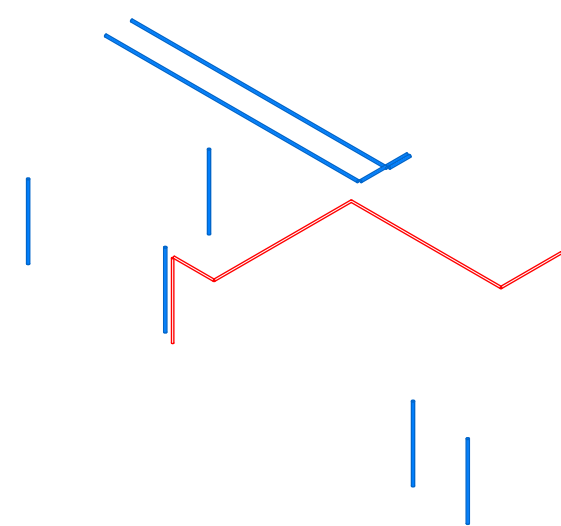


6 3D_CL_SOTANO - HIDRAULICO_2

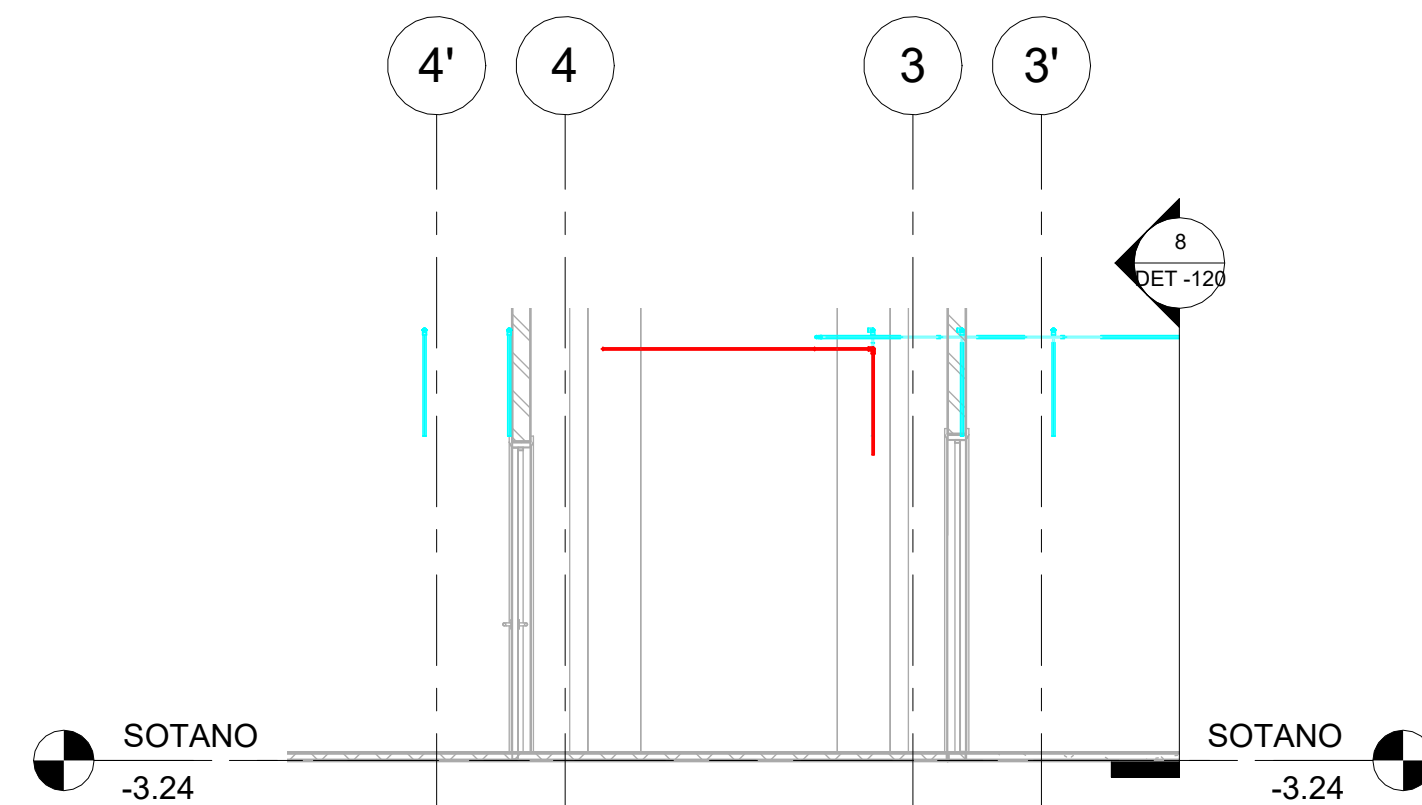


7 SEC_Long_CL_SOTANO - HIDRAULICO_2
1 : 50

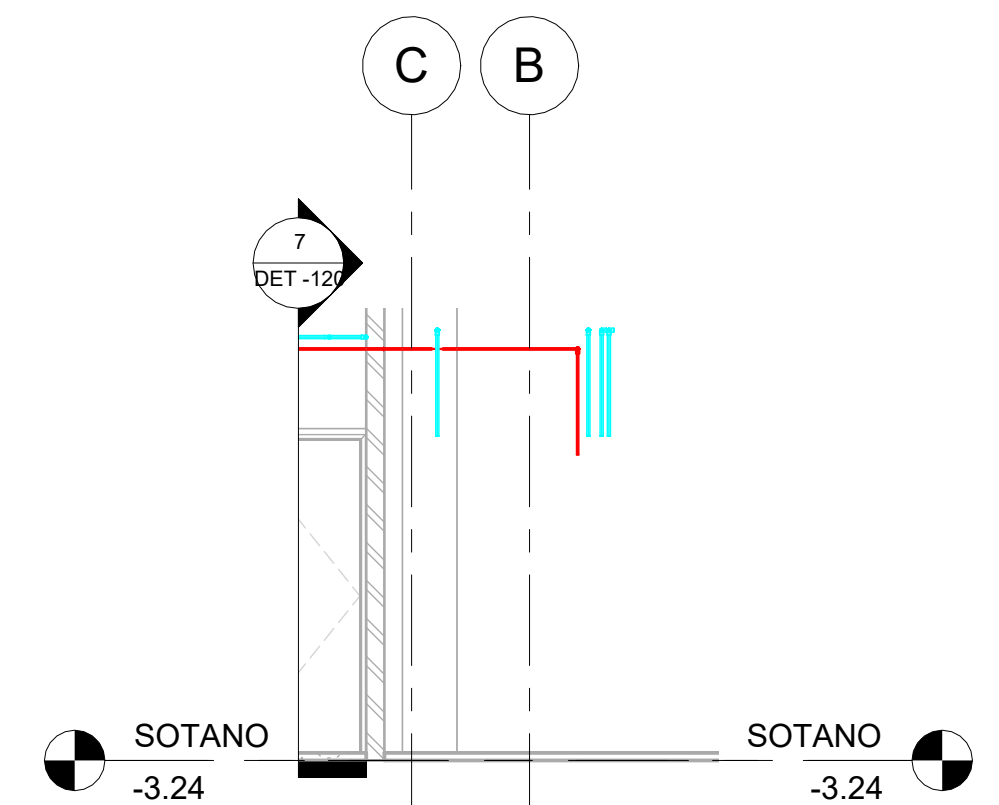


8 SEC_Trans_CL_SOTANO - HIDRAULICO_2
1 : 50

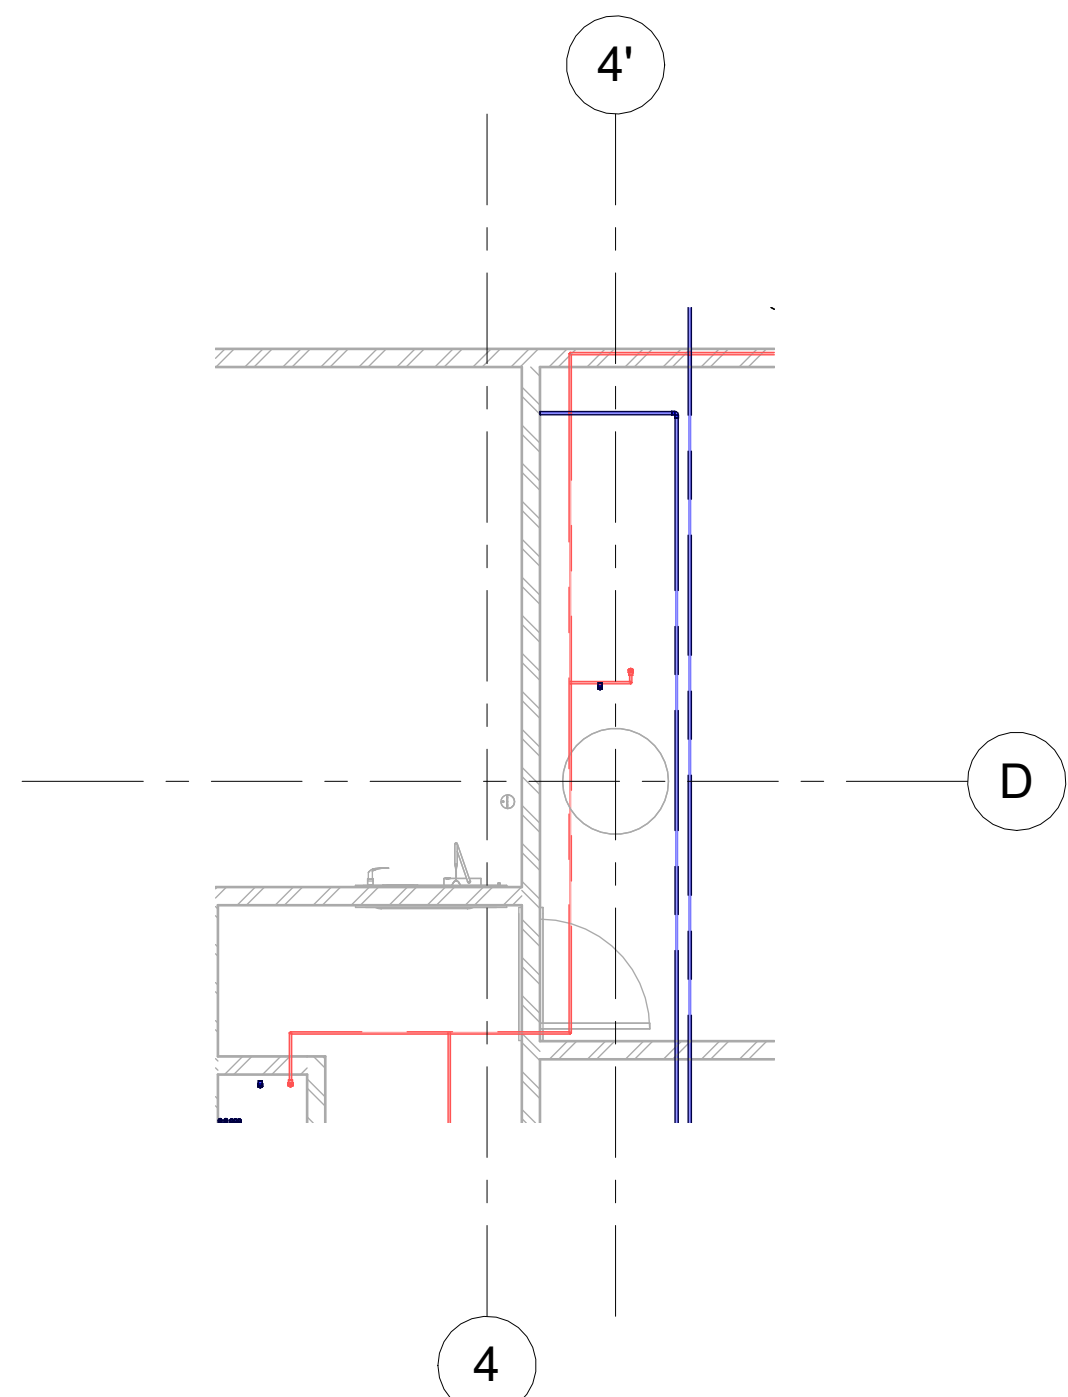


9 CL_SOTANO - HIDRAULICO_3
1 : 50

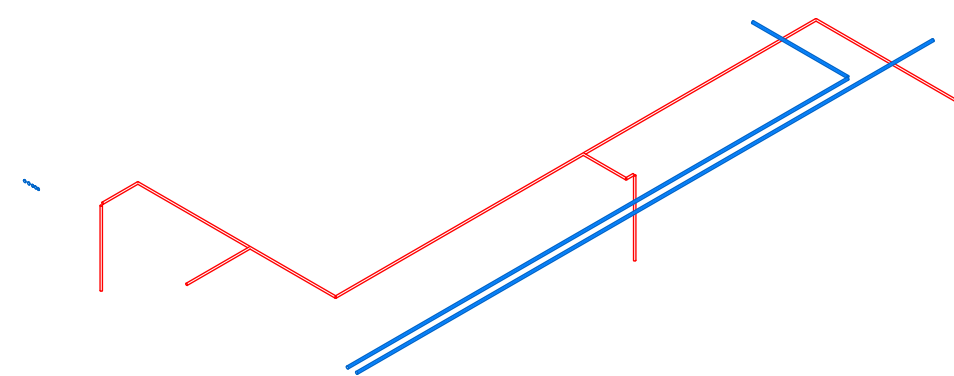

10 3D_CL_SOTANO - HIDRAULICO_3

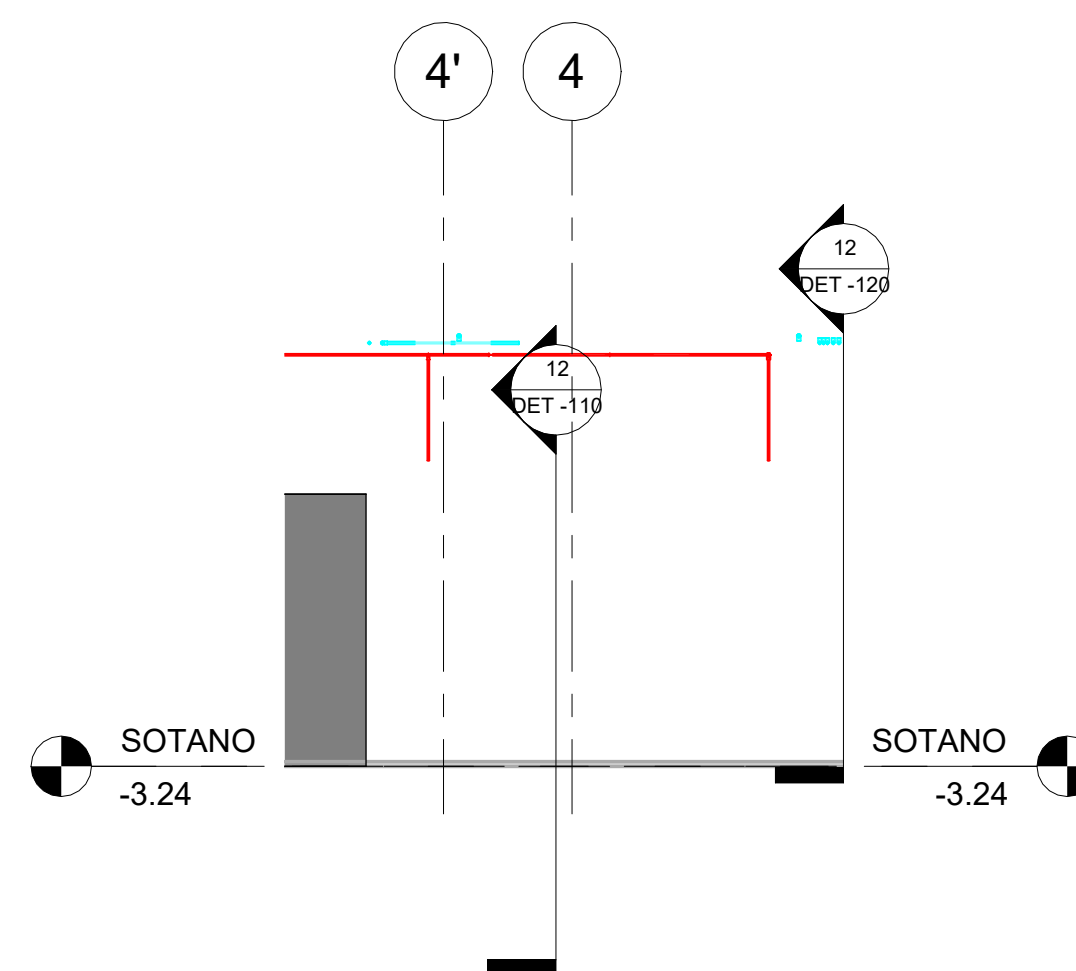

11 SEC_Long_CL_SOTANO - HIDRAULICO_3
1 : 50

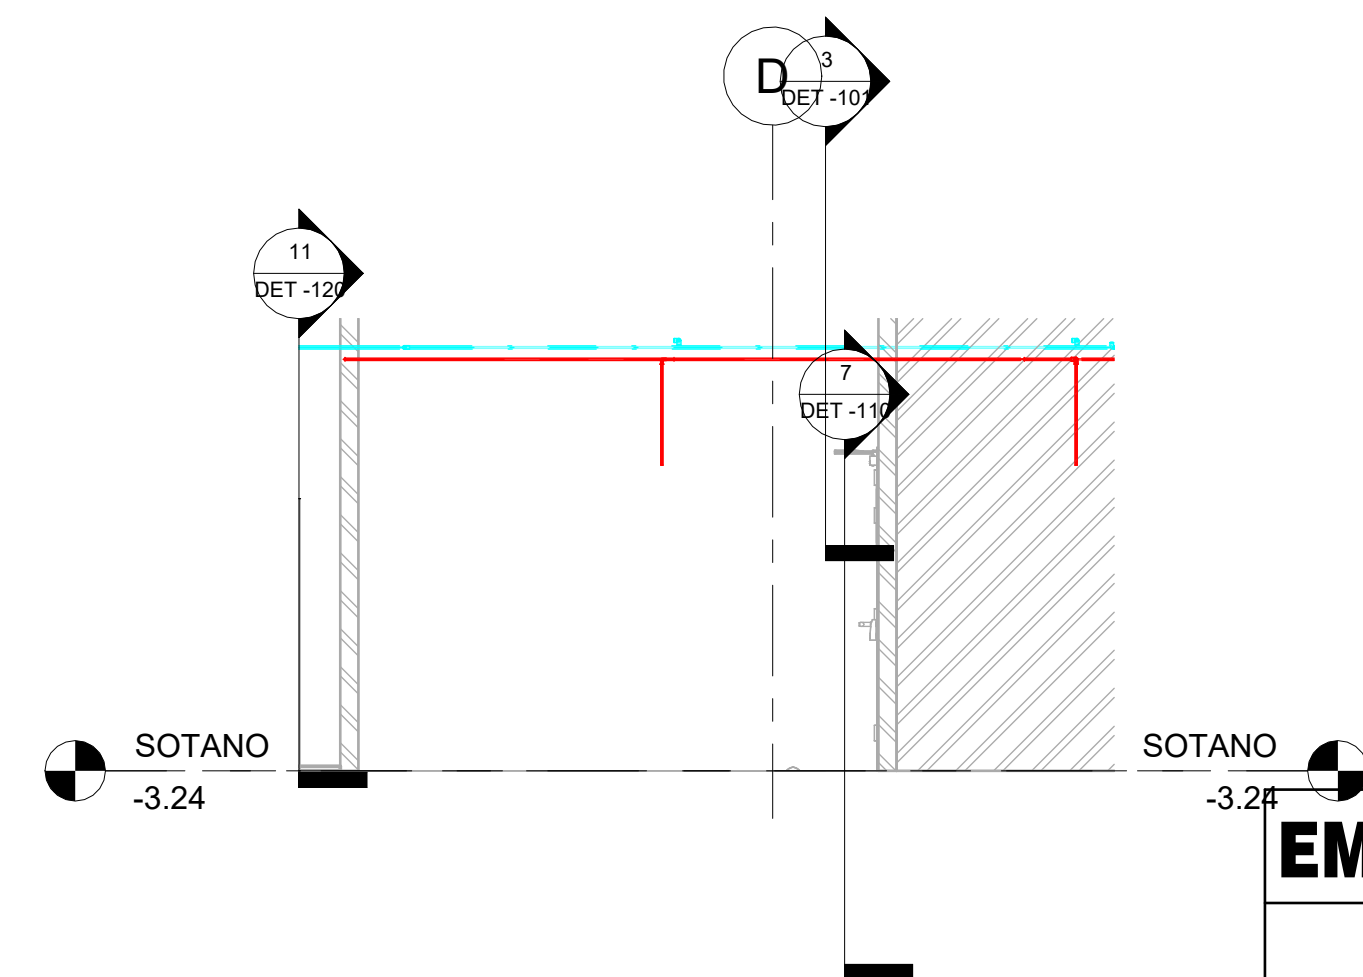

12 SEC_Trans_CL_SOTANO - HIDRAULICO_3
1 : 50

EMCALI GERENCIA DE UEN ACUEDUCTO Y ALCANTARILLADO
UNIDAD DE INGENIERIA

FLORENTINO LIVING

DETALLE 20

PROYECTO		CALCULO:	
DESIGNER		CHECKER	
PRESUPUESTO No.		REVISOR:	
		APPROVER	
FECHA		REVISIONES	
		APROBÓ	