


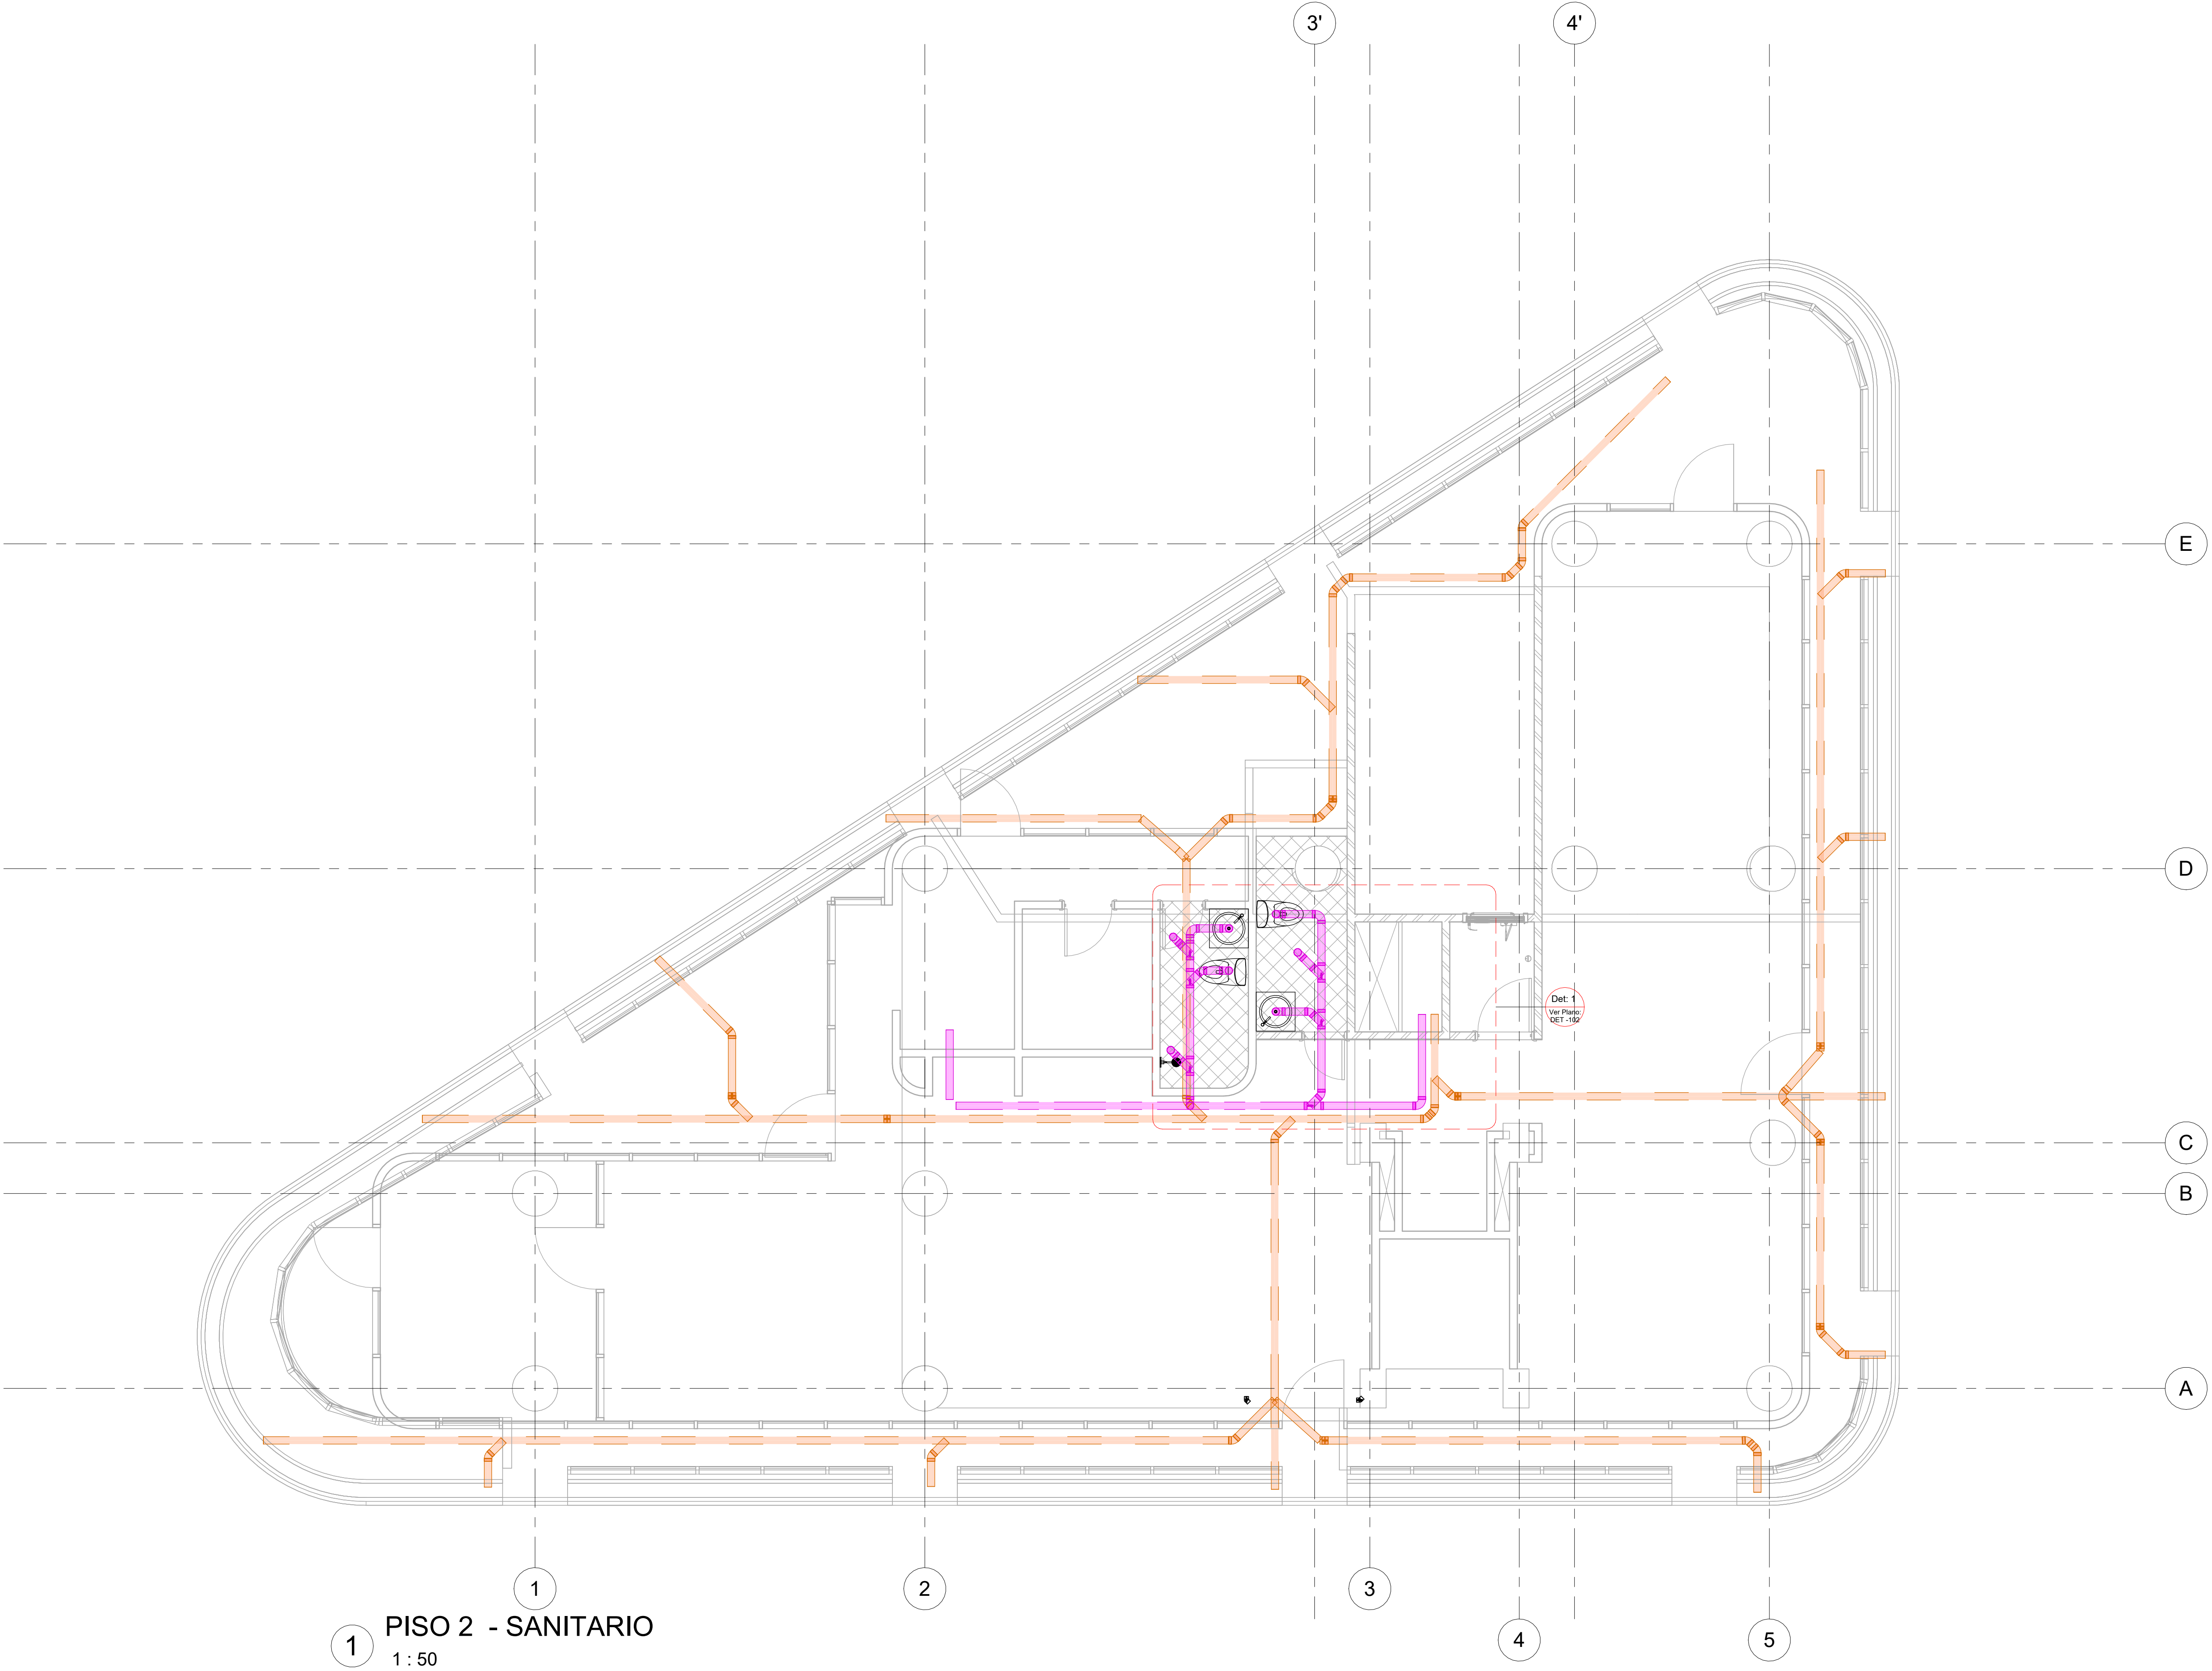

1

1

PISO 2 - SANITARIO

1 : 50

EMCALI

GERENCIA DE UEN ACUEDUCTO Y ALCANTARILLADO

UNIDAD DE INGENIERIA

FLORENTINO LIVING

PISO 2 – SANITARIO

PROYECTO	Designer	CALCULO:	Checker
PRESUPUESTO No.		DIBUJO:	Author
		REVISO:	Checker
ESCALA:	1 : 50	APROBO:	Approver
FECHA:	SEPTIEMBRE 2025	ARCHIVO:	

FECHA	REVISIONES	REVISO	APROBO