


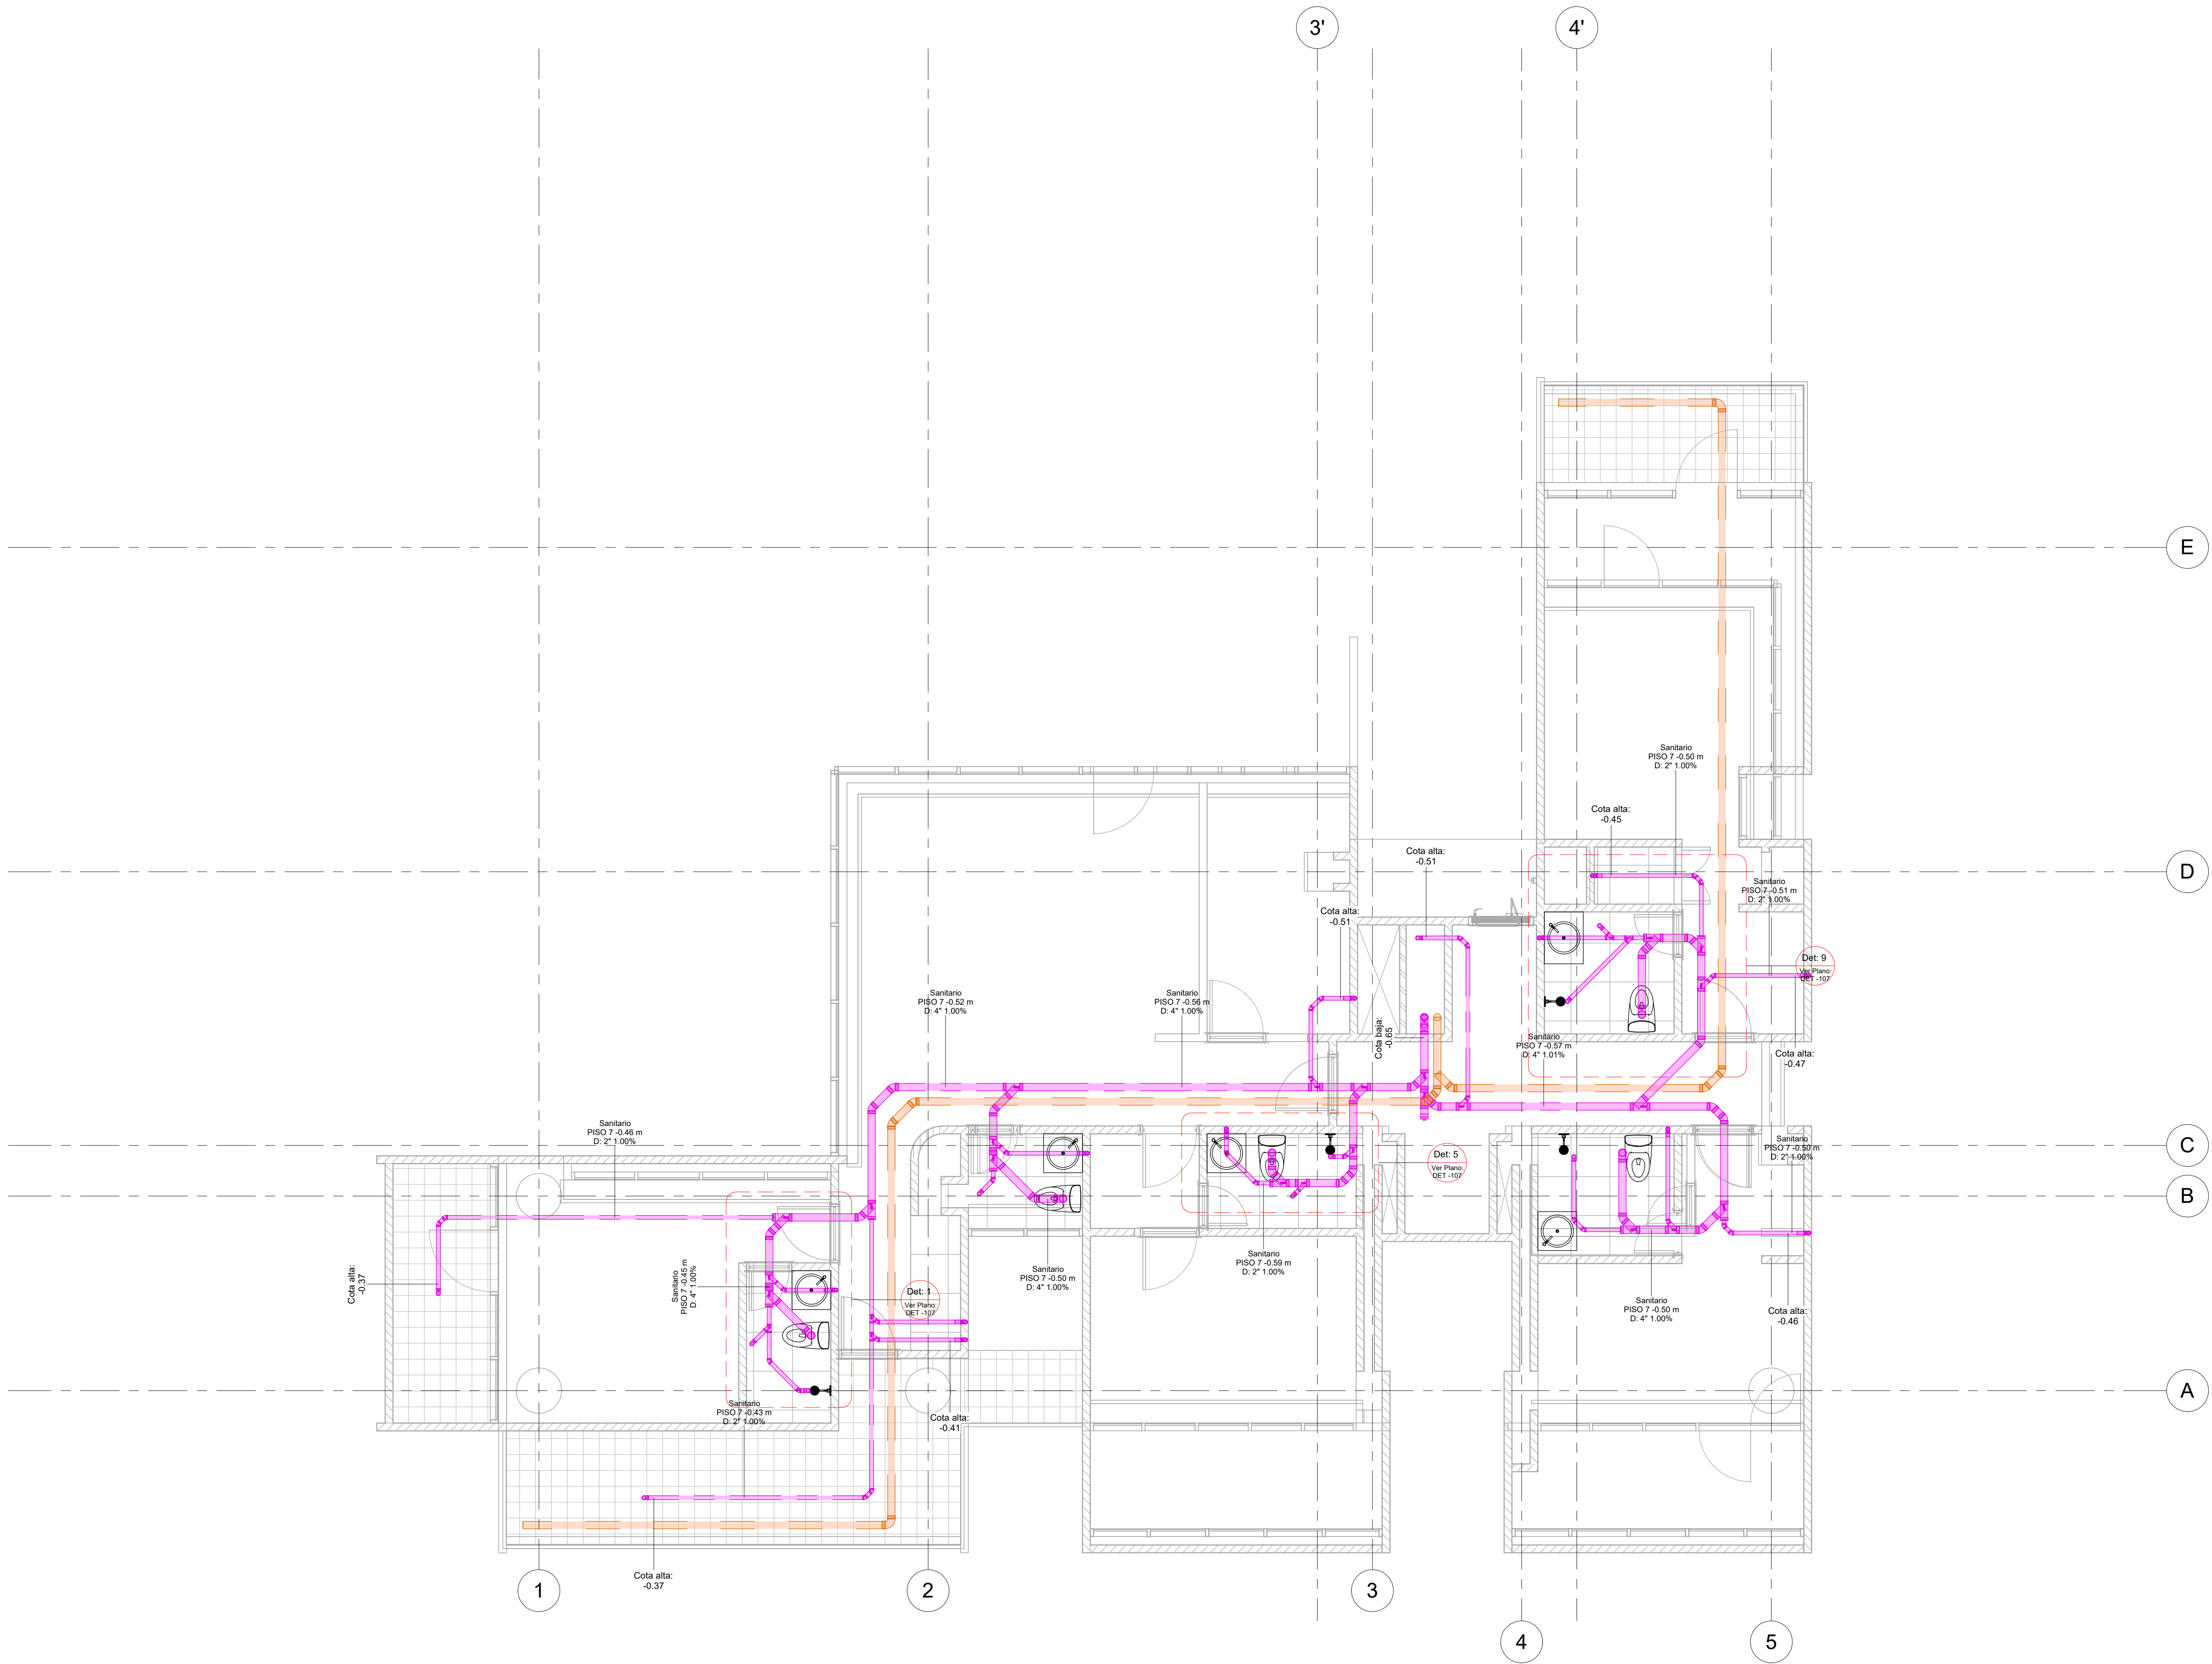

1

PISO 7 - SANITARIO

1 : 50

EMCALI GERENCIA DE UEN ACUEDUCTO Y ALCANTARILLADO UNIDAD DE INGENIERIA			
FLORENTINO LIVING			
PISO 7 – SANITARIO			
PROYECTO	Designer	CALCULO:	Checker
PRESUPUESTO No.		DIBUJO:	Author
		REVISO:	Checker
ESCALA:	1 : 50	APROBO:	Approver
FECHA:	SEPTIEMBRE 2025	ARCHIVO:	

FECHA	REVISIONES	REVISO	APROBO