


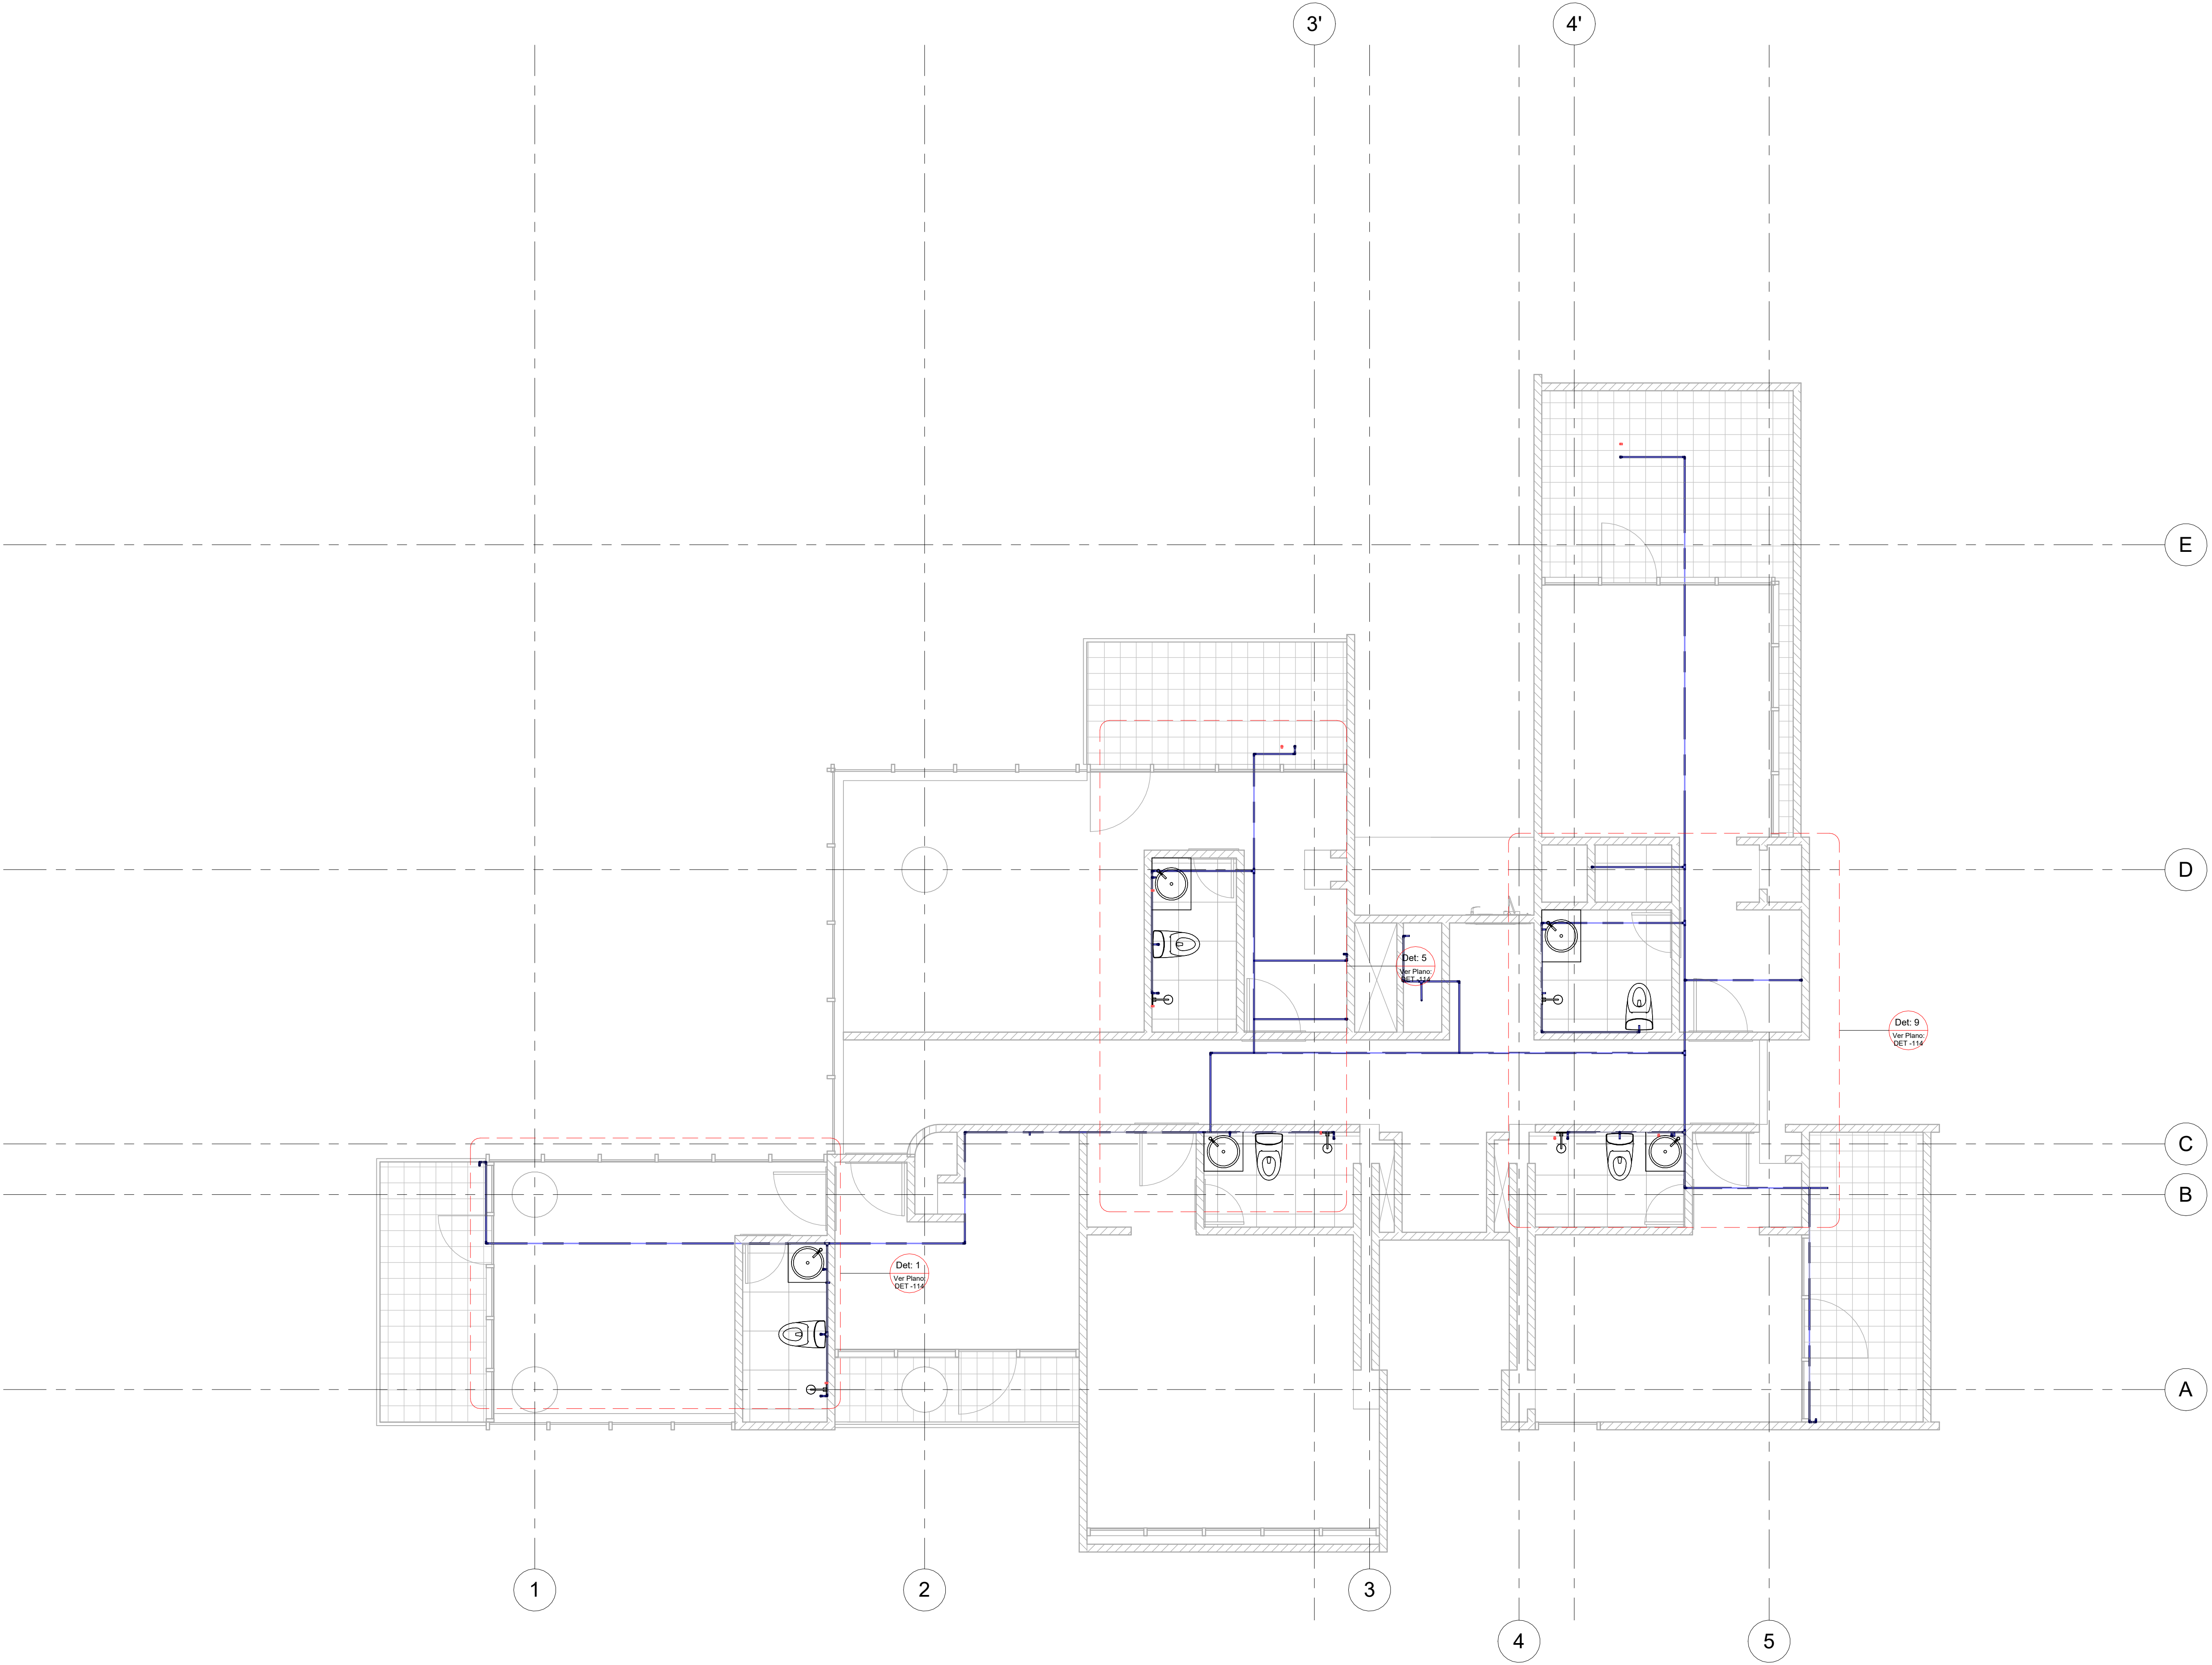

1 PISO 4 - HIDRAULICO
1 : 50

FECHA	REVISIONES	REVISÓ	APROBÓ

EMCALI GERENCIA DE UEN ACUEDUCTO Y ALCANTARILLADO UNIDAD DE INGENIERIA			
FLORENTINO LIVING			
PISO 4 – HIDRAULICO			
PROYECTO Designer		CALCULO:	Checker
PRESUPUESTO No.		DIBUJO:	Author
		REVISO:	Checker
ESCALA: 1 : 50		APROBO:	Approver
FECHA: SEPTIEMBRE 2025		ARCHIVO:	