


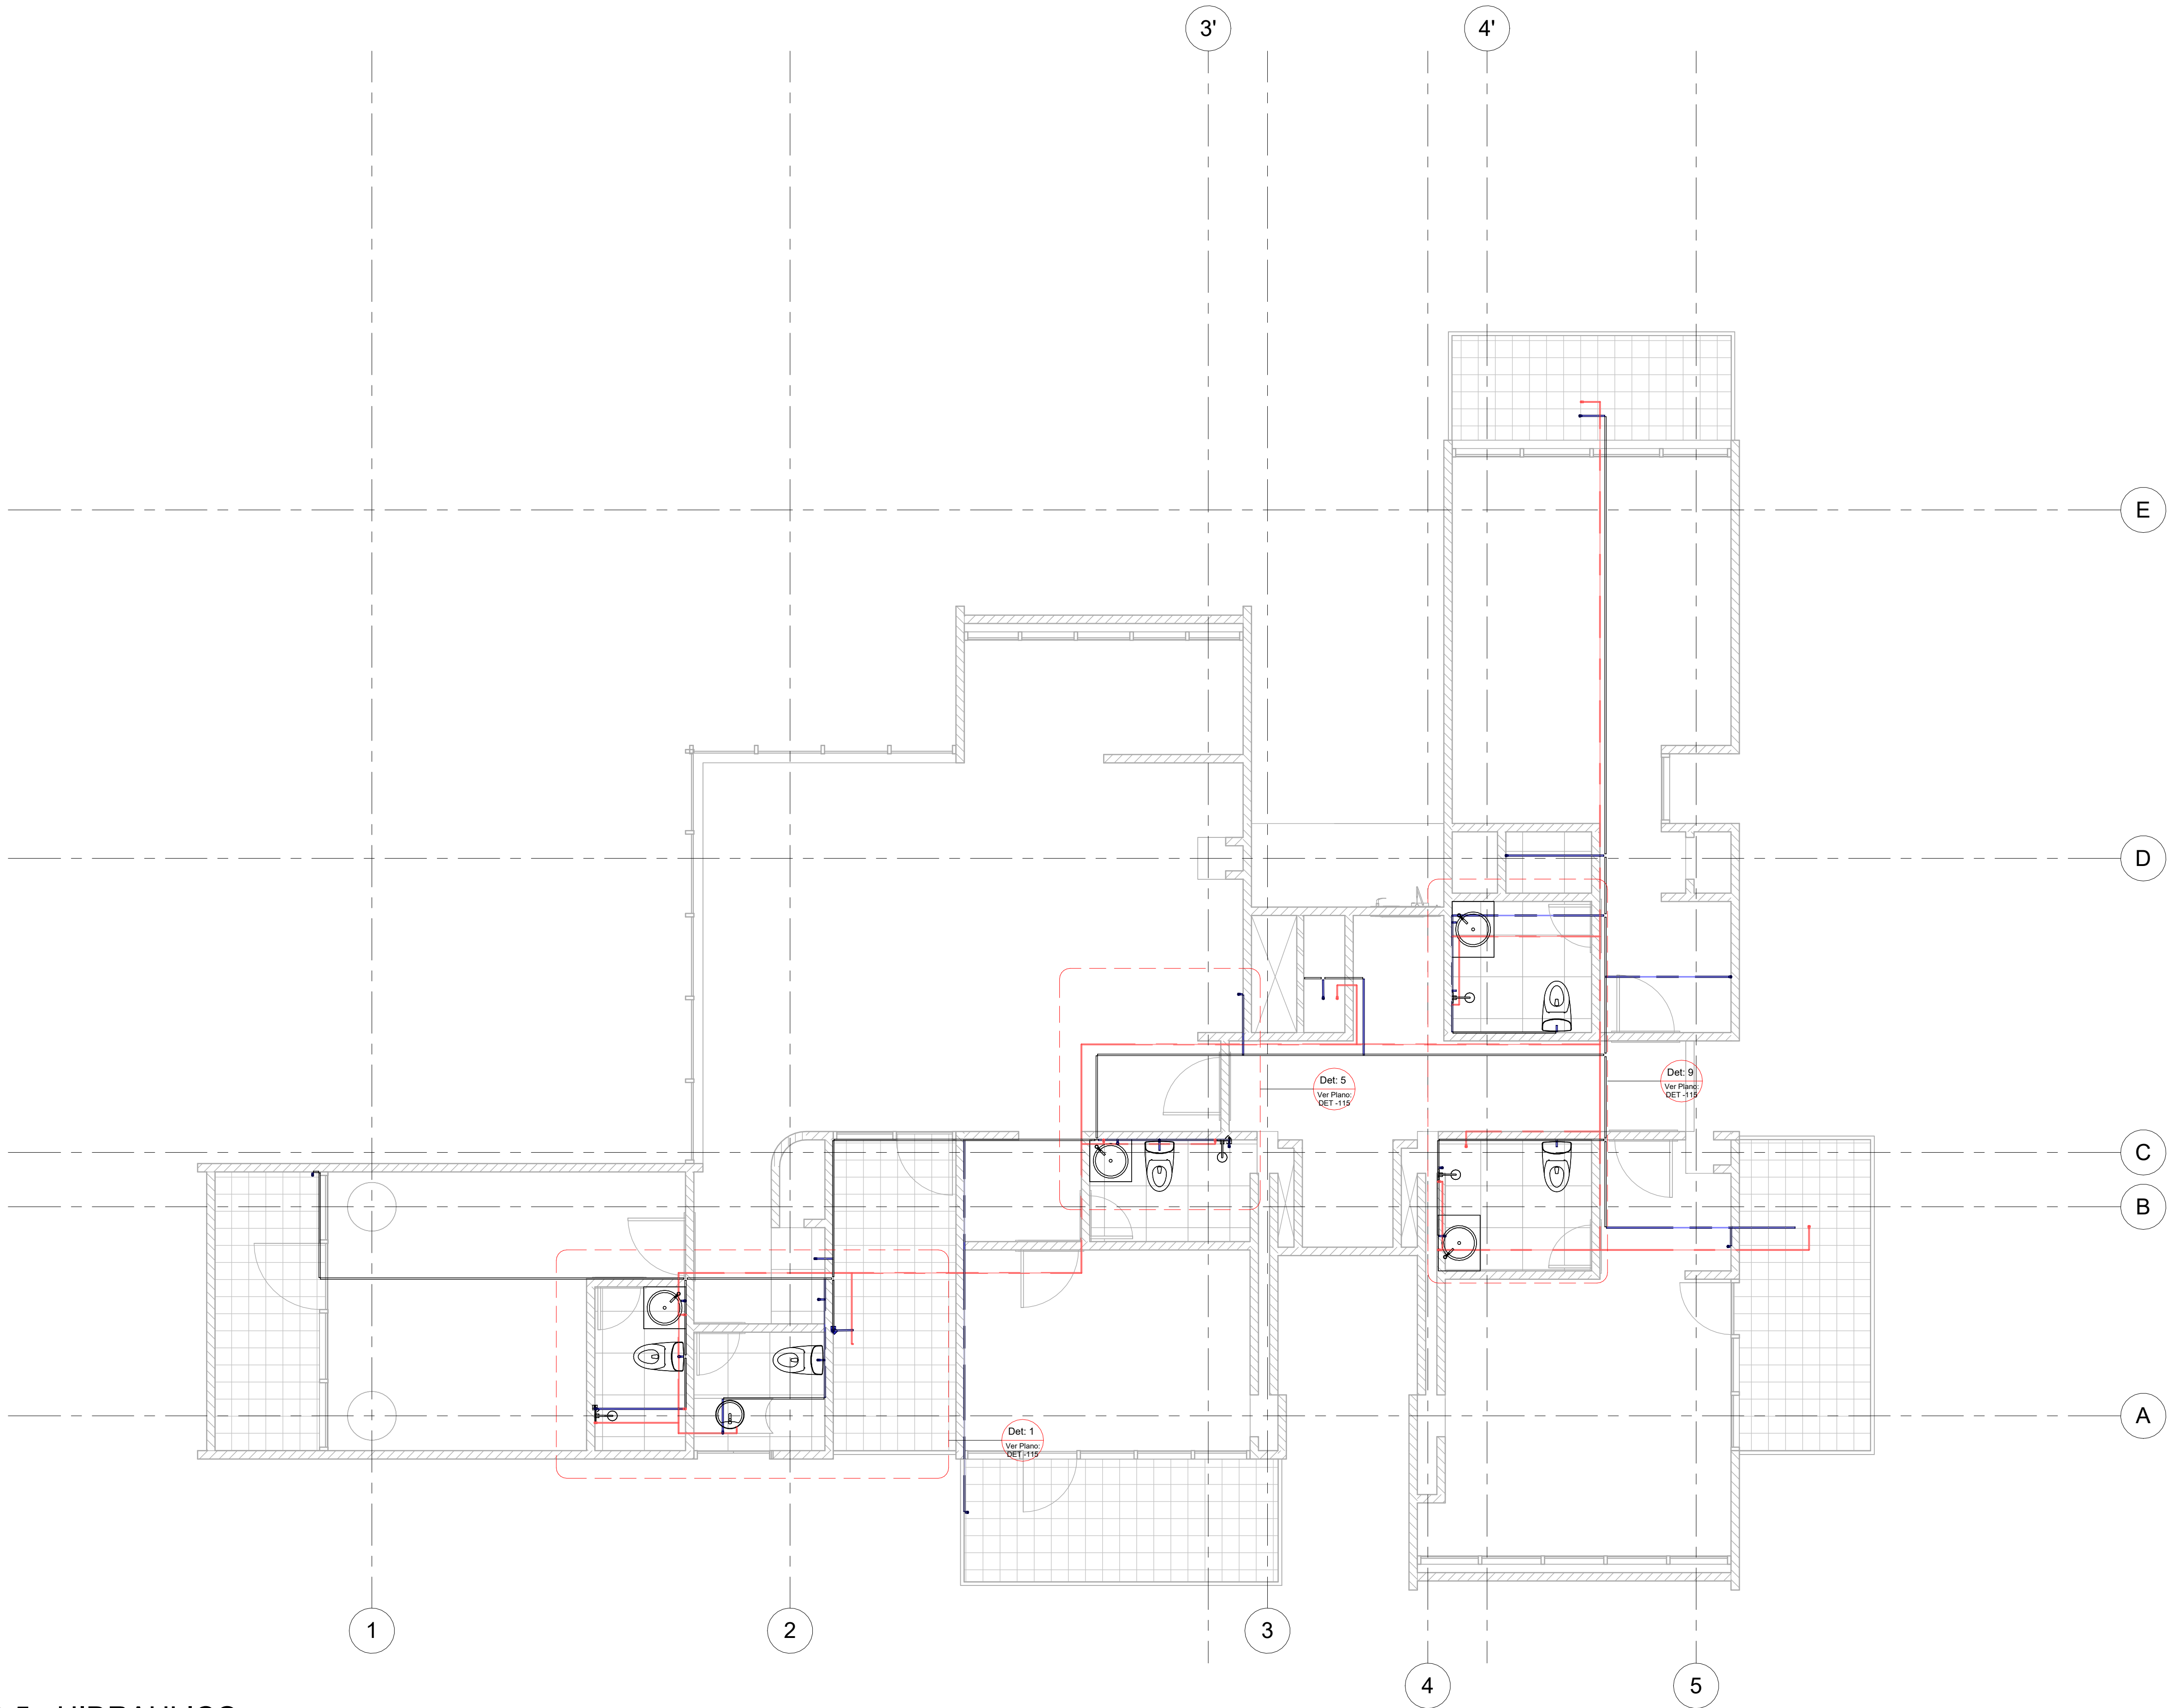

1 PISO 5 - HIDRAULICO
1 : 50

FECHA	REVISIONES	REVISÓ	APROBÓ	FECHA:	SEP TIEMBRE 2025

PROYECTO	Designer	CALCULO:	Checker
PRESUPUESTO No.		DIBUJO:	Author
		REVISÓ:	Checker
ESCALA:	1 : 50	APROBO:	Approver
FECHA:	SEP TIEMBRE 2025	ARCHIVO:	

EMCALI

GERENCIA DE UEN ACUEDUCTO Y ALCANTARILLADO
UNIDAD DE INGENIERIA

FLORENTINO LIVING

PISO 5 – HIDRAULICO