


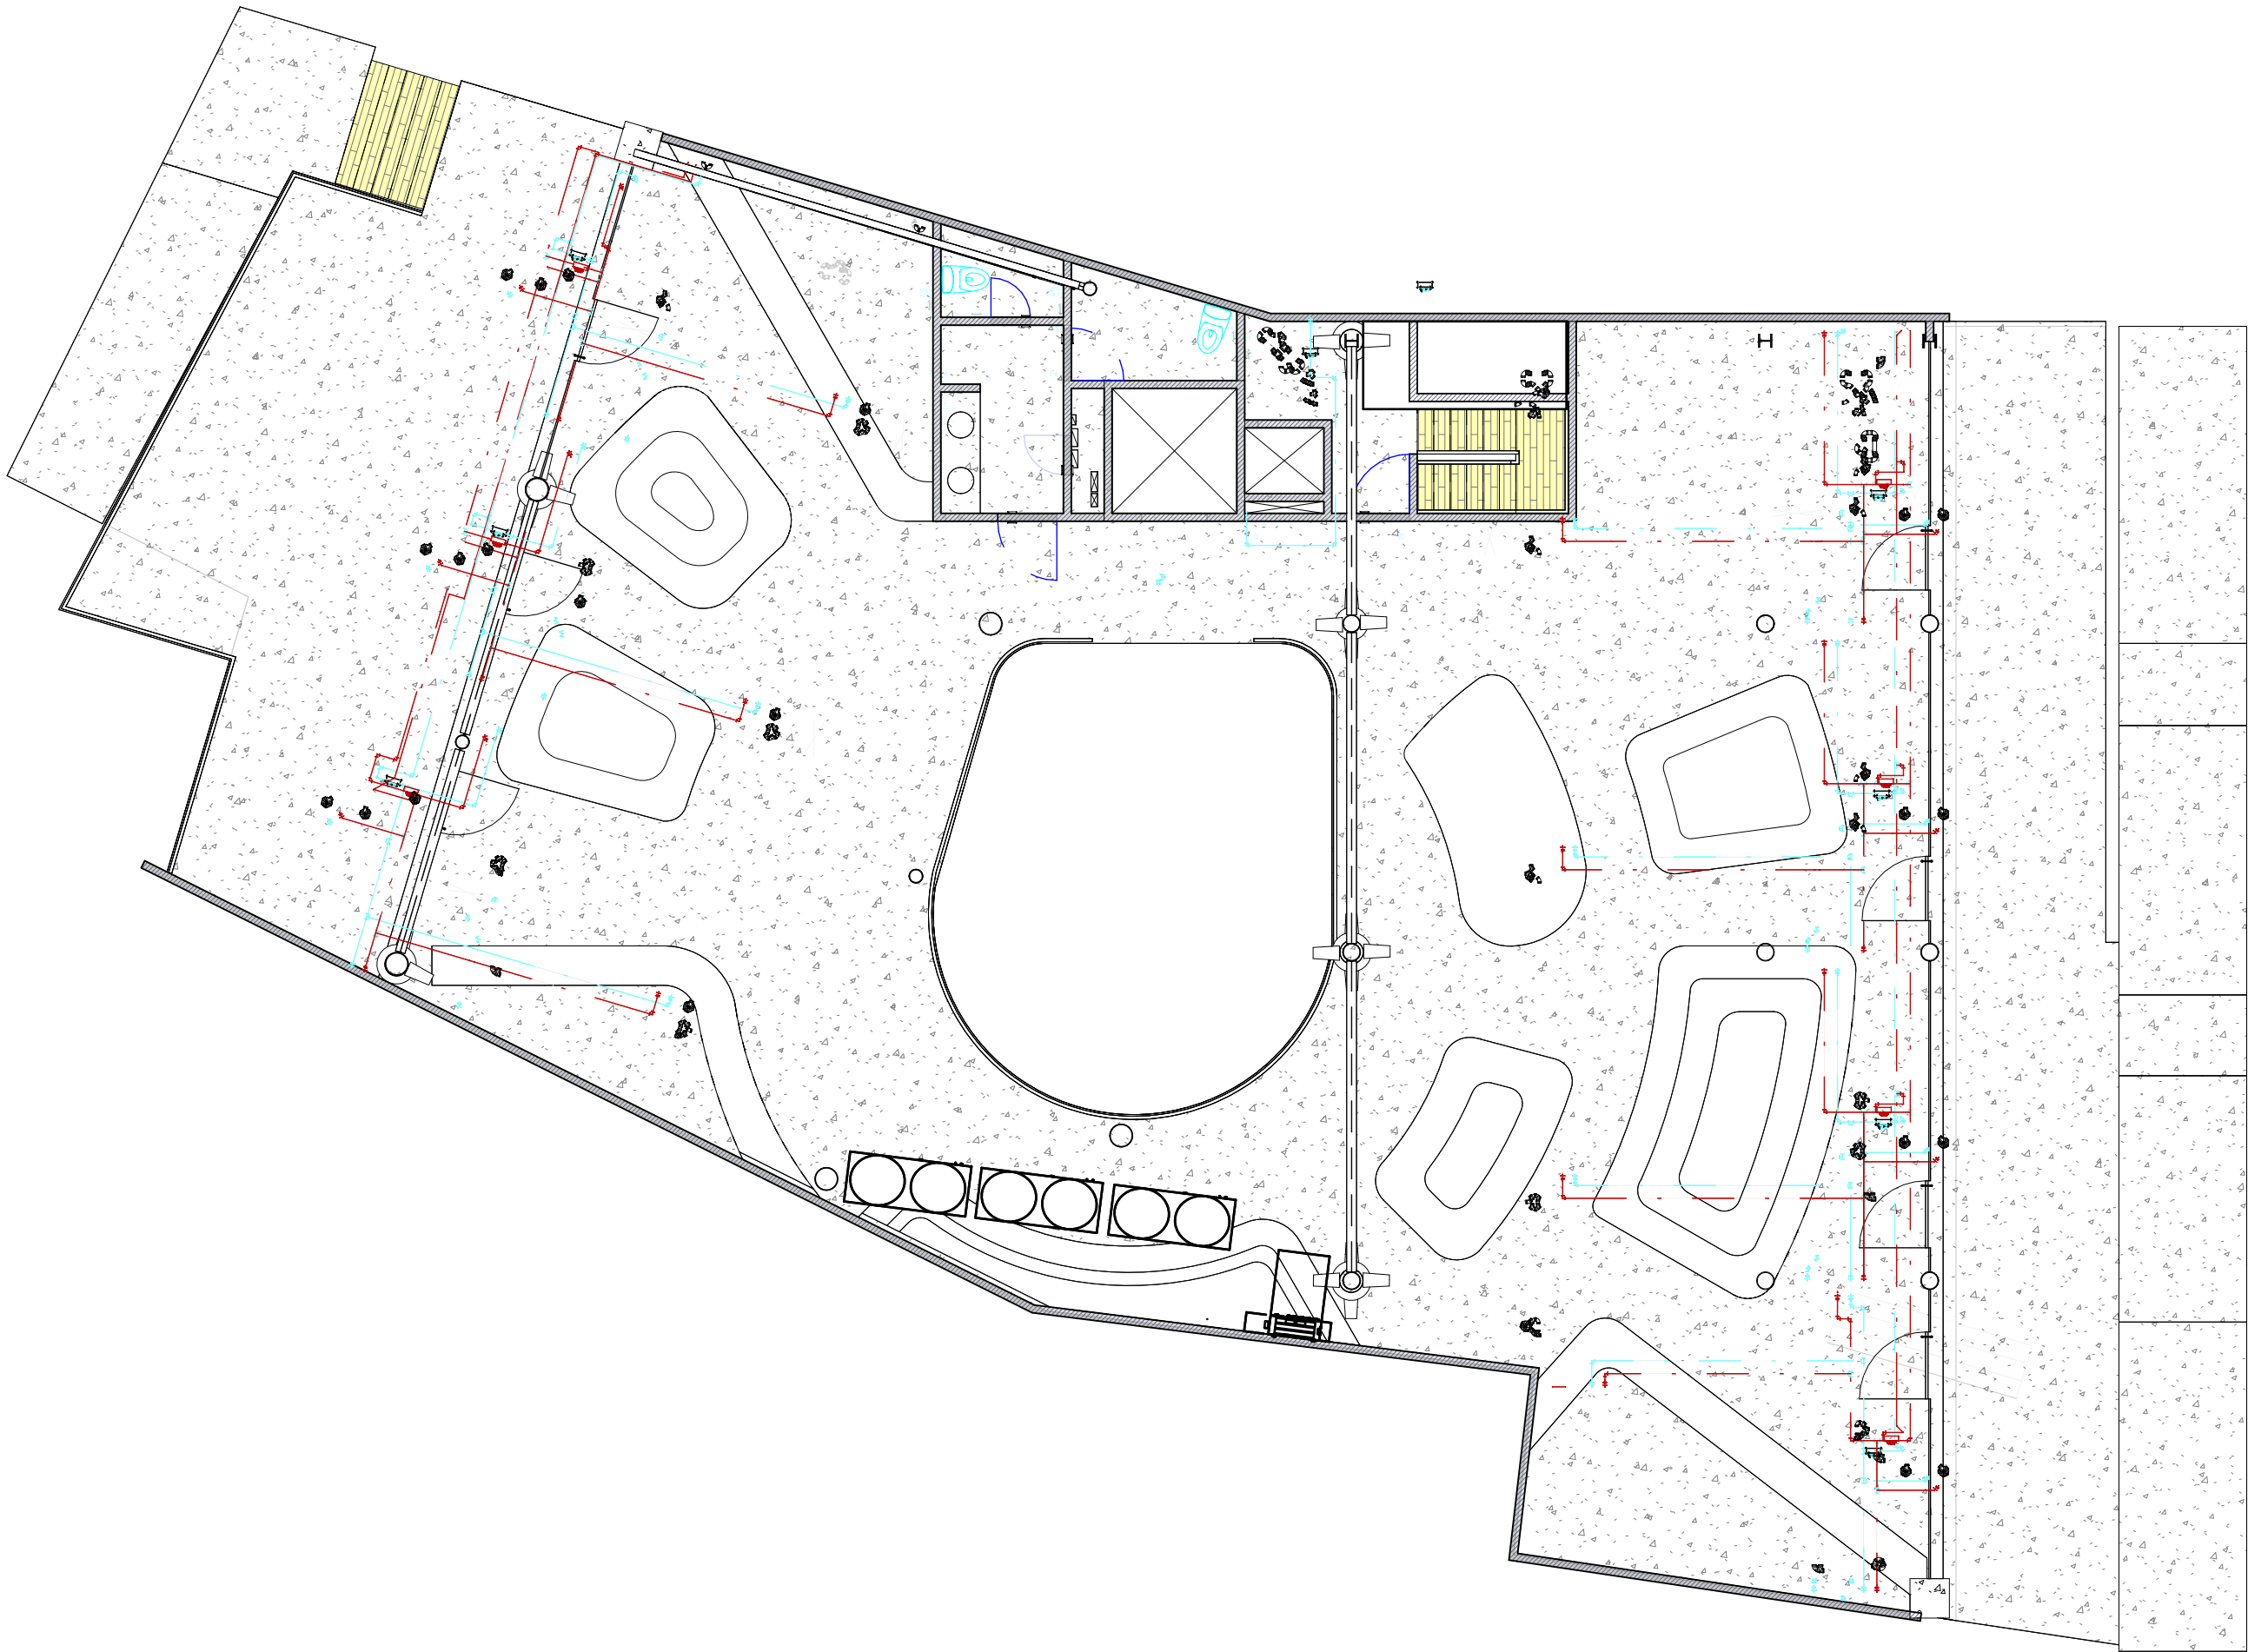

BASTOS

EMCALI		GERENCIA DE UEN DE ACUEDUCTO Y ALCANTARILLADO	
		UNIDAD DE INGENIERIA	
EDIFICIO E			
AV. 4 OESTE No. 3-104			
HIDRAULICO – NIVEL 1			
PLANO:		HS 107	
PROYECTO:		CALCULO:	
PRESUPUESTO No.		DIBUJO	
DIBUJO No.		REVISO	
ESCALA:		APROBO	
FECHA:		ARCHIVO:	
SEPTIEMBRE 2025			

FECHA	REVISIONES	REVISO	APROBO