


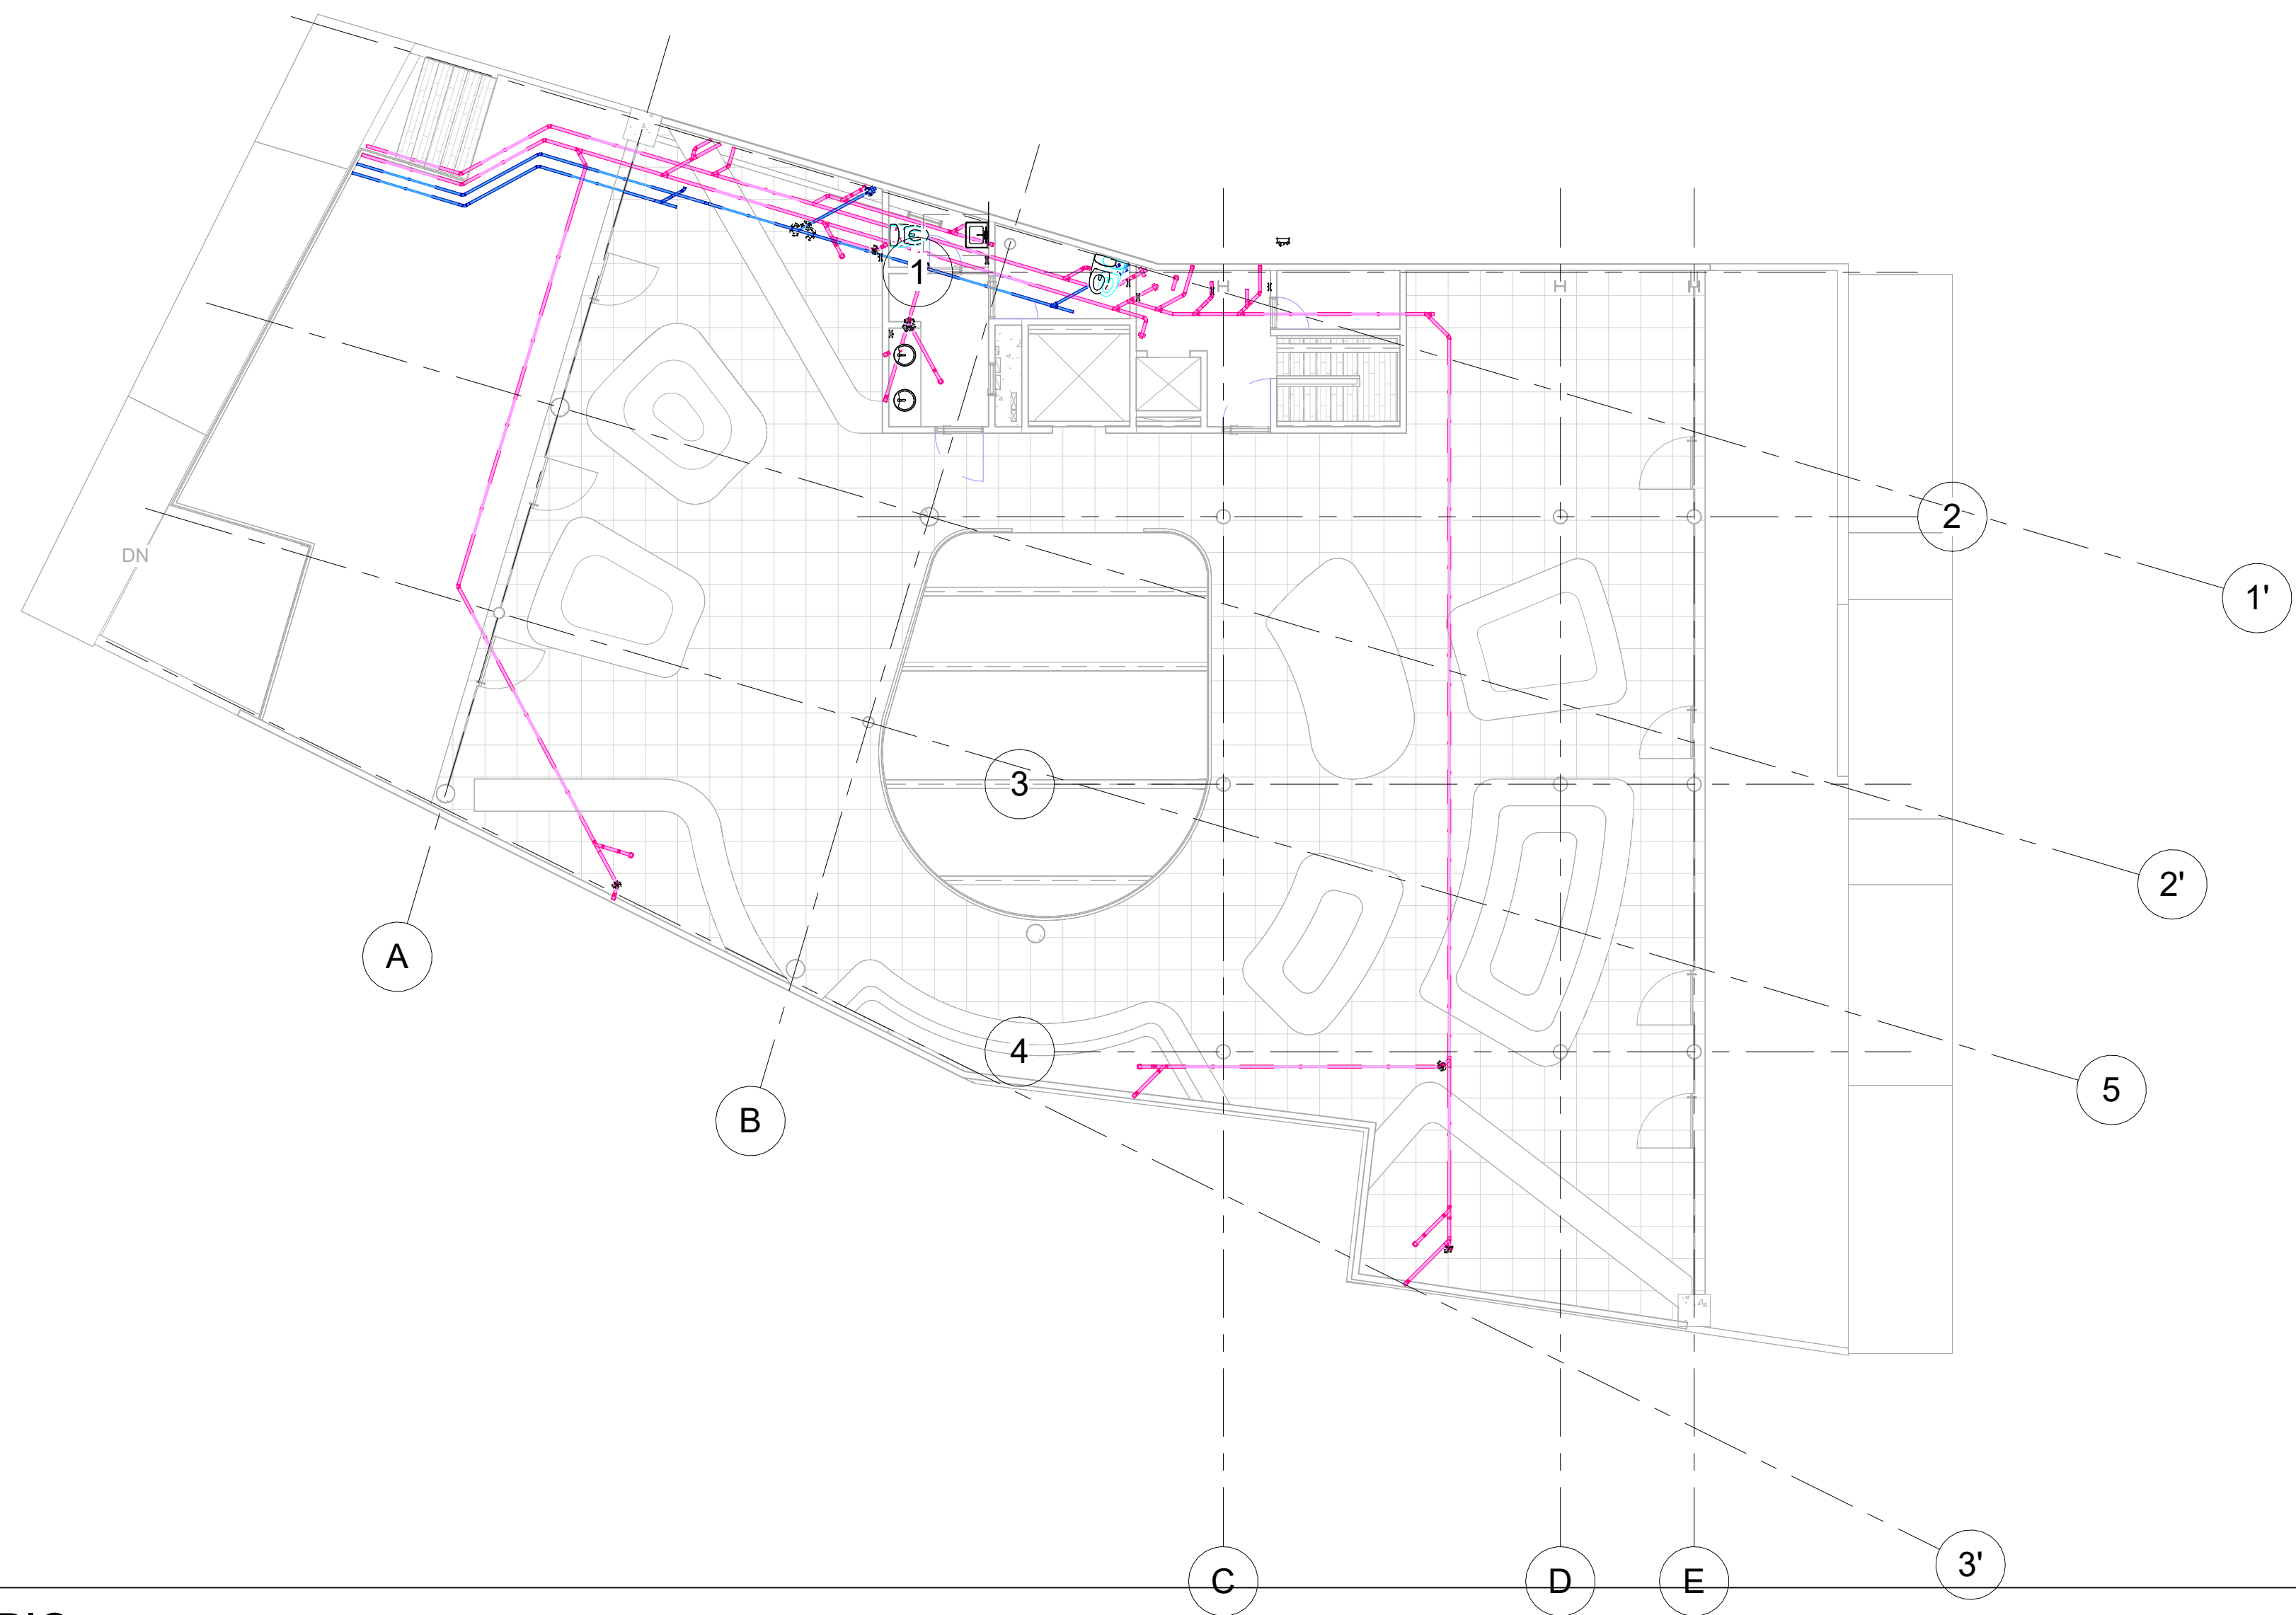

EMCALI GERENCIA DE UEN DE ACUEDUCTO Y ALCANTARILLADO
UNIDAD DE INGENIERIA

EDIFICIO E
AV. 4 OESTE No. 3-104
SANITARIO 1

PLANO: S-101

PROYECTO:	CALCULO:
PRESUPUESTO No.	DIBUJO
DIBUJO No.	SON DIBUJOS
ESCALA:	1 : 100
FECHA:	SEPTIEMBRE 2025
REVISIONES	REVISO
APROBO	ARCHIVO: