


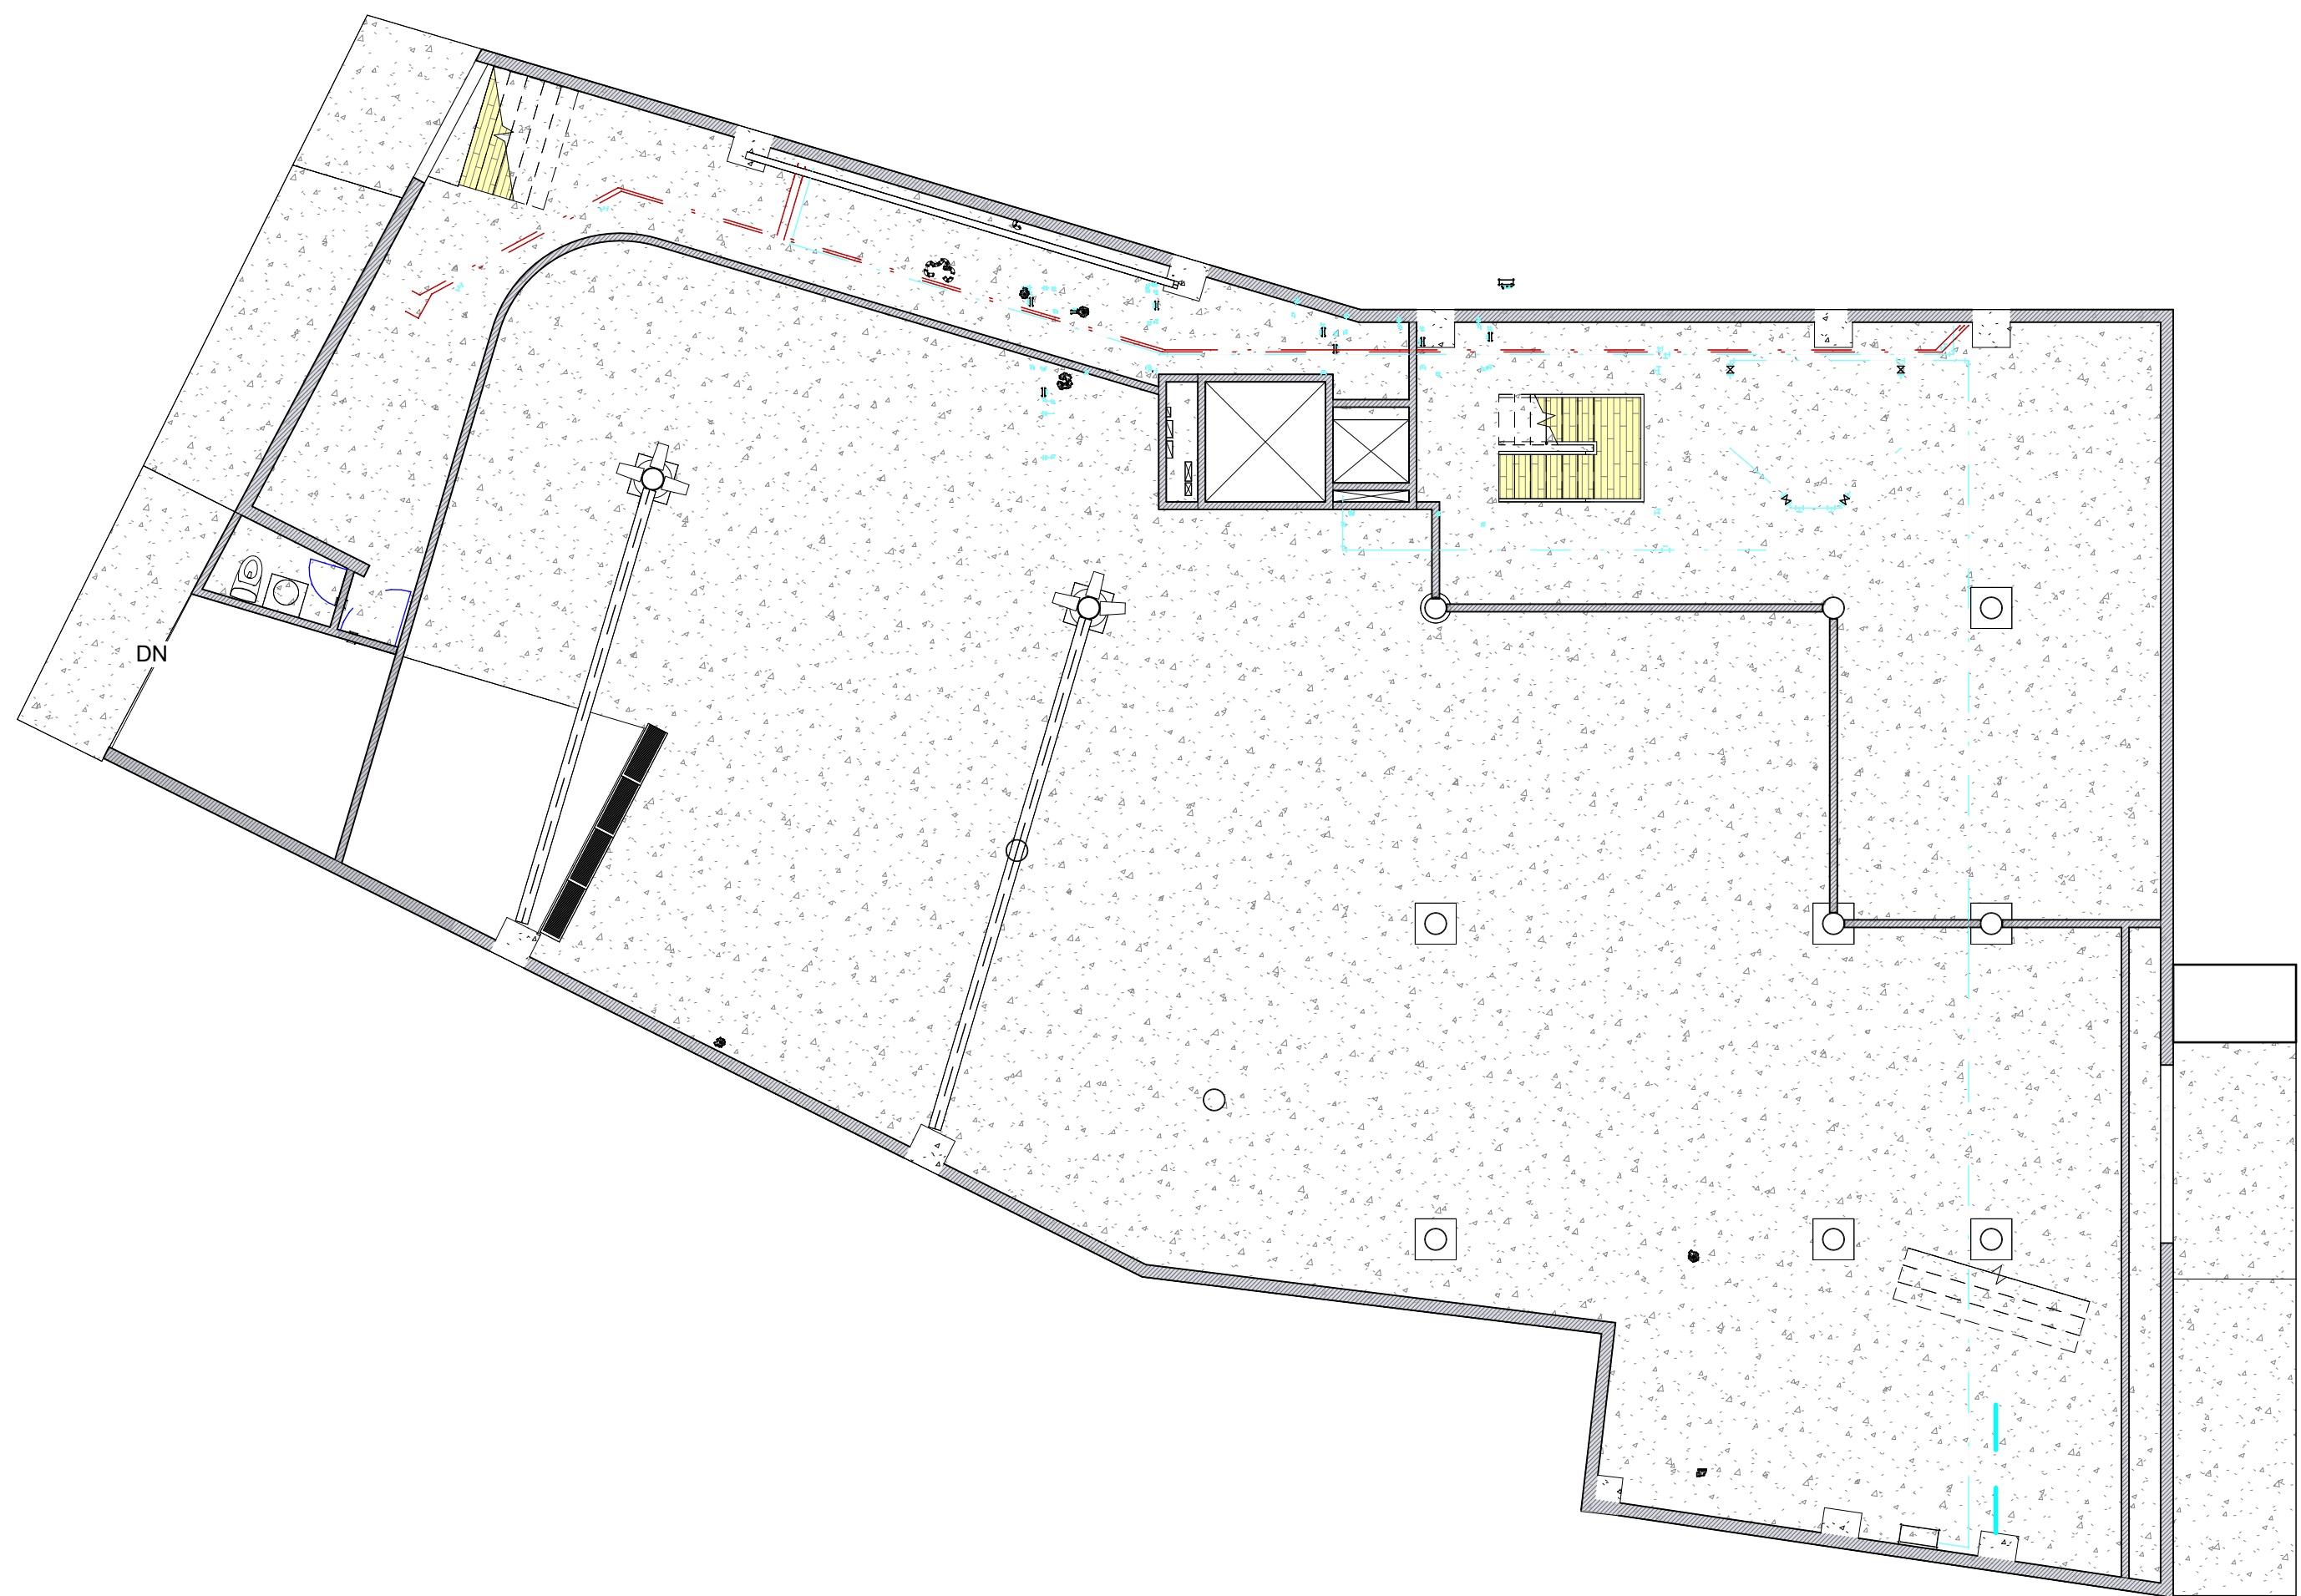

EMCALI GERENCIA DE UEN DE ACUEDUCTO Y ALCANTARILLADO
UNIDAD DE INGENIERIA

EDIFICIO E
AV. 4 OESTE No. 3-104
SANITARIO SOTANO

PLANO: S-106

				PROYECTO:	CALCULO:
				PRESUPUESTO No.	DIBUJO
				DIBUJO No. SON DIBUJOS	REVISO
				ESCALA: 1 : 100	APROBO
FECHA	REVISIONES	REVISO	APROBO	FECHA: SEPTIEMBRE 2025	ARCHIVO: