



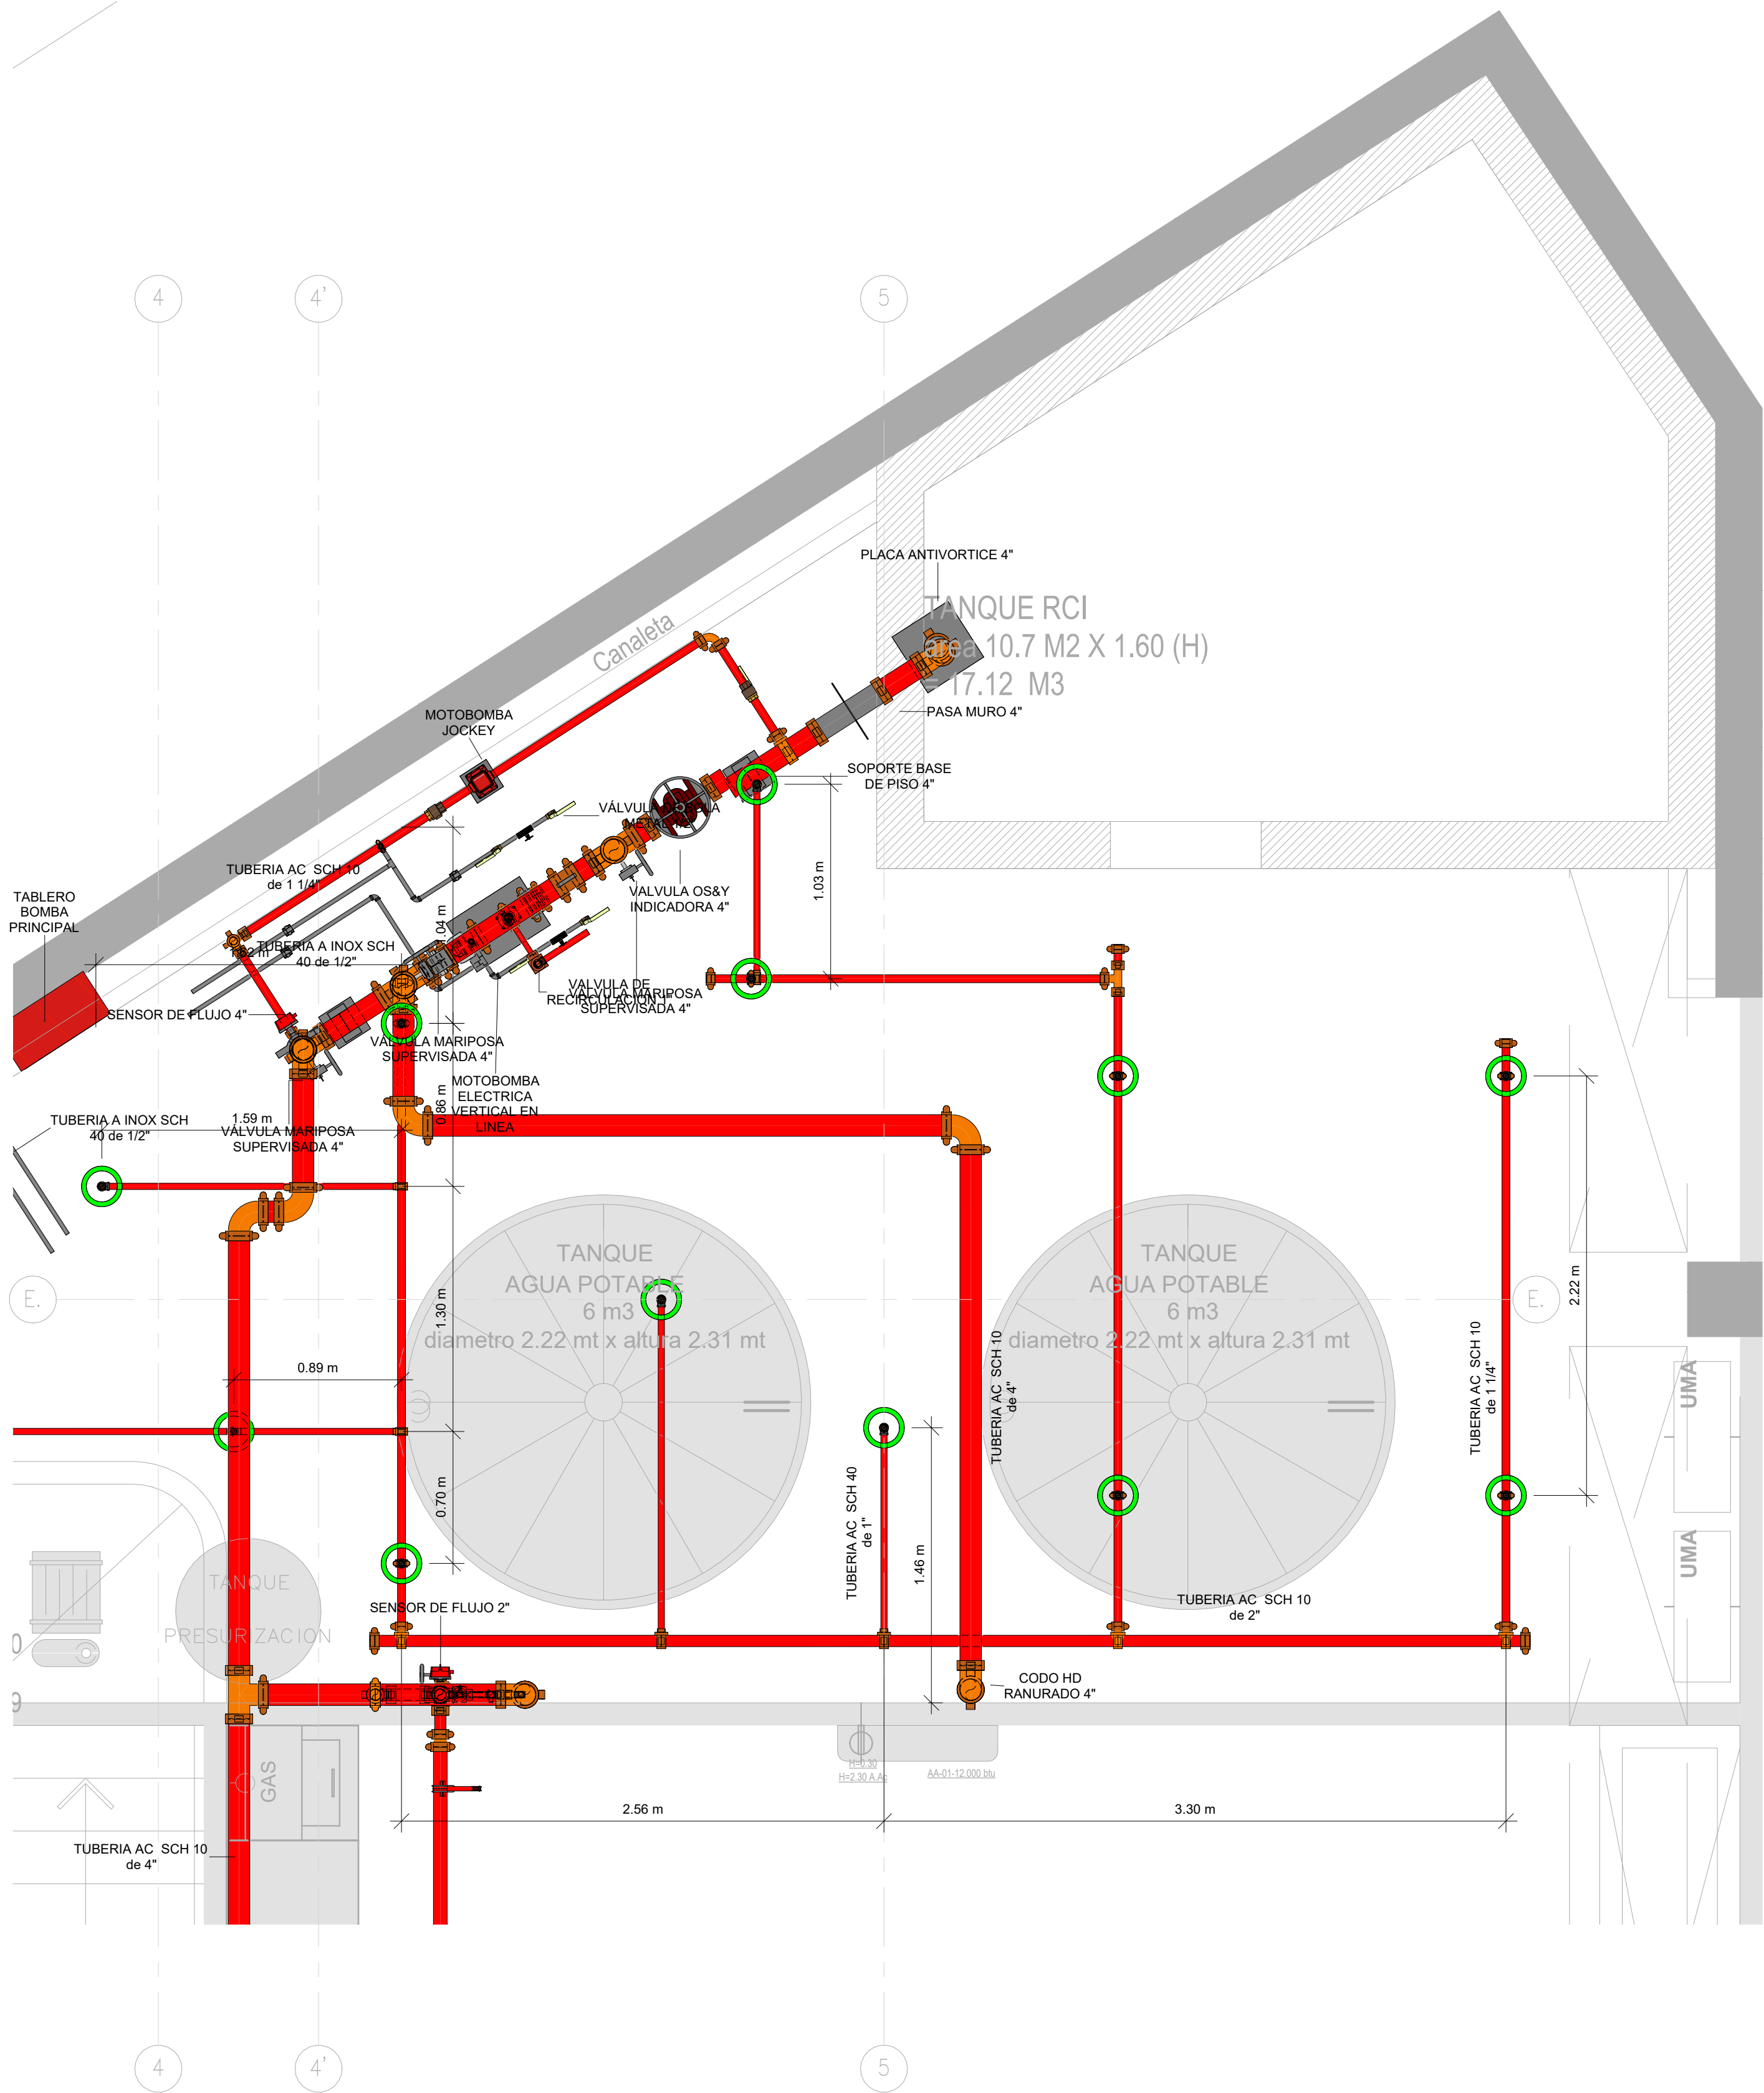

1 PLANTA CUARTO DE BOMBAS RCI
1 : 25

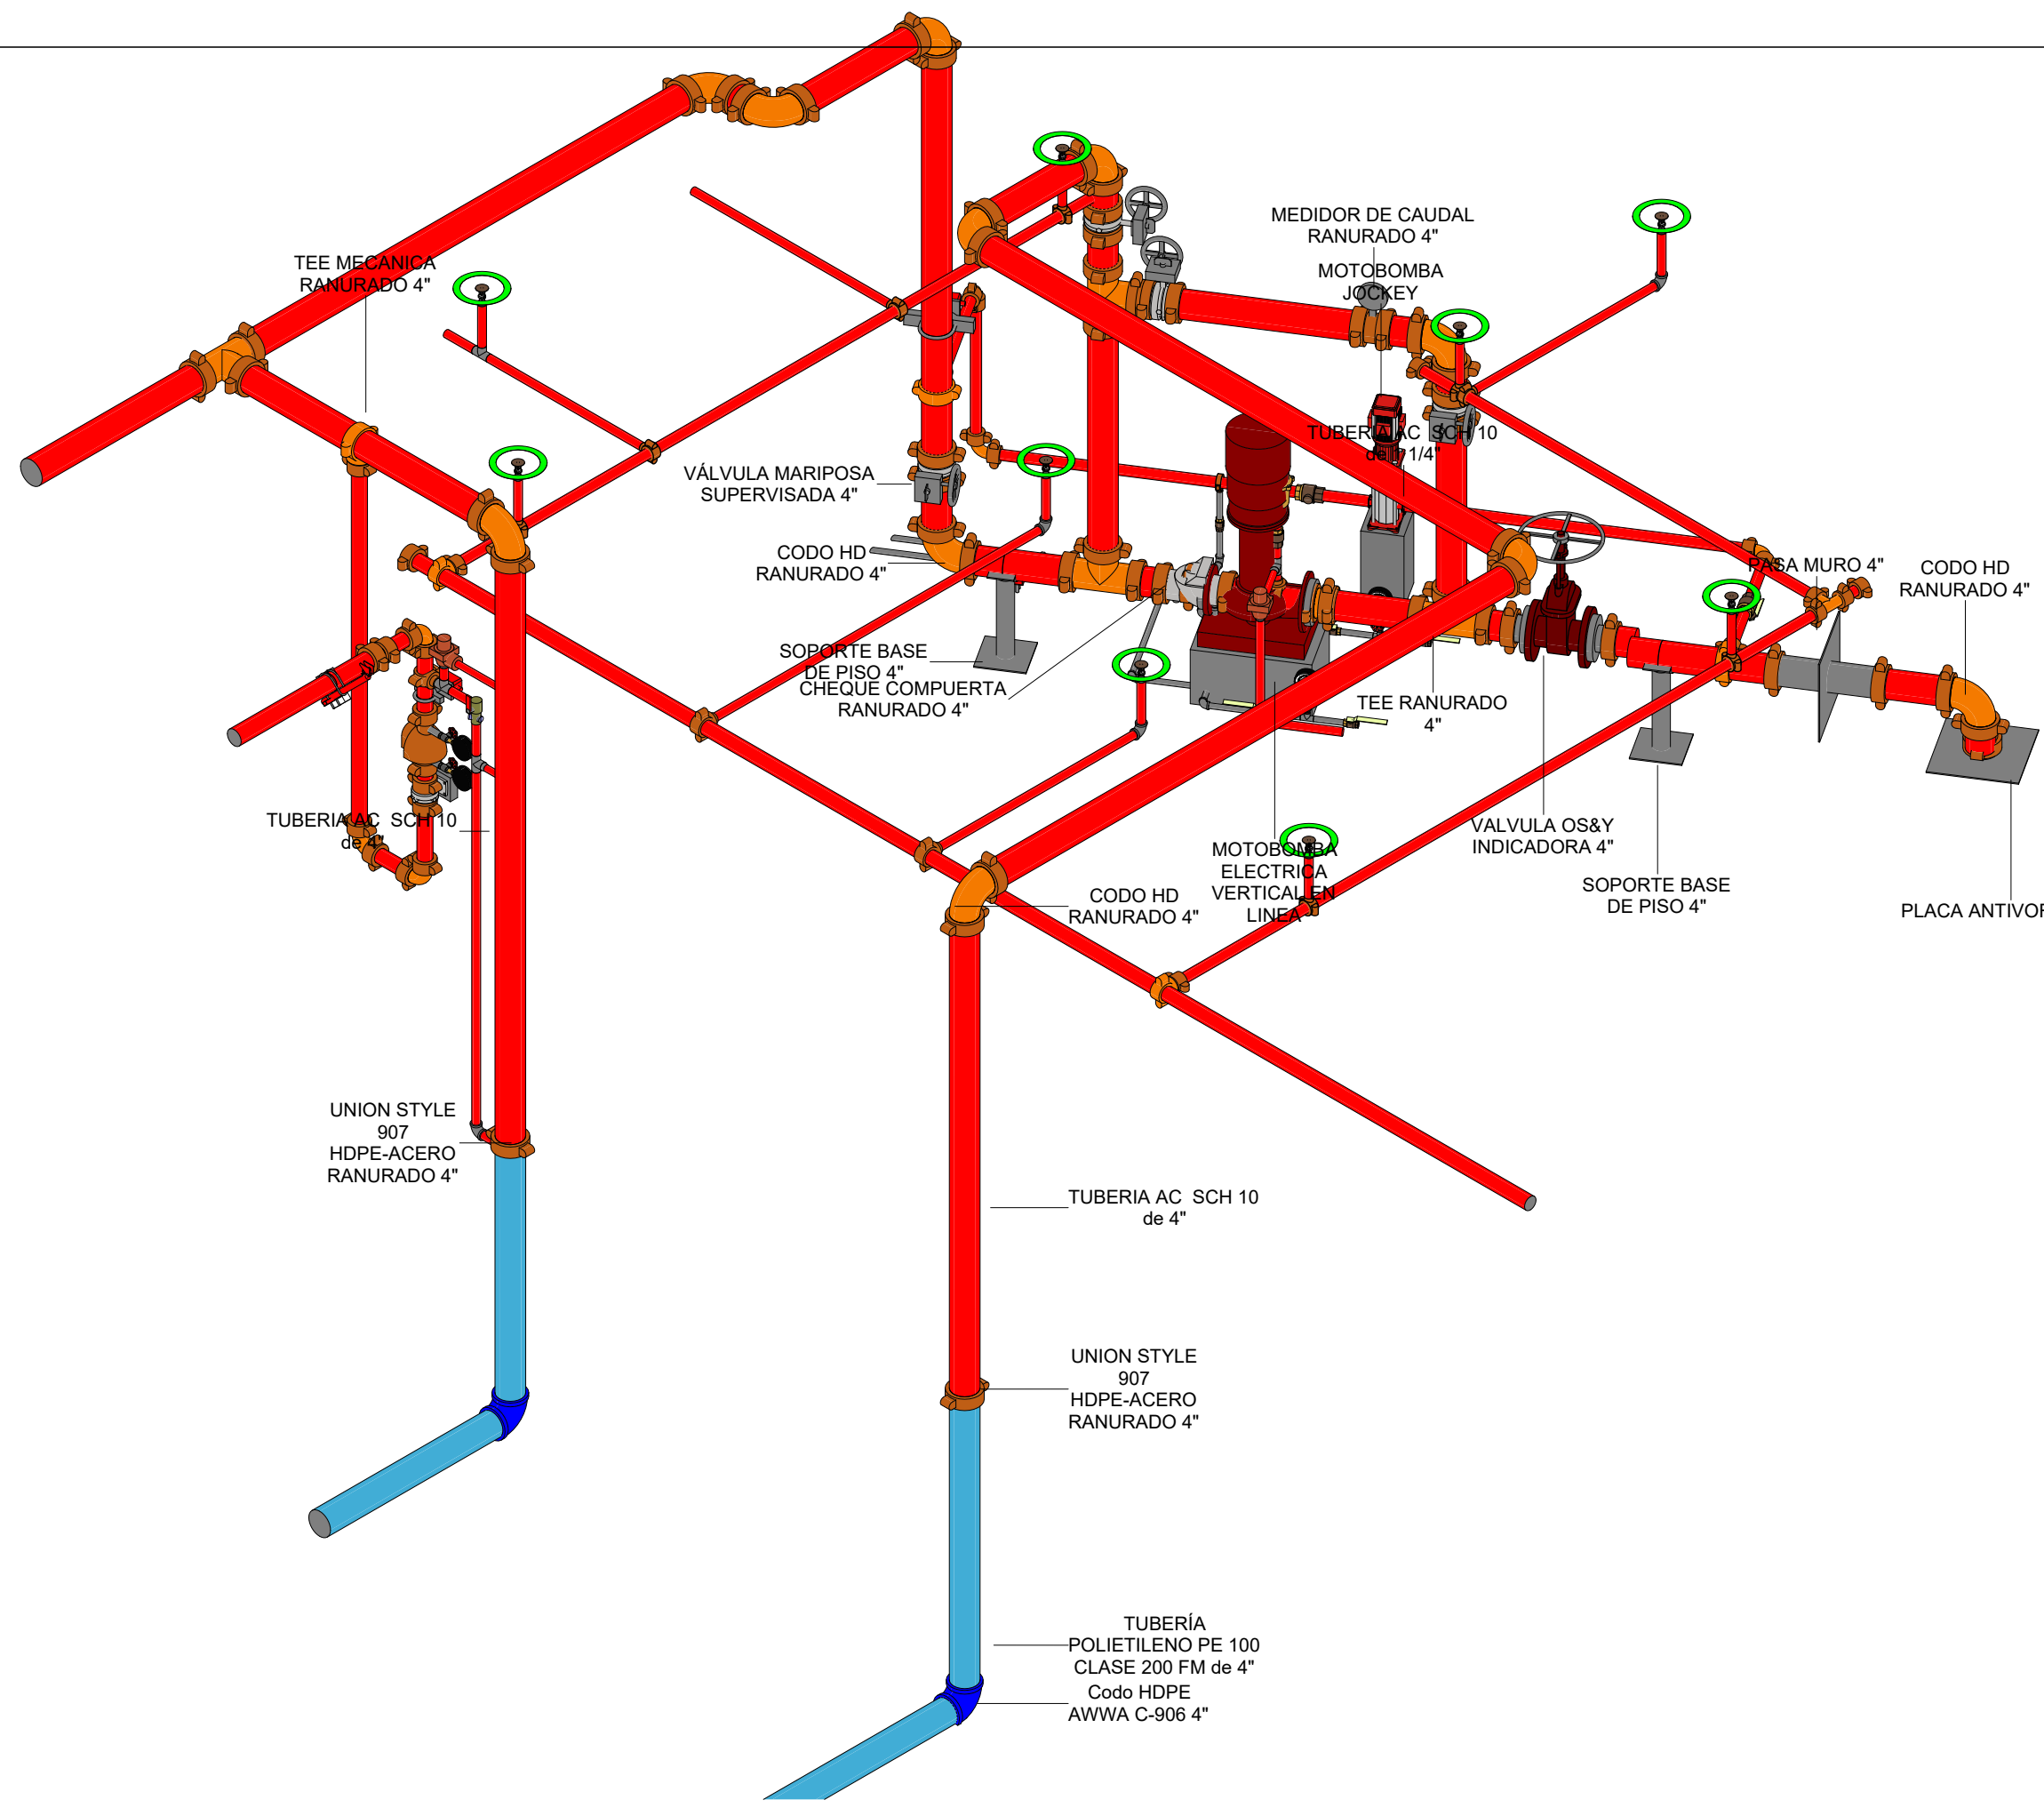

2 ISOMETRÍA CUARTO DE BOMBAS RCI


CONVENCIONES	
	Valvula Cheque de compuerta Ranuado
	Valvula Cheque Roscado
	Extintor de CO2
	Extintor de ABC de Polvo Quimico Seco
	Válvula angular de 2.1/2"
	Manómetro de 300 psi
	Medidor de caudal
	Pasa muros
	Placa Antivortice
	Sensor de flujo de agua
	Siamesa en bronce, dos entradas de 2.1/2" una salida de 4"
	Válvula de bola
	Válvula Mariposa indicadora y supervisada
	Válvula de compuerta OS&Y
	Válvula desaireadora
	Acople ranurado
	Flanche o brida ranurada
	Codo ranurado
	Reducción copa Ranurada
	Soporte vertical para tubería
	Tee ranurada
	Tee mecánica ranurada o roscada
	Tubería AC SCH 10/40
	Tubería Polietileno 100 CLASE 200 FM
	Rociador montante
	Rociador pendiente

CUADRO DE NOTAS DE INSTALACIÓN

- Se instalan rociadores de respuesta rápida, cobertura estándar, temperatura ordinaria, factor de descarga K=5.6 con orientación Montante en cuartos de sotano.
- Se ubican válvulas de 2.1/2 de pulgadas (gabinete tipo I) a una altura entre 0.90m y 1.20m del suelo a la válvula en escaleras de emergencia.
- Se ubican estaciones de mangueras de 1.1/2 de pulgadas (gabinete tipo II) a una altura del suelo a la válvula de 1.50 m en los pasillos de circulación.
- La siamesa se instala en la fachada del edificio, a no más de 30 m del hidrante como lo indica la norma NFPA 14.
- Se instala una moto-bomba vertical en línea con motor eléctrico de 200 Gpm 135 Psi.
- La reserva de agua debe ser no menor a 6000 galones (23 m³).
- Se instala un sistema de extintores portátiles de fuego de Polvo Químico Seco (PQS) en pasillos, de agua en UAR y de Co2 en cuartos técnicos.
- Las tuberías instaladas deben cumplir con las condiciones de la norma NTC 1669 y NFPA 14 (Corresponde al ejecutor de la obra, replantear en sitio los distanciamientos de tubería, equipos y accesorios, sin alterar el alcance del diseño y la norma).
- La soportería empleada debe cumplir con las condiciones de la norma NFPA 13, las especificaciones técnicas de la instalación y de los equipos se encuentran consignadas en las memorias conceptuales.
- La soportería sismo resistente empleada debe cumplir con las condiciones de la norma NFPA.
- Las especificaciones técnicas de la instalación y de los equipos se encuentran consignadas en las memorias conceptuales.
- La instalación y puesta en marcha del sistema deben ser realizadas por una empresa o persona profesional en el tema, idónea y conocedora de las normas vigentes. Que asuma la responsabilidad de cumplimiento y el objeto de facilitar la observancia de la ley. (El constructor es responsable de verificar en sitio las condiciones constructivas y arquitectónicas en garantía de las estabilidad para la instalación del proyecto).
- Seguir las recomendaciones de mantenimiento del sistema contra incendio de la norma NFPA 25 y lo NFPA 22.
- Los equipos, tuberías y accesorios deben ser listados y certificados UL/FM según las exigencias de la norma.
- La tubería enterrada va a 1.2 a clave como mínimo en vías y en zona verde y andén mínimo a 0.80 m.

NOTA: Las especificaciones técnicas de la instalación y de los equipos mencionados anteriormente se encuentran consignadas en las memorias conceptuales.

NOTA: Las especificaciones técnicas de la instalación y de los equipos mencionados anteriormente se encuentran consignadas en las memorias conceptuales.

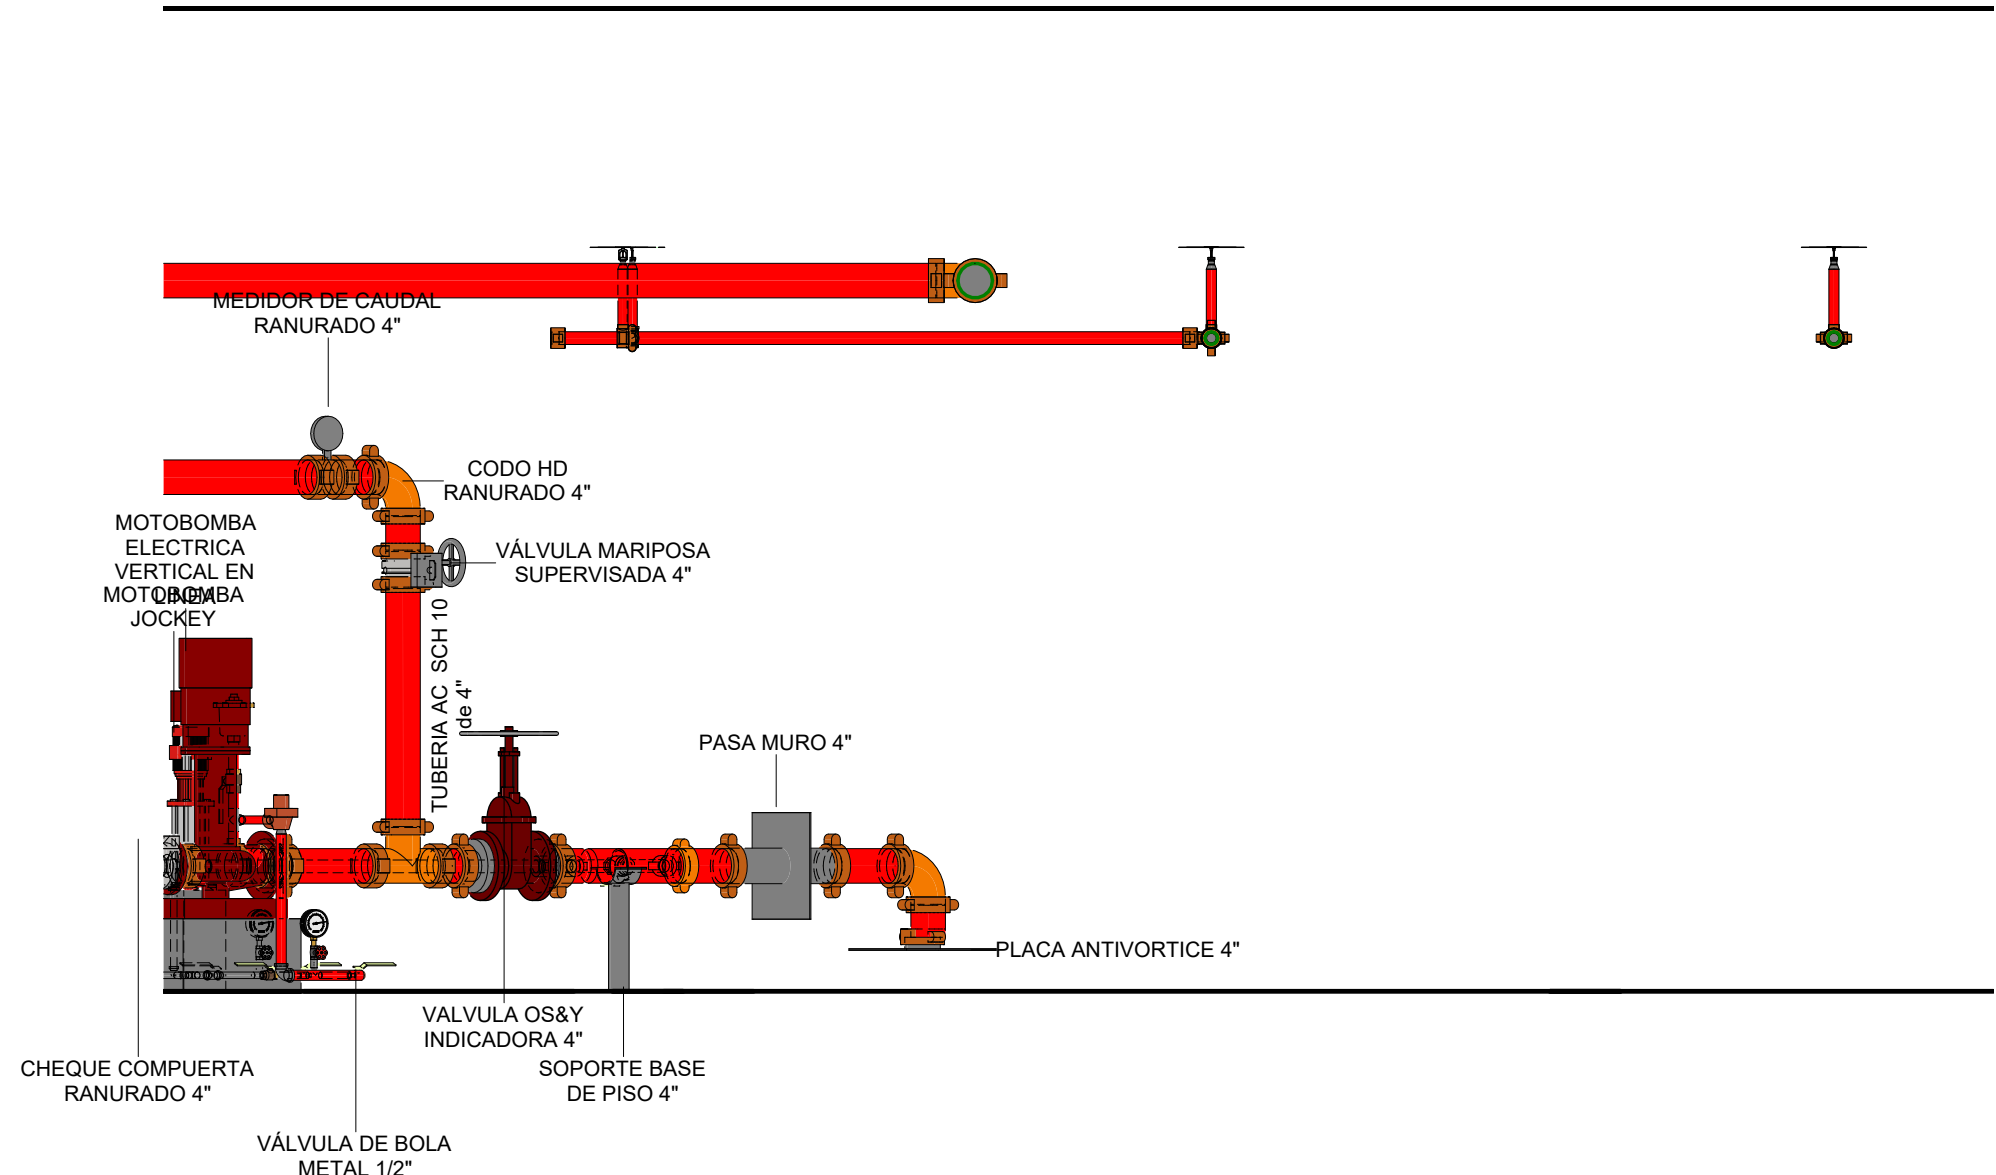

3 SECCIÓN CUARTO DE BOMBAS RCI
1 : 25

CLIENTE:

Diseñado por

Autor
Verificador

[Signature]
CC 1144052558

CONTIENE:

UBICACIÓN DEL
PROYECTO:
CALI-VALLE

Nº	Actualización	Fecha

CUARTO DE BOMBAS
RCI

Fecha JUNIO 2026

PL04

Escala Como se indica