


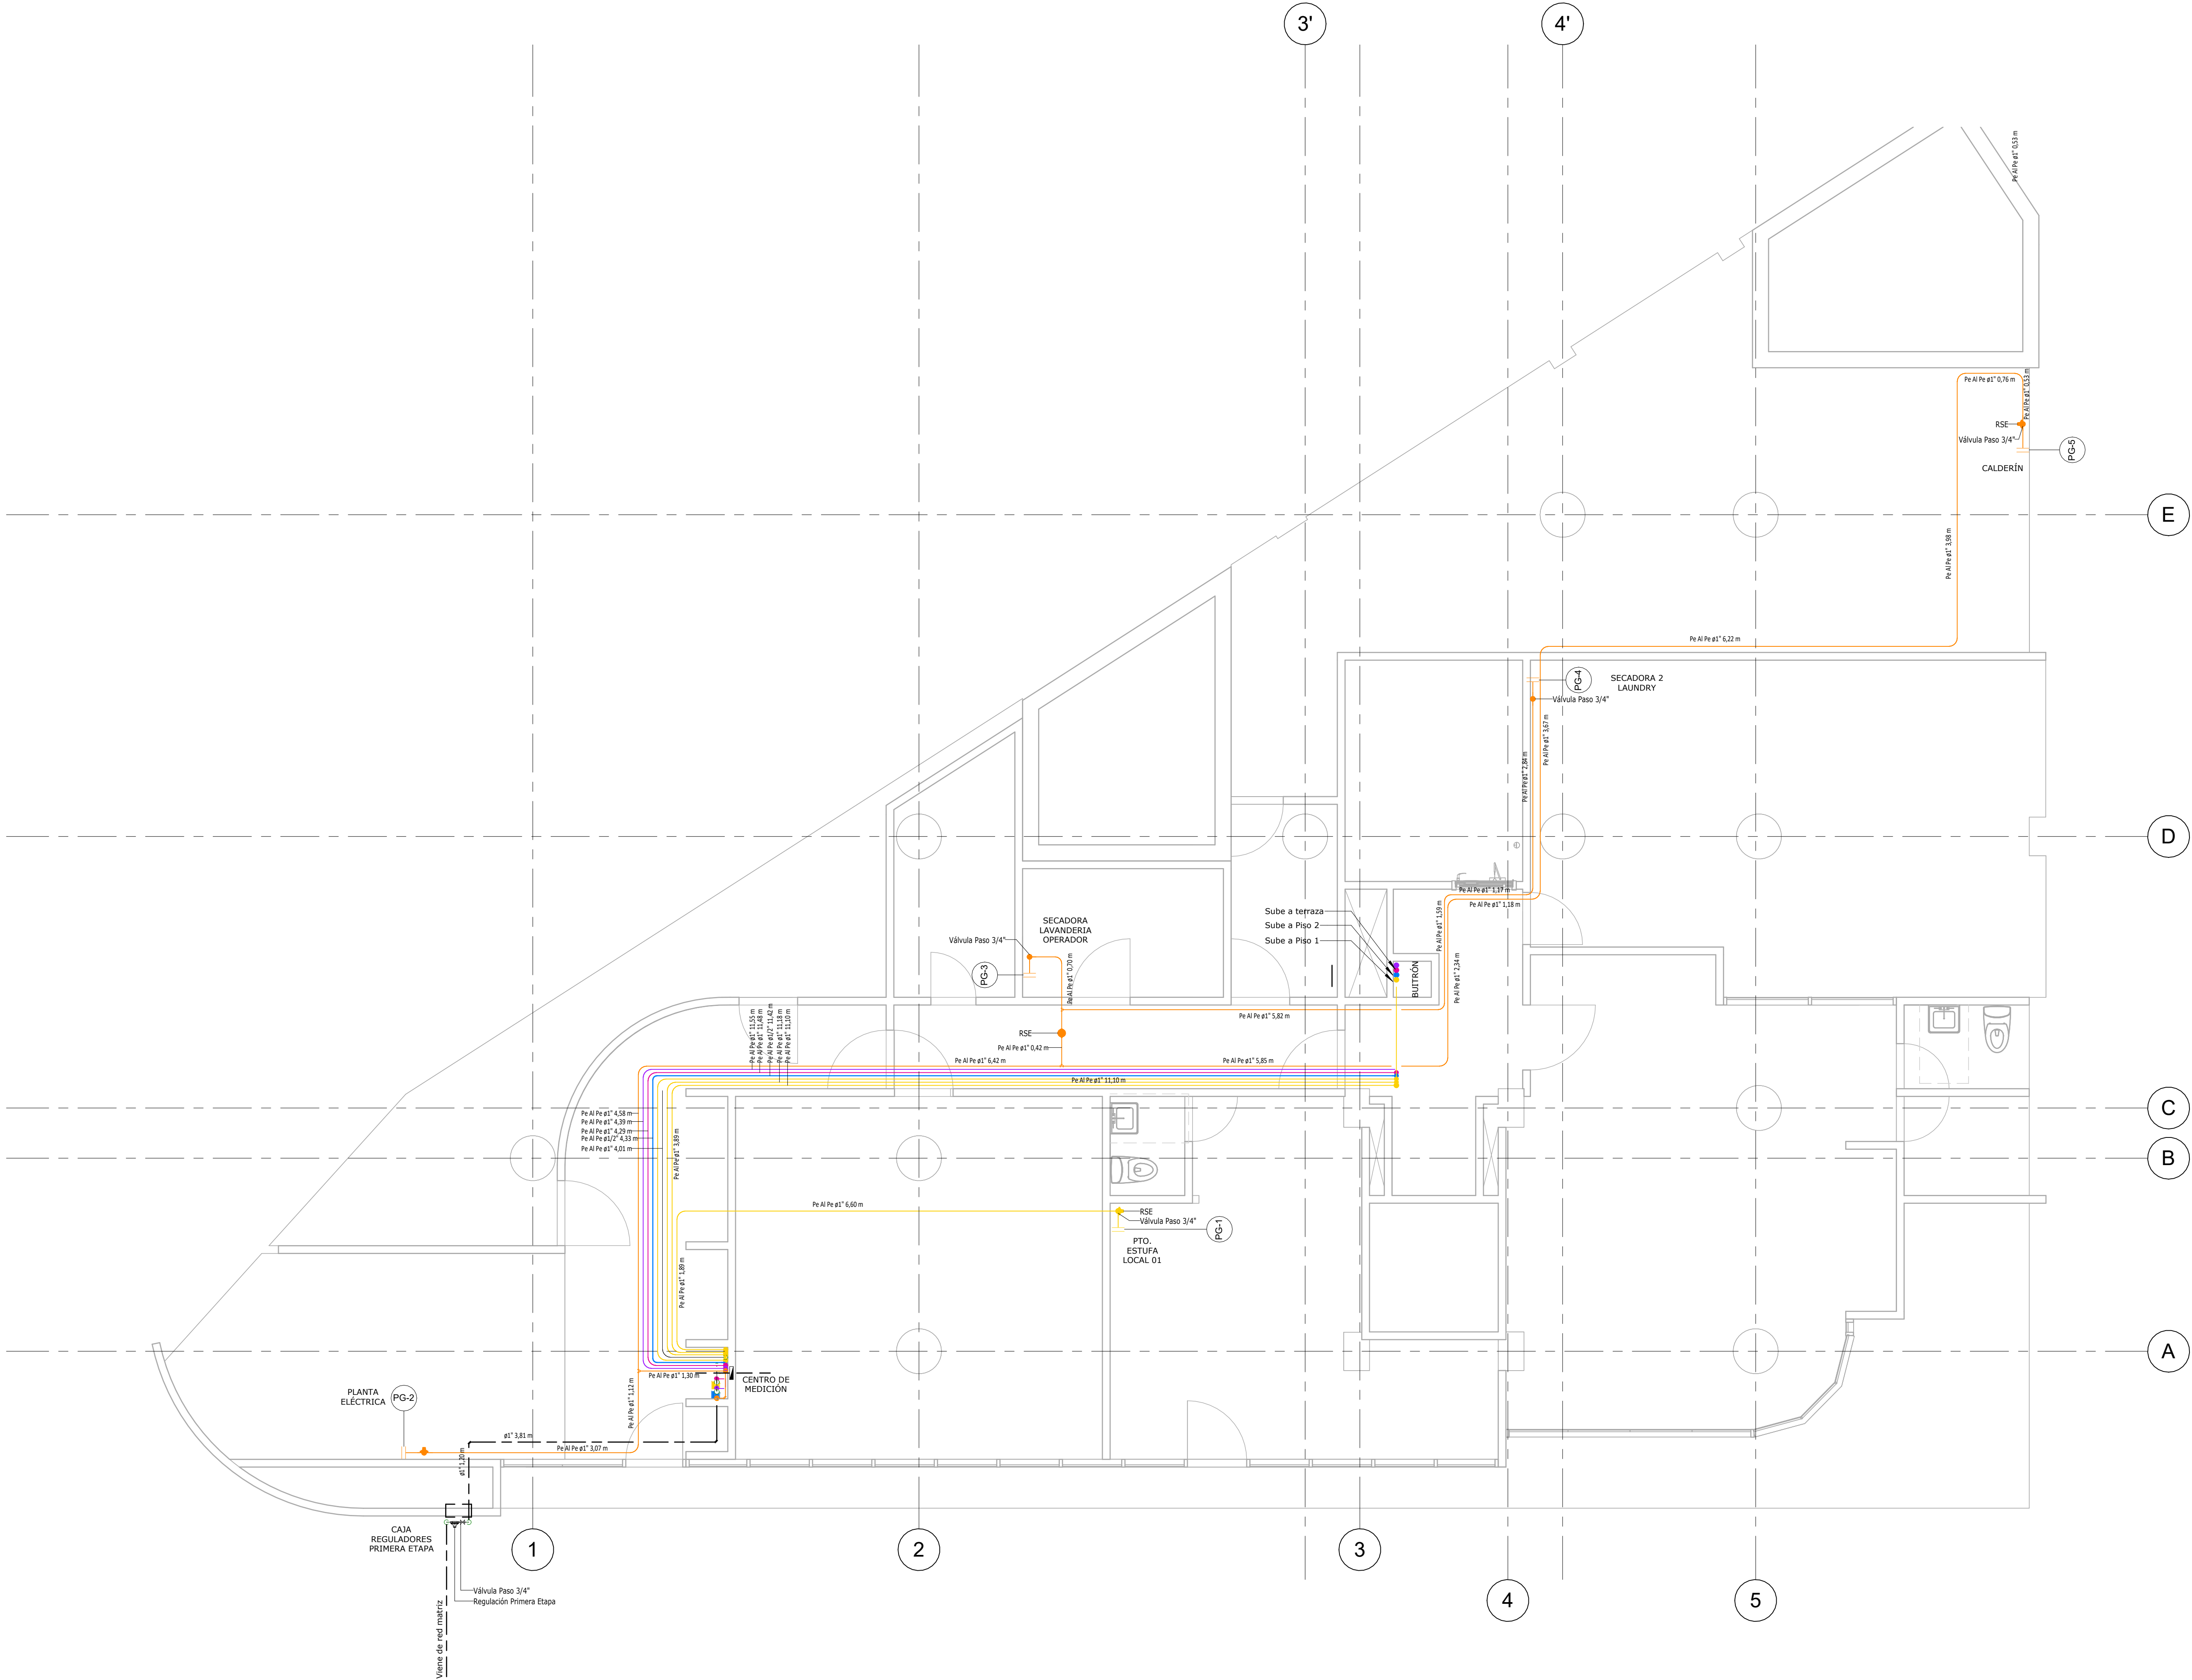

CONVENCIONES

Centro de Medición
Curva 90° Pe al Pe
Codo 90°
Válvula de Paso Pe al Pe
Reducción Pe al Pe
Te Pe al Pe
Punto salida de gas
Sube / baja
RSE - Regulador de segunda etapa
Pase en muro

Tuberías

Red Locales
comerciales por cielo
Red Zonas comunes
por cielo
Red Oficinas por piso
Red Zonas comunes
terrazza por cielo
Red Zonas comunes
sobre cubierta técnica
Conexión a Red
principal

Norte:

Proyecto:

FLORENTINO

Dirección:

El Peñón - Cali

Notas Generales:

- Todas las medidas son indicativas y deben ser verificadas en sitio.
- Los buitrones por donde subirá la tubería de gas deberán llevar un tabique de separación en caso de que se encuentren compartido con otro servicio.
- Se deberán instalar rejillas para garantizar la ventilación en buitrones cerrados.
- Se deben considerar registros de inspección en cada piso del buitrón.
- La modificación de las redes internas solo podrán hacerse por personal calificado.

Observaciones:

REV.	DESCRIPCIÓN.	FECHA.
------	--------------	--------

Diseño:

MAURICIO CASANOVA
INGENIERO INDUSTRIAL
M.P. 76045616

Firma:

Contenido:

PLANTA DE SEMISOTANO
REDES DE GAS NATURAL

Dibujó:

Arq. Germán Ramírez

Escala:

Como se indica

Fecha:

02/05/2026

Revisión:

01 07

GN-001