


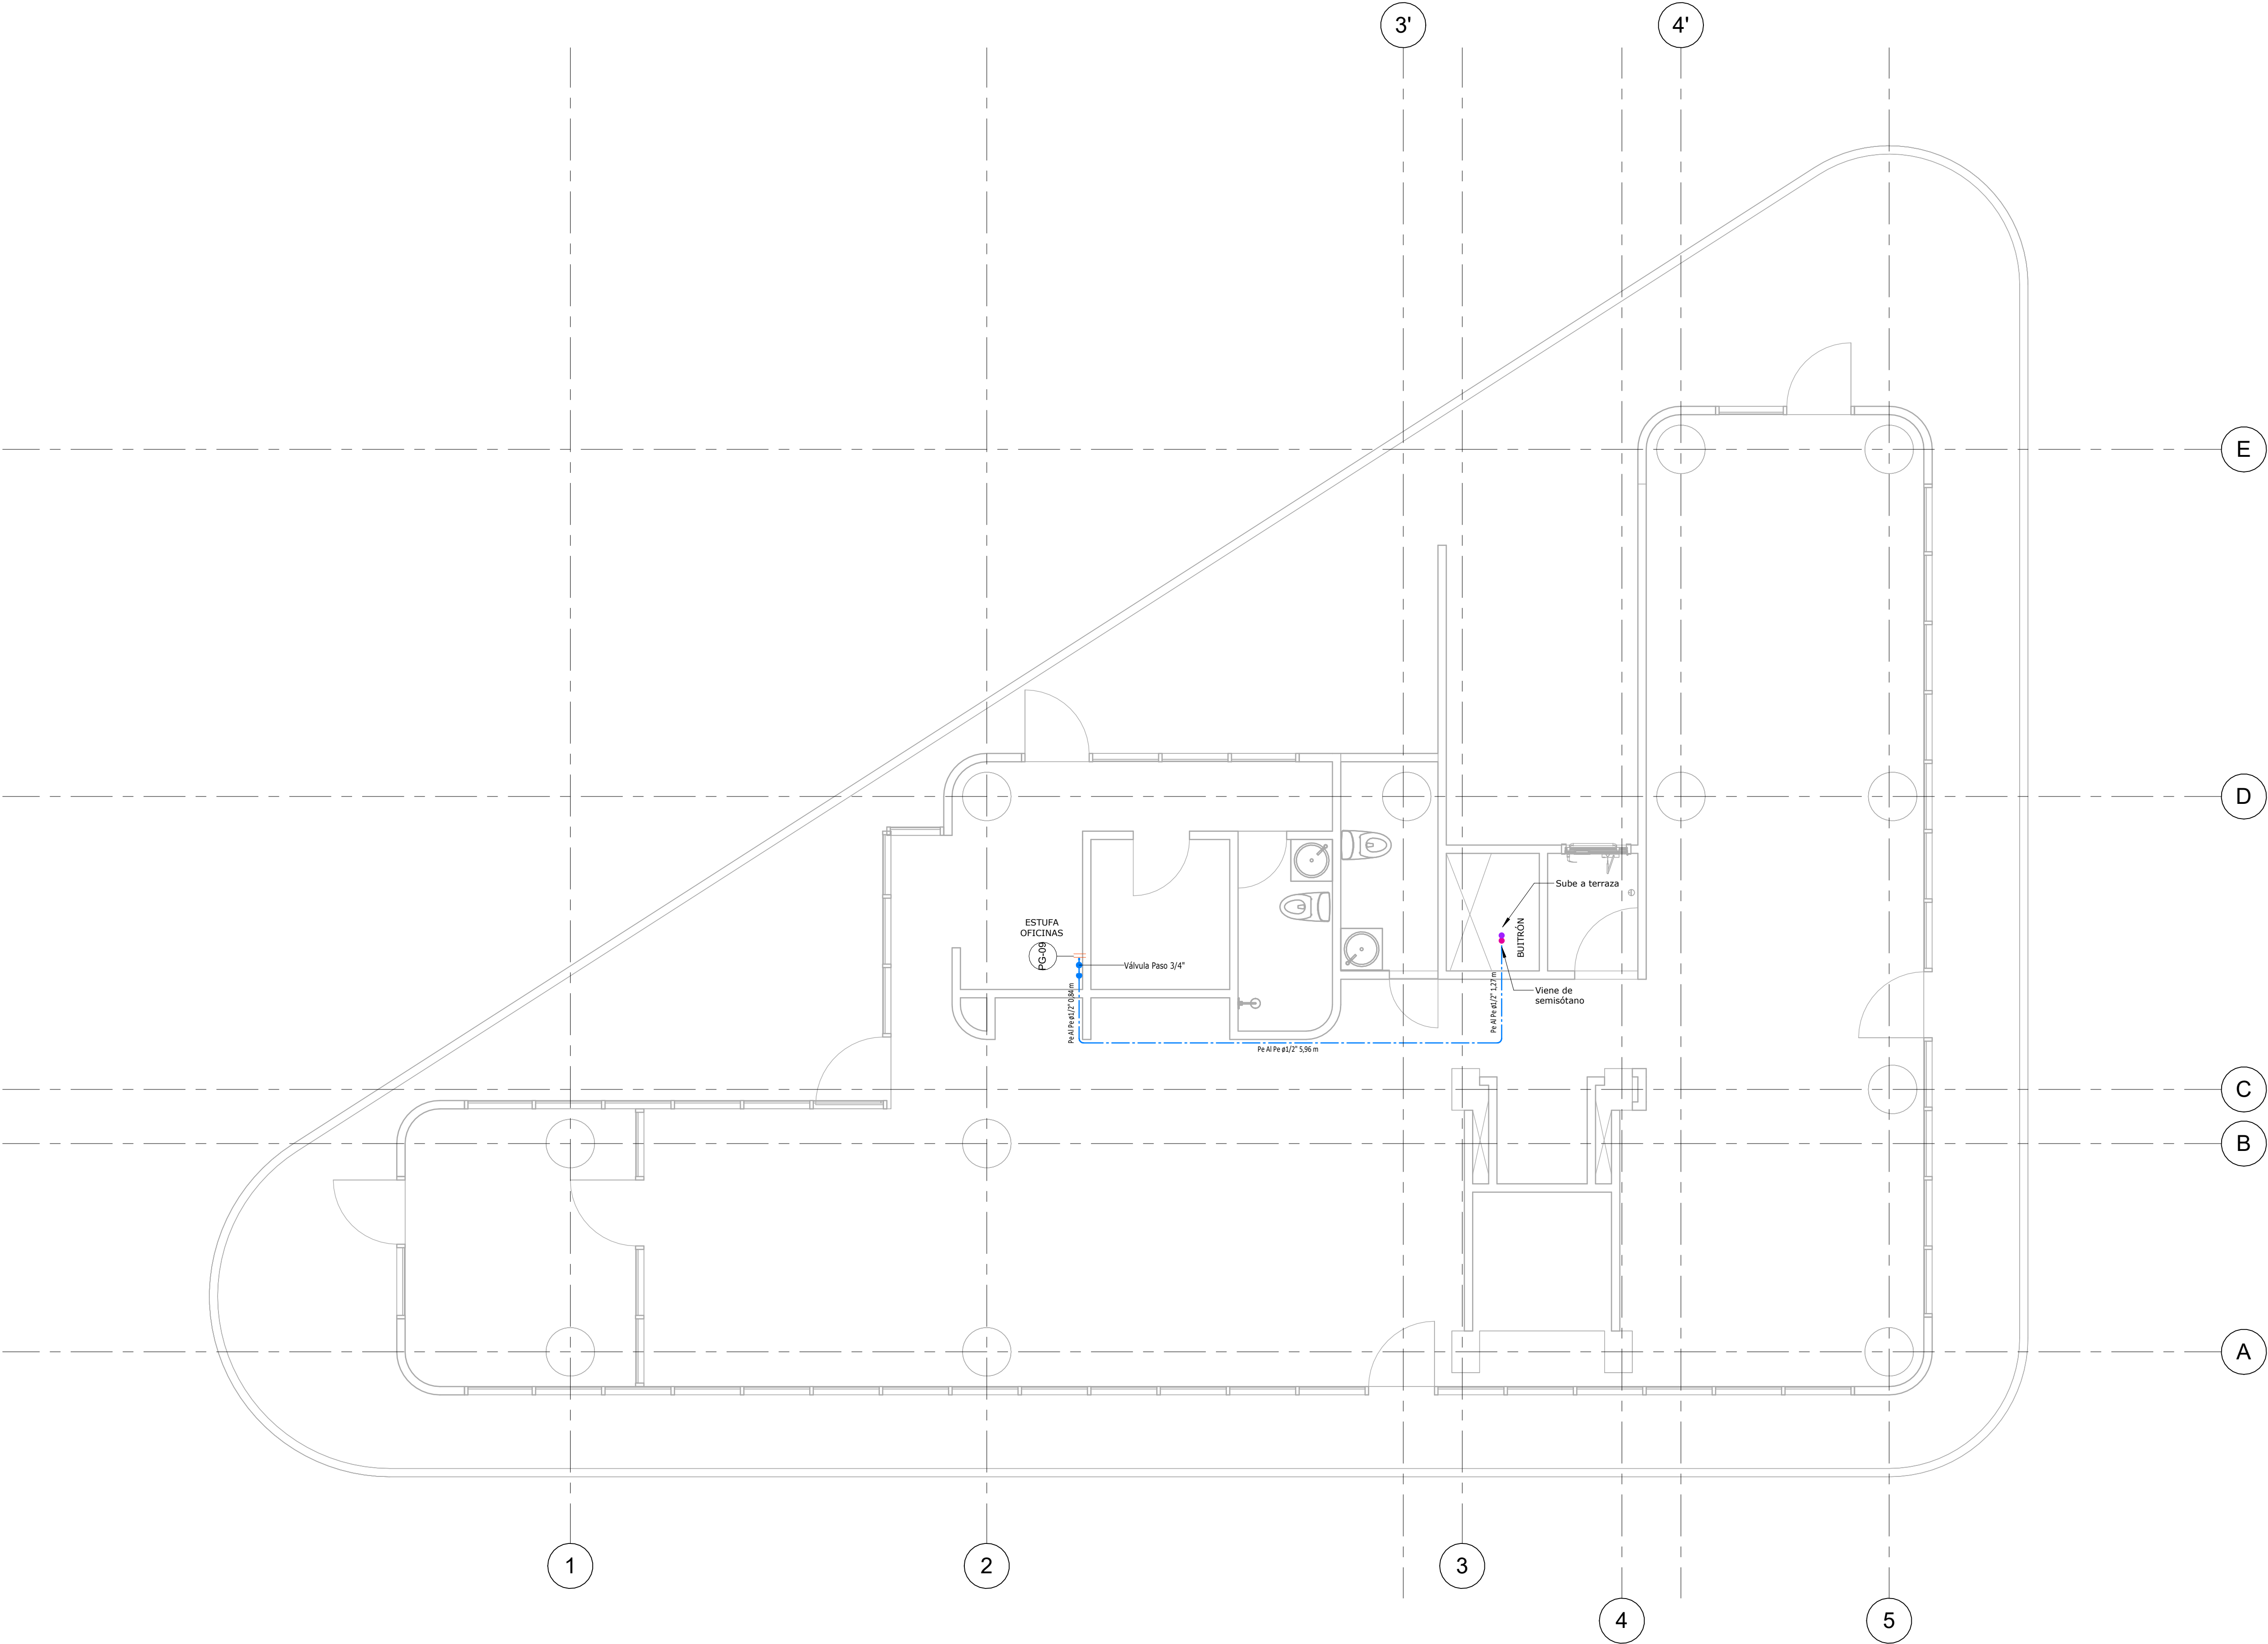

PLANTA DE SEGUNDO PISO RED DE GAS NATURAL

1 : 50

CONVENCIONES

Centro de Medición

Curva 90° Pe al Pe

Codo 90°

Válvula de Paso Pe al Pe

Reducción Pe al Pe

Te Pe al Pe

Punto salida de gas

Sube / baja

RSE - Regulador de segunda etapa

Pase en muro

Tuberías

Red Locales comerciales por cieloRed Zonas comunes por cieloRed Oficinas por pisoRed Zonas comunes terraza por cieloRed Zonas comunes sobre cubierta técnicaConexión a Red principal

Norte:

Proyecto:

FLORENTINO

Dirección:

El Peñón - Cali

Notas Generales:

1. Todas las medidas son indicativas y deben ser verificadas en sitio.

2. Los buitrones por donde subirá la tubería de gas deberán llevar un tabique de separación en caso de que se encuentren compartido con otro servicio.

3. Se deberán instalar rejillas para garantizar la ventilación en buitrones cerrados.

4. Se deben considerar registros de inspección en cada piso del buitrón.

5. La modificación de las redes internas solo podrán hacerse por personal calificado.

Observaciones:

REV.	DESCRIPCIÓN.	FECHA.
------	--------------	--------

Diseño:

MAURICIO CASANOVA

INGENIERO INDUSTRIAL

M.P. 76045616

Firma:

Contenido:

PLANTA DE SEGUNDO PISO REDES DE GAS NATURAL

Dibujó:

Arq. Germán Ramírez

Escala:

Como se indica

Fecha:

02/05/2026

Revisión:

0307

GN-003