



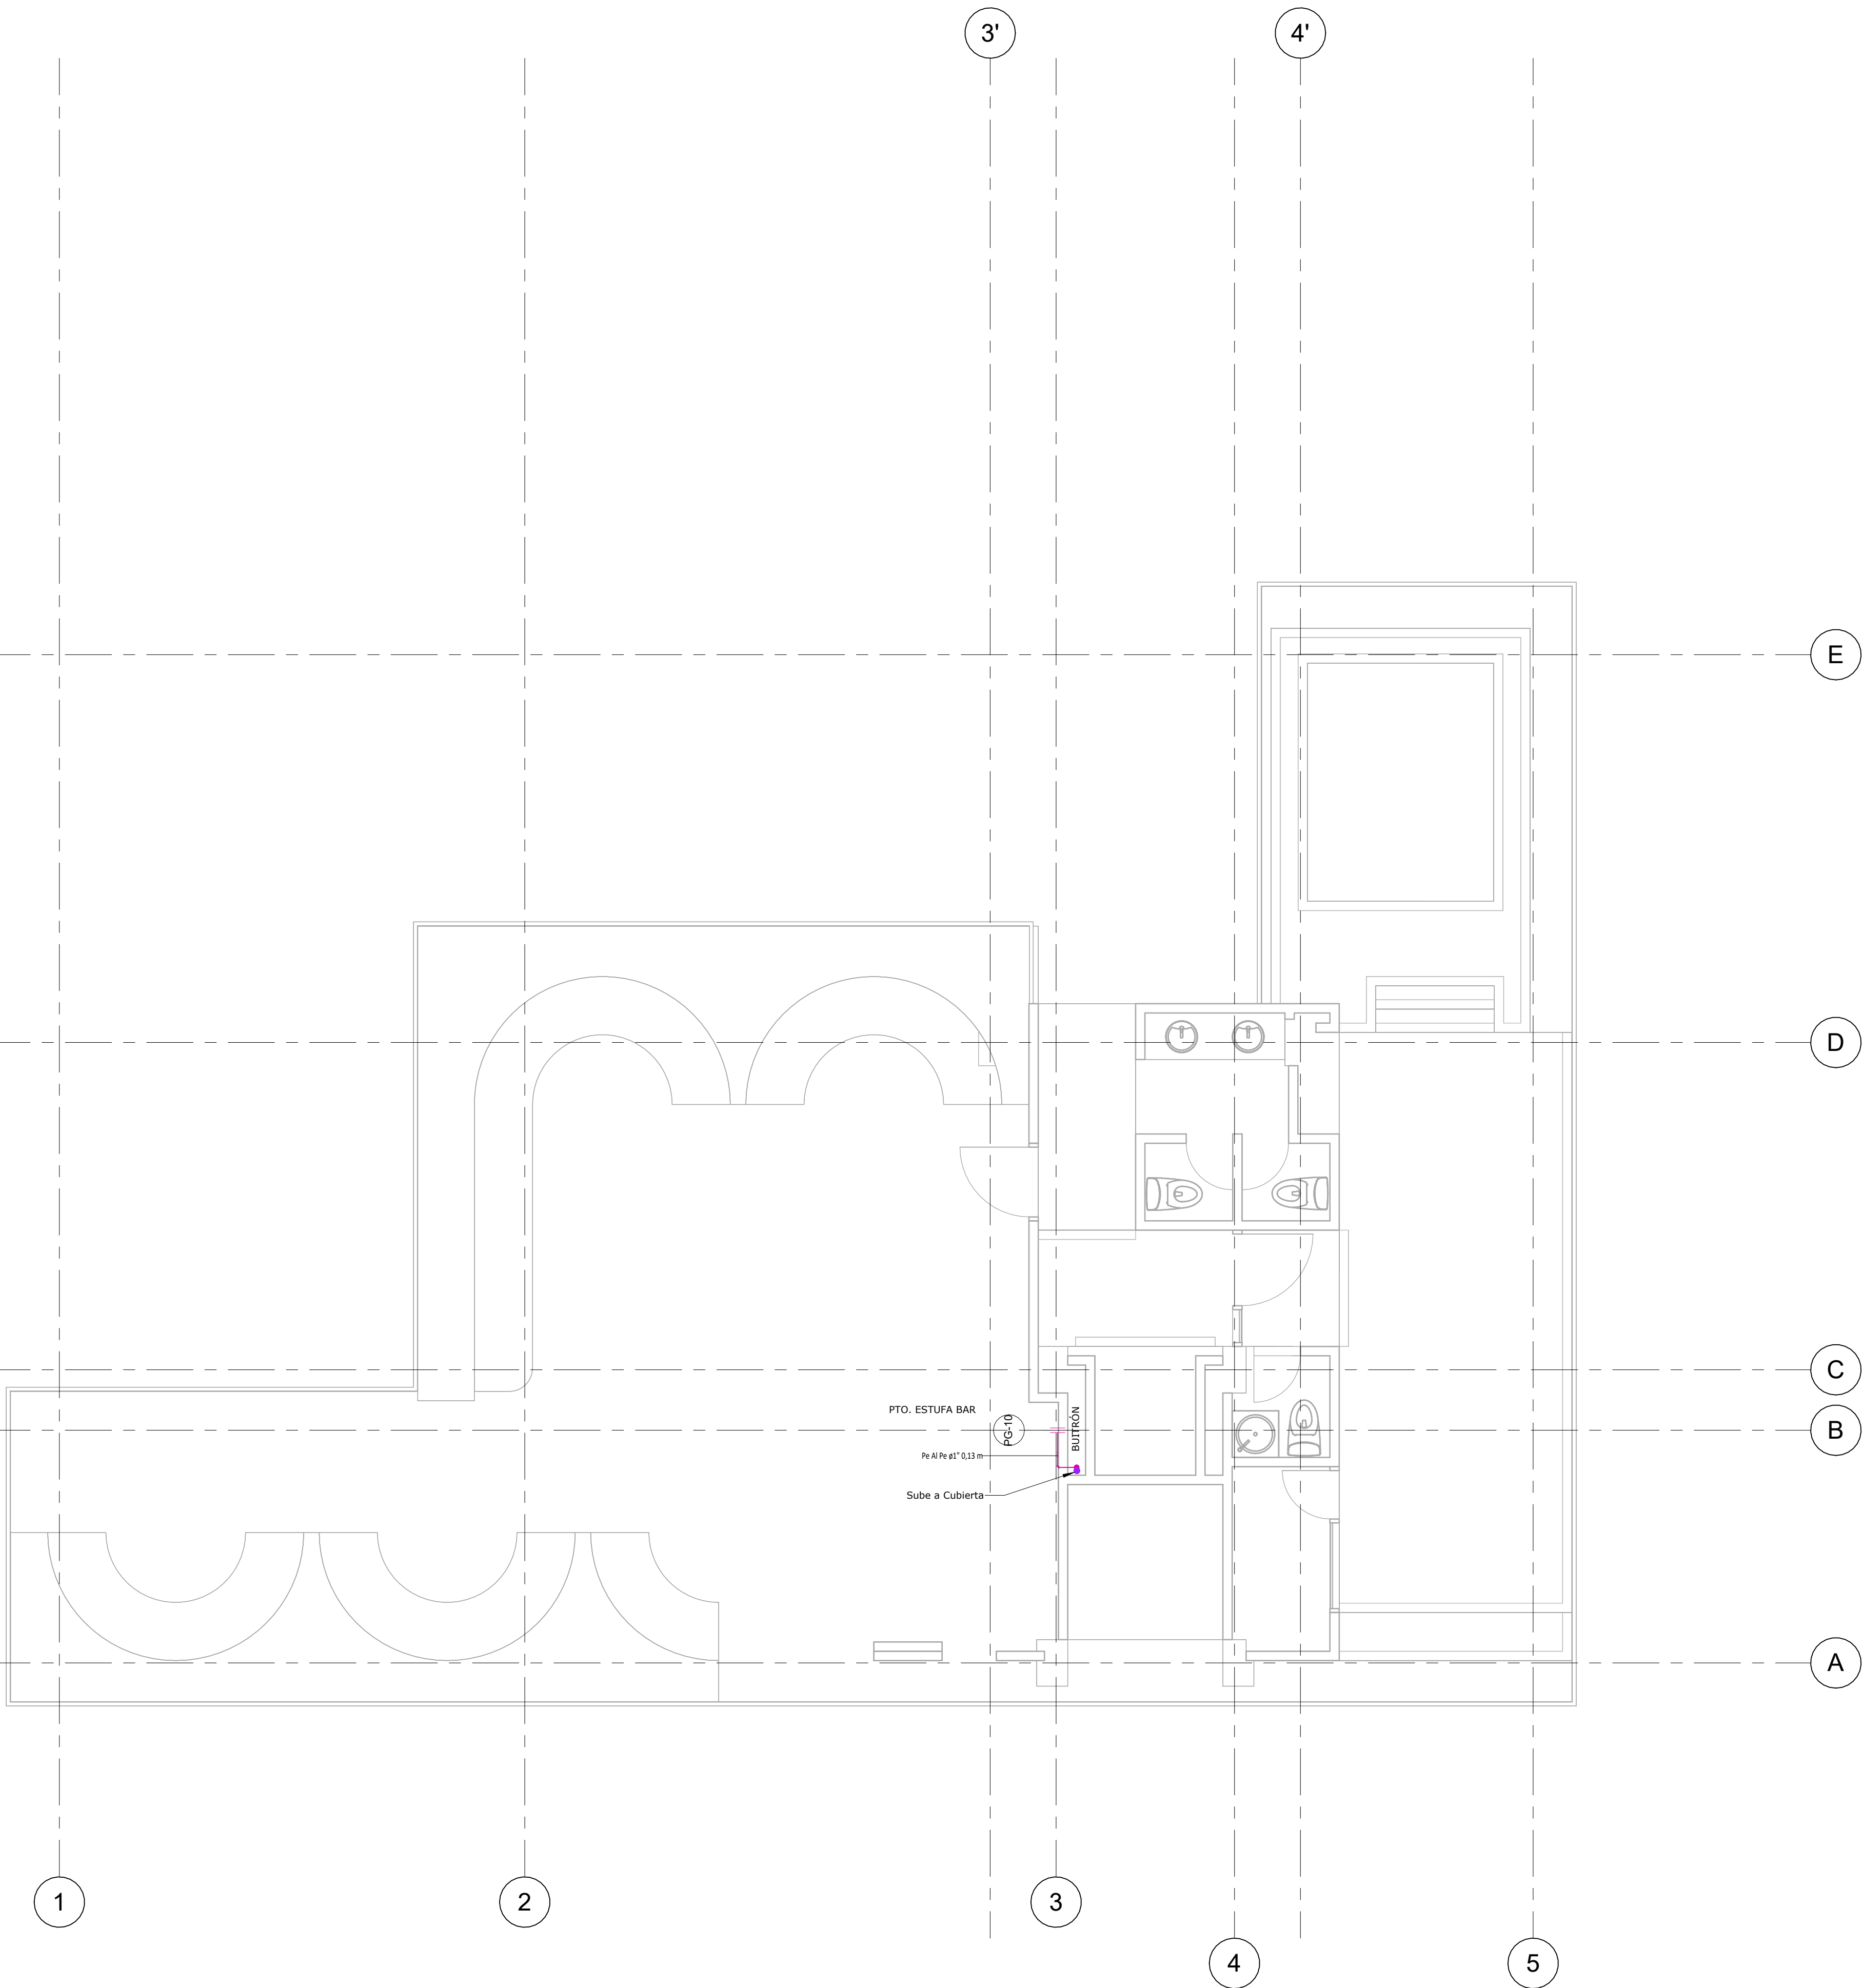

CONVENCIONES	
	Centro de Medición
	Curva 90° Pe al Pe
	Codo 90°
	Válvula de Paso Pe al Pe
	Reducción Pe al Pe
	Te Pe al Pe
	Punto salida de gas
	Sube / baja
	RSE - Regulador de segunda etapa
	Pase en muro
Tuberías	
	Red Locales comerciales por cielo
	Red Zonas comunes por cielo
	Red Oficinas por piso
	Red Zonas comunes terraza por cielo
	Red Zonas comunes sobre cubierta técnica
	Conexión a Red principal

Norte:

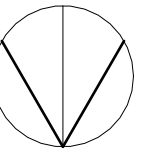

Proyecto:

FLORENTINO

Dirección:

El Peñón - Cali

Notas Generales:

1. Todas las medidas son indicativas y deben ser verificadas en sitio.
2. Los buitrones por donde subirá la tubería de gas deberán llevar un tabique de separación en caso de que se encuentren compartido con otro servicio.
3. Se deberán instalar rejillas para garantizar la ventilación en buitrones cerrados.
4. Se deben considerar registros de inspección en cada piso del buitrón.
5. La modificación de las redes internas solo podrán hacerse por personal calificado.

Observaciones:

REV.	DESCRIPCIÓN.	FECHA.
------	--------------	--------

Diseño:

MAURICIO CASANOVA
INGENIERO INDUSTRIAL
M.P. 76045616

Firma: _____

Contenido:

PLANTA DE TERRAZA
REDES DE GAS NATURAL
CUADROS DE
CANTIDADES

Dibujó:

Arq. Germán Ramírez

Escala:

Como se indica

Fecha:

02/05/2026

Revisión:

05
07

GN-005