

PLANO:

UNIAJC

PROPIETARIO:

 **Antonio José Camacho**
INSTITUCIÓN UNIVERSITARIA



COLABORADORES:

CONTENIDO:

PLANTA ELÉCTRICA PRIMER PISO

VoBo:

DIBUJO:

ESCALA:

FECHA:

ARCHIVO:


MODIFICACIONES:


OBSERVACIONES:

CONVENCIONES:

PLANO:

ELEC-001

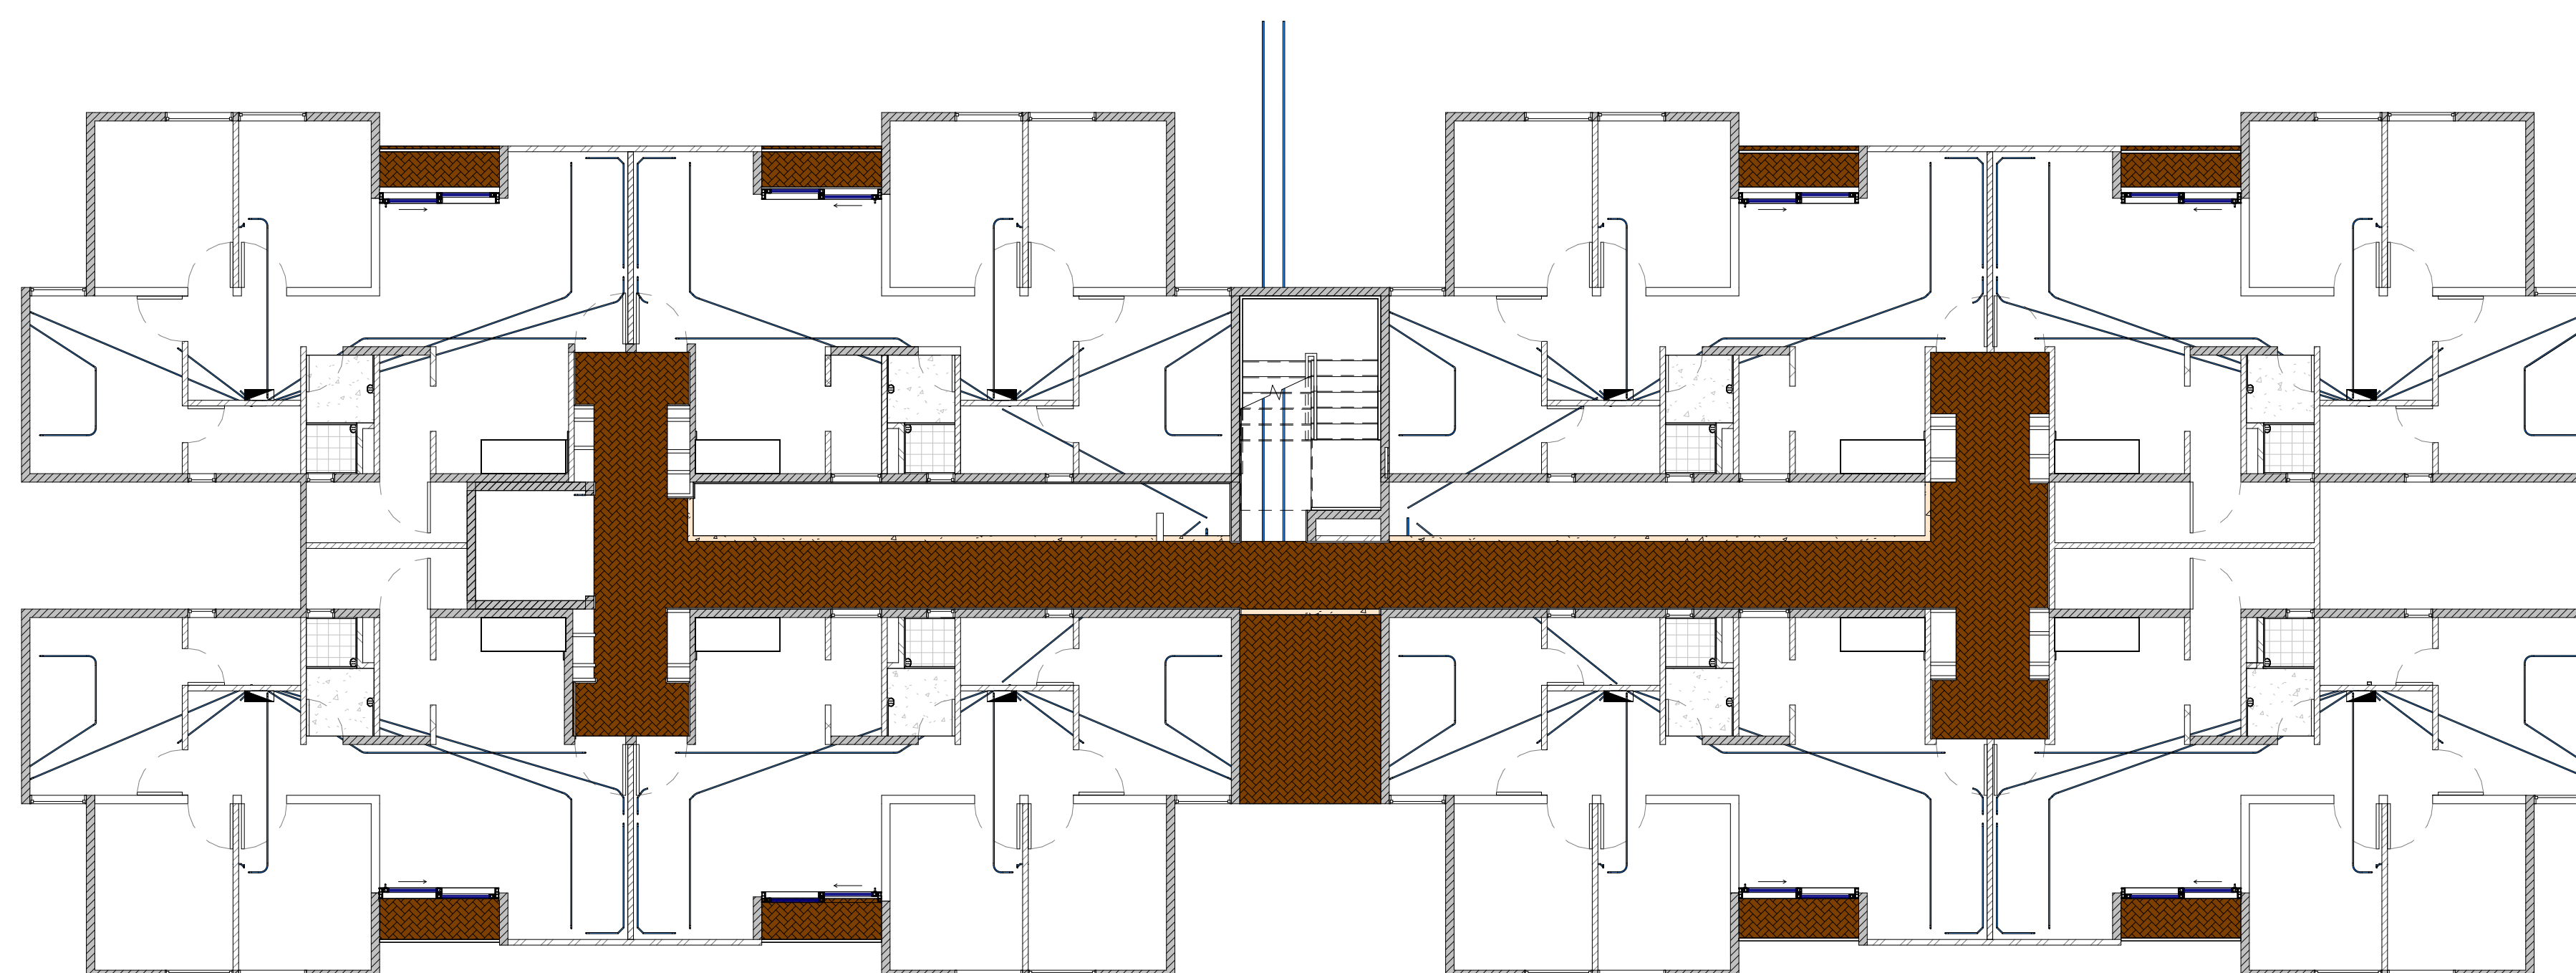

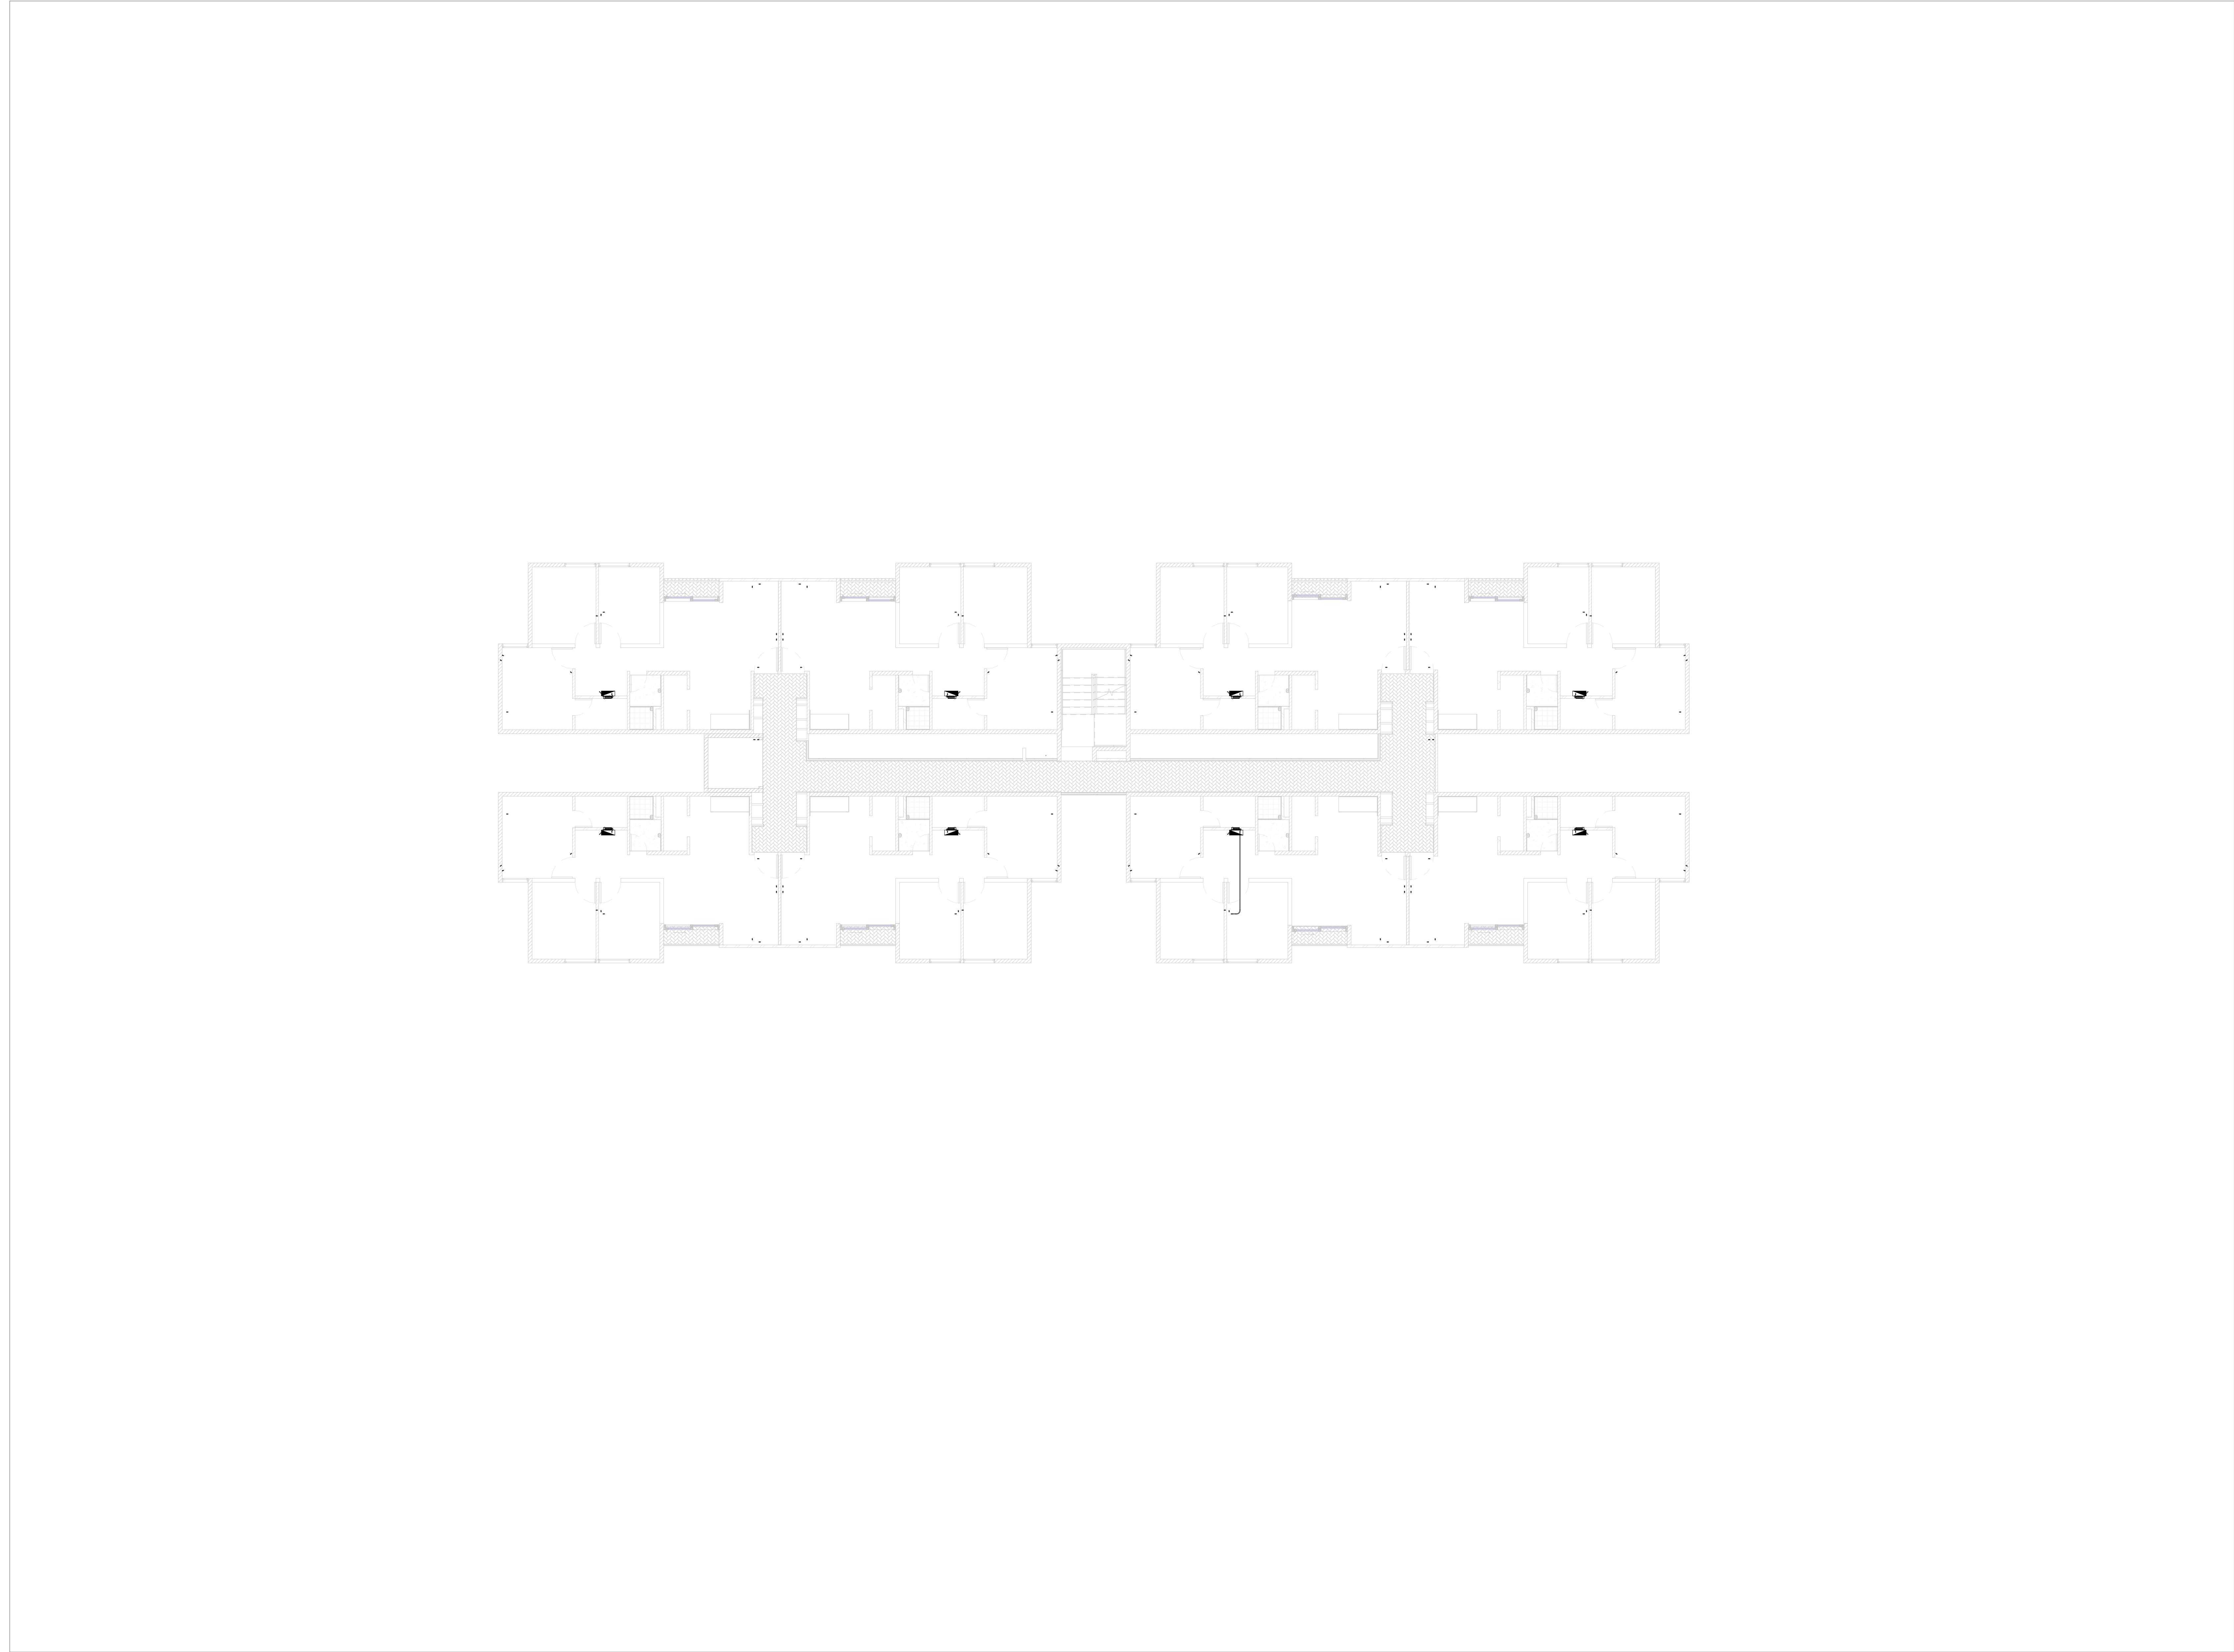

ELEC-003

PLANO:

PROYECTO:

UNIAJC

EDIFICIO 4 - BIBLIOTECA

PROPIETARIO:

INSTITUCIÓN
UNIVERSITARIA
ANTONIO JOSÉ CAMACHO



Antonio José
Camacho
INSTITUCIÓN UNIVERSITARIA



fodesep
FONDO DE DESARROLLO DE LA EDUCACIÓN SUPERIOR

DISEÑO:

ING. JOSE LUIS GALVIS MAT. VL.205-34332
VALLE

COLABORADORES:

CONTENIDO:

PLANTA
ELÉCTRICA
SEGUNDO PISO

VoBo:

DIBUJO:

ESCALA:

FECHA:

ARCHIVO:

MODIFICACIONES:

OBSERVACIONES:

CONVENCIONES:

PLANO:

ELEC-003

PROYECTO:

UNIAJC

EDIFICIO 4 - BIBLIOTECA

PROPIETARIO:

INSTITUCIÓN
UNIVERSITARIA
ANTONIO JOSÉ CAMACHO



DISEÑO:

ING. JOSE LUIS GALVIS MAT. VL.205-34332
VALLE

COLABORADORES:

CONTENIDO:

PLANTA
ELÉCTRICA
TERCER PISO

VoBo:

DIBUJO:

ESCALA:

FECHA:

ARCHIVO:

MODIFICACIONES:


OBSERVACIONES:

CONVENCIONES:

PLANO:

	Tubería EMT
	Tubería Conduit
	Línea de circuito
	Interruptor Doble
	Interruptor sencillo
	Interruptor Triple
	Interruptor Doble conmutable
	Interruptor sencillo conmutable
	Panel de distribución de circuitos
	Tomacorriente doble p/1 PISO 120v
	Tomacorriente doble p/1 REGULADO 120v
	Tomacorriente doble p/1 GFCI 120V
	Conductores: Neutro - Tierra - Fase
	Ducto bandeja portacable eléctrico
	Balizador de fachada
	Luminaria high bay 100w
	Cinta encauchetada, decorativa 6w/m
	Ducto bandeja portacable eléctrico
	Luminaria de incrustar, escalizable 15w
	Riel tracklight con spot 14.5w
	Panel led 60x 60cm - 40w
	Luminaria Fractal I de 45w - Fractal II de 70w
	Luminaria Bela 45w por ala
	Aplique Cartagenera, Luz Guía 8w
	Luminaria de emergencia sylvania 4w
	Panel led de incrustar de 12w
	Aplicques de pared de 12 w
	Lineal de 120cm dím 0-10v - 48w
	Panel led con cilindro de 25w
	Luminaria tortuga sobreponer en muro 10w

Cuadro de convenciones
1 : 50

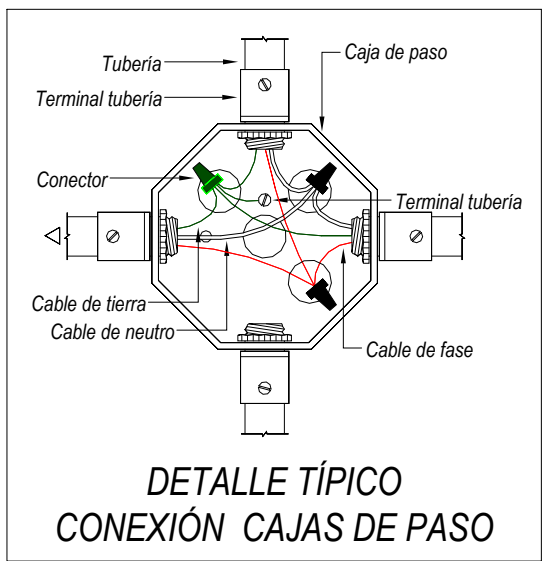

DETALLE TÍPICO 2
1 : 100

PROYECTO:

UNIAJC

EDIFICIO 4 - BIBLIOTECA

PROPIETARIO:

INSTITUCIÓN
UNIVERSITARIA
ANTONIO JOSÉ CAMACHO



DISEÑO:

ING. JOSE LUIS GALVIS MAT. VL.205-34332
VALLE

COLABORADORES:

CONTENIDO:

PLANTA
ELÉCTRICA
QUINTO NIVEL
LOSA TÉCNICA

VoBo:

DIBUJO:

ESCALA:

FECHA:

ARCHIVO:

MODIFICACIONES:

OBSERVACIONES:

CONVENCIONES:

PLANO:

Tubería EMT

Tubería Conduit

Línea de circuito

Interruptor Doble

Interruptor sencillo

Interruptor Triple

Interruptor Doble conmutable

Interruptor sencillo conmutable

Panel de distribución de circuitos

Tomacorriente doble p/1 PISO 120v

Tomacorriente doble p/1 REGULADO 120v

Tomacorriente doble p/1 GFCI 120V

Conductores: Neutro - Tierra - Fase

Ducto bandeja portacable eléctrico

Bañador de fachada

Luminaria high bay 100w

Cinta encauchetada, decorativa 8w/m

Ducto bandeja portacable eléctrico

Luminaria de incrustar, escalizable 15w

Rel tracklight con spot 14.5w

Panel led 60x 60cm - 40w

Luminaria Fractal I de 45w - Fractal II de 70w

Luminaria Biela 45w por ala

Aplicue Cartagenaera, Luz Guía 8w

Luminaria de emergencia sylvania 4w

Panel led de incrustar de 12w


Aplicues de pared de 12 w

Lineal de 120cm dim 0-10v - 48w

Panel led con cilindro de 25w

Luminaria tortuga sobreponer en muro 10w

Cuadro de convenciones
1 : 50

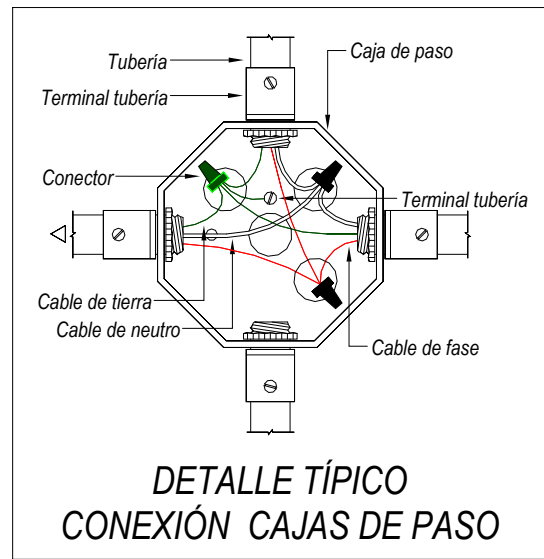

DETALLE TÍPICO 2
1 : 100